


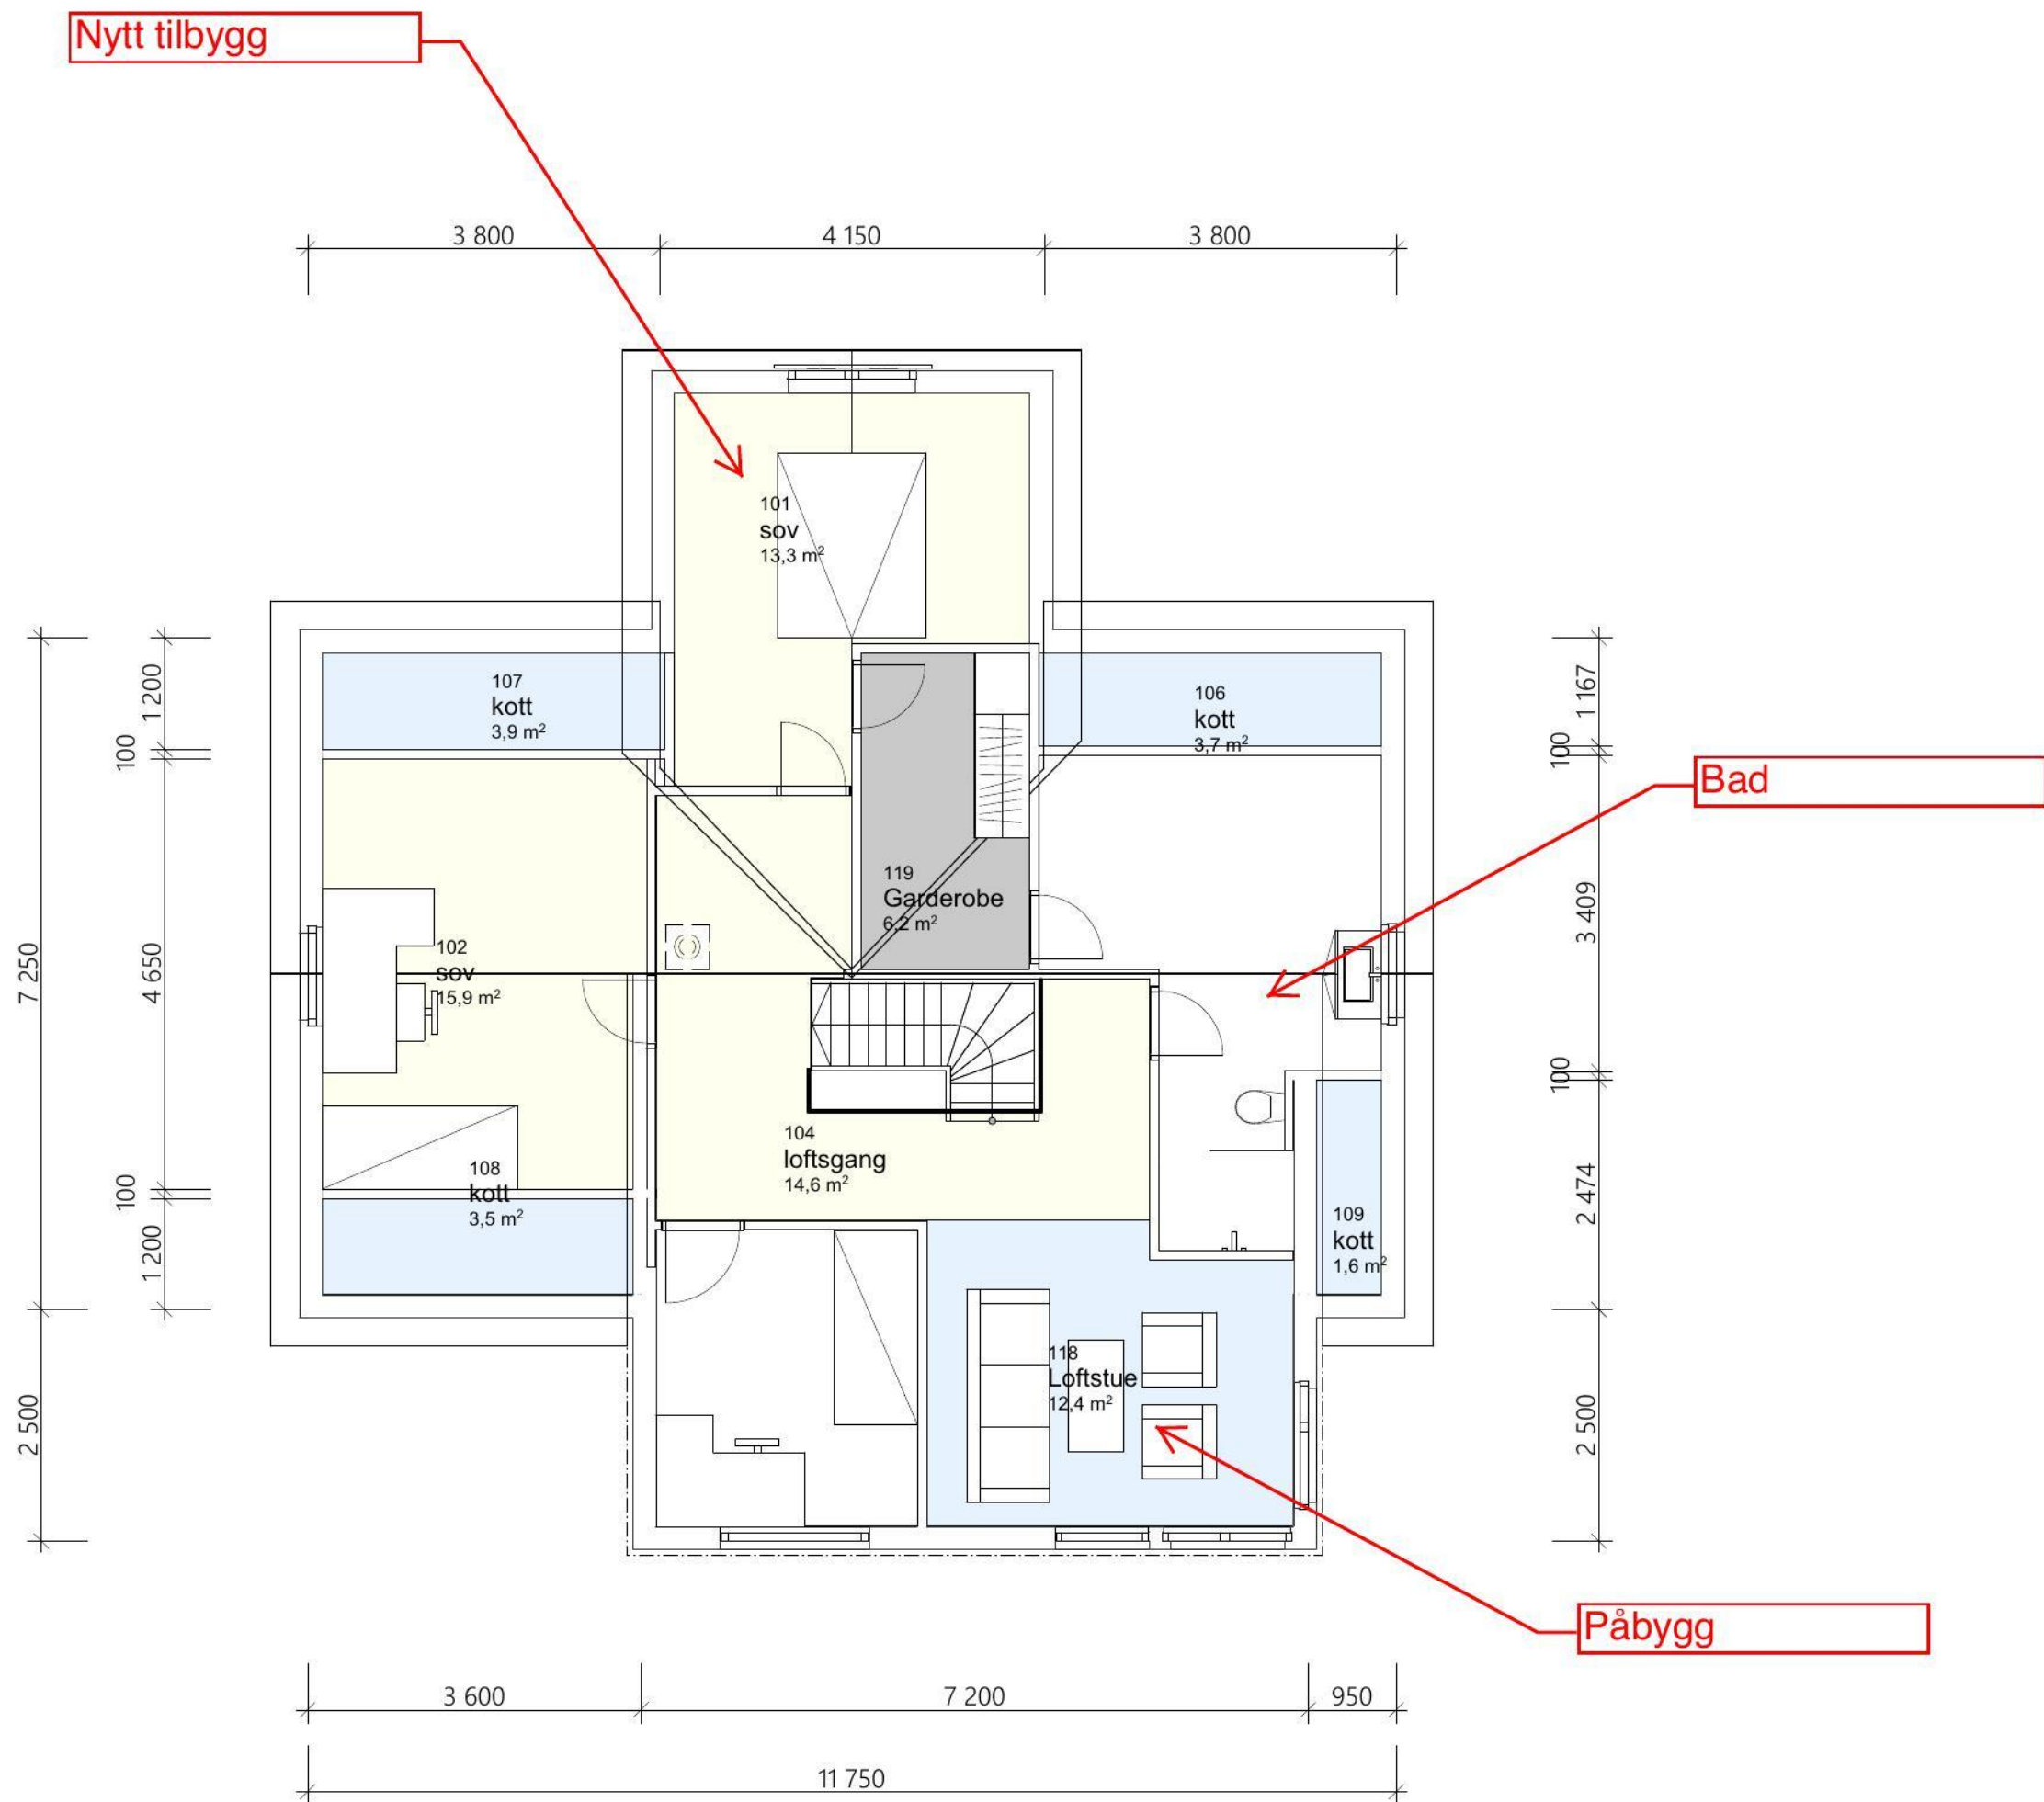

Tegningsnr.
A20-2

Revisjon nr.

Type tegning
Plan 2.etg

	Revidert	07.07.2022			
	Revidert	02.01.2023			
	Revidert vindusliste	09.01.2023			
Rev	Nr	Beskrivelse	Dato	Sign	Kontr
Lokalisering:					
N					
Prosjekteringsgruppen					
● ARK : Skjærgårdsbygg a/s ● RIB : Rådg. ing. Bygg ● RIE : Rådg. ing. Elektro ● RIV : Rådg. ing. VVS Østerøya 240 4625 Flekkerøy Tlf.: 90522750 steinar@skjaergardsbygg.no RIBveien18 0000 RIBbyen Tlf: 000 00 000 rib@ribfirma.no RIEveien18 0000 RIEbyen Tlf: 000 00 000 rie@riefirma.no RIVveien18 0000 RIVbyen Tlf: 000 00 000 riv@rivfirma.no					
Fase					
Fase					
Tiltakshaver					Godkjent
Mia og Sivert					
Prosjekt					Kontroll prosjekt.
					Sign. Kontroll
Filnavn					Sivert og Mia.pln,lck.pln
Dato					20.04.2022
Målestokk					1:100
Kontroll utførende					
Gnr./Bnr./Festenr.:					Sign. Kontroll
Gnr/Bnr/Festenr					
Prosjektnr.:		Tegningsnr.:		Prosjektnr. for prosjekterende/lev.	
Prosjektnr.		A20-2			
Type tegning:					
Plan 2.etg					