



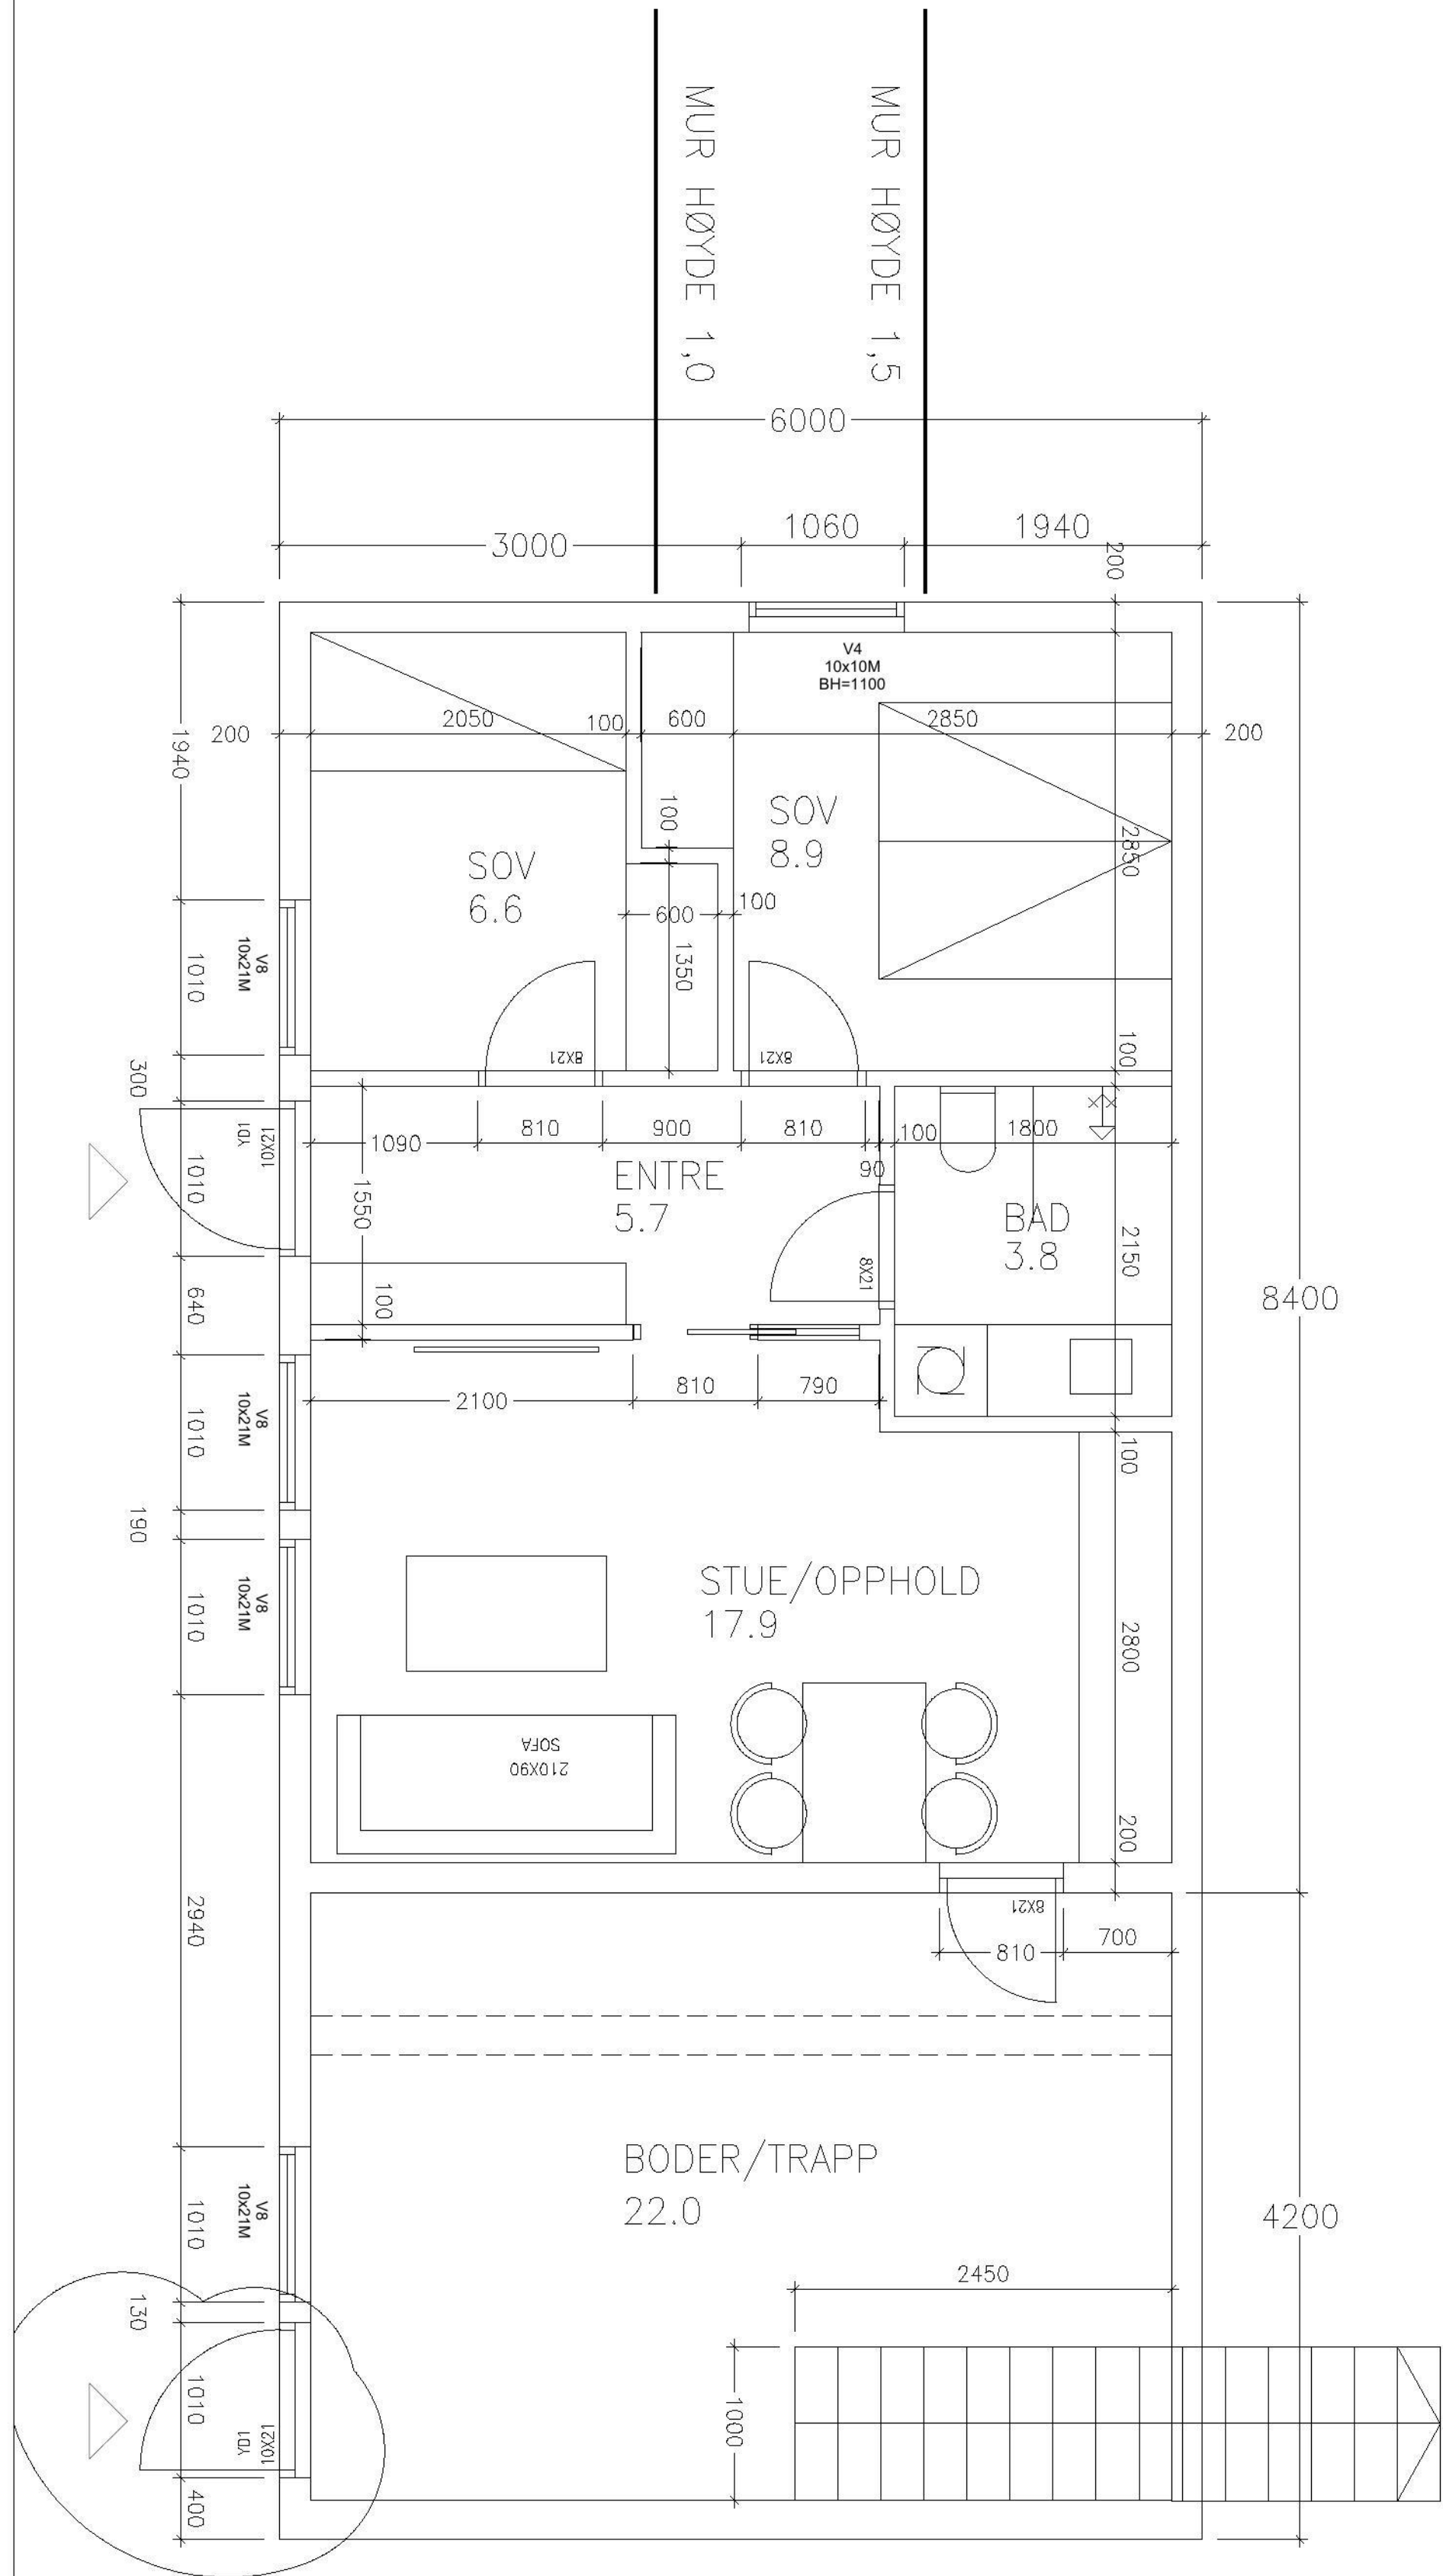

(BYA = 75.5M2)
BRA = 68.0M2
HYBEL = BRA = 45.0m2

PLAN U.ETG.

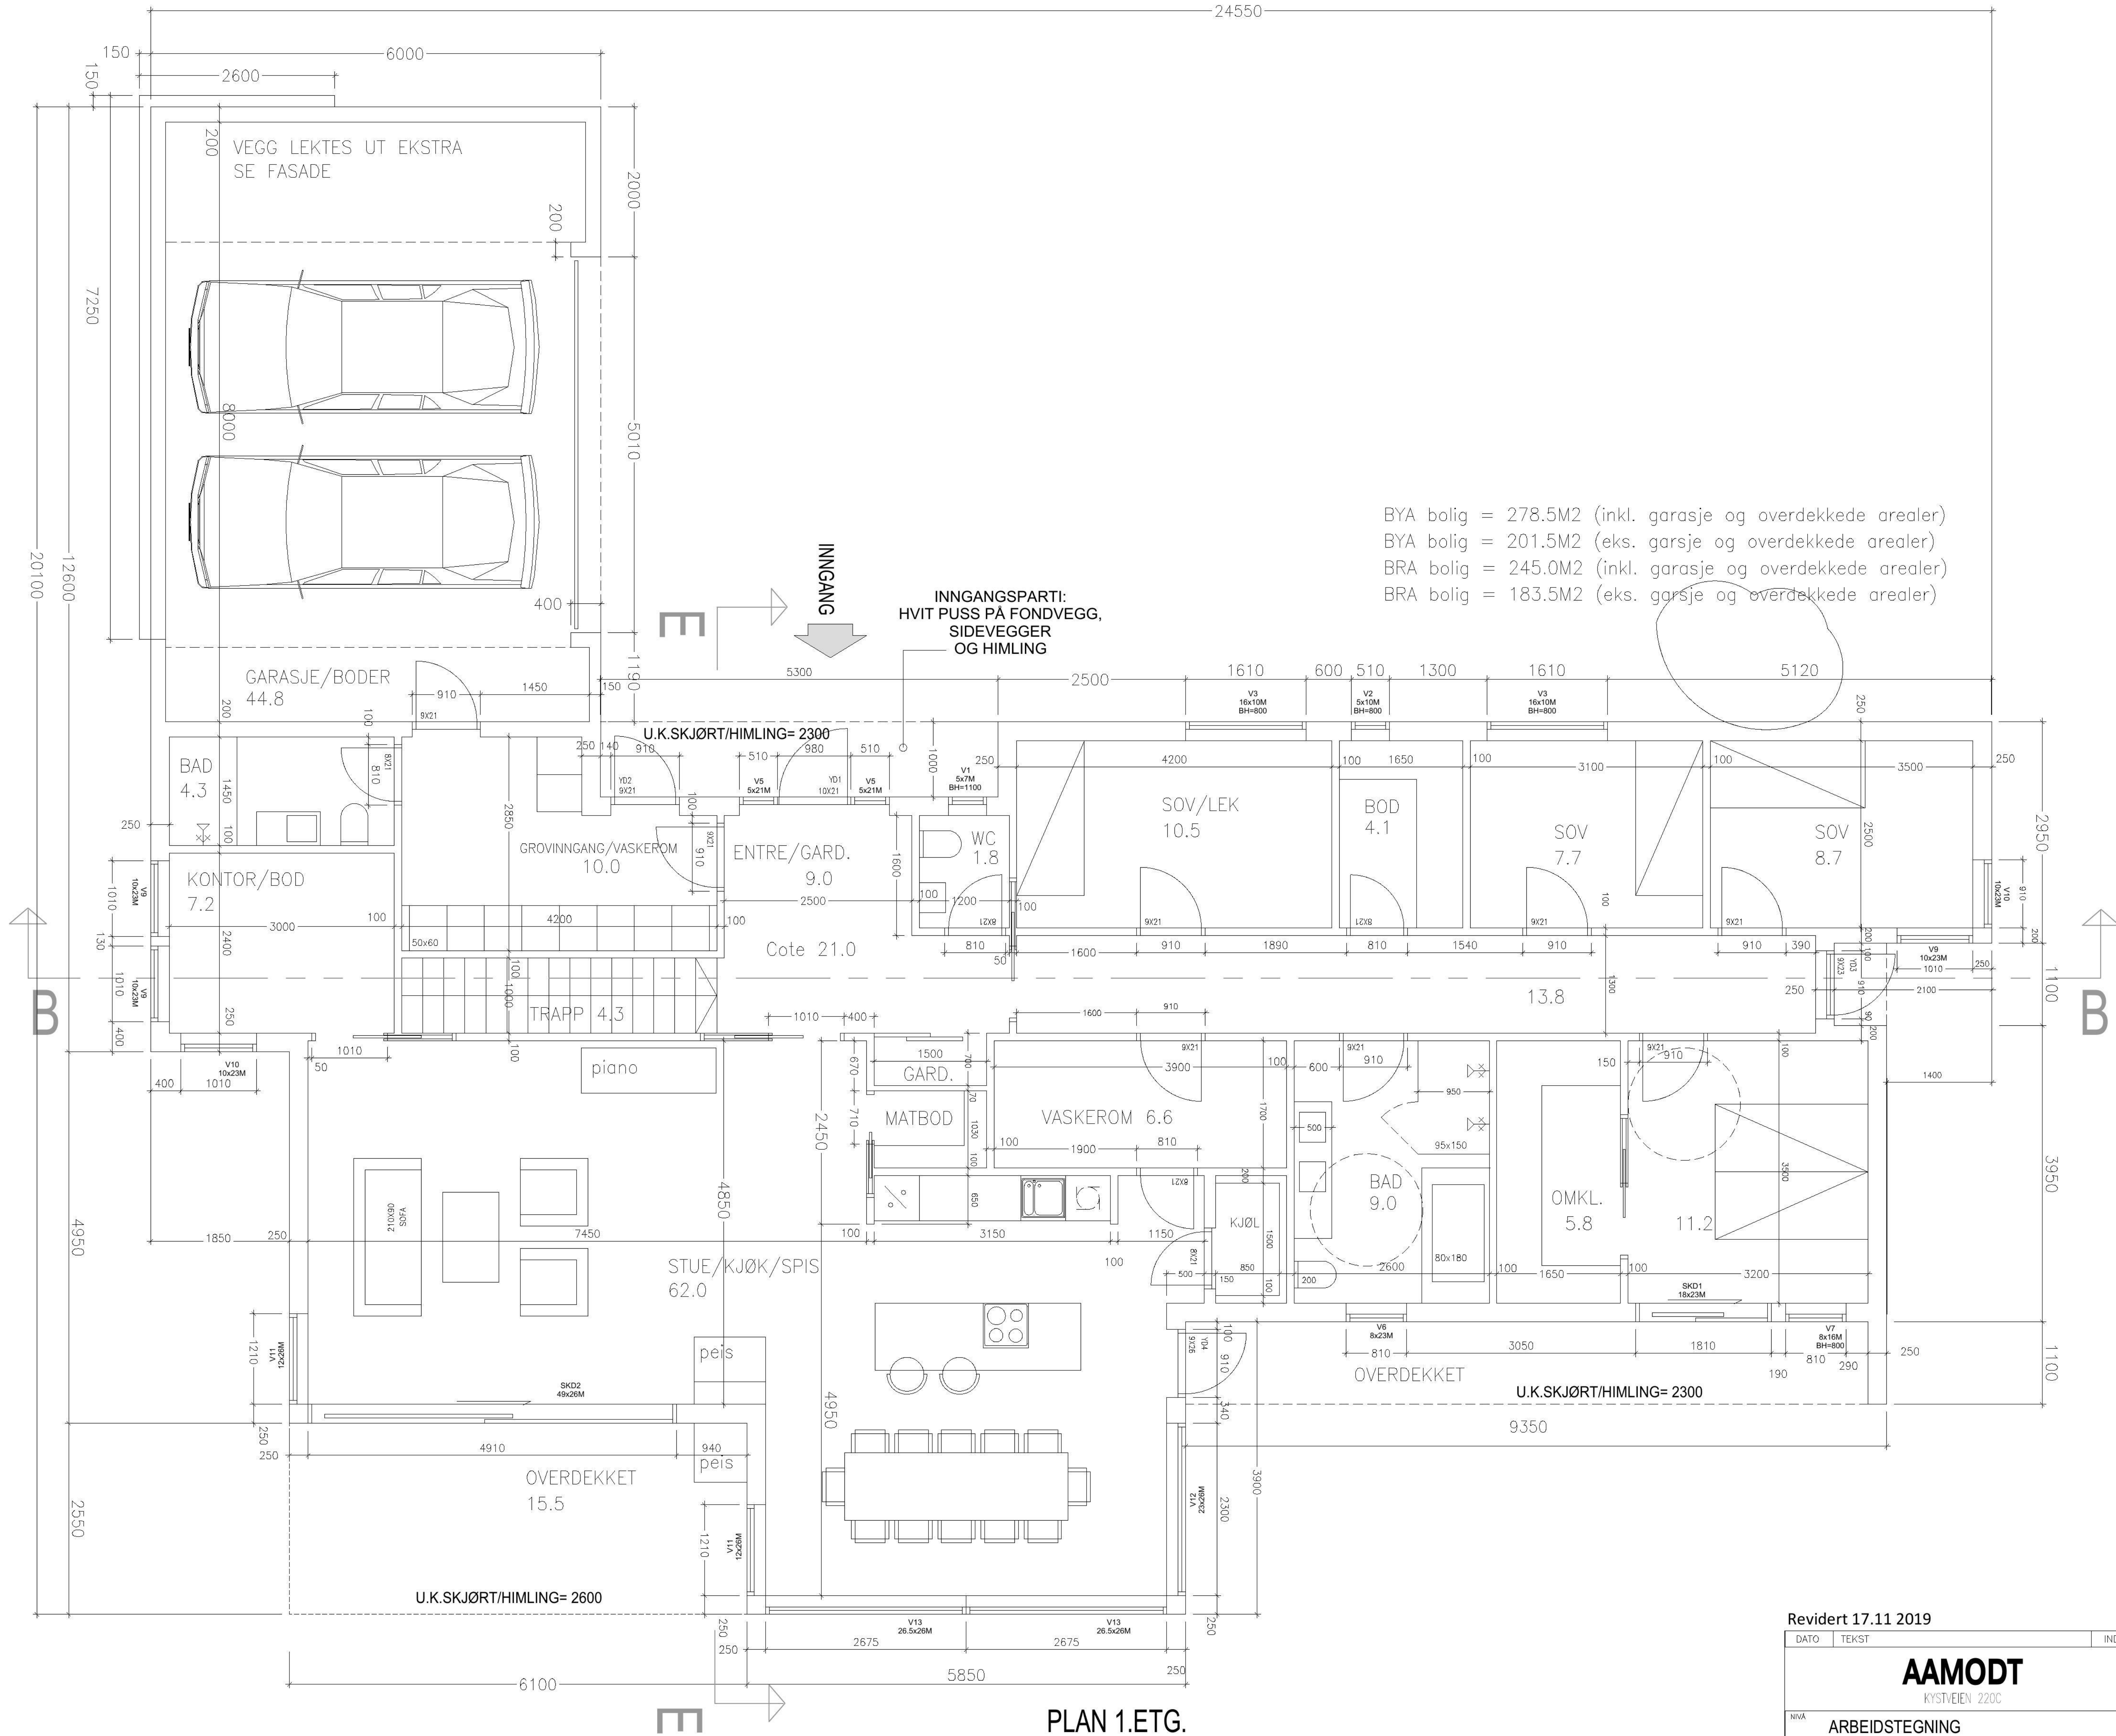

PLAN 1.ETG.

BYA bolig = 278.5M2 (inkl. garasje og overdekkede arealer)
BYA bolig = 201.5M2 (eks. garsje og overdekkede arealer)
BRA bolig = 245.0M2 (inkl. garasje og overdekkede arealer)
BRA bolig = 183.5M2 (eks. garsje og overdekkede arealer)

Revidert 17.11 2019				INDEX	
DATO		TEKST			
AAMODT					
KYSTVEIEN 220C					
ARBEIDSTEGNING					
PLAN U.ETG. OG 1.ETG.					
TEGN.NR.		REV.		SIVILARKITEKT M.N.A.L	
A-101				JEBSEN-VINJE AS	
MÅL:		TEGN.LAV		NØDEVIGA 18 4810 KRISTIANSAND	
1:50		1:50		MOBIL 97 57 11 14 jens@jebsen-vinje.no	
DATO:		ANSV.		KONTR.	
07.11.19		JW			
FILE:		c:\kontor\prosjekter\privat\kystveien			