


1 SOVEROM 10,9m ² /1,84	20 STUE 39,2m ² /8,17
2 " 7,4m ² /0,86	25 VASKEROM
3 " 6,3m ² /0,86	26 MATBOD
10 KJØKKEN 11,5m ² /1,36	27 BRENDSEL
11 BAD 3,3m ² /0,86	28 REDSKAP
12 DUSJ 2,7m ²	29 TØRKEROM
15 VINDFANG	30 HOBBYROM
16 HALL 11,2m ²	
33 KJELLERTRAPP	

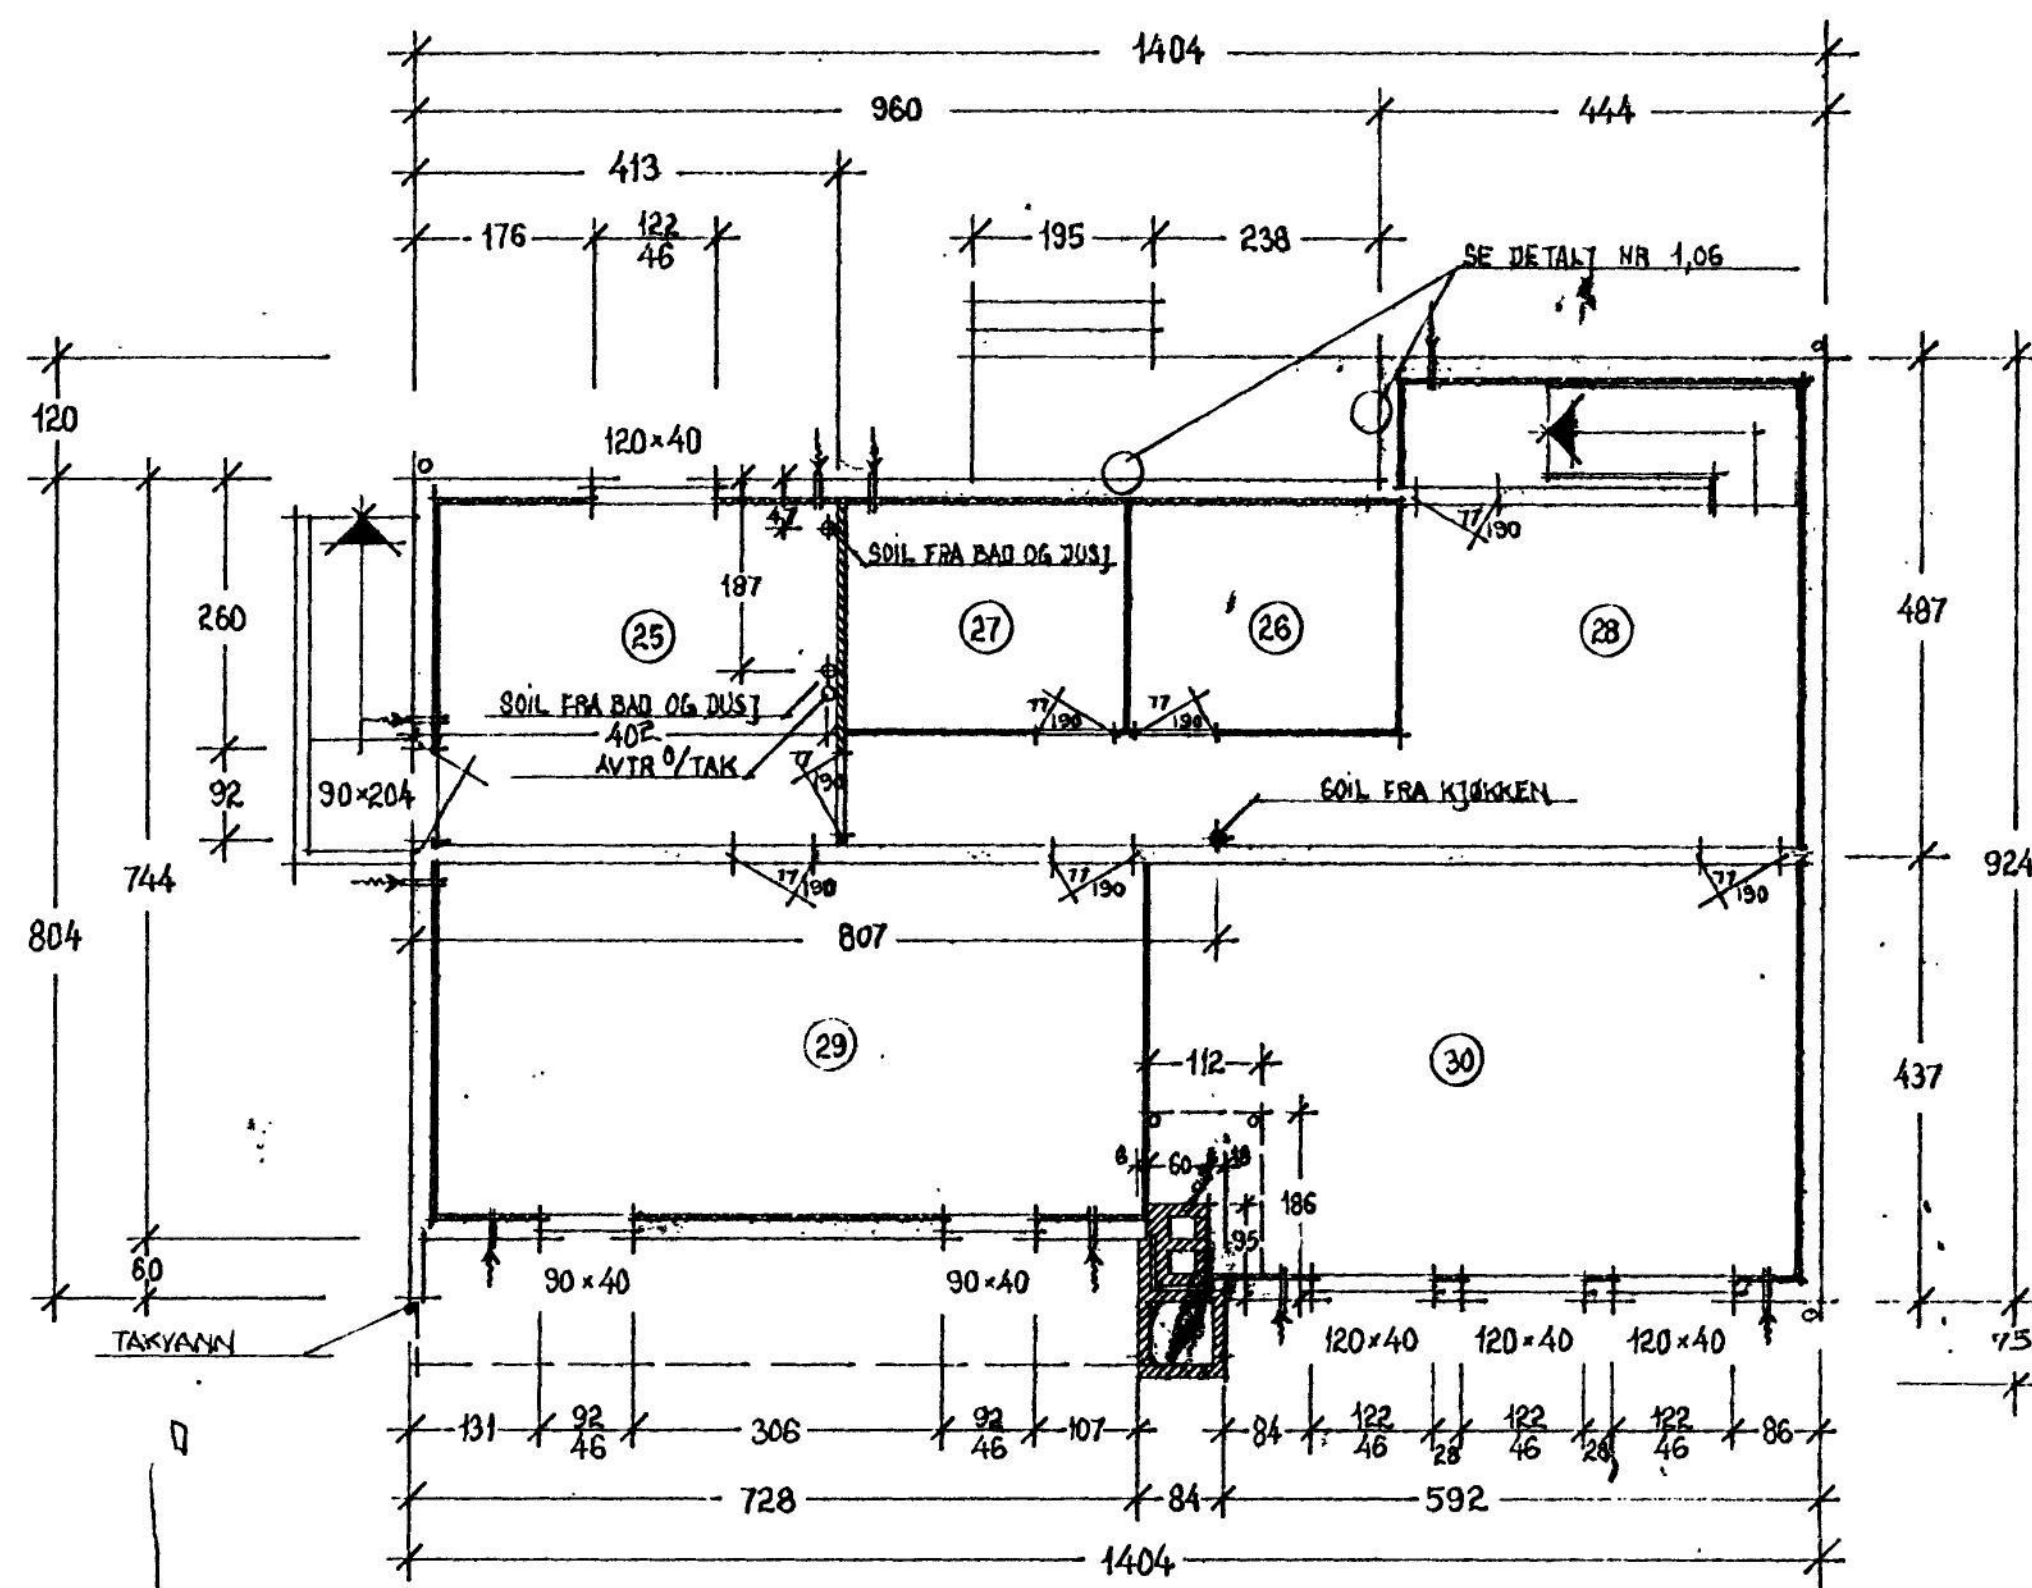

FOR F
SE 3A

Situationskartet er hentet fra kommunens kart base, men kan inneholde feil.

Rev.:	Dato:	Beskrivelse:	Sign:
Prosjekt:			
Austrusheia 2 - Brukseendring			
Byggeadresse:			
Austrusheia 2			
4640 Søgne			
Gnr./Bnr./Festnr. 423/376			
Tiltakshaver:			
Runar Larsen			
Austrusheia 2 Søgne 4640			
Tegningsfase:			
Søknad			
Tegning:			
E10-01			
Plan 1. etasje Eksisterende			
Format:			
A3 1:100			
Dato opprettet:			
01.11.2023			
Prosjektnr.:			
23083			

MOLO

Molo Consulting AS
post@molo.no
www.molo.no

Signatur: T.F

Kontroll: F.B

Arkitektonisk Prosjekterende:
Molo Consulting AS

Tegningen er Arkitektonisk prosjektert. Dimensjoner, isolasjonstykkelse, vindusstørrelser, porter m.m. er basert på erfaringstall, men må dimensjoneres og kontrolleres. Tegningen er Molo consulting AS sin eiendom inntil varen er betalt. Kopiering eller bruk av tegningen tillates ikke uten tillatelse.