


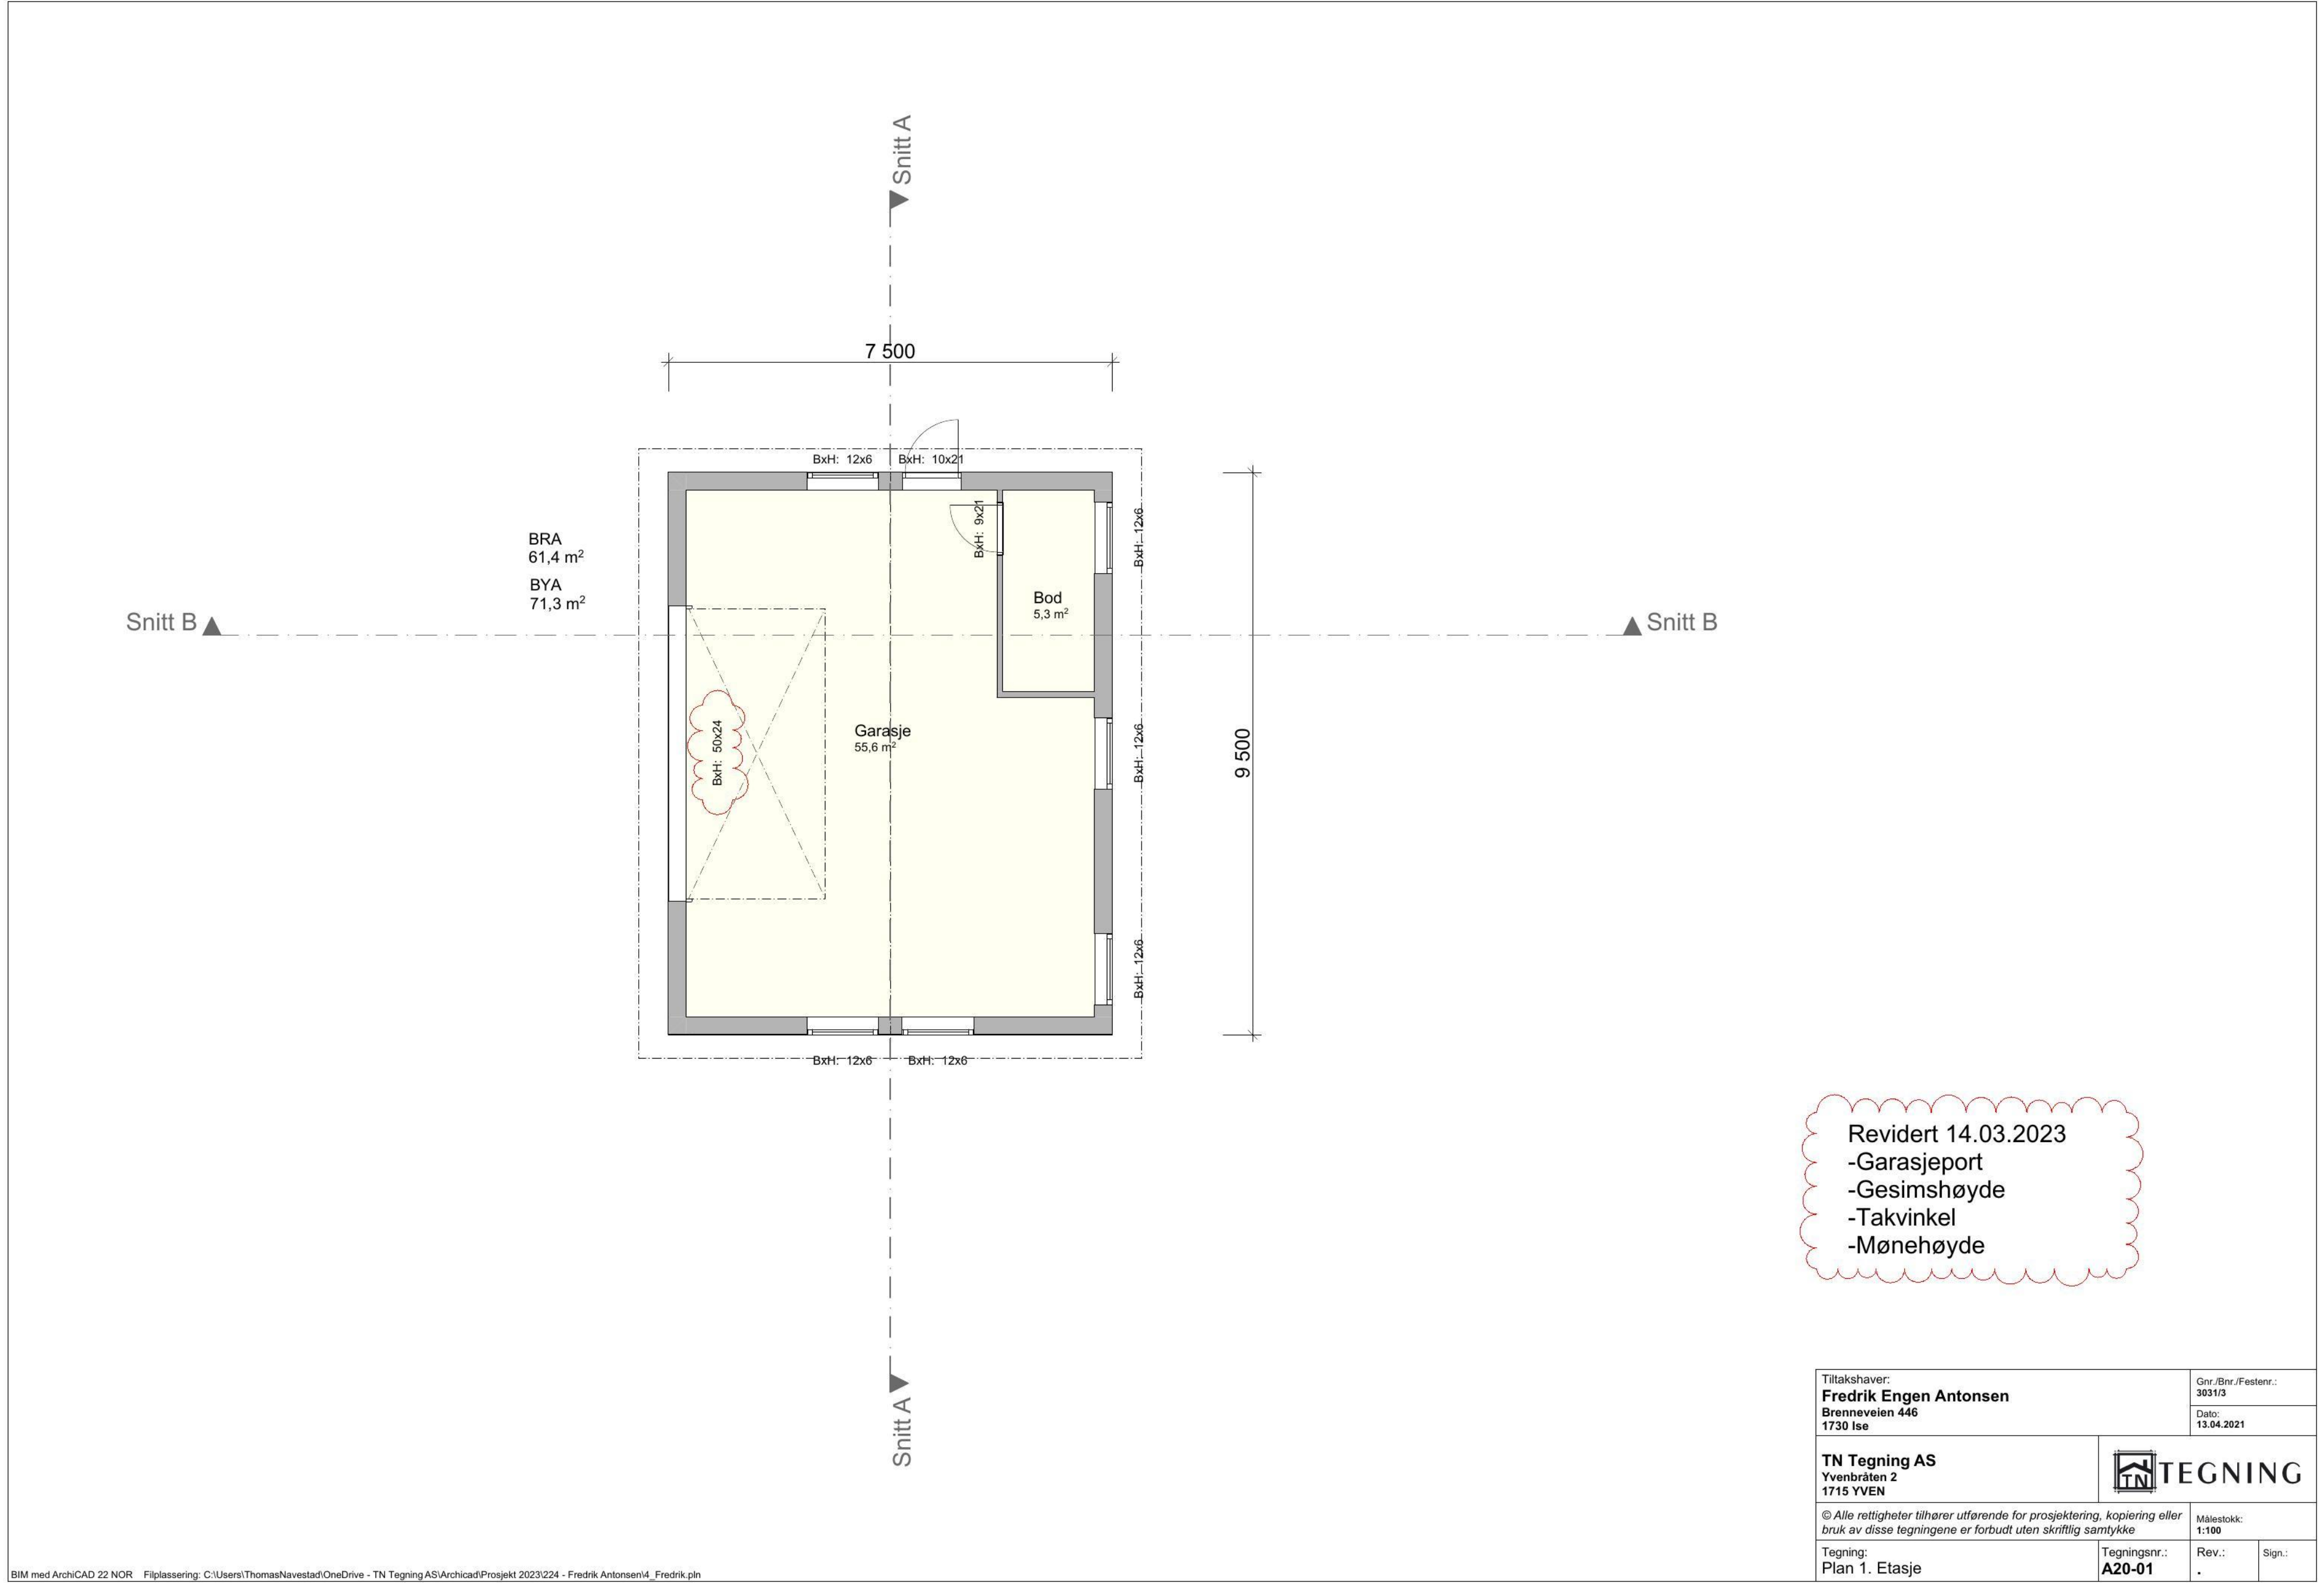

Tiltakshaver: Fredrik Engen Antonsen Brenneveien 446 1730 Ise		Gnr./Bnr./Festnr.: 3031/3	
		Dato: 13.04.2021	
TN Tegning AS Yvenbråten 2 1715 YVEN			
© Alle rettigheter tilhører utførende for prosjektering, kopiering eller bruk av disse tegningene er forbudt uten skriftlig samtykke		Målestokk: 1:100	
Tegning: Plan 1. Etasje		Tegningsnr.: A20-01	Rev.: .
		Sign.:	