
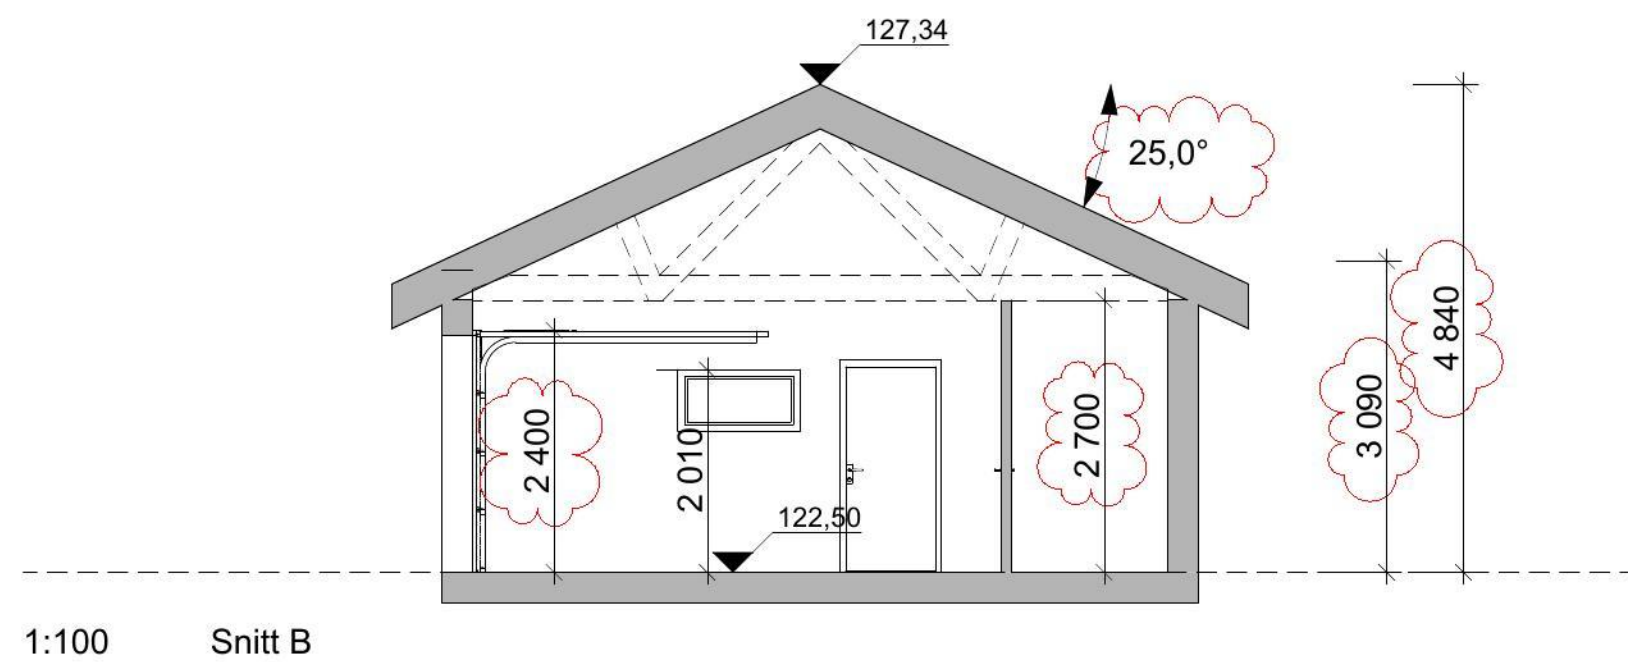


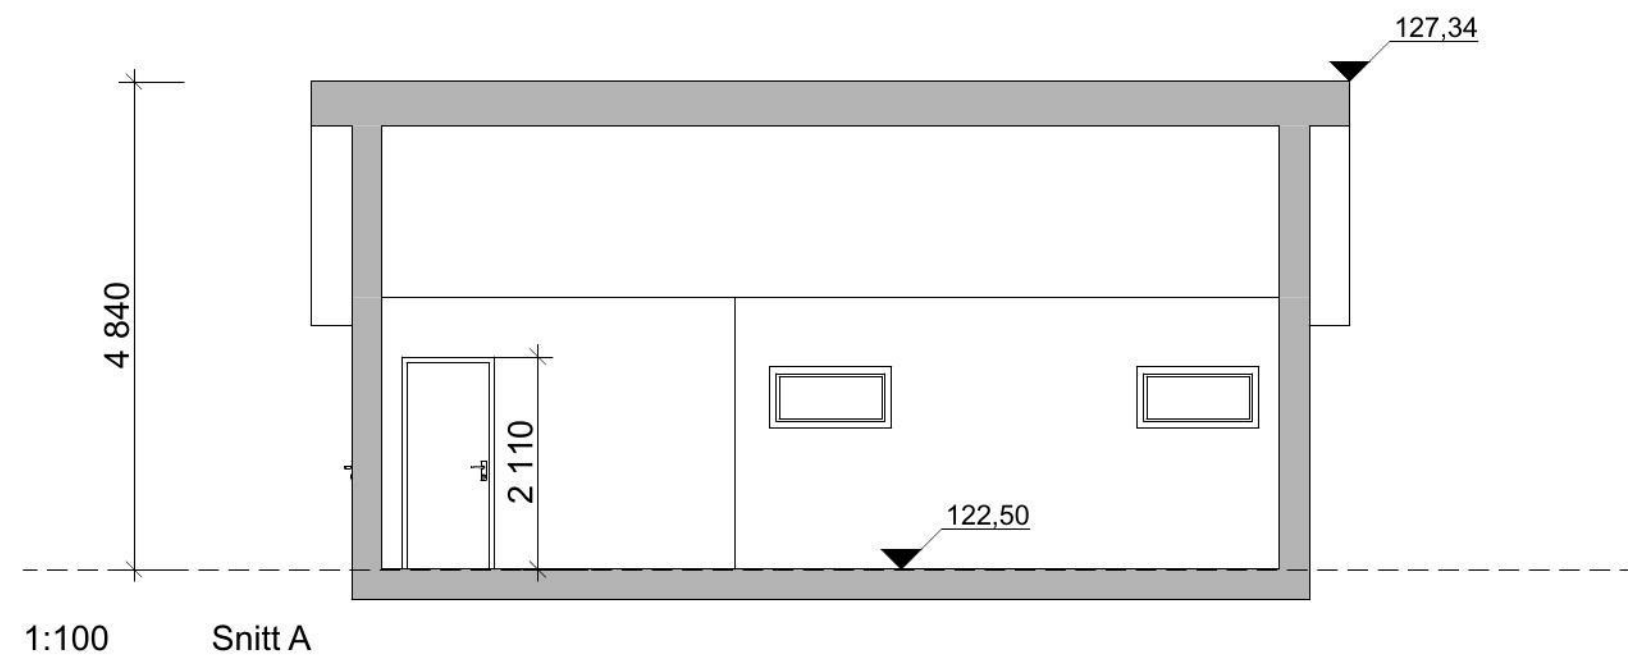

Revidert 14.03.2023
-Garasjeport
-Gesimshøyde
-Takvinkel
-Mønehøyde

Tiltakshaver: Fredrik Engen Antonsen Brenneveien 446 1730 lse		Gnr./Bnr./Festnr.: 3031/3	
		Dato: 13.04.2021	
TN Tegning AS Yvenbråten 2 1715 YVEN			
© Alle rettigheter tilhører utførende for prosjektering, kopiering eller bruk av disse tegningene er forbudt uten skriftlig samtykke		Målestokk: 1:100	
Tegning: Snitt A og B		Tegningsnr.: A30-01	Rev.: . Sign.: