



Fasade Nord Vest - Del øst

44.0

| Bolig D - Bruksareal (BRA) |                |                      | Bolig E - Bruksareal (BRA) |                |                      | Bolig F - Bruksareal (BRA) |                |                      |
|----------------------------|----------------|----------------------|----------------------------|----------------|----------------------|----------------------------|----------------|----------------------|
| Bolig                      | Etg.           | Areal                | Bolig                      | Etg.           | Areal                | Bolig                      | Etg.           | Areal                |
| 1D oppvarmet               | Plan 1. Etasje | 47.8 m <sup>2</sup>  | 1E oppvarmet               | Plan 1. Etasje | 72.5 m <sup>2</sup>  | 1F oppvarmet               | Plan 1. Etasje | 81.4 m <sup>2</sup>  |
| 2D oppvarmet               | Plan 2. Etasje | 61.6 m <sup>2</sup>  | 2E oppvarmet               | Plan 2. Etasje | 88.1 m <sup>2</sup>  | 2F oppvarmet               | Plan 2. Etasje | 78.2 m <sup>2</sup>  |
| 3D oppvarmet               | Plan 3. Etasje | 32.1 m <sup>2</sup>  | 3E oppvarmet               | Plan 3. Etasje | 48.2 m <sup>2</sup>  | 3F oppvarmet               | Plan 3. Etasje | 42.7 m <sup>2</sup>  |
| Total BRA                  |                | 141.5 m <sup>2</sup> | Total BRA                  |                | 208.8 m <sup>2</sup> | Total BRA                  |                | 202.4 m <sup>2</sup> |


FASADEFARGE: JOTUN 734 BRUNSVART NCS-KODE: 8501-G90Y

PLATER VED INNTREKK 1. OG 2. ETASJE ( inngangssoner og terrasser/balkonger): CEMBRIT, SOLID- S 353

HOVEDDØRER: VENSTRE: 1376 FROSTRØYK NCS-KODE: 1002-Y24R (Tilgjengelig bolig)  
MIDTRE: 1376 FROSTRØYK NCS-KODE: 1002-Y24R (Tilgjengelig bolig)  
HØYRE: 4109 GUSTAVIANSK BLÅ NCS-KODE: S3010-R80B

VINDUER: RAL 7022 UMBRAGRAU  
BELISTNING: SOM TILHØRENDE VEGG  
HÅGEØDER OG LEVEGGER MED FARGE SOM FASADE  
TAKTEKKING: FARGE MØRK GRÅ ELLER SVART  
BESLAG: MØRK GRÅ

— PLANERT TERRENG  
- - - NÅVÆRENDE TERRENG

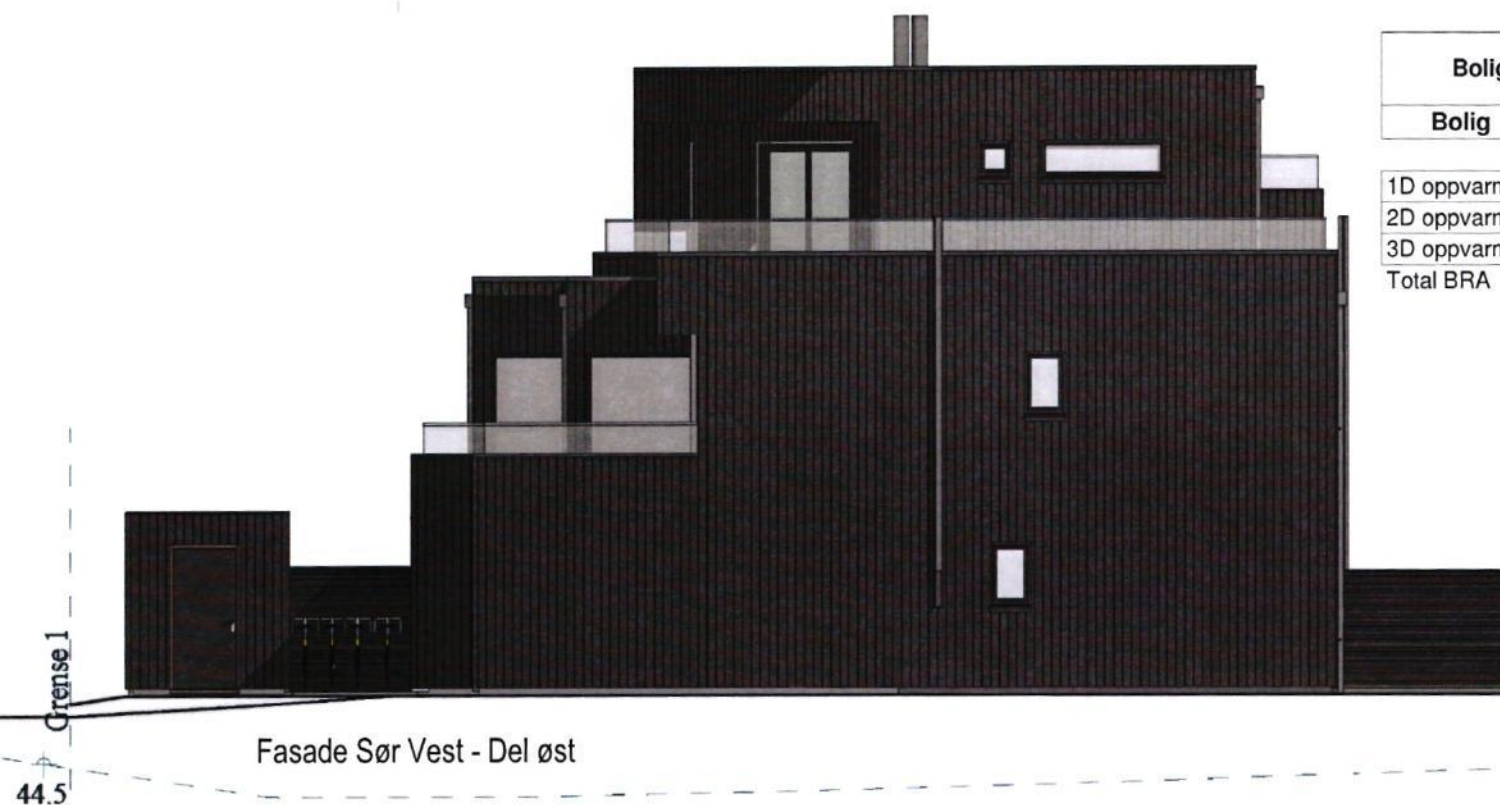

Fasade Sør Vest - Del øst

44.5

Fasade - Del Øst

Bygningens høydeplassering som er angitt på tegning, baserer seg på kjente opplysninger ved prosjekteringstidspunktet. Endelig høydeplassering må vurderes av kommune og ansvarlig for høydeplassering / utstikking på byggeplass.

|                              |                                   |                     |               |                                                                    |
|------------------------------|-----------------------------------|---------------------|---------------|--------------------------------------------------------------------|
| utbygger<br>Bygg. Egeland AS | Tiltakshaver:<br>Sørøhagane BKS 4 | Byggm. Egeland AS   | Rev:          | ARKITEKTKONTORET<br>med rom for<br>begeistning<br>IHT<br>www.ih.no |
|                              | Byggeplass:<br>Sørøhagane BKS 4   |                     | Format: A3    |                                                                    |
|                              | Kommune:<br>Sandnes               | G.nr: 45            | B.nr: 654     |                                                                    |
|                              | Tegn: HMB                         | Arkitekt: HMB       | Type: Spesial |                                                                    |
|                              | Dato: 20.03.19                    | Tegn.nr.: A3_BM_301 |               |                                                                    |
|                              | Skala: 1:100                      | Prosjekt.nr.: 8155  |               |                                                                    |

Tegningen må verken helt eller delvis kopieres eller benyttes ved utførelse av arbeider som ARKITEKTKONTORET IHT AS ikke medvirker i.