




Fasade Sør Øst - Del øst

44.0

44.0

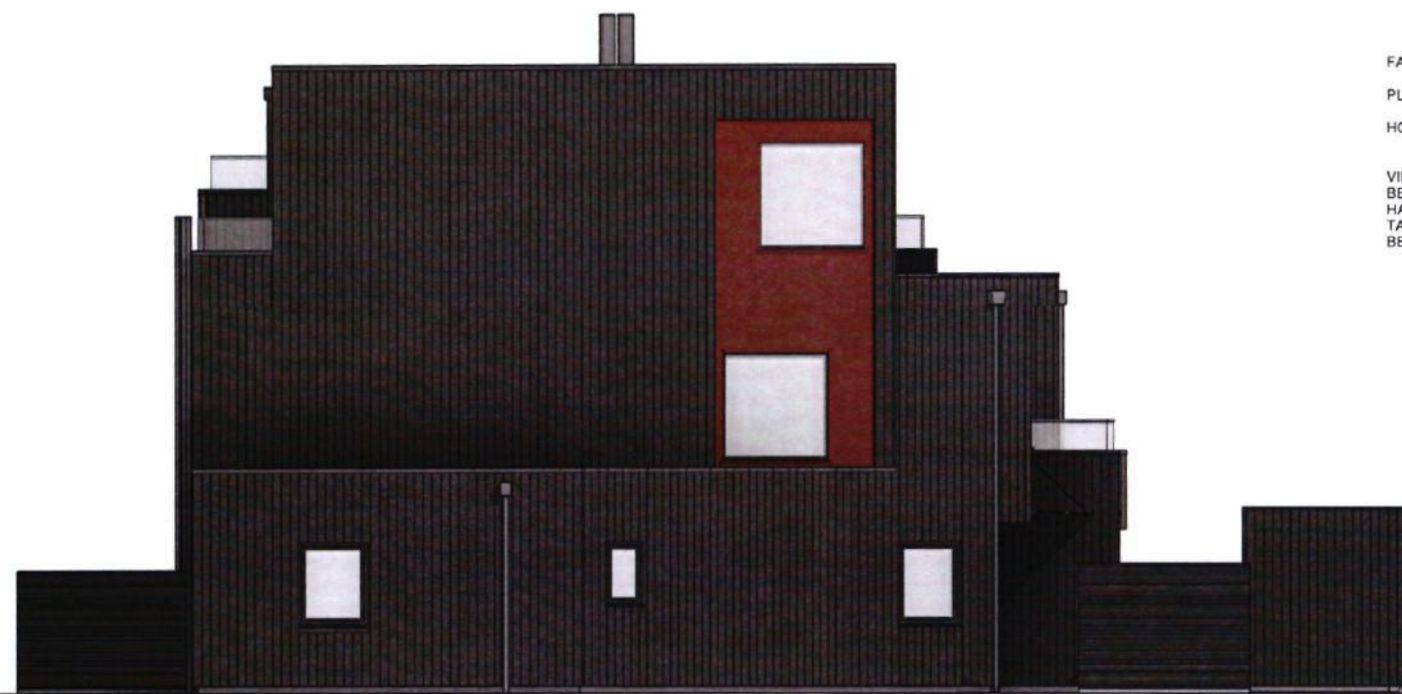

Fasade Nord Øst - Del øst

44.0

FASADEFARGE: JOTUN 734 BRUNSVART NCS-KODE: 8501-G90Y
 PLATER VED INNTREKK 1. OG 2. ETASJE (inngangssoner og terrasser/balkonger): CEMBRIT, SOLID- S 353
 HOVEDDØRER: VENSTRE: 1376 FROSTRØYK NCS-KODE: 1002-Y24R (Tilgjengelig bolig)
 MIDTRE: 1376 FROSTRØYK NCS-KODE: 1002-Y24R (Tilgjengelig bolig)
 HØYRE: 4109 GUSTAVIANSK BLÅ NCS-KODE: S3010-R80B
 VINDUER: RAL 7022 UMBRAGRAU
 BELISTNING: SOM TILHØRENDE VEGG
 HAGEBODER OG LEVEGGER MED FARGE SOM FASADE
 TAKTEKKING: FARGE MØRK GRÅ ELLER SVART
 BESLAG: MØRK GRÅ

— PLANERT TERRENG
 - - - NÅVÆRENDE TERRENG

Bygningens høydeplassering som er angitt på tegning, baserer seg på kjente opplysninger ved prosjekteringstidspunktet. Endelig høydeplassering må vurderes av kommune og ansvarlig for høydeplassering / utstikking på byggeplass.

Fasade Del Øst

utbygger Bygg. Egeland AS	Tiltakshaver:	Sørbohagane BKS 4	Byggm. Egeland AS	Rev:	
	Byggeplass:	Sørbohagane BKS 4		Format:	A3
	Kommune:	Sandnes	G.nr: 45	B.nr:	654
	Tegn:	HMB	Arkitekt: HMB	Type:	Spesial
	Dato:	20.03.19	Tegn.nr.: A3_BM_302		
	Skala:	1:100	Prosjekt.nr.: 8155		
Tegningen må verken helt eller delvis kopieres eller benyttes ved utførelse av arbeider som ARKITEKTKONTORET IHT AS ikke medvirker i.					

ARKITEKTKONTORET
 med rom for
 bevisning
IHT
 www.ih.no