




Sandnes kommune

Situasjonskart

Eiendom: 45/654
Adresse: Bronsekarveien 17
Dato: 23.10.2023
Målestokk: 1:500



UTM-32

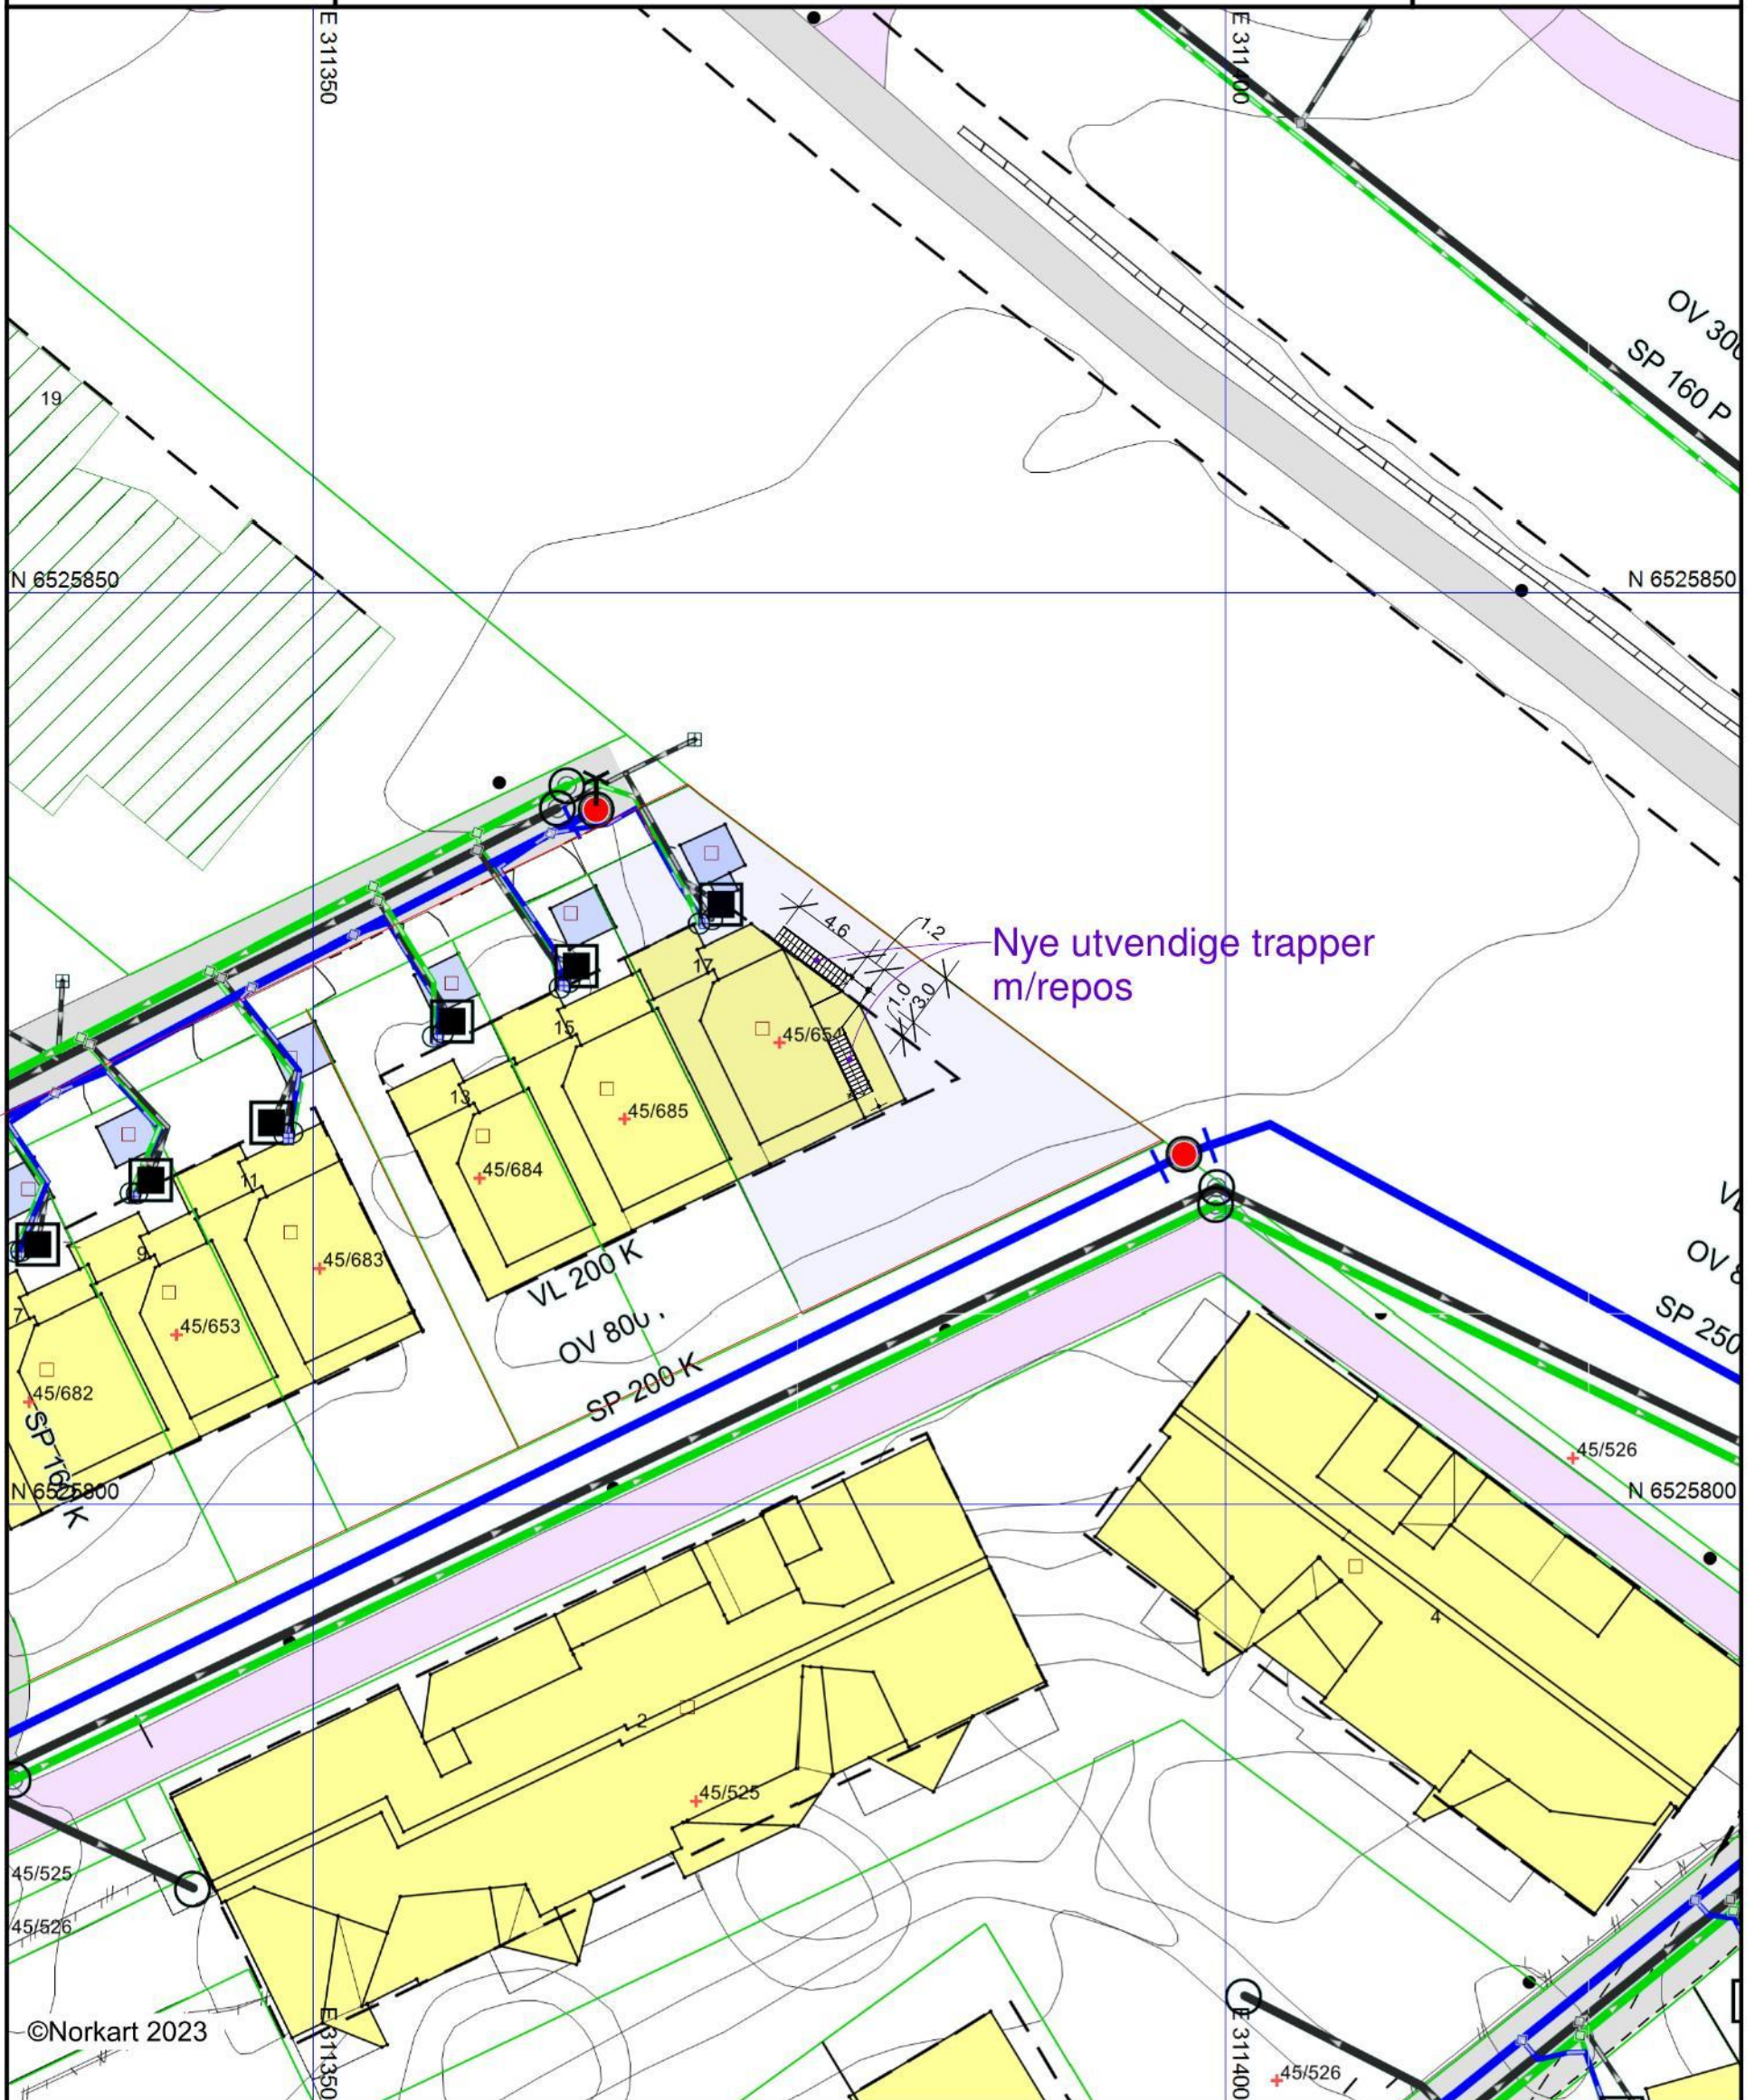

- 1) Det tas forbehold om feil i kartgrunnlaget
- 2) Ved utskrift fra PDF-fil kan målestokken bli unøyaktig