




Alle vertikale mål på snitt angir ferdige rom-høyder.
For utførelse av grunnmur/støpt plate, konf. nødv. U-verdier
og egne detaljer fra byggefirma/leverandør/produzent eller NBI.

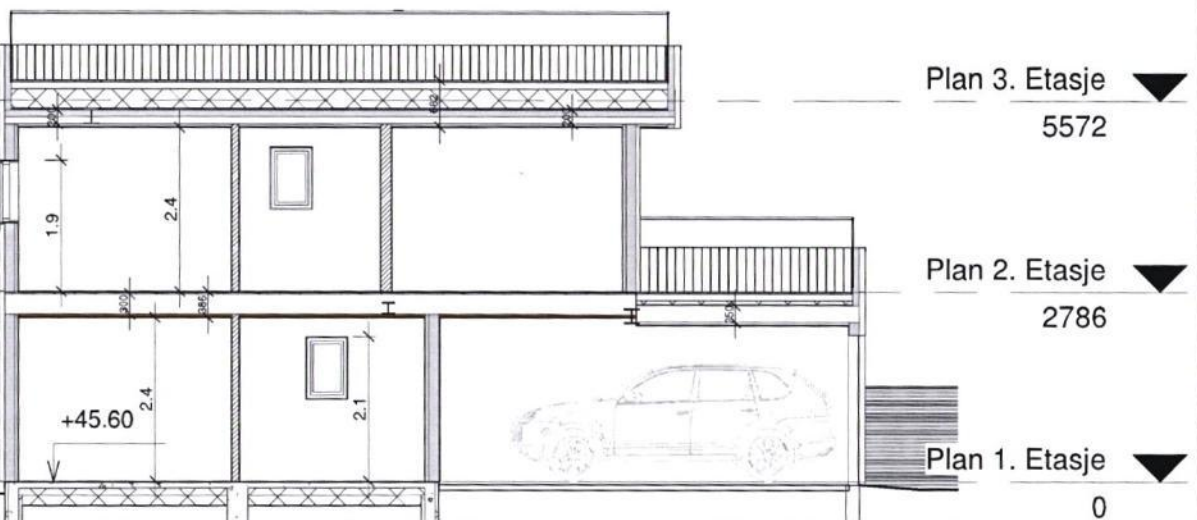

Snitt B-B

Snitt A-A, B-B og C-C Del Øst

utbygger Bygg. Egeland AS	Tiltakshaver:		Rev:	ARKITEKTKONTORET <i>med rom for begjæring</i> IHT www.ih.no
	Sørbohagane BKS 4	Byggm. Egeland AS		
	Byggeplass:		Format: A3	
	Sørbohagane BKS 4			
	Kommune:		B.nr: 654	
	Sandnes		G.nr: 45	
Tegn: HMB	Arkitekt: HMB		Type: Spesial	
Dato: 20.03.19	Tegn.nr.: A3_BM_201			
Skala: 1:100	Prosjekt.nr.: 8155			

Tegningen må verken helt eller delvis kopieres eller benyttes ved utførelse av arbeider som ARKITEKTKONTORET IHT AS ikke medvirker i.

Tegningen må verken helt eller delvis kopieres eller benyttes ved utførelse av arbeider som ARKITEKTKONTORET IHT AS ikke medvirker i.