


1. Etasje

1 : 100


ROMSKJEMA

HAGESTUE

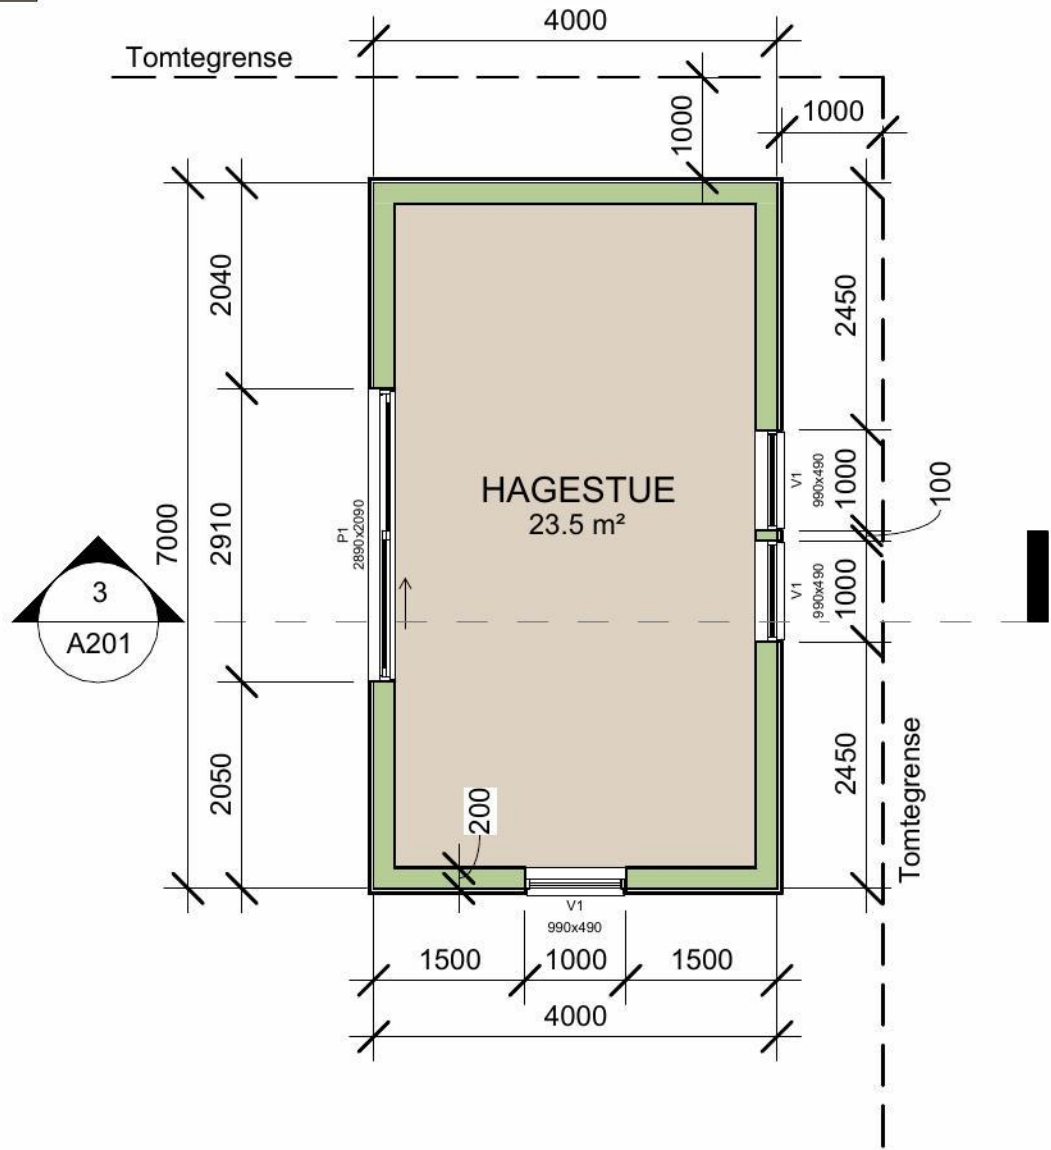

3 AA

1 : 100

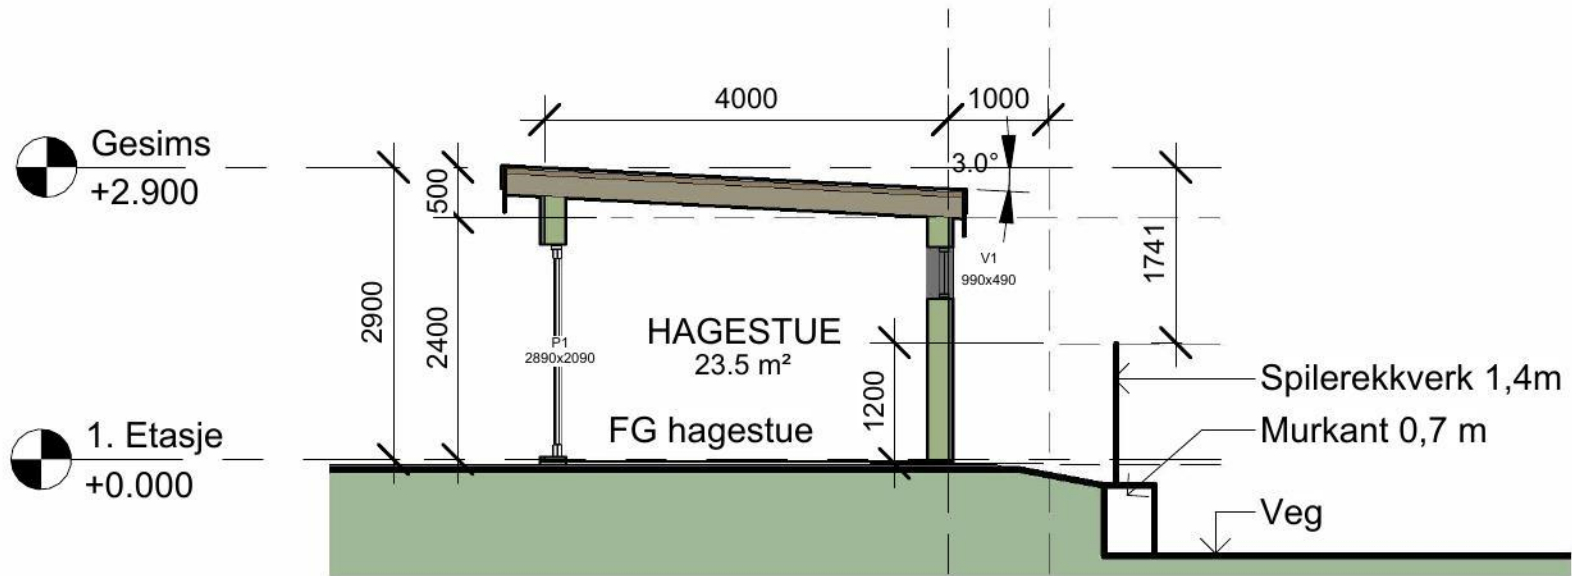

2 3D View 1



4 BYA

1 : 200



5 BRA

1 : 200



FORPROSJEKT

ARKITEKT
GISKEGJERDE



Arkitekt Giskegjerde AS
email: kenneth@arkgiske.no
hjemmeside: www.arkgiske.no
Tlf: 56 33 53 41
Forsikring: Gjensidige ASA

I samarbeid med:

Volynets
architectural bureau

HAGESTUE

A201

HAGESTUE GBNR 33-876

SN-001

målestokk / ark	arkitekt / kontroll	dato	tiltakshaver
As indicated A3	KAG HS	24012024	Chriss Rovik