
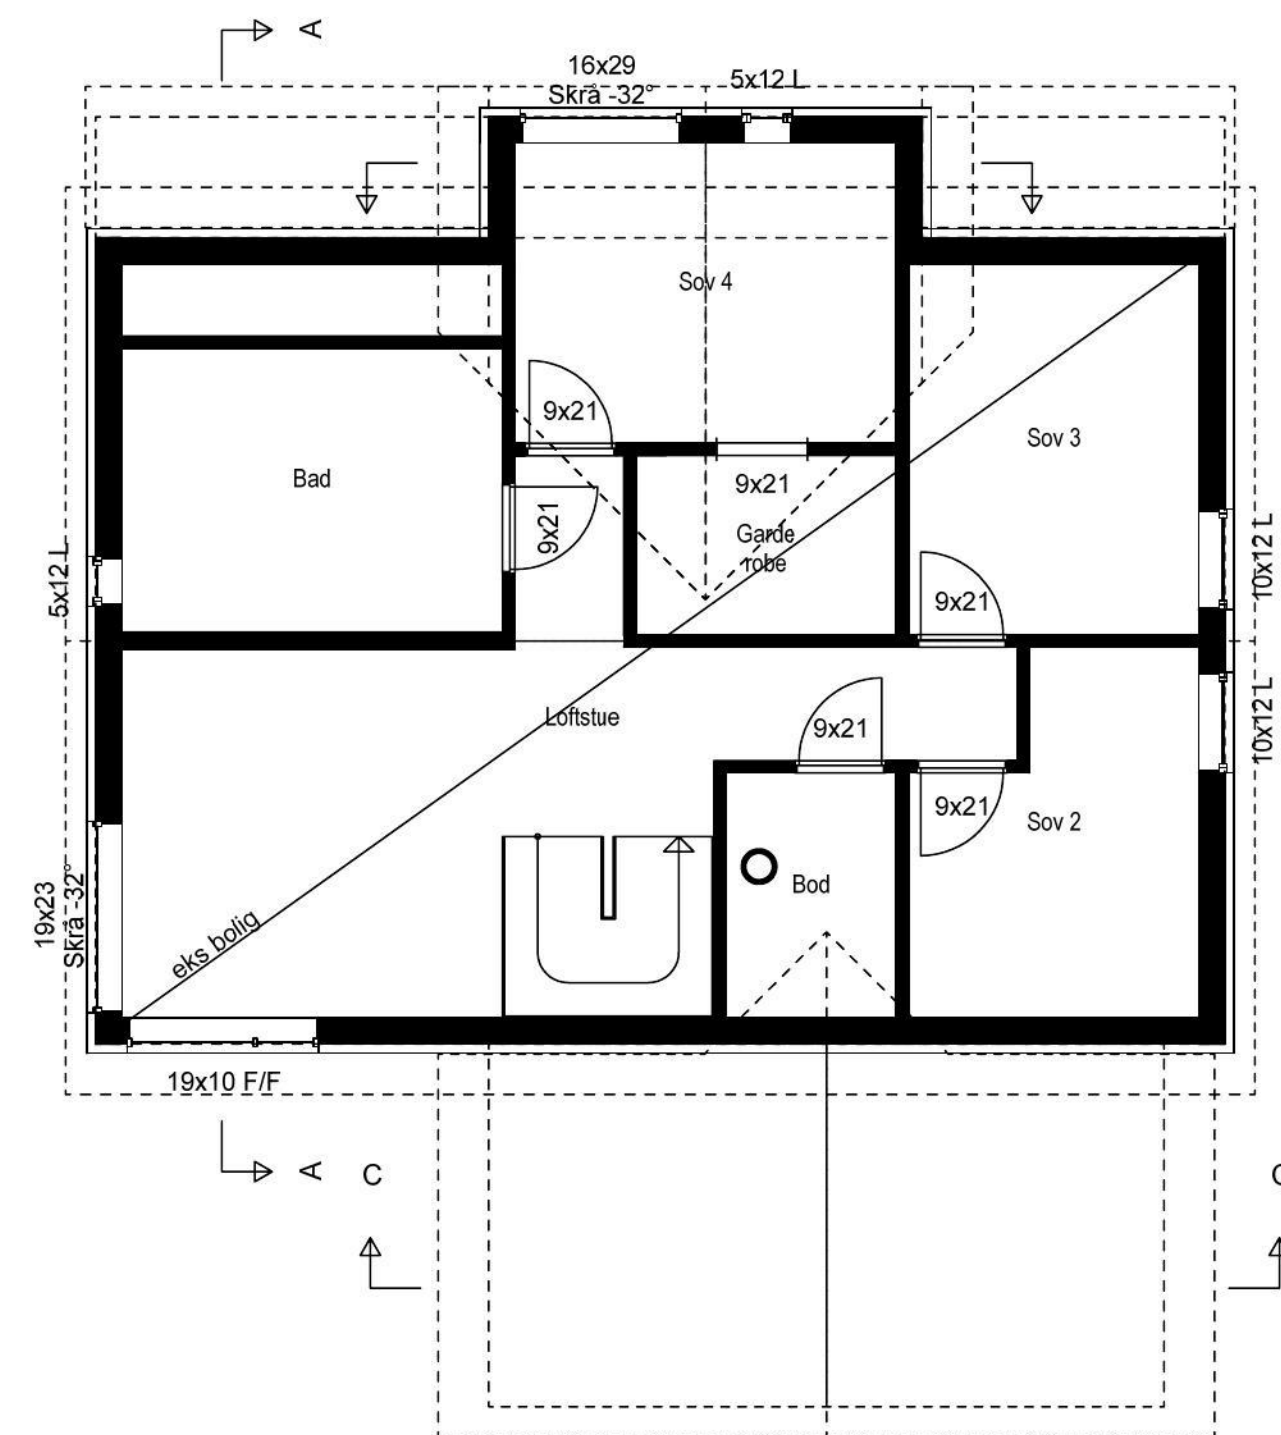


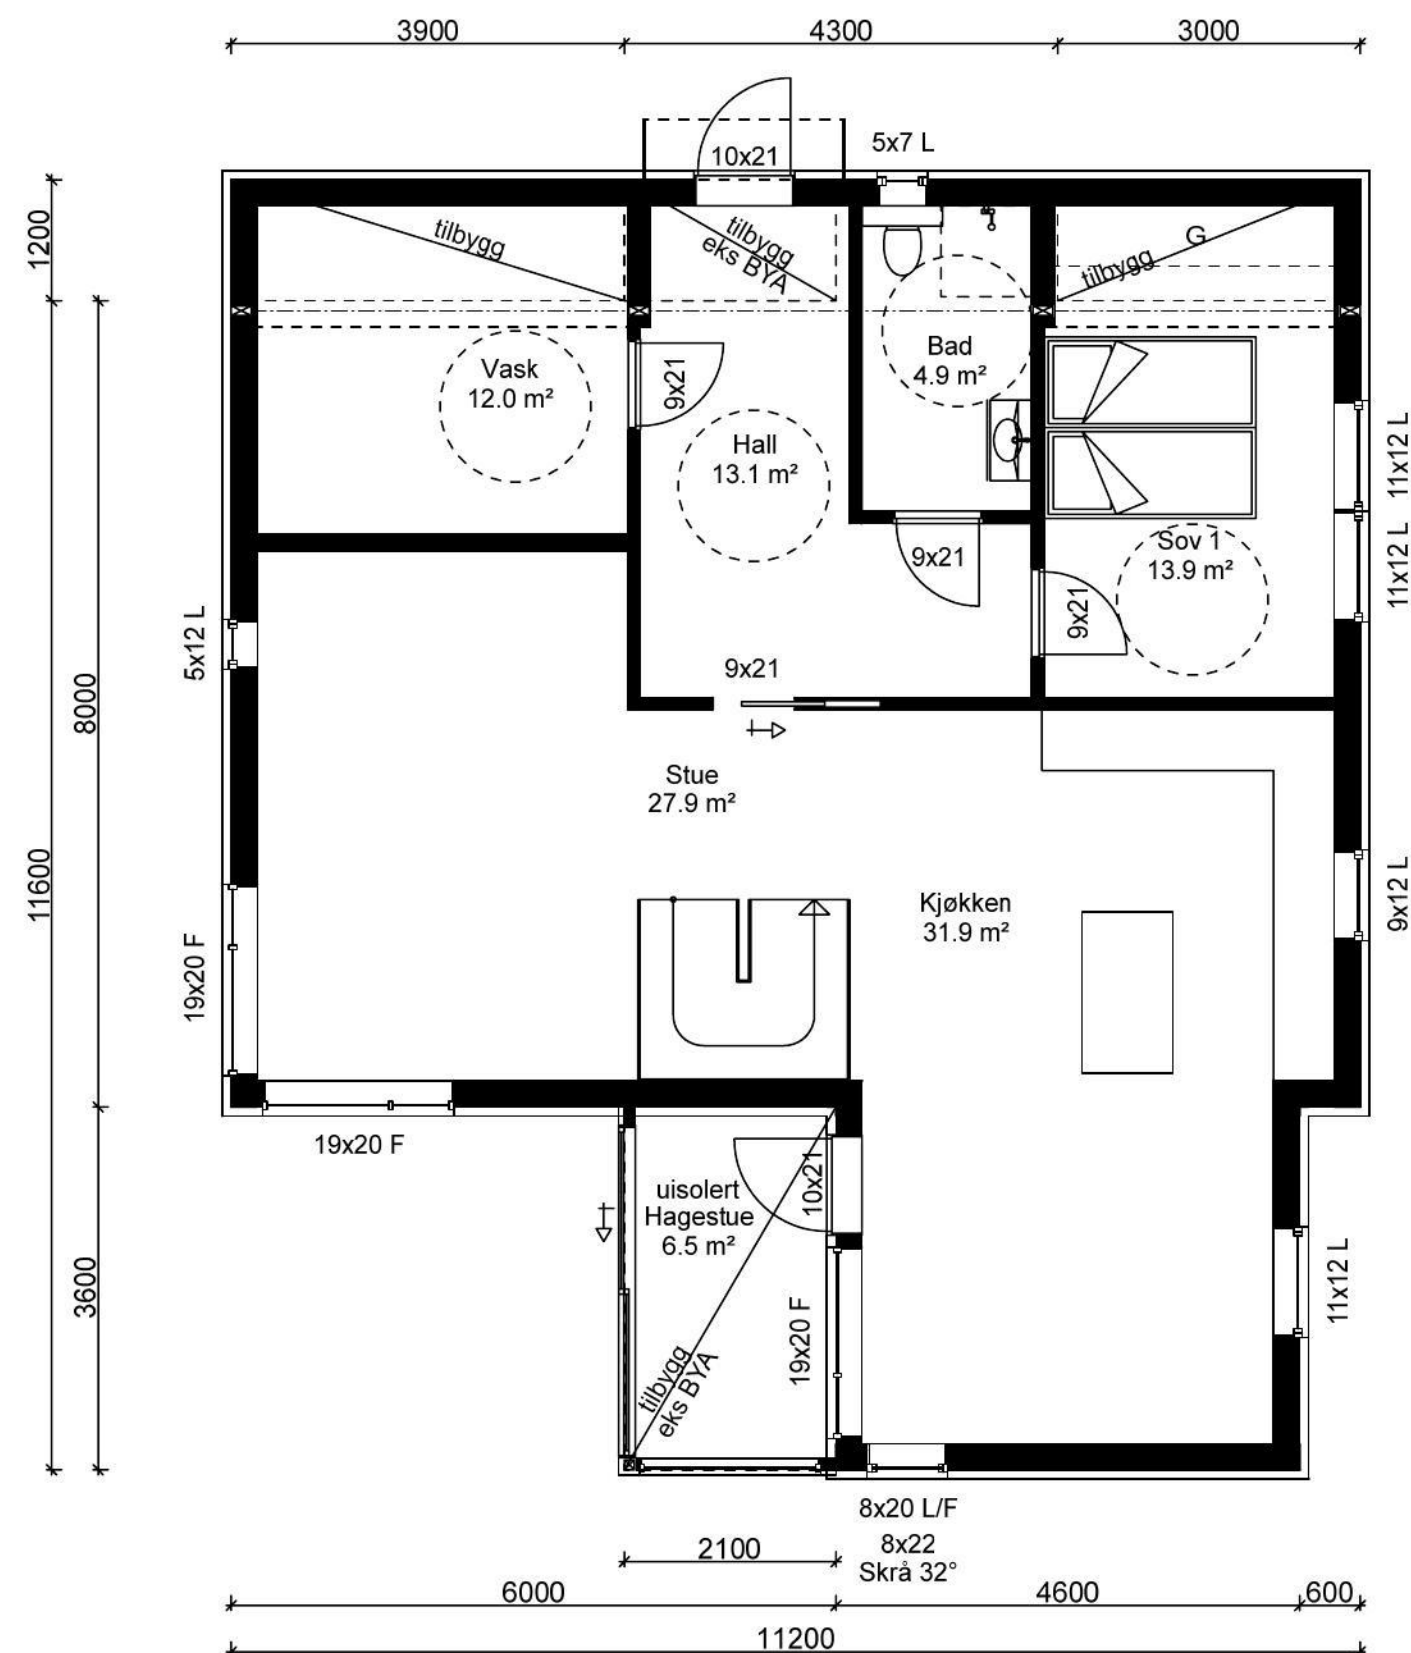

BYA bolig og garasje: 130,8+50 = 180,8 m²
BYA 180,8/497 => 36,4%

Tilbygg				Eks bolig		
Arealberegninger i hht. NS 3940	Bruksareal BRA kvm			Arealberegninger i hht. NS 3940	Bruksareal BRA kvm	
	Pr etasje	uisolert hagestue	Sum BRA		Pr etasje	Sum BRA
1. etasje	10.8	6.5	17.3	1. etasje	96.6	96.6
SUM :	10.8	6.5	17.3	2. etasje	78.3	78.3
BYA :	8.4	0.0	8.4	SUM :	174.9	174.9
				BYA :	113.2	122.4

Tiltakshaver: Yifei Zhu og Bjarne PS Lindman			Målestokk	Tegn AIL	Dato 04.12.2023
Byggeplass : Draugveien 173B			1:100	Trac	Dato
Kommune : Sandnes			Gnr69	Bnr3116	Disk Draugvei
Utbygger			Sak		
Planlegger			Tegn nr Drau1502		
ark1			Prosj nr		
anniren@ark-1.no - tlf 99090113					