


Beregninger i hht NS3940

Arealer (m²)	BRA
Hovedplan	96.6
Etg.plan	78.3
Tilleggsareal utvendig	8.2
Bruksareal bolig	175
Totalt bruksareal	183

Bebygd areal bolig (BYA) 122

Areal av primærrom (P-rom) 160

Forutsetter etablering av 5m²
tilgjengelig utvendig sportsbod.

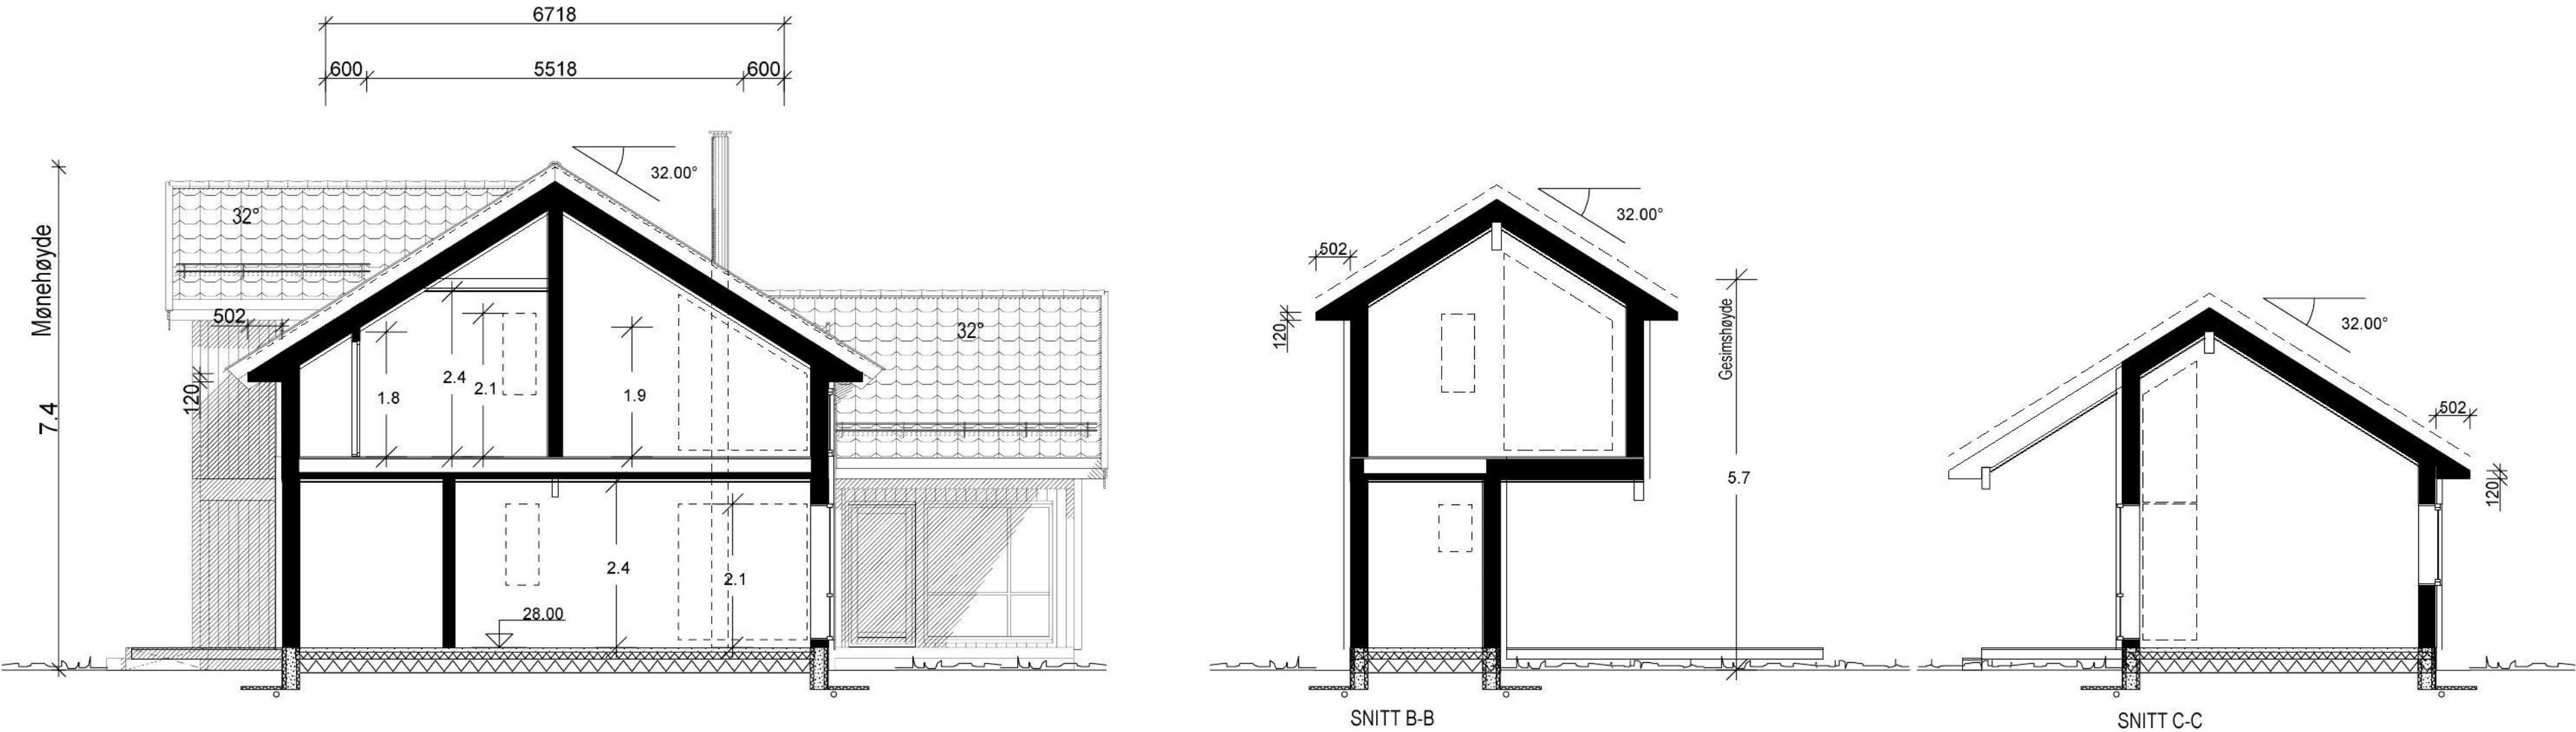

Prato spes.

SNITT OG AREALER	Tiltakshaver : BoligPartner AS, avd. Stavanger		MÅL 1 : 100
			Dato 24.10.18 Sign.HB
	Byggeplass : Draugveien 173 B, 4314 Sandnes		Pnr.:P171020270101
			Tegnings Nr. — 501

BoligPartner

Denne tegning tilhører BoligPartner AS og kan ikke benyttes uten skriftlig samtykke