


- A = Avstivende vegg
B = Bærevegg
L = Åpningsbart vindu
F = Fast vindu
L/F = Fast med åpningsbart felt iht. fasade
Syn = Synlig drager
Skj = Skjult drager

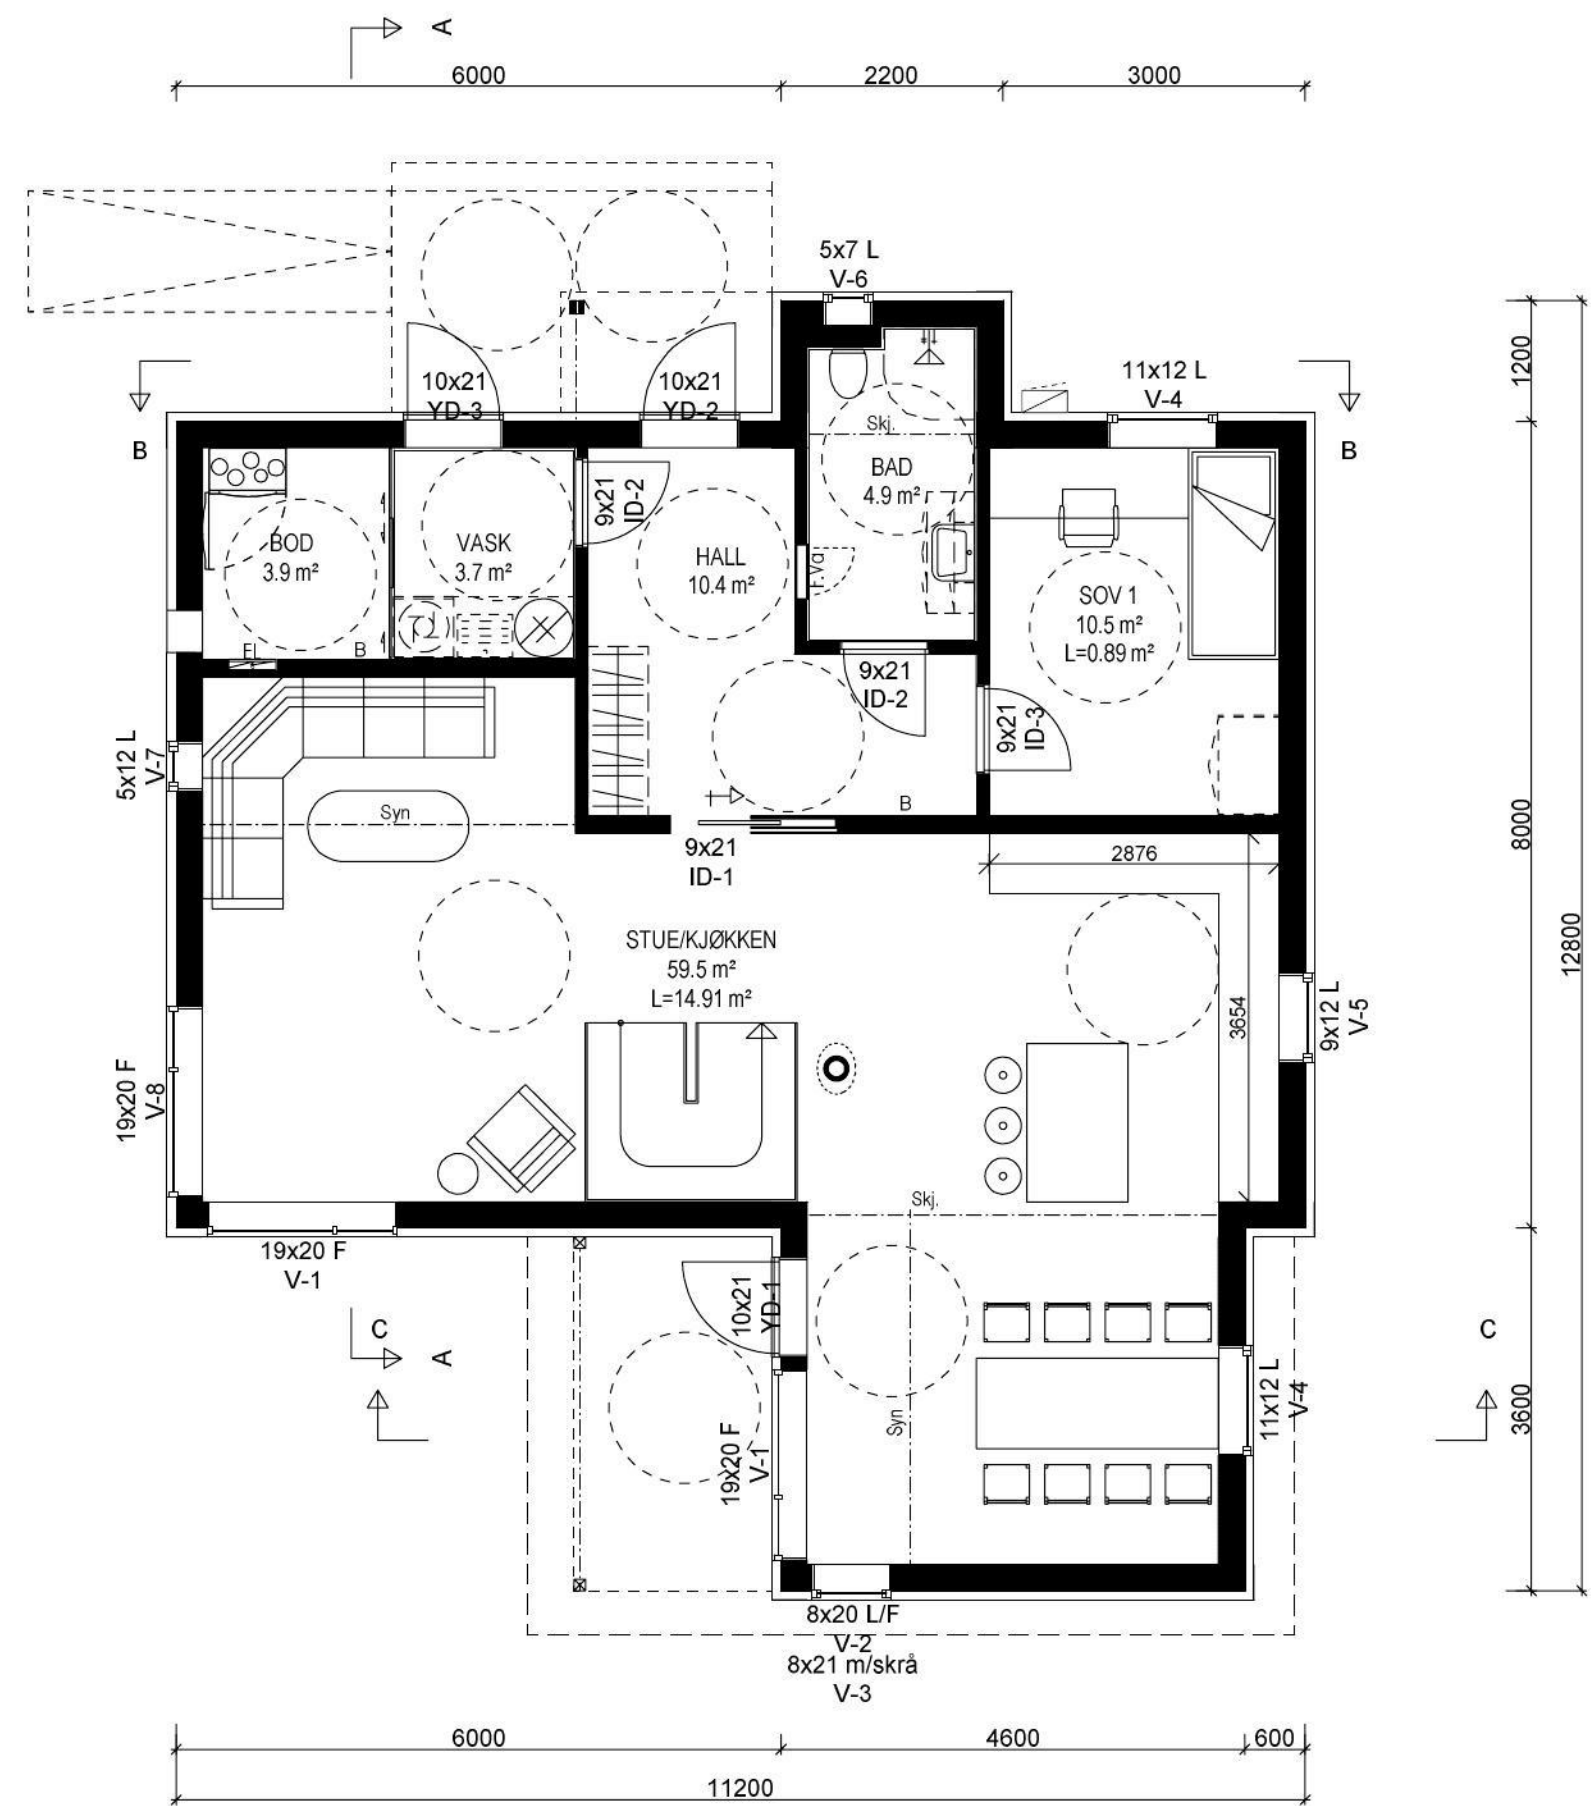

Prato spes.

El.skap, fjernet brannmur 06.11.18 HB A

HOVEDPLAN 1.etg. <i>BoligPartner</i> Denne tegning tilhører BoligPartner AS og kan ikke benyttes uten skriftlig samtykke	Tiltakshaver : BoligPartner AS, avd. Stavanger		MÅL 1 : 100
	Byggeplass : Draugveien 173 B, 4314 Sandnes		Dato 24.10.18 Sign.HB
	Gnr: 69 Bnr: 3116 Fnr:		Pnr.:P171020270101
			Tegnings Nr. — 502 A