


- A = Avstivende vegg
B = Bærevegg
L = Åpningsbart vindu
F = Fast vindu
L/F = Fast med åpningsbart felt iht. fasade
Syn = Synlig drager
Skj = Skjult drager

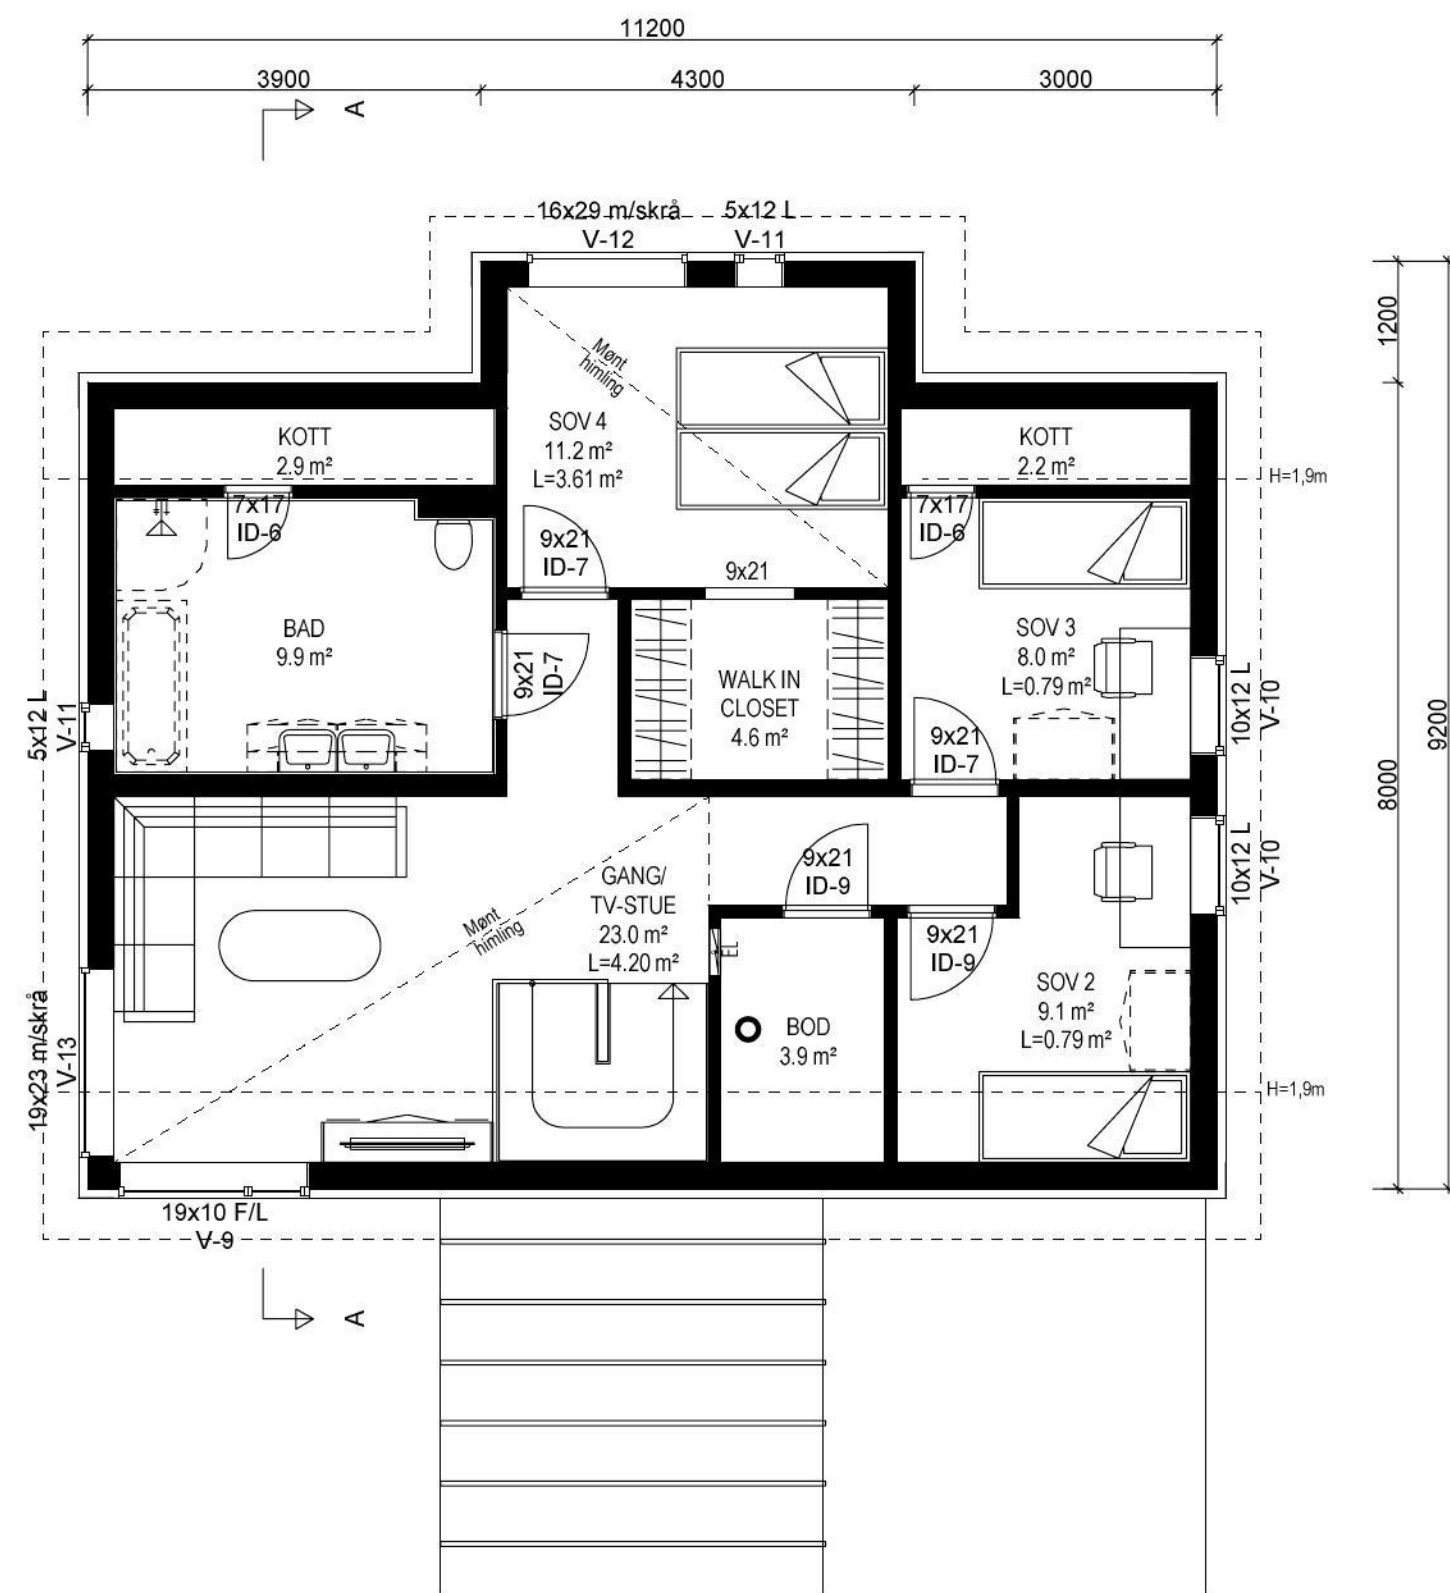

Prato spes.

Fjernet sikringsskap, endret romareal i tvstue/gang 06.11.18 HB A

LOFTPLAN 2.etg.

Tiltakshaver :
BoligPartner AS, avd. Stavanger

MÅL 1 : 100

Dato 24.10.18 Sign.HB

Pnr.:P171020270101

Byggeplass :
Draugveien 173 B, 4314 Sandnes

Gnr: 69
Bnr: 3116
Fnr:

Tegnings Nr.
— 503 A

BoligPartner

Denne tegning tilhører BoligPartner AS og kan ikke benyttes uten skriftlig samtykke