
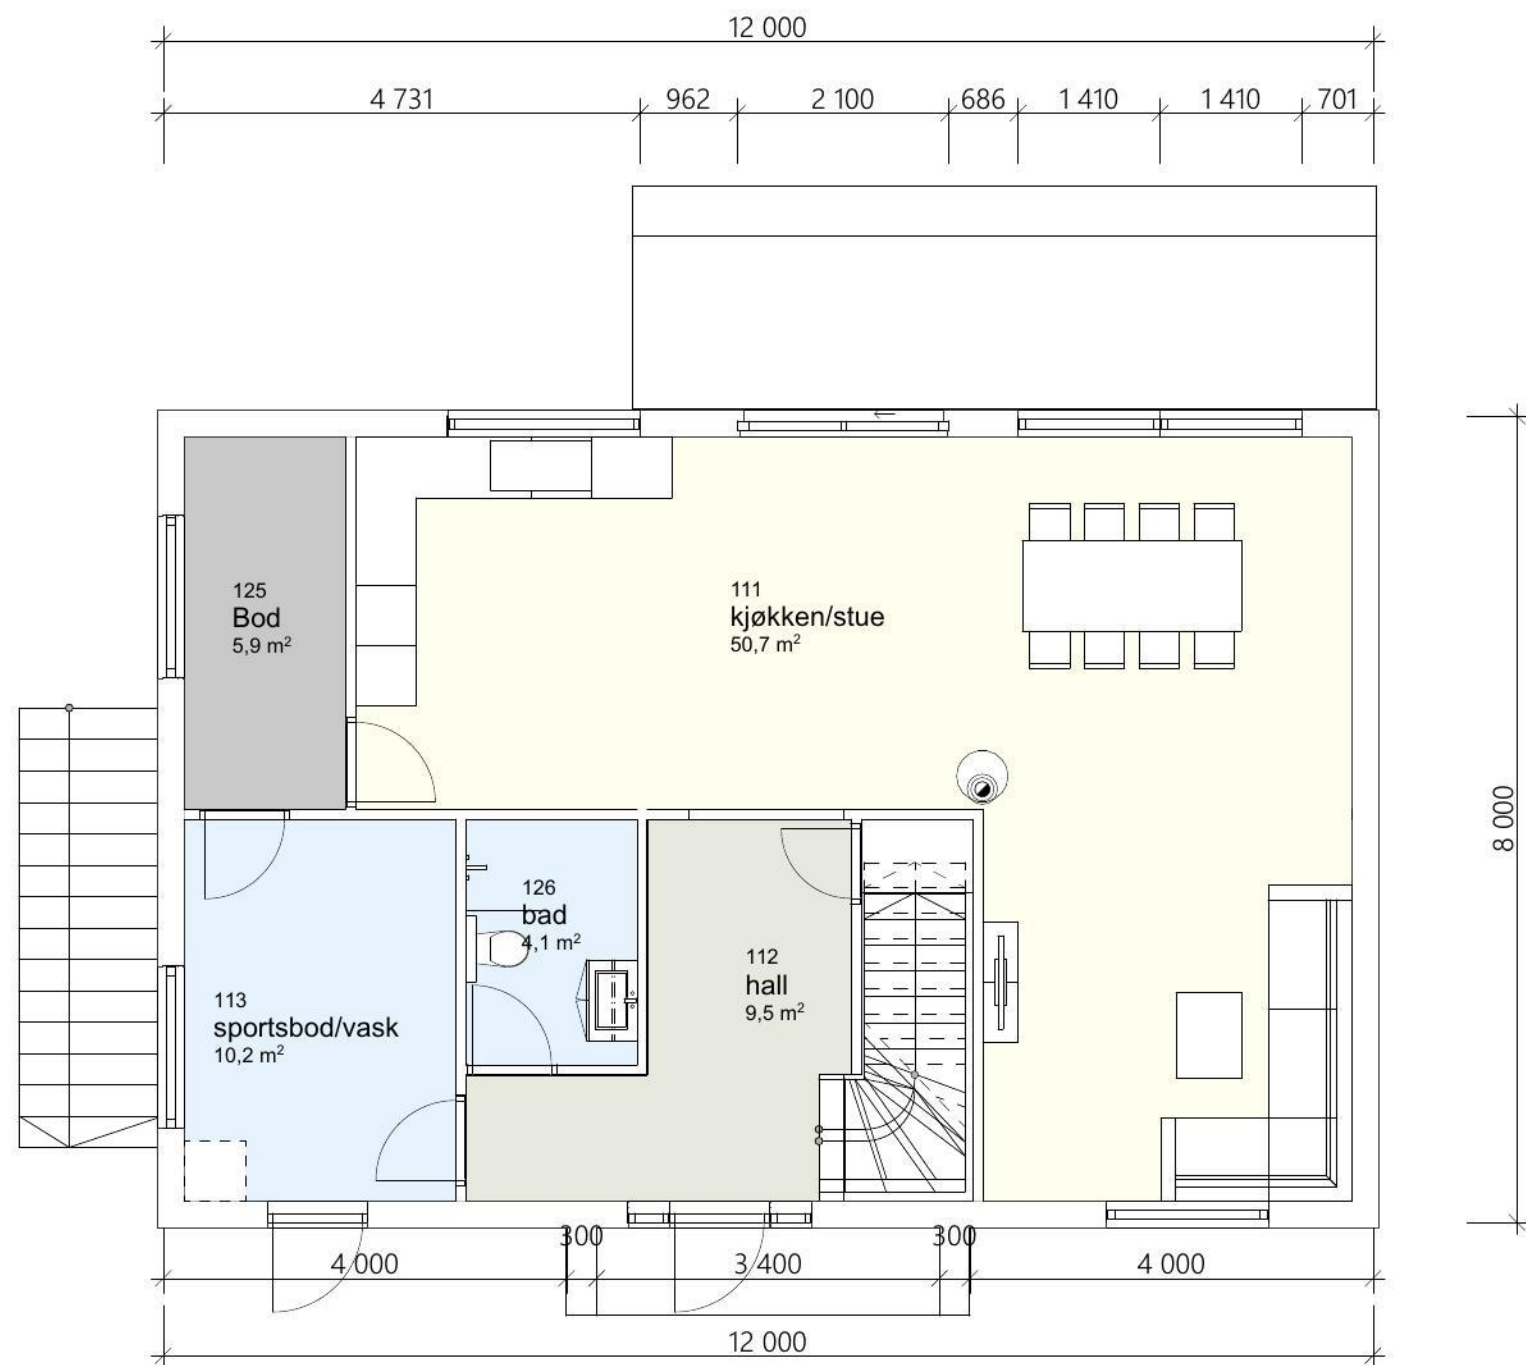
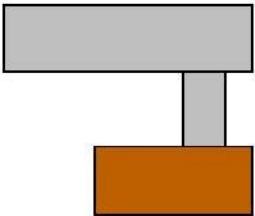


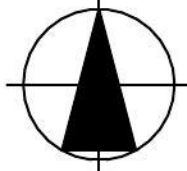

BRA: kjeller 80m2
1.etg 88m2
2.etg 74m2
Total BRA:242m2
BYA: bolig 98m

Tegningsnr. A20-3		Revisjon nr.	
Type tegning Plan 1.etg	
<table><tr><td>REV</td><td></td><td>23.12.2022</td><td></td></tr><tr><td>REV</td><td></td><td>26.05.2023</td><td></td></tr><tr><td></td><td></td><td></td><td></td></tr><tr><td></td><td></td><td></td><td></td></tr><tr><td></td><td></td><td></td><td></td></tr><tr><td></td><td></td><td></td><td></td></tr><tr><td></td><td></td><td></td><td></td></tr><tr><td></td><td></td><td></td><td></td></tr><tr><td></td><td></td><td></td><td></td></tr><tr><td></td><td></td><td></td><td></td></tr><tr><td>Rev</td><td>Nr</td><td>Beskrivelse</td><td>Dato</td></tr><tr><td></td><td></td><td></td><td>Sign</td></tr><tr><td></td><td></td><td></td><td>Kontr</td></tr></table>				REV		23.12.2022		REV		26.05.2023																																		Rev	Nr	Beskrivelse	Dato				Sign				Kontr
REV		23.12.2022	
REV		26.05.2023	
Rev	Nr	Beskrivelse	Dato	
			Sign	
			Kontr	
Lokalisering: 	
Prosjekteringsgruppen ● ARK : Skjærgårdsbygg a/s ● RIB : Rådg. ing. Bygg ● RIE : Rådg. ing. Elektro ● RIV : Rådg. ing. VVS Østerøya 240 4625 Flekkerøy Tlf.: 90522750 steinar@skjaergardsbygg.no RIBveien18 0000 RIBbyen Tlf: 000 00 000 rib@ribfirma.no RIEveien18 0000 RIEbyen Tlf: 000 00 000 rie@riefirma.no RIVveien18 0000 RIVbyen Tlf: 000 00 000 riv@rivfirma.no	
	
Tiltakshaver Skjærgårdsbygg a/s		Godkjent	
Prosjekt Paulen 77 Skålevig 4625 Flekkerøy		Kontroll prosjekt. Sign. Kontroll	
Gnr./Bnr./Festenr.: Gnr2/Bnr628		Filnavn Paulen 77.pln	
Dato 14.09.2022		Målestokk 1:100	
Kontroll utførende		Sign. Kontroll	
Prosjektnr.: Prosjektnr.		Tegningsnr.: A20-3	
Type tegning: Plan 1.etg		Prosjektnr. for prosjekterende/lev.	