



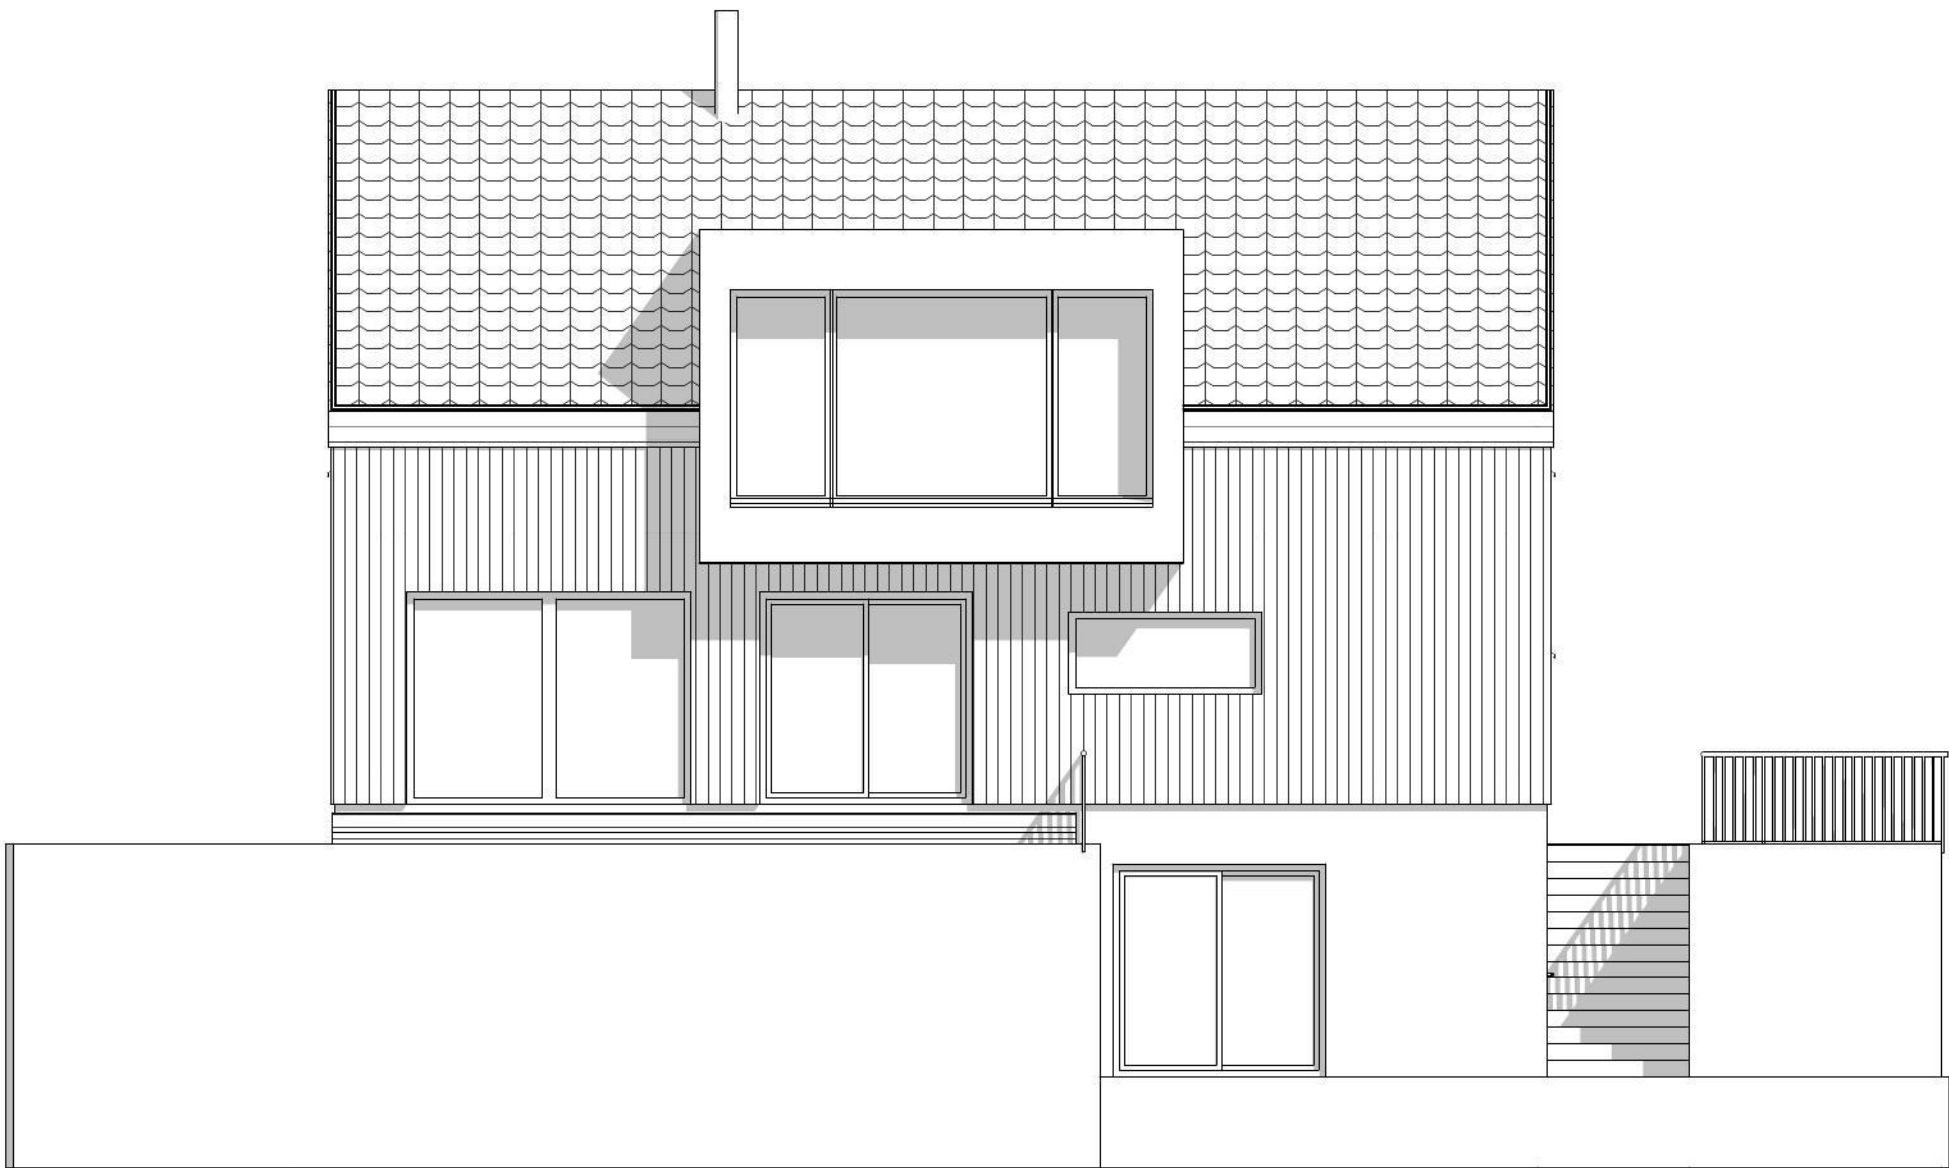

1:100 Fasade Øst

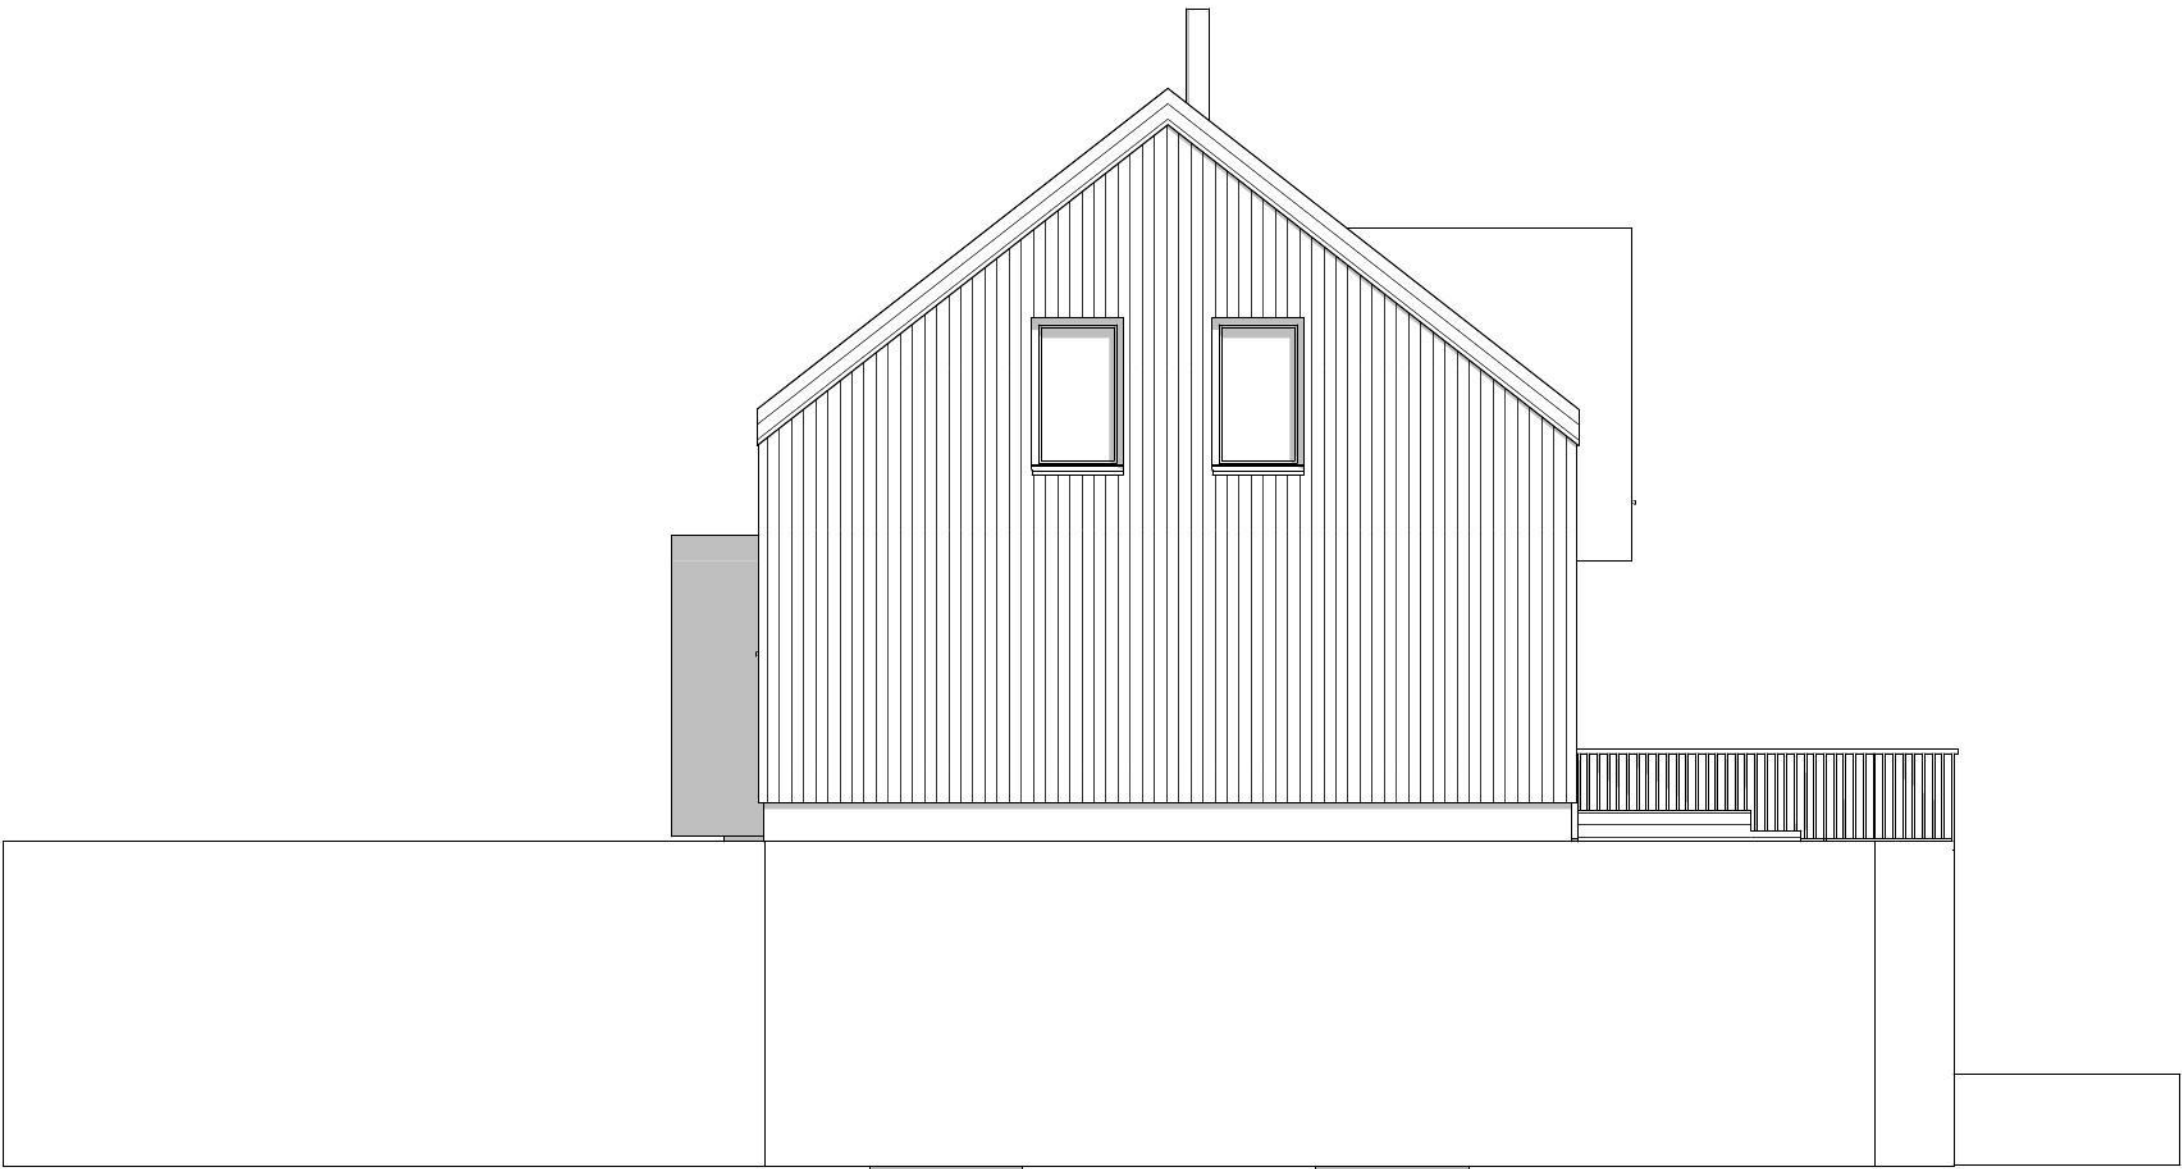

1:100 Fasade Sør

Tegningsnr. A40-2		Revisjon nr.			
Type tegning Fasade Sør og Øst					
REV		23.12.2022			
REV		26.05.2023			
Rev	Nr	Beskrivelse	Dato	Sign	Kontr
Lokalisering:					
Prosjekteringsgruppen					
● ARK :		Skjærgårdsbygg a/s		Østerøya 240 4625 Flekkerøy Tlf.: 90522750 steinar@skjaergardsbygg.no	
● RIB :		Rådg. ing. Bygg		RIBveien18 0000 RIBbyen Tlf: 000 00 000 rib@ribfirma.no	
● RIE :		Rådg. ing. Elektro		RIEveien18 0000 RIEbyen Tlf: 000 00 000 rie@riefirma.no	
● RIV :		Rådg. ing. VVS		RIVveien18 0000 RIVbyen Tlf: 000 00 000 riv@rivfirma.no	
Tiltakshaver				Godkjent	
Skjærgårdsbygg a/s				Kontroll prosjekt.	
				Sign.	Kontroll
Prosjekt				Filnavn	
Paulen 77				Paulen 77.pln	
Skålevig				Dato	
4625 Flekkerøy				14.09.2022	
				Målestokk	
				1:100	
				Kontroll utførende	
Gnr./Bnr./Festenr.:				Sign.	Kontroll
Gnr2/Bnr628					
Prosjektnr.:		Tegningsnr.:		Prosjektnr. for	
Prosjektnr.		A40-2		prosjekterende/lev.	
Type tegning:					
Fasade Sør og Øst					