



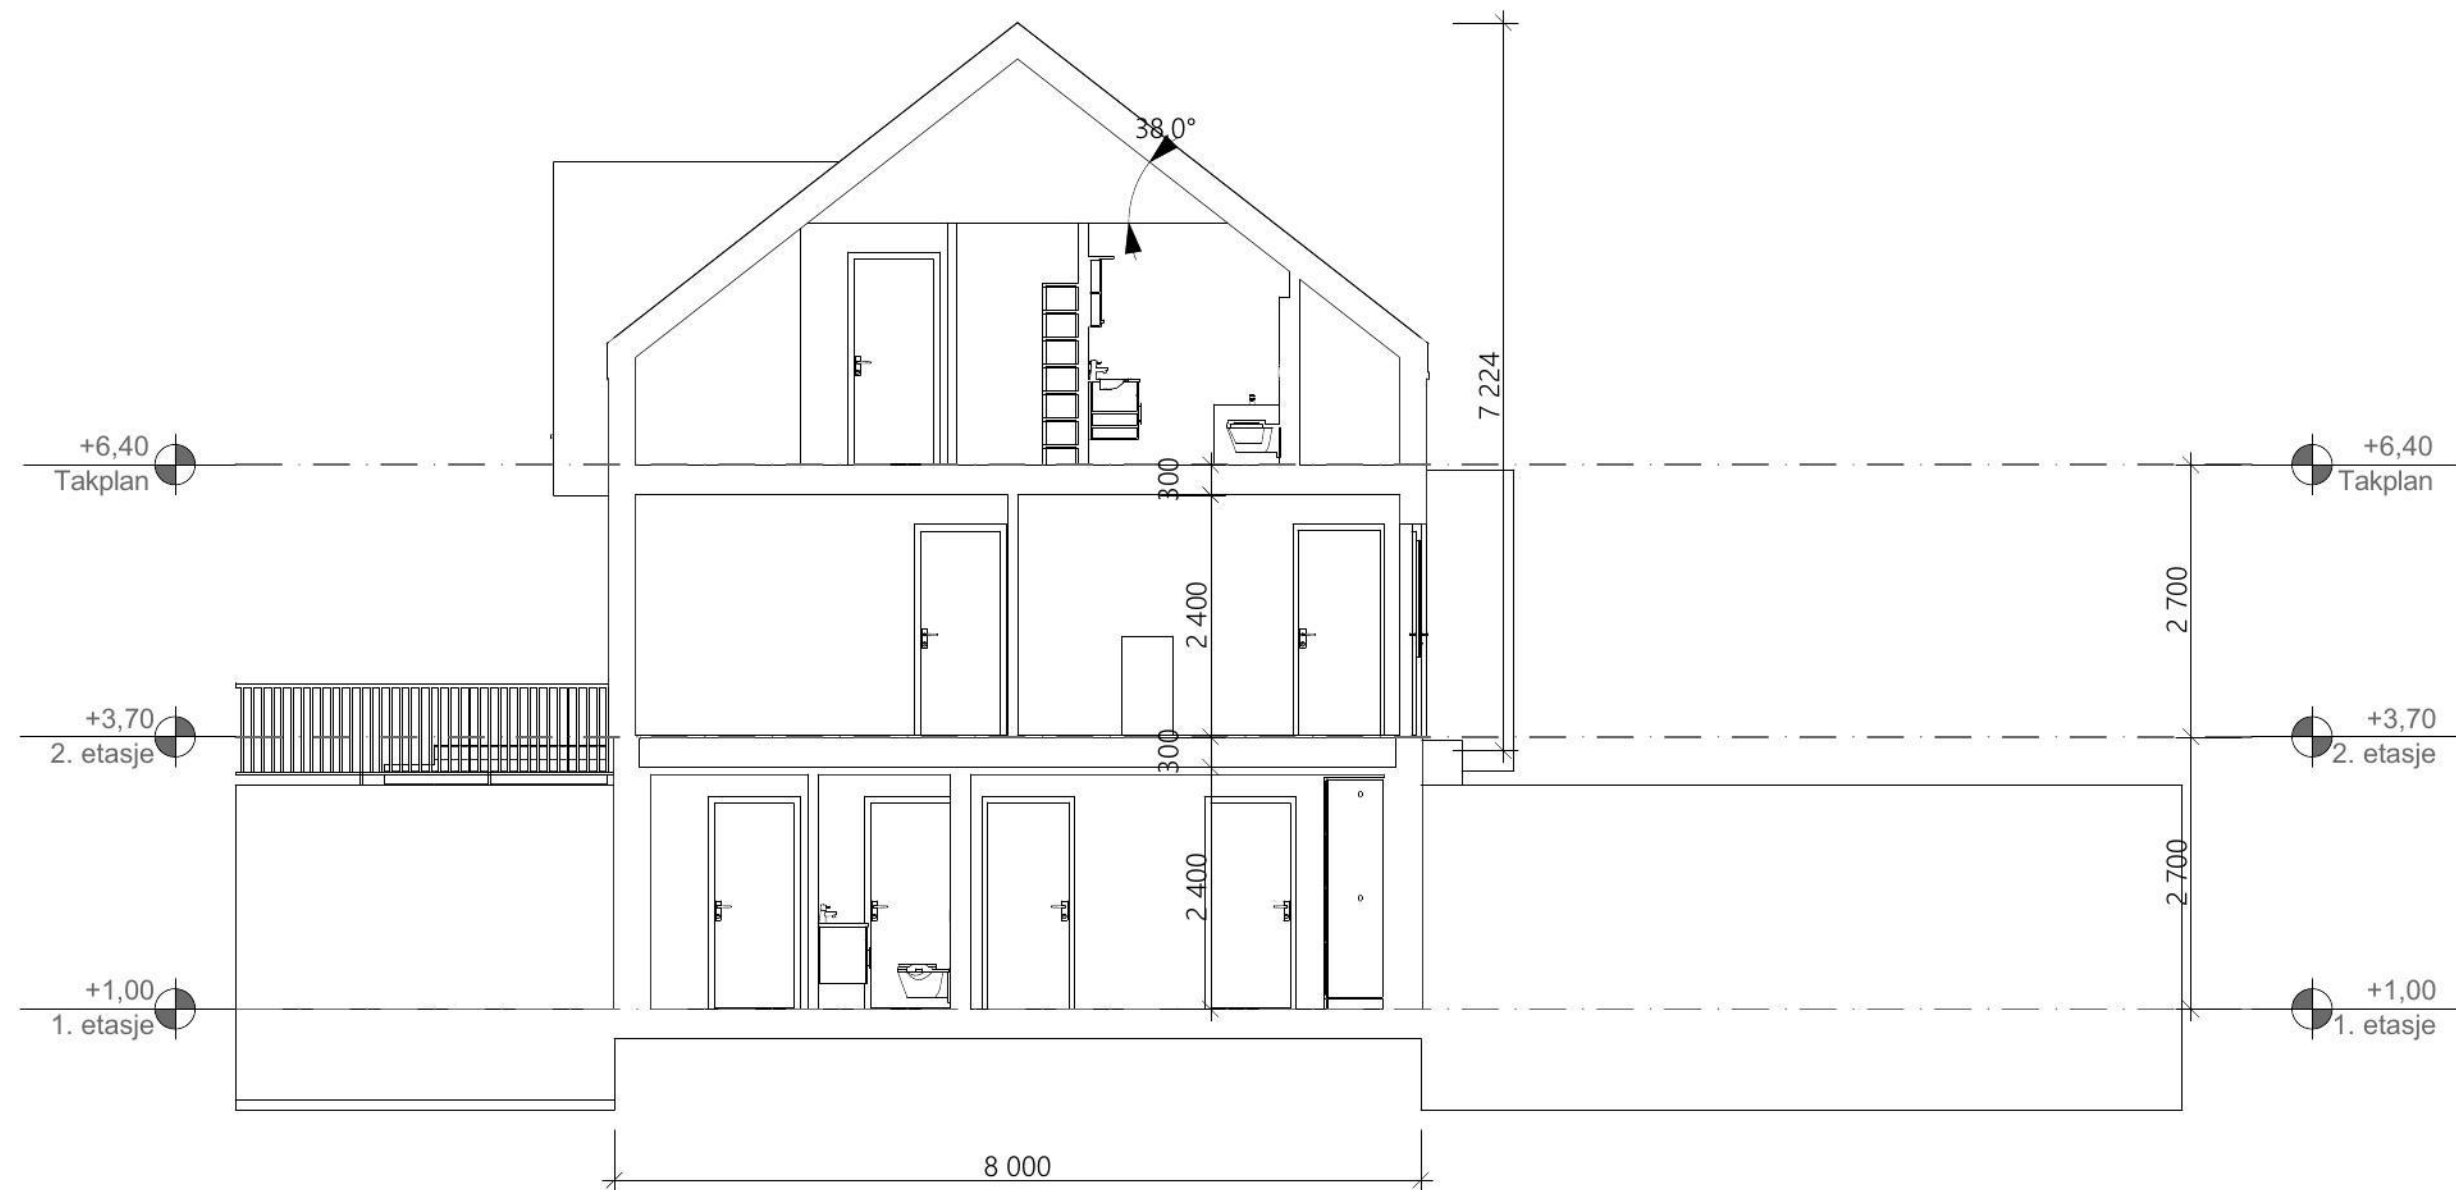

1:100 Snitt A

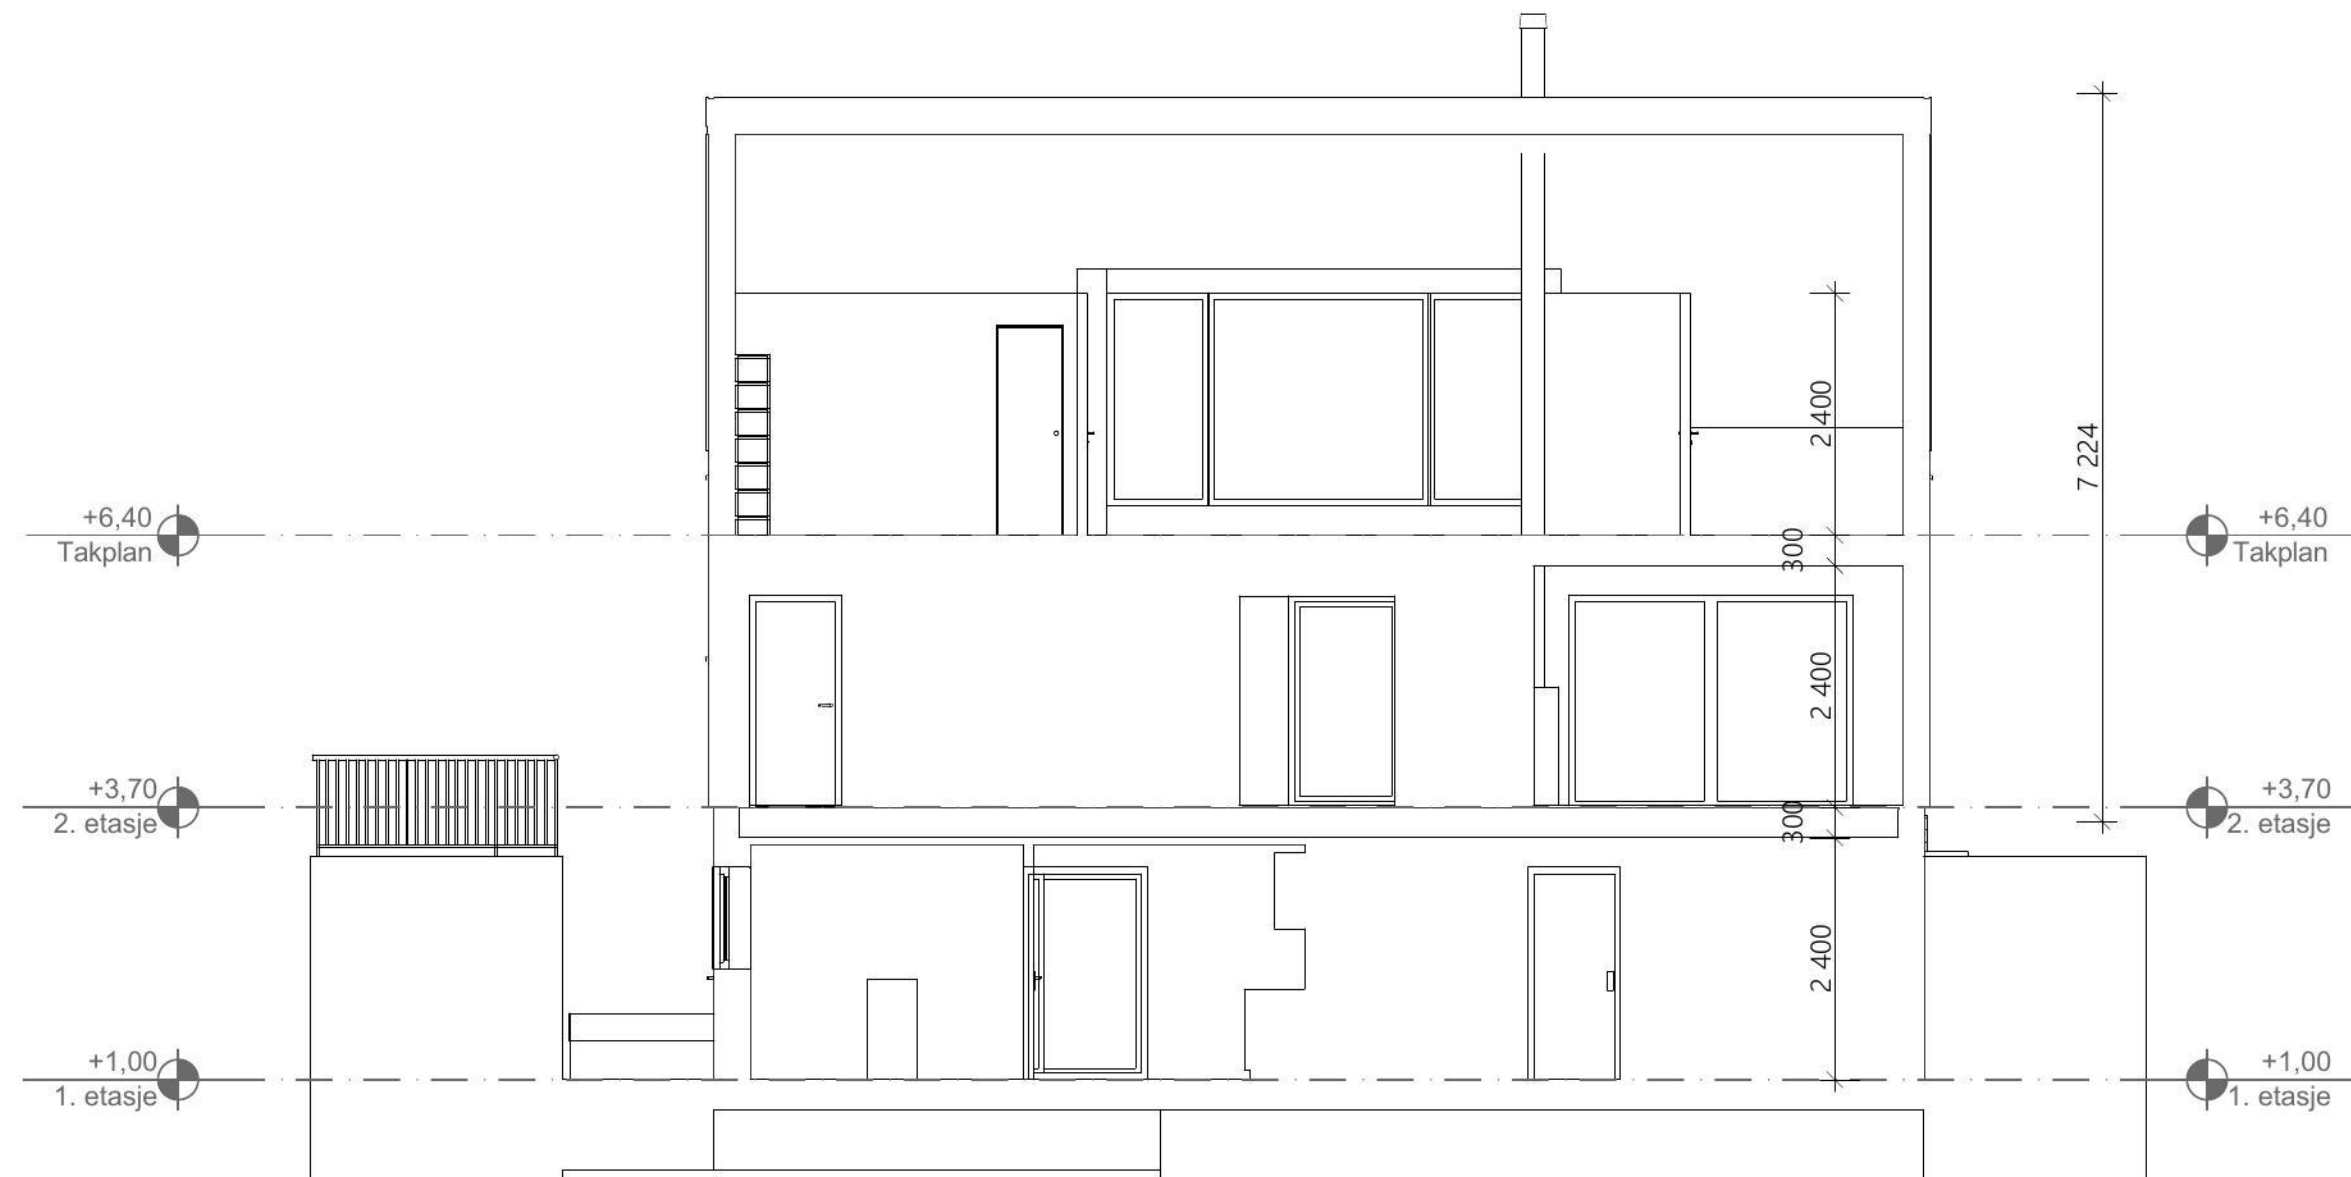

1:100 Snitt B

Tegningsnr. A30-1		Revisjon nr.																																	
Type tegning Snitt A og B																																			
<table><tr><td>REV</td><td>23.12.2022</td><td></td><td></td></tr><tr><td>REV</td><td>26.05.2023</td><td></td><td></td></tr><tr><td></td><td></td><td></td><td></td></tr><tr><td></td><td></td><td></td><td></td></tr><tr><td></td><td></td><td></td><td></td></tr><tr><td></td><td></td><td></td><td></td></tr><tr><td></td><td></td><td></td><td></td></tr><tr><td></td><td></td><td></td><td></td></tr></table>				REV	23.12.2022			REV	26.05.2023																										
REV	23.12.2022																																		
REV	26.05.2023																																		
Rev		Nr	Beskrivelse	Dato	Sign	Kontr																													
Lokalisering:																																			
Prosjekteringsgruppen																																			
● ARK :		Skjærgårdsbygg a/s		Østerøya 240 4625 Flekkerøy Tlf.: 90522750 steinar@skjaergardsbygg.no																															
● RIB :		Rådg. ing. Bygg		RIBveien18 0000 RIBbyen Tlf: 000 00 000 rib@ribfirma.no																															
● RIE :		Rådg. ing. Elektro		RIEveien18 0000 RIEbyen Tlf: 000 00 000 rie@riefirma.no																															
● RIV :		Rådg. ing. VVS		RIVveien18 0000 RIVbyen Tlf: 000 00 000 riv@rivfirma.no																															
Tiltakshaver				Godkjent																															
Skjærgårdsbygg a/s				Kontroll prosjekt.																															
				Sign.	Kontroll																														
Prosjekt				Filnavn																															
Paulen 77				Paulen 77.pln																															
Skålevig				Dato																															
4625 Flekkerøy				14.09.2022																															
				Målestokk																															
				1:100																															
				Kontroll utførende																															
Gnr./Bnr./Festenr.:				Sign.			Kontroll																												
Gnr2/Bnr628																																			
Prosjektnr.:		Tegningsnr.:		Prosjektnr. for prosjekterende/lev.																															
Prosjektnr.		A30-1																																	
Type tegning:																																			
Snitt A og B																																			