
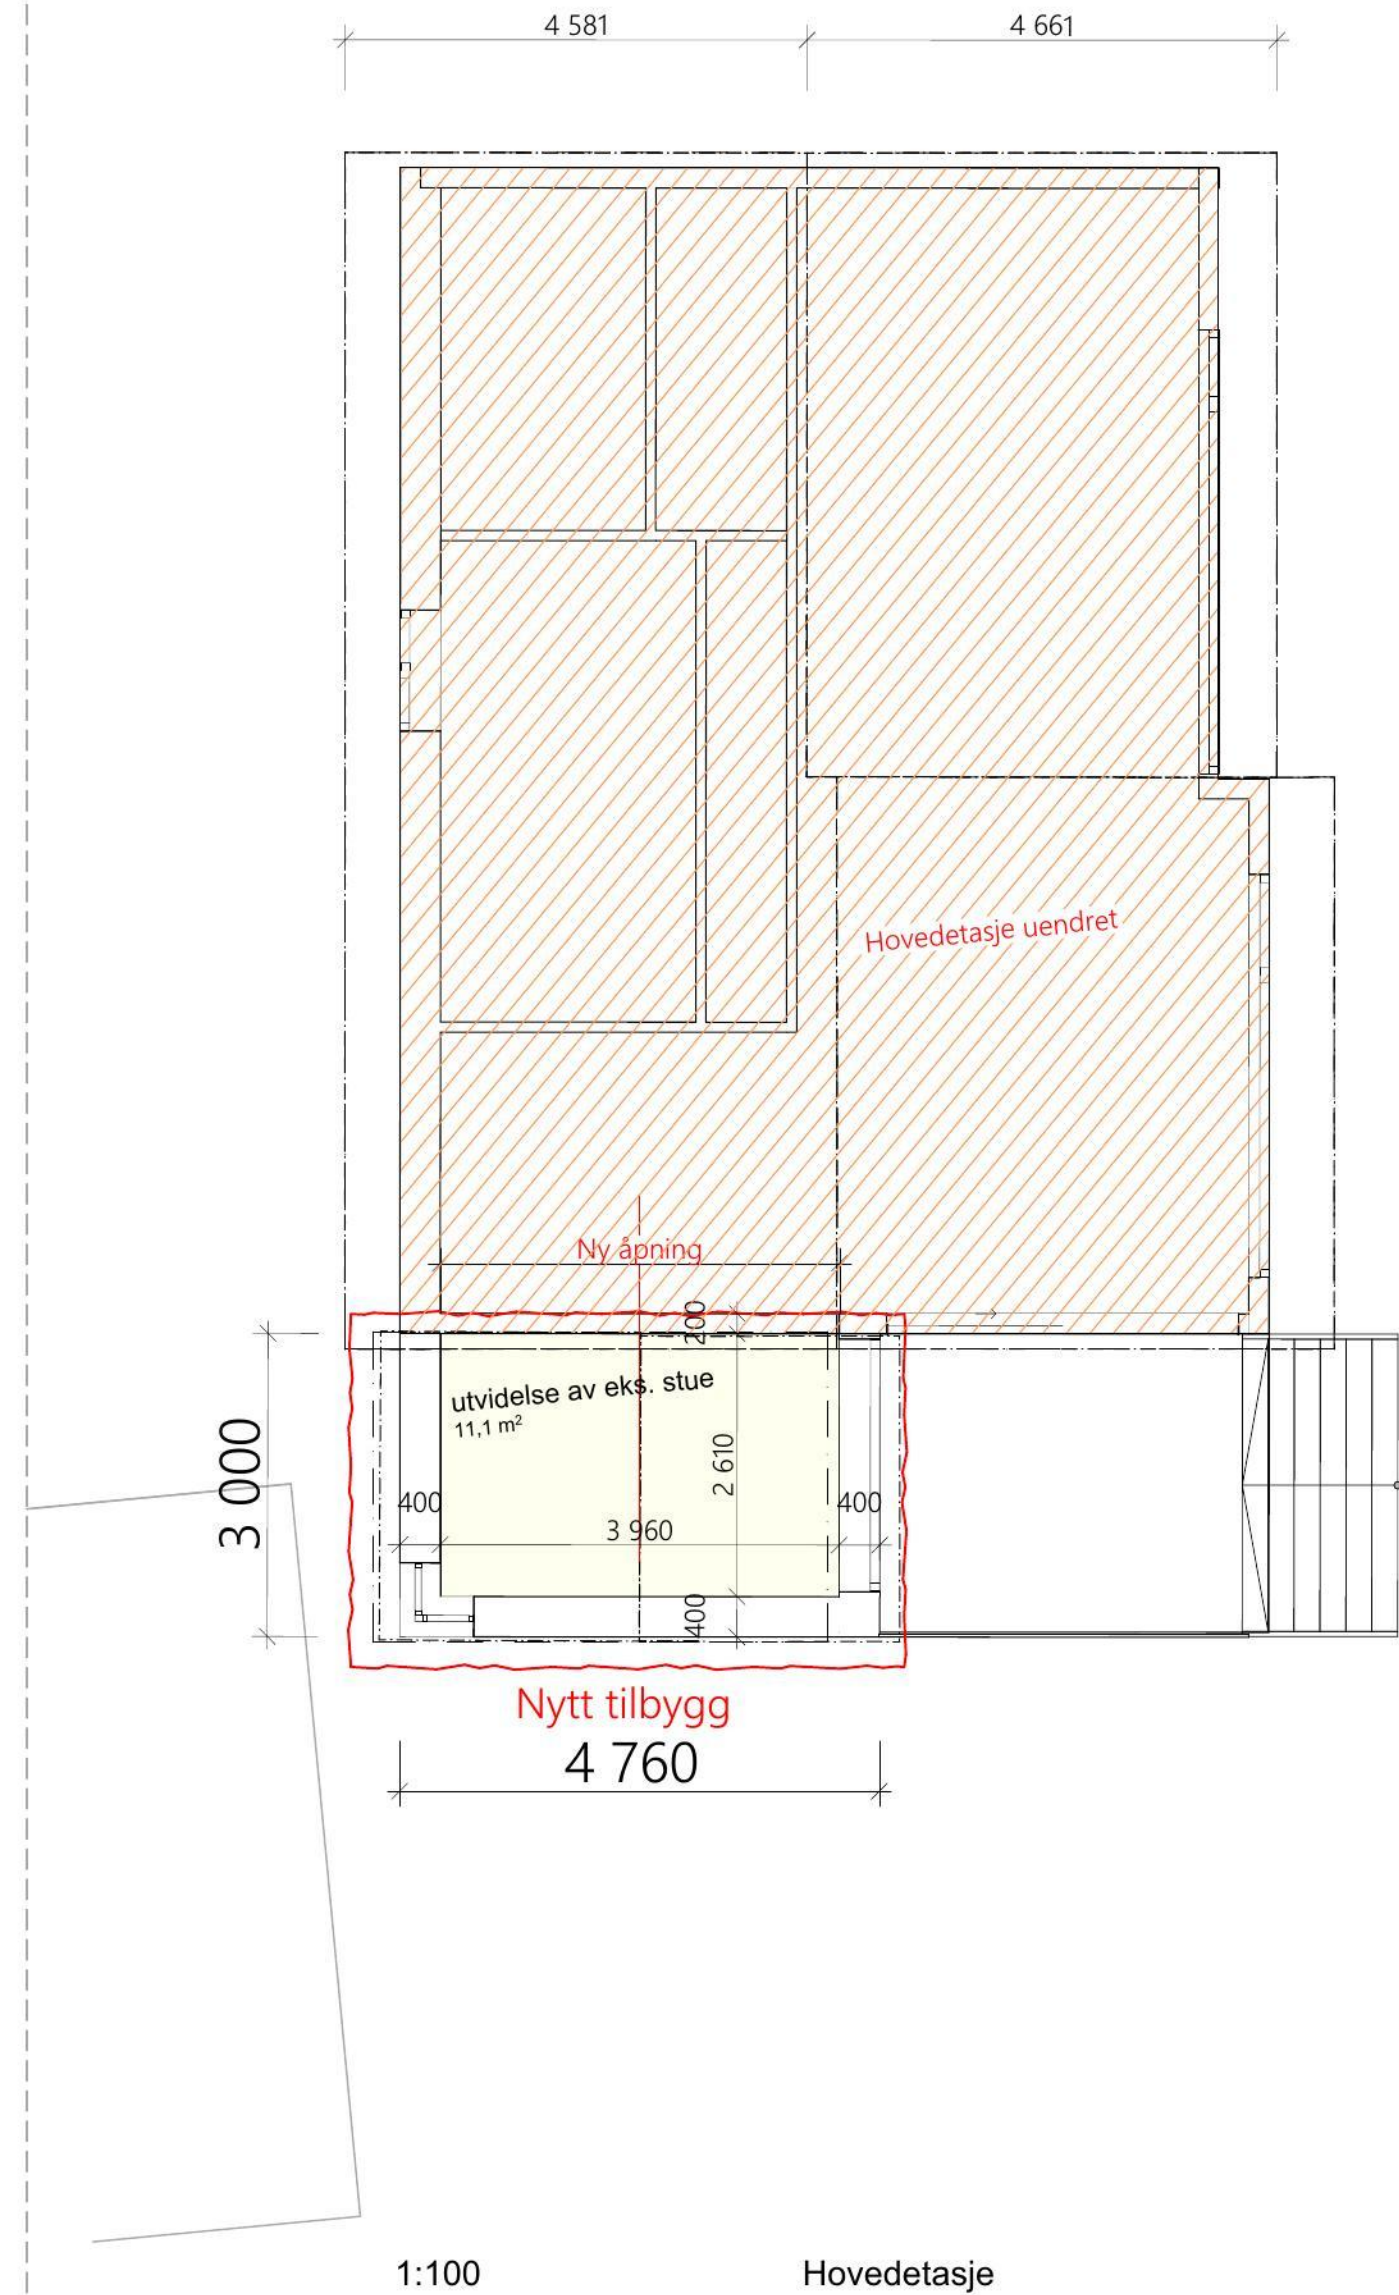


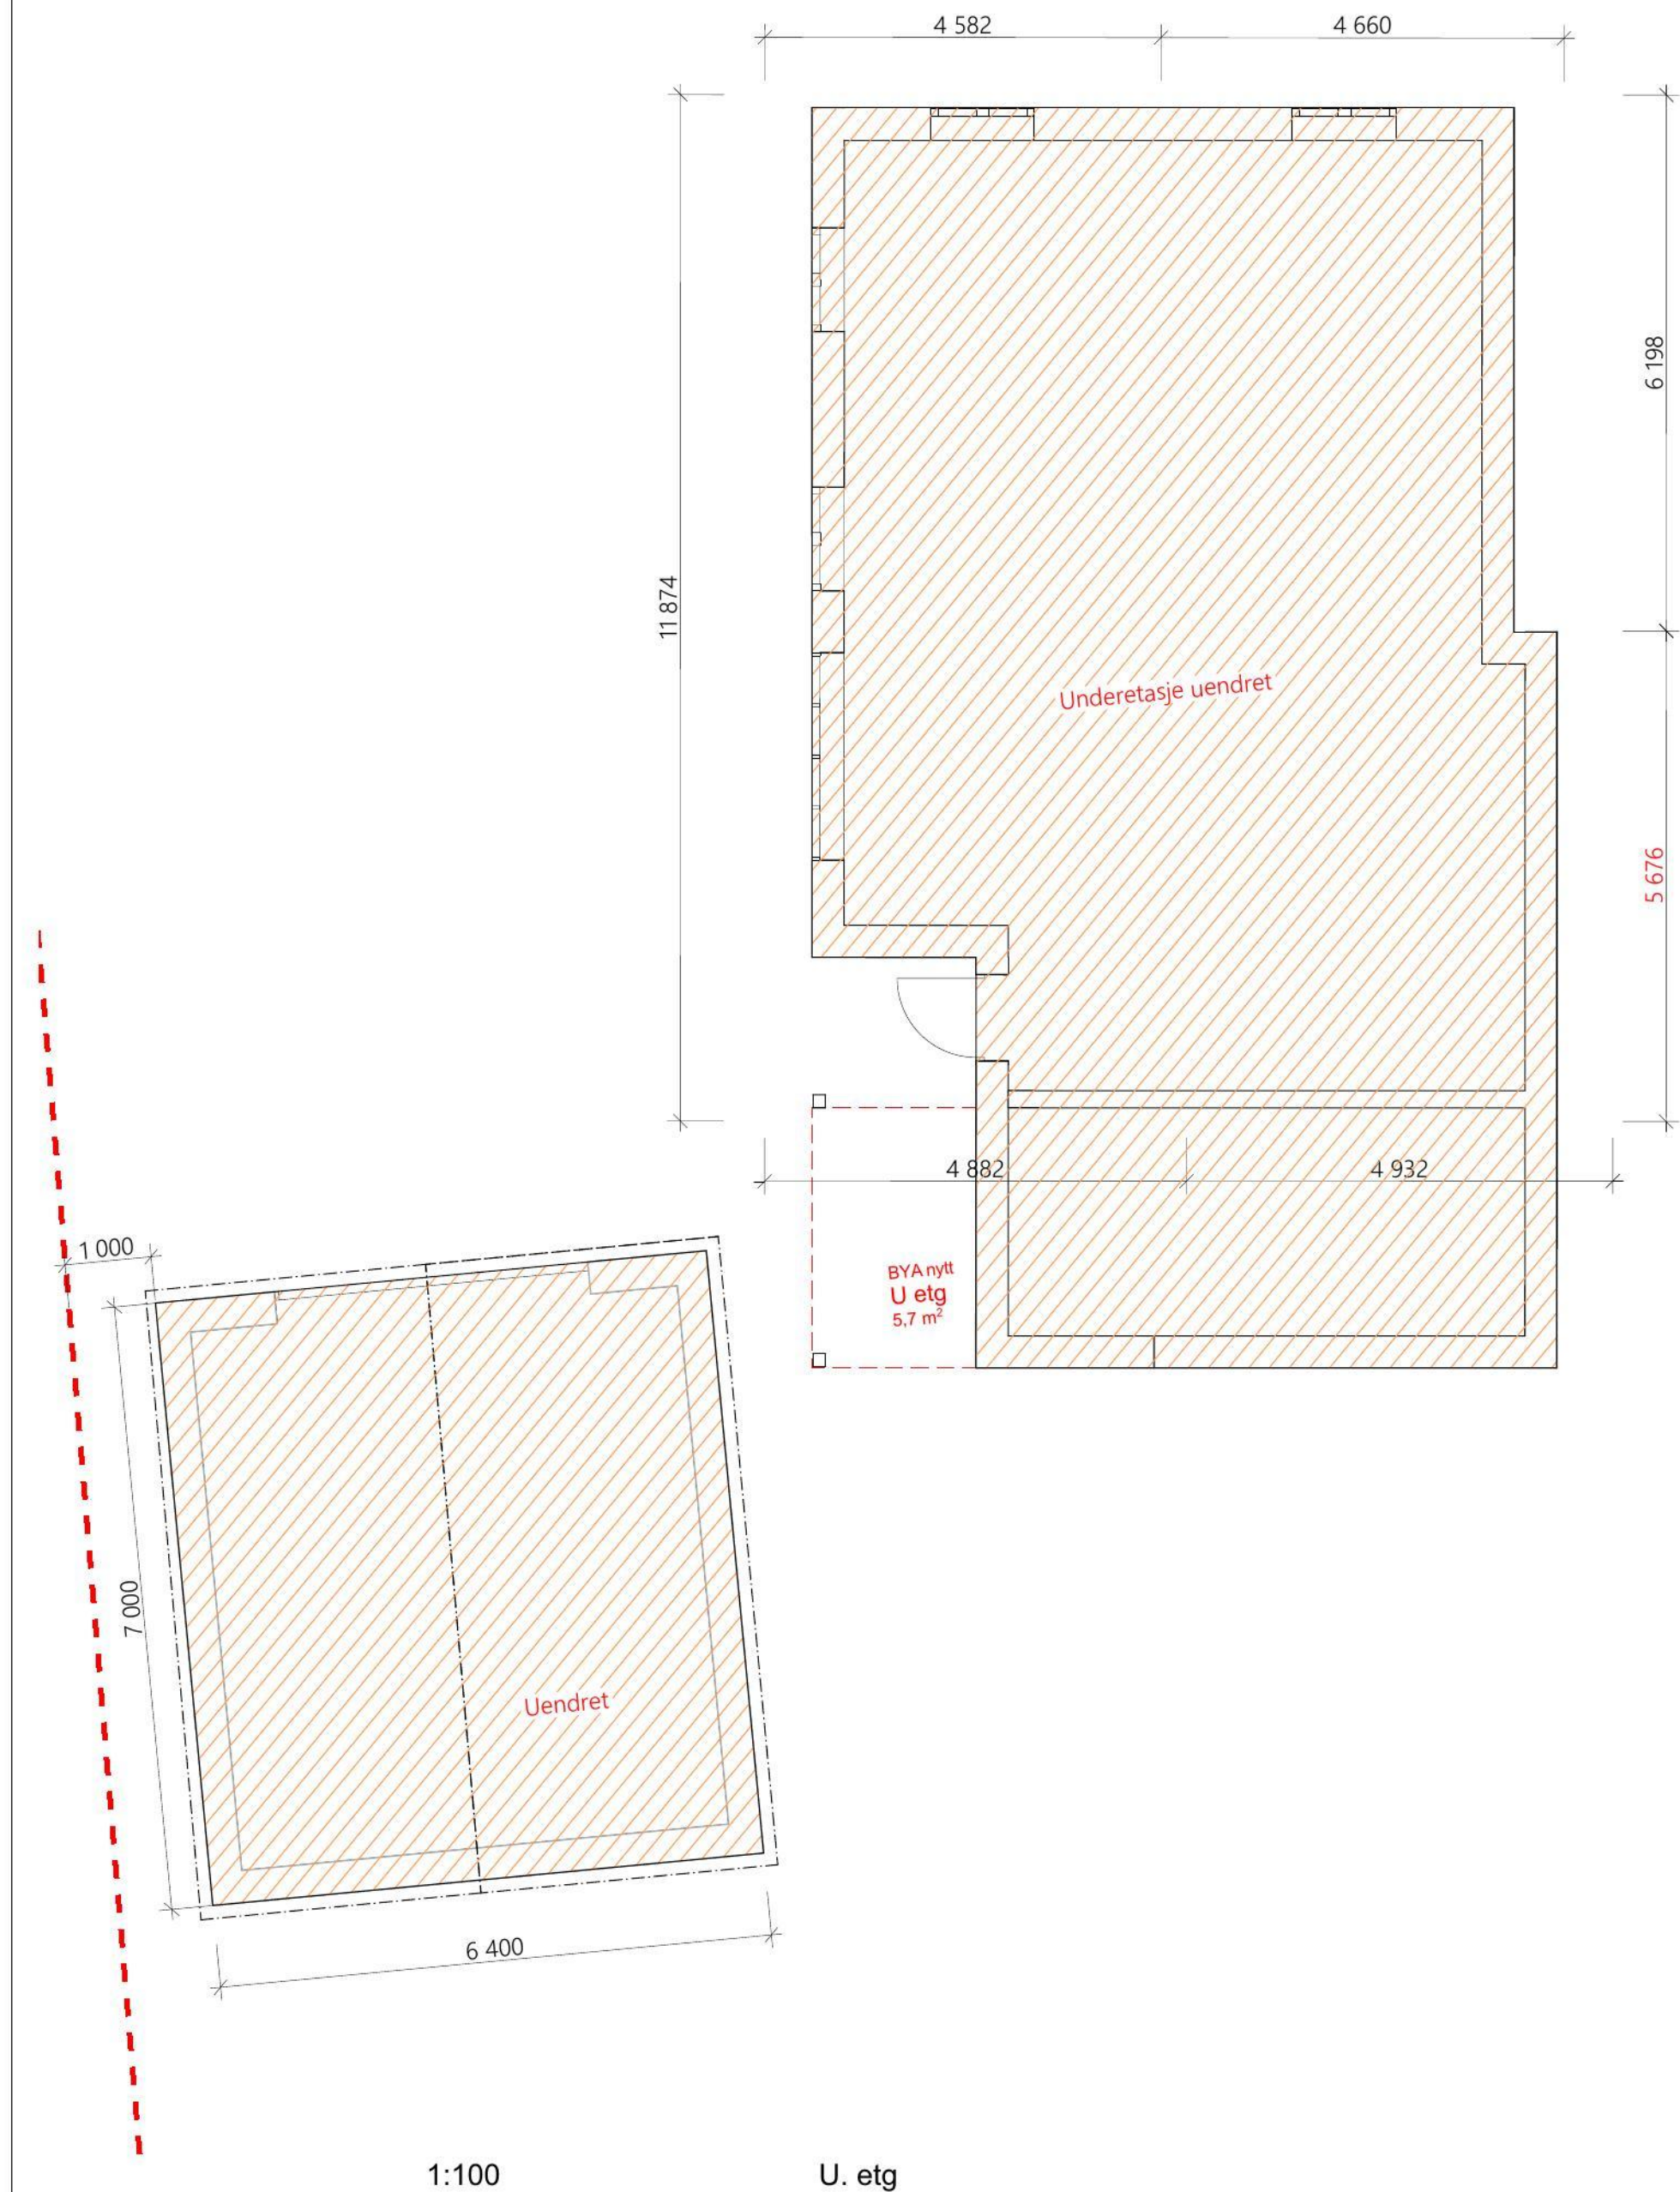

 SPISS ARKITEKTUR & PLAN AS			Prosjekt:		Rammesøknad			
SPISS Arkitektur & Plan AS Vestre Strandgate 26 Telefon: 41778000			Postboks 151 Mail: post@spissark.no		4662 Kristiansand			
Tegnet	Arkitekt	Ark	Oppdragsgiver:					
MAG	MAG/ SEB	A3	Ina Eriksen Sæbø og Anders Høibakk					
ProsjektNr..	Dato	Målestokk	Tegningsnr.: Rev.					
2339	29.08.2023	1:100	A20-1					
			Tegnings Tittel:					
			Plan Uetg og Hovedetasje					