



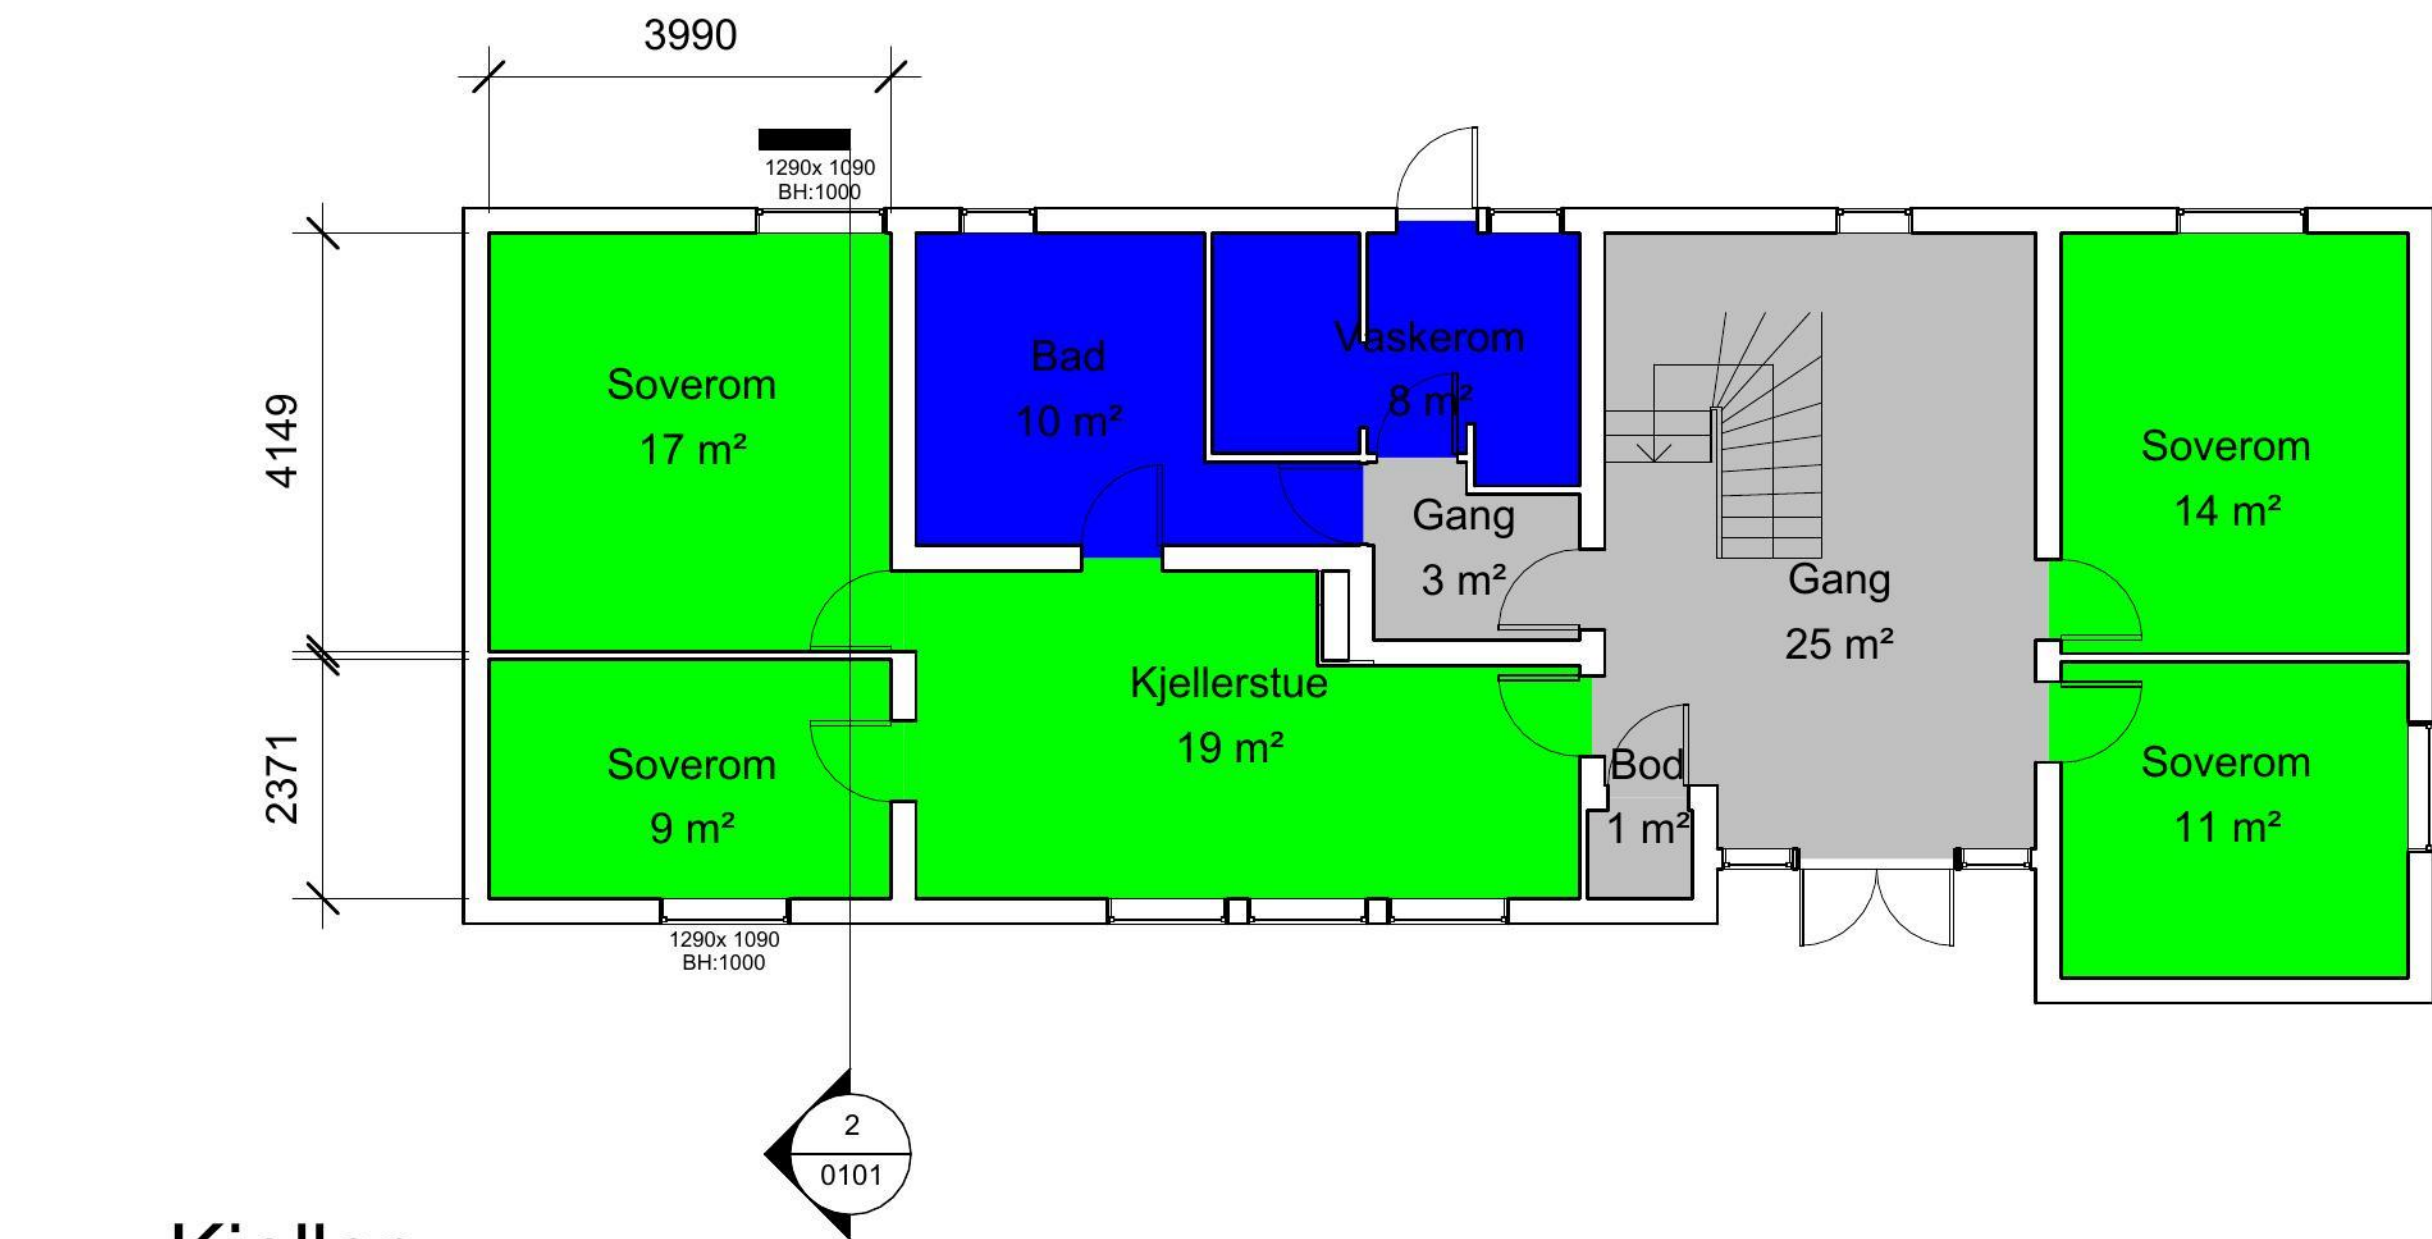

1 Kjeller
1 : 100

Romskjema			
Etasje	Rom	Areal	Kommentar
Kjeller	Soverom	17 m²	Bruksendres fra tilleggsdel til hoveddel
Kjeller	Soverom	9 m²	Bruksendres fra tilleggsdel til hoveddel
Kjeller	Kjellerstue	19 m²	Uendret
Kjeller	Bad	10 m²	Uendret
Kjeller	Vaskerom	8 m²	Uendret
Kjeller	Gang	3 m²	Uendret
Kjeller	Bod	1 m²	Uendret
Kjeller	Soverom	11 m²	Uendret
Kjeller	Soverom	14 m²	Uendret
Kjeller	Gang	25 m²	Uendret

BRA som bruksendres: 26 m²

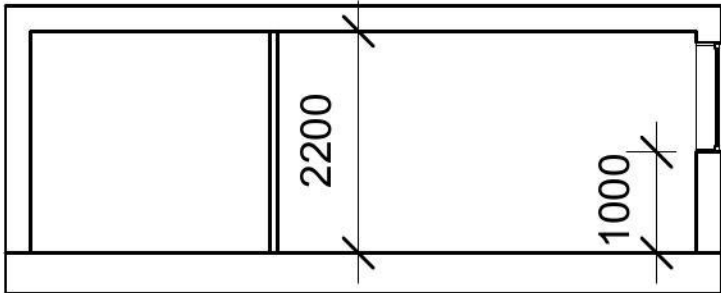

2 Snitt A
1 : 100