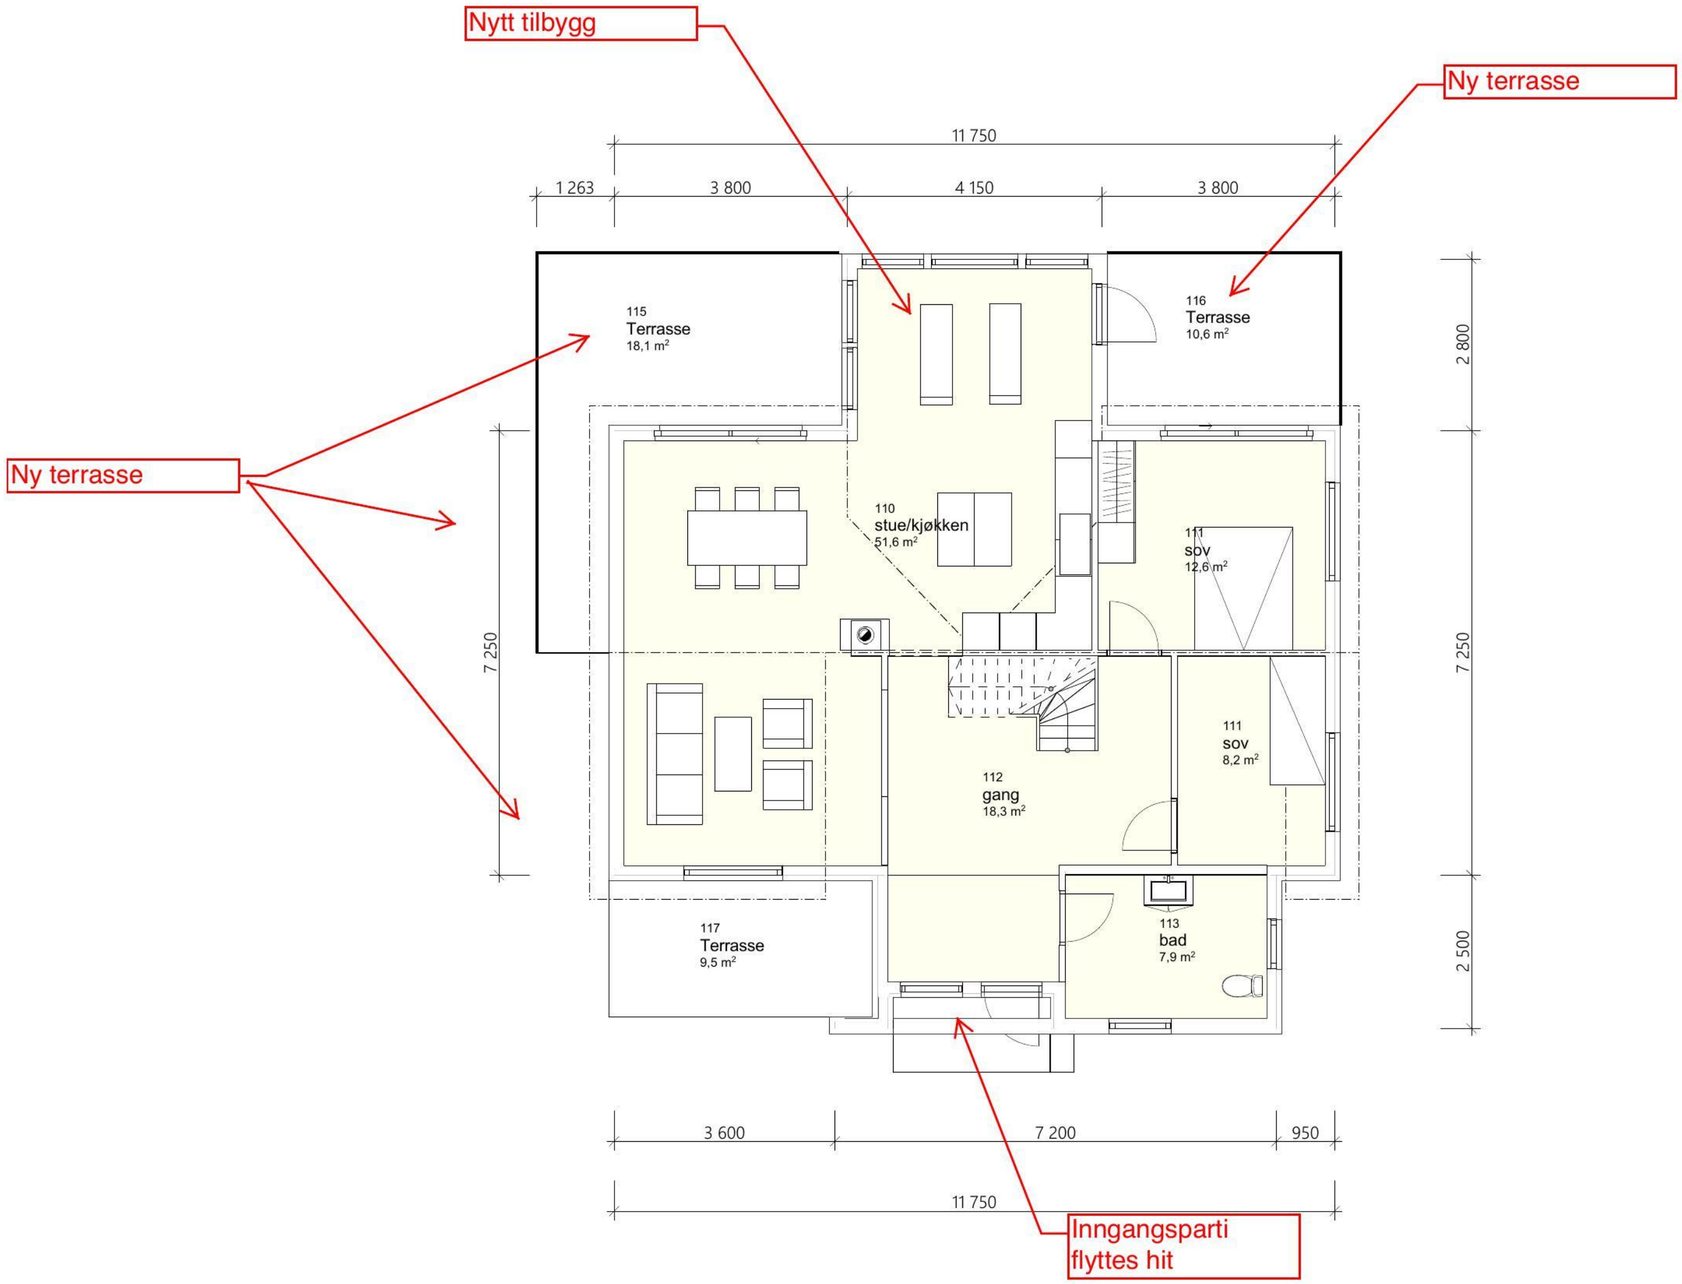



Tegningsnr.
A20-3


Revisjon nr.

Type tegning
Plan 1.etg.

Rev	Nr	Beskrivelse	Dato	Sign	Kontr
		Revidert	07.07.2022		
		Revidert	02.01.2023		
		Revidert vindusliste	09.01.2023		

Lokalisering:

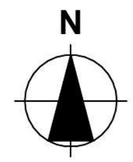

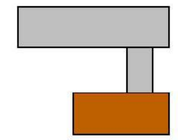

Prosjekteringsgruppen

ARK : Skjærgårdsbygg a/s
Østerøya 240
4625 Flekkerøy
Tlf.: 90522750
steinar@skjaergardsbygg.no

RIB : Rådg. ing. Bygg
RIBveien18
0000 RIBbyen
Tlf: 000 00 000
rib@ribfirma.no

RIE : Rådg. ing. Elektro
RIEveien18
0000 RIEbyen
Tlf: 000 00 000
rie@riefirma.no

RIV : Rådg. ing. VVS
RIVveien18
0000 RIVbyen
Tlf: 000 00 000
riv@rivfirma.no

Fase
Fase

SKJÆRGÅRDSBYGG
Tlf.38 10 01 78
Mob. 915 94 500

Tiltakshaver
Mia og Sivert

Prosjekt
Enebolig
Kårholmsveien 77
4625 Flekkerøy

Godkjent

Kontroll prosjekt.
Sign. | Kontroll

Filnavn
Sivert og Mia.pln.lck.pln

Dato
20.04.2022

Målestokk
1:100

Kontroll utførende
Sign. | Kontroll

Gnr./Bnr./Festenr.:
Gnr/Bnr/Festenr

Prosjektnr.:
Prosjektnr.

Tegningsnr.:
A20-3

Prosjektnr. for prosjekterende/lev.

Type tegning:
Plan 1.etg.