

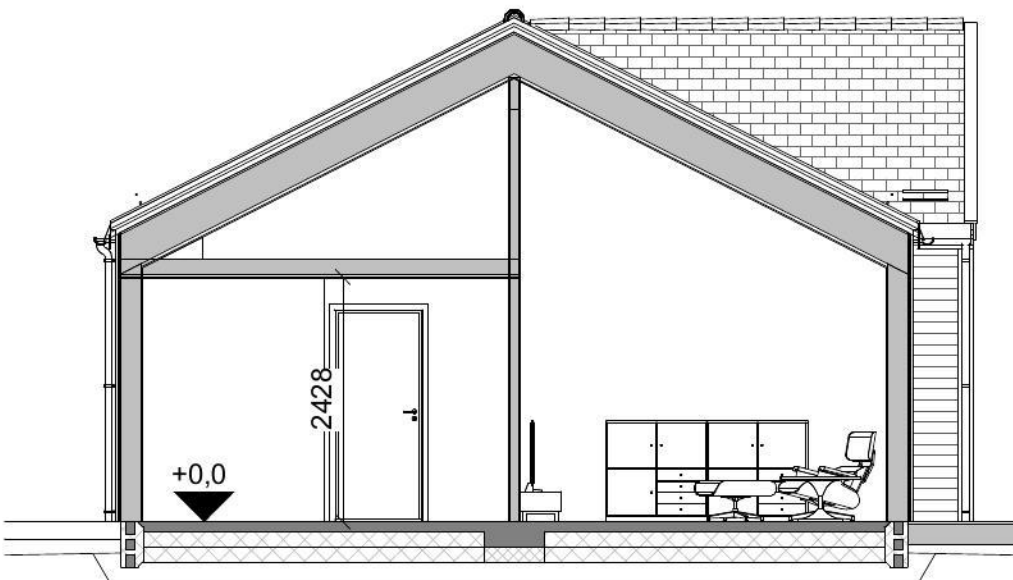


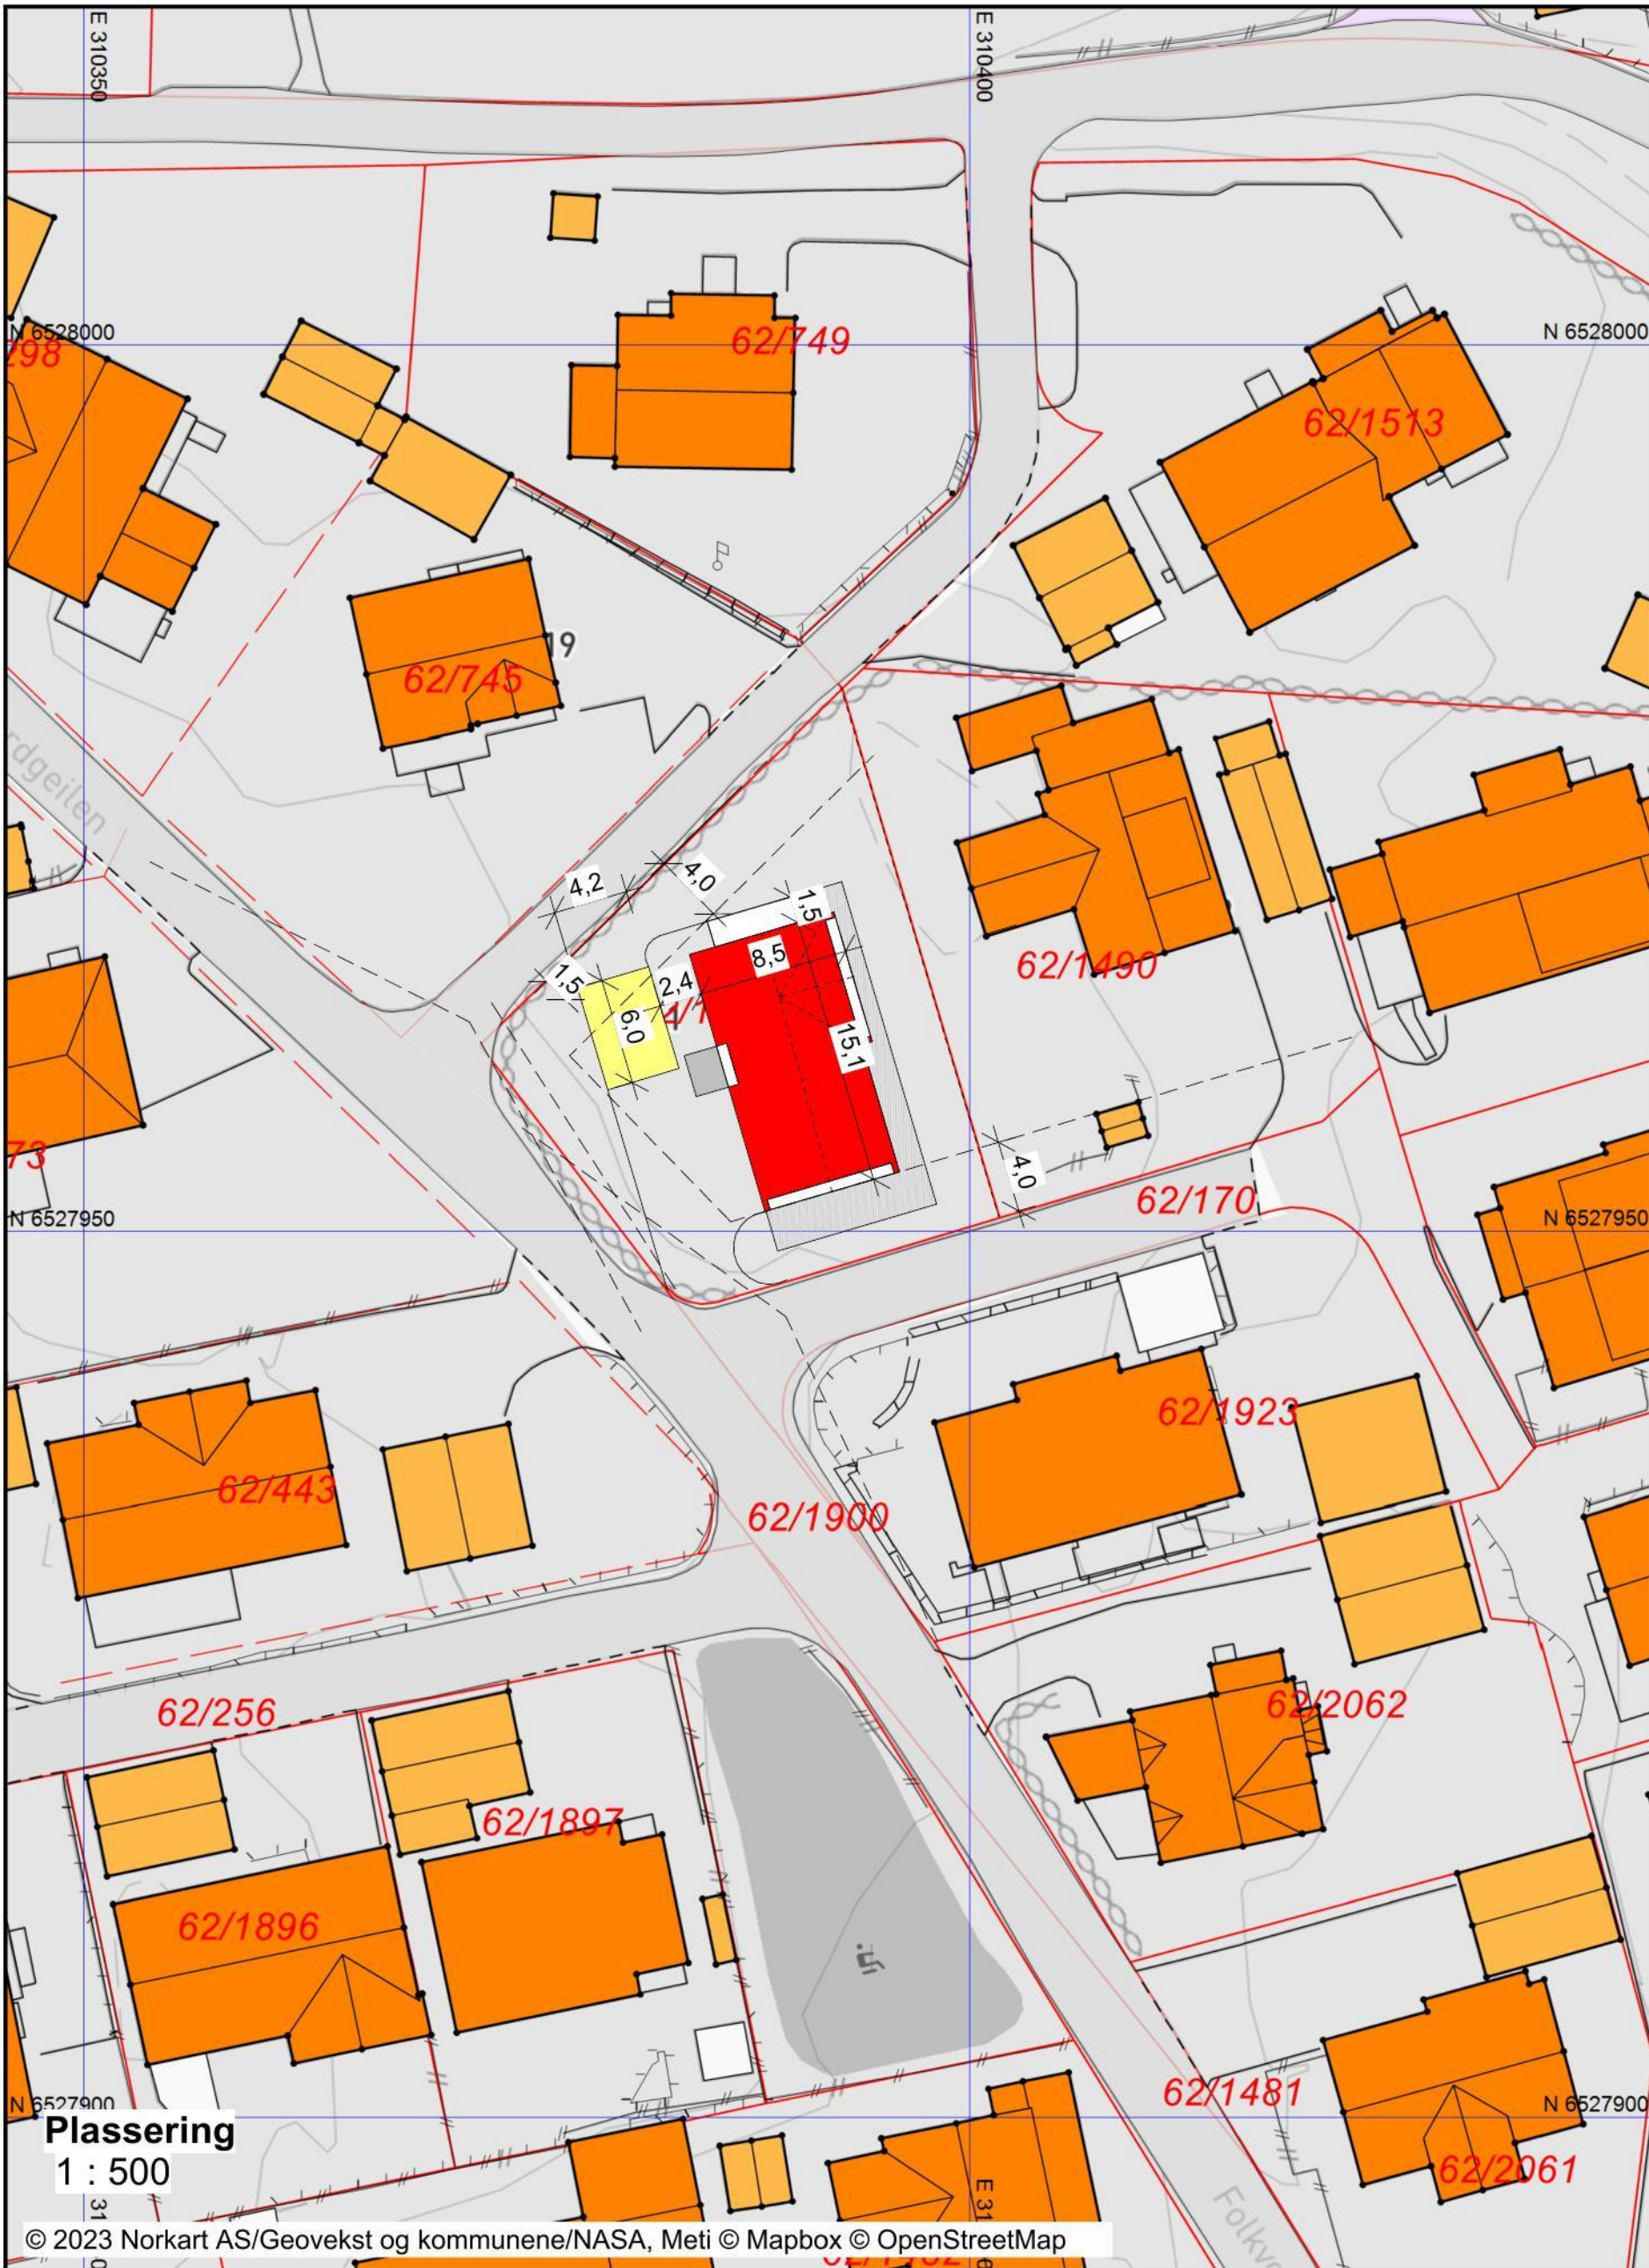

A
1 : 100

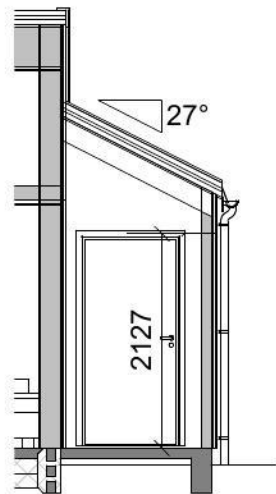

B
1 : 100

Bebyggelse areal (BYA)	
BYA Bebyggelse areal	131,4 m²
Bruksareal (BRA)	
BRA 1.etg	101,4 m²
BRA utv.bod	6,2 m²
AOA	9,6 m²
	117,2 m²
Primær/sekundær del	
P-rom	101,4 m²
S-rom	6,2 m²
	107,6 m²

Glassfelt og glassdør i kommunikasjonsvei
har personsikkerhetsrute

Bjørn Pettersen
Enebolig m/mønt stue/kjøkken
Folkvordgeilen 11

62/1491
Sandnes kommune

Målestokk	Dato	23.08.23
As indicated	Tegnet	ib
	Kontr.	kw
Prosjekt status	Rev.	C
Salgstegning		
Tegning nr.	Prosjekt nr.	Original
A-04		Lime1
Tittel		
Snitt og plassering		



Hellvik Hus Teknologi og Produksjon AS
Jærveien 1250, 4375 Hellvik
51 46 16 00
post@hellvikhus.no
www.hellvikhus.no

C	Mønt himling	ib	kw	23.11.23
B	Rev.iht.skisse	ib	kw	06.11.23
A	Div.rev.	ib	kw	10.10.23
Rev.	Revisjonen gjelder	Utført	Kontr.	Dato