


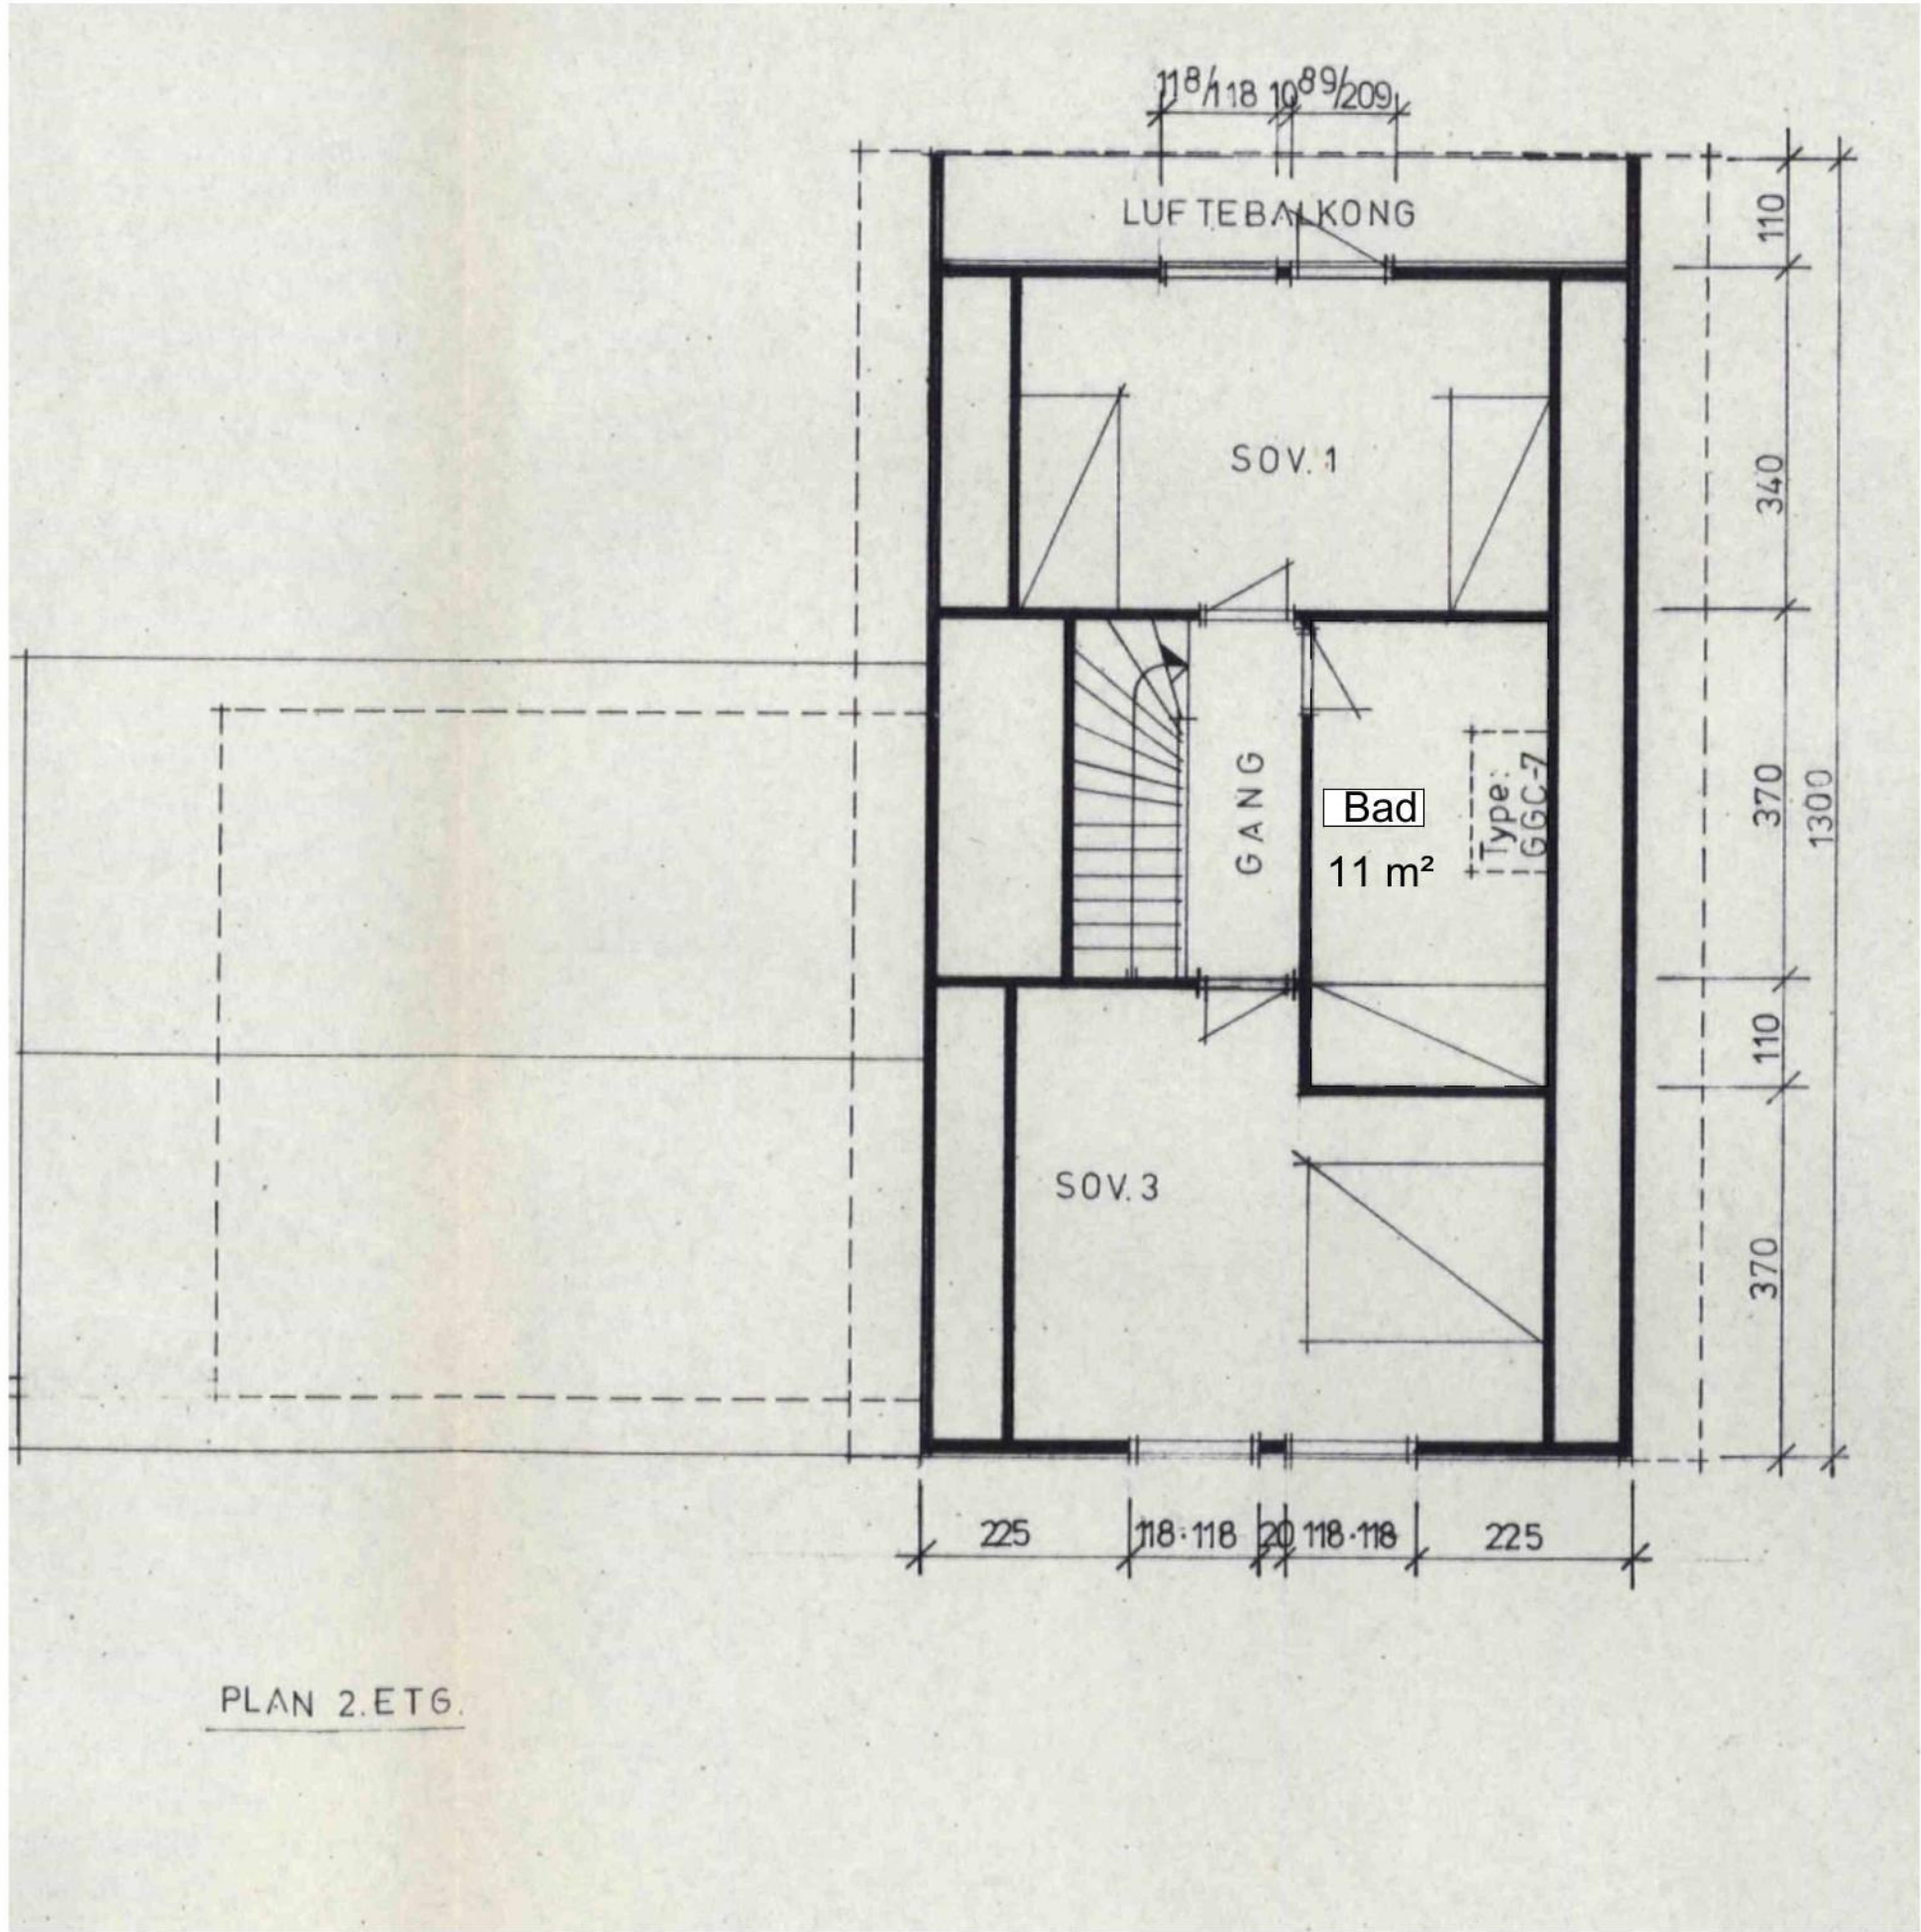


1 2. etasje As-built tegning
1 : 100

Det har blitt etablert bad hvor sov. 2 har vært. Etablering av bad i eksisterende bygg er ikke søknadspliktig forutsatt man ikke endrer på brannskillende konstruksjoner eller bærende konstruksjoner. I dette tilfellet er ikke hverken bærende konstruksjon eller brannskillende konstruksjon blitt endret.

Bad er definert som hoveddel, men ettersom opprinnelig godkjenning er soverom, medfører dette ikke endring fra tilleggsdel til hoveddel.

Endring/økning av vindu anses ikke som søknadspliktig tiltak jf. Pbl § 20-5 bokstav b.

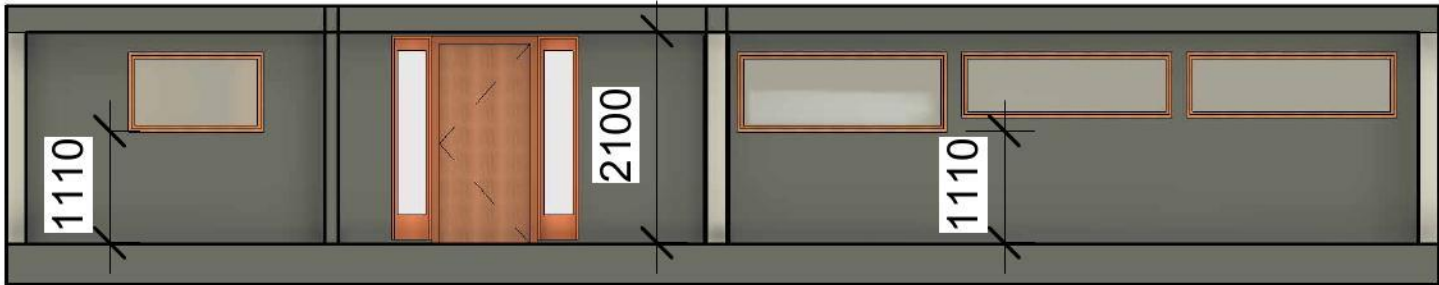

2 Snitt
1 : 100

© Alle rettigheter tilhører Mentor Prosjektering AS, kopiering eller bruk av disse tegningene er forbudt uten skriftlig samtykke