



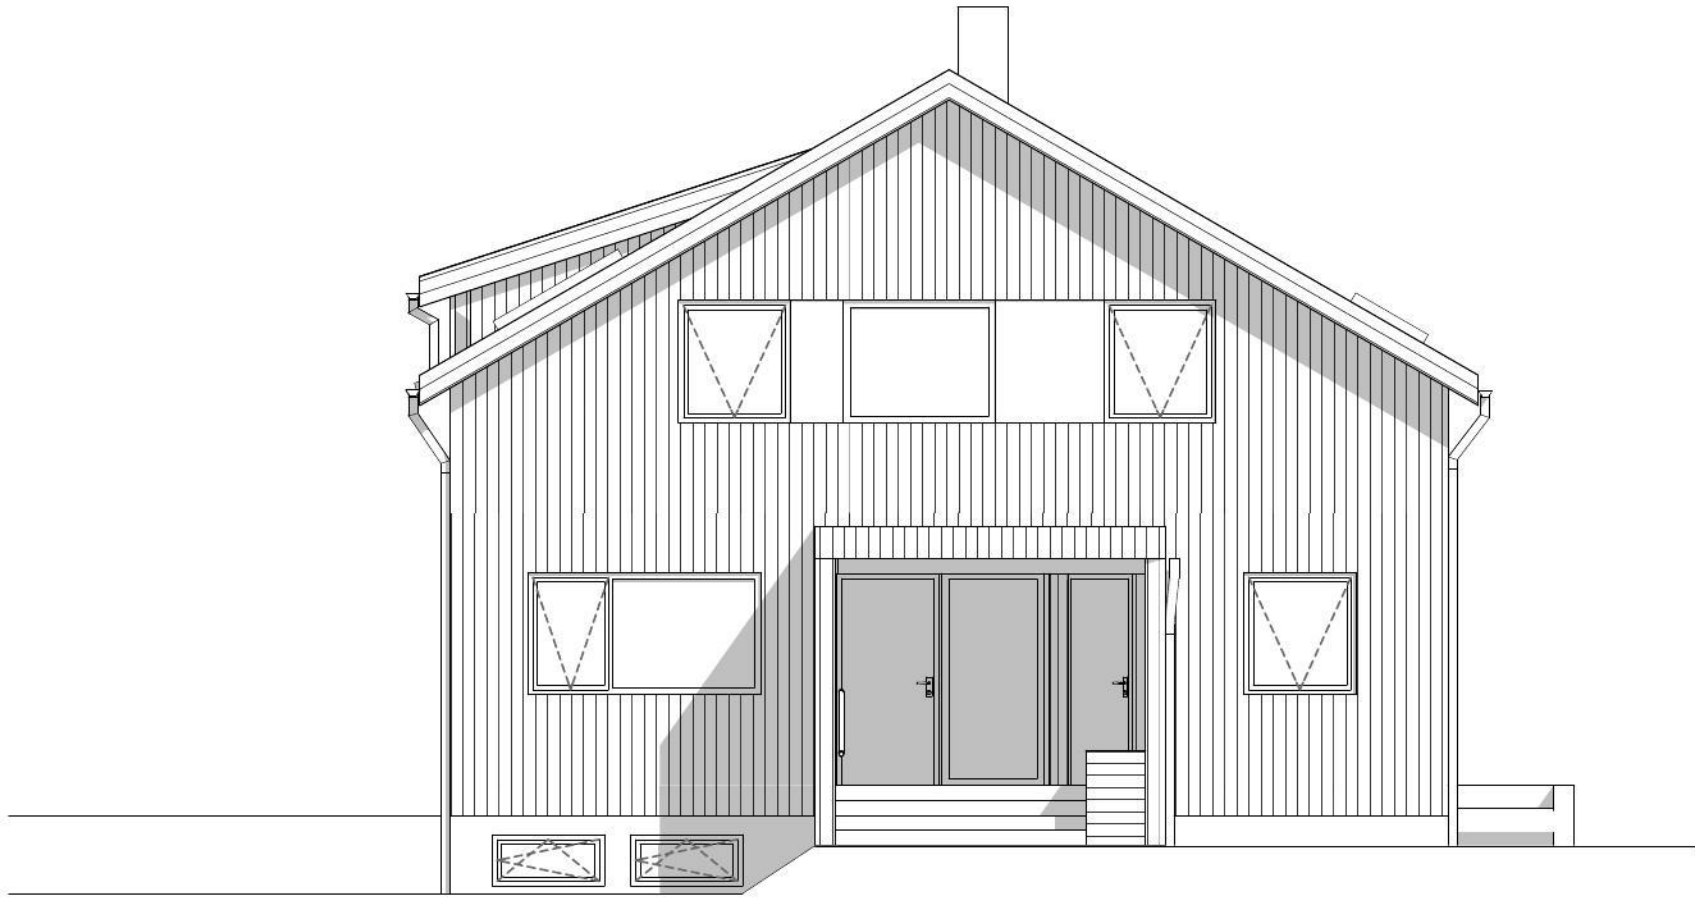

PLANLAGT FASADE ØST

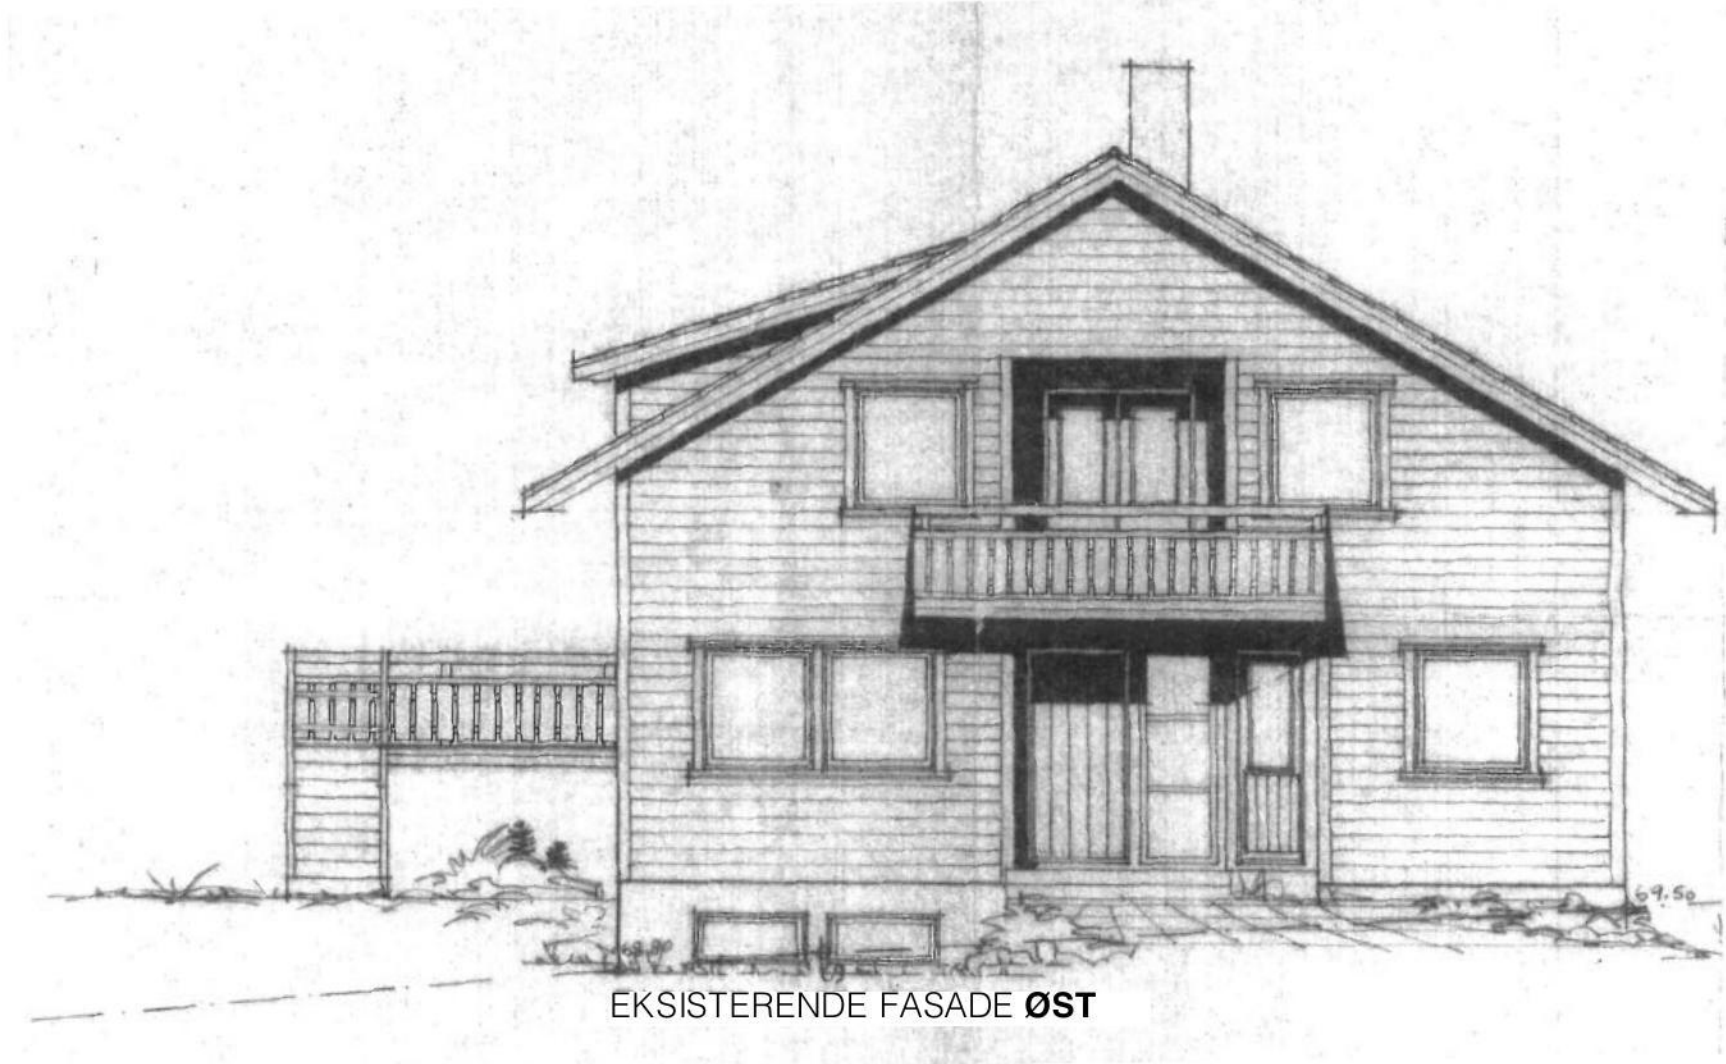

EKSISTERENDE FASADE ØST

A	08.01.2023	AES	BAS	BAS	Mindre justeringer av vindustørrelser og plassering
REV.	DATO	TEGN	KONTR	GODKJ	ENDRING
Kommunenr-, gårds- og bruksnr.: 38/1686		AROS	ARKITEKTER AS Havnegata 15 4306 Sandnes		Kine Bøe og Lars Olav Rønnevik Ombygging enebolig Gamle Austråttvei 16, 4326 Sandnes, Norge Fasade øst
Kartdatum: Euref89, UTM sone 32, NN2000	tlf: 476 84 000 web: www.aros.no org.nr: 999 655 114				
Prosjektfase: Rammesøknad					
TEGN	KONTR	GODKJ	MÅLESTOKK		DATO
LBI	BAS	BAS	1:100 (A3)		01.12.23
OPPDRAGSNR.:3944					REV.
TEGNING NR. A40-01					A