

Filplassering: \Volumes\Prosjekt2\3944 Ombygging Gamle Austråttvei 16 - Bygg BAS.pln

A	08.01.2023	AES	BAS	BAS	Mindre justeringer av vindustørrelser og plassering
REV.	DATO	TEGN.	KONTR.	GODKJ.	ENDRING
KOMMUNE-, GARDS- OG BRUKSNR. 38/1686				KARTDATUM Euref89, UTM sone 32, NN2000	PROSJEKTFASE Rammesøknad

AROS


ARKITEKTER AS
Havnegata 15
4306 Sandnes

tlf: 476 84 000
web: www.aros.no
org.nr: 999 655 114

Kine Bøe og Lars Olav Rønnevik
Ombygging enebolig
Gamle Austråttvei 16, 4326 Sandnes, Norge

Plan 1. etasje

TEGN.	KONTR.	GODKJ.	MALESTOKK	DATO	REV. A
LBI	BAS	BAS	1:100 (A3)	01.12.23	
OPPDRAGS NR. 3944					
TEGNINGS NR. A20-01					

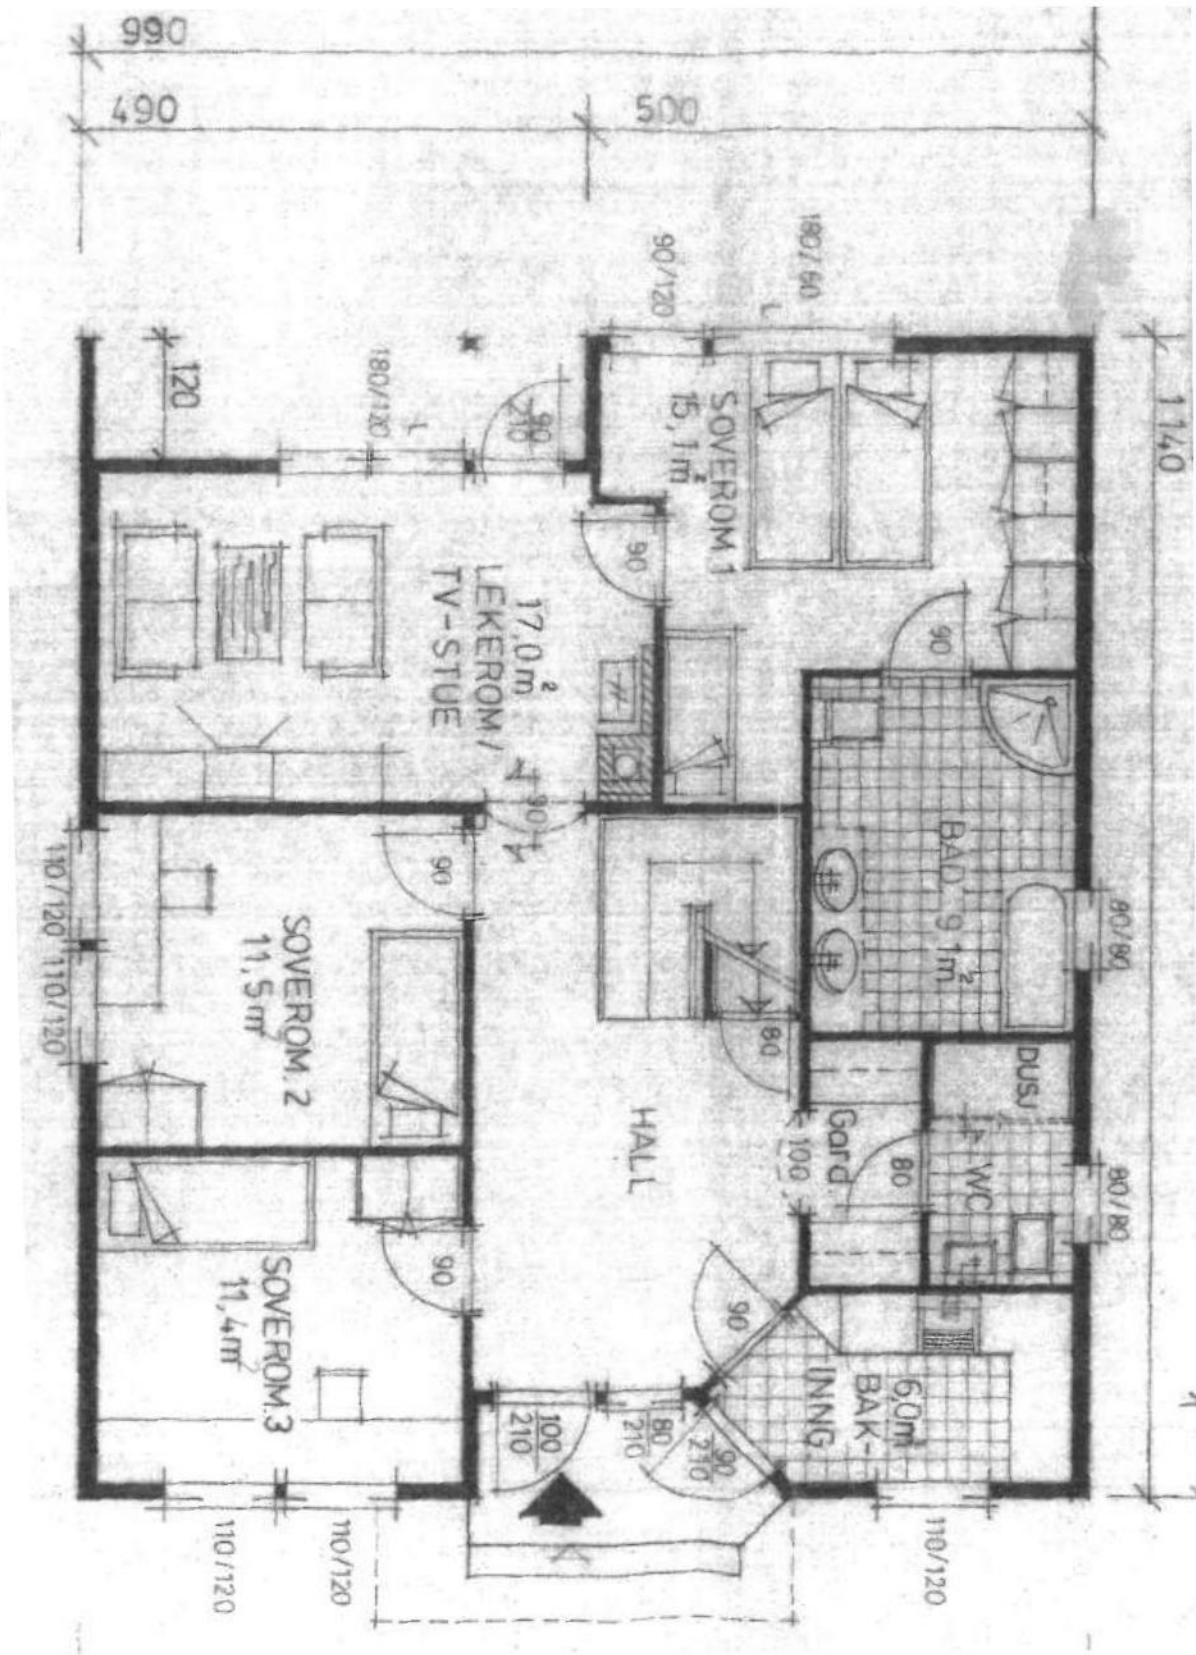

Eksisterende 1. etg

Fasade sør

Planlagt 1. etg

