


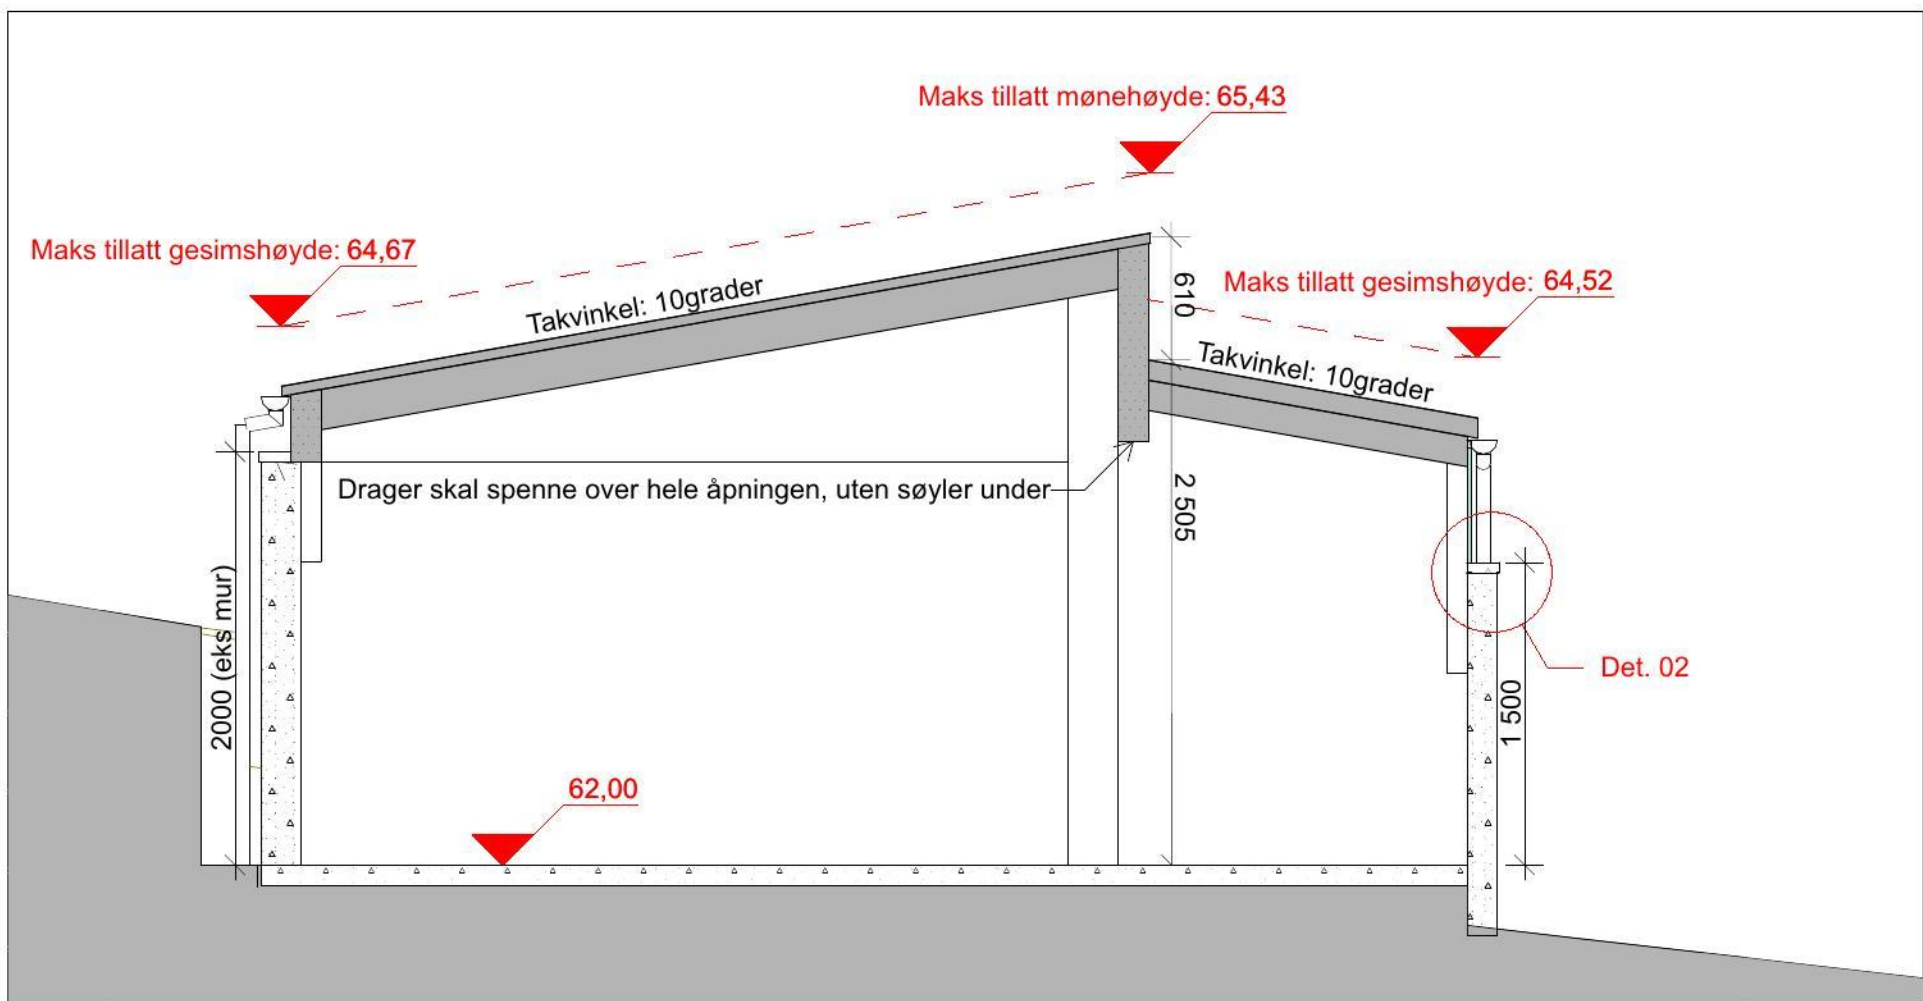


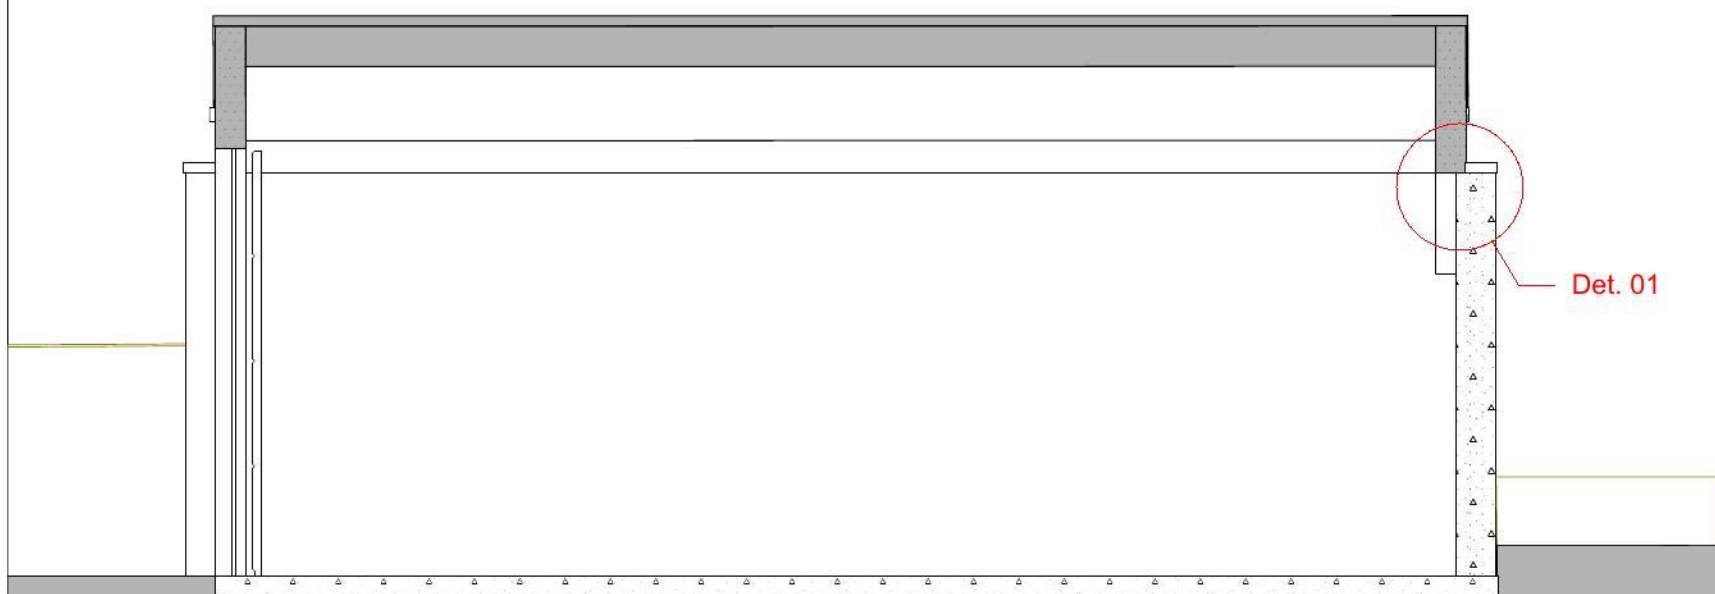

A-A

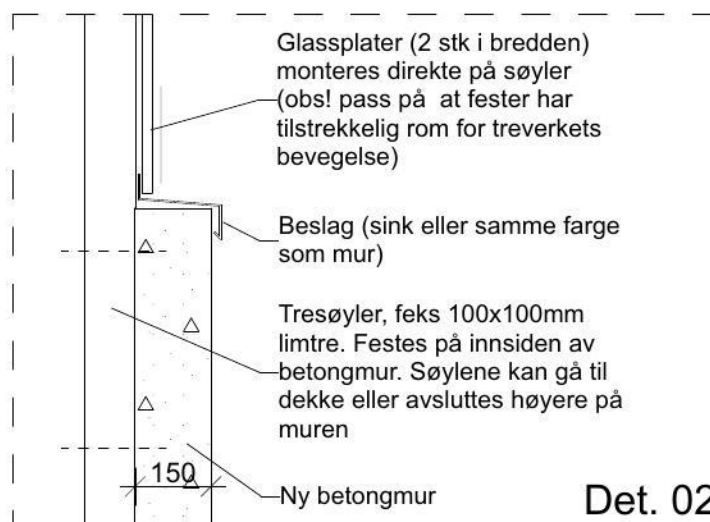

B-B

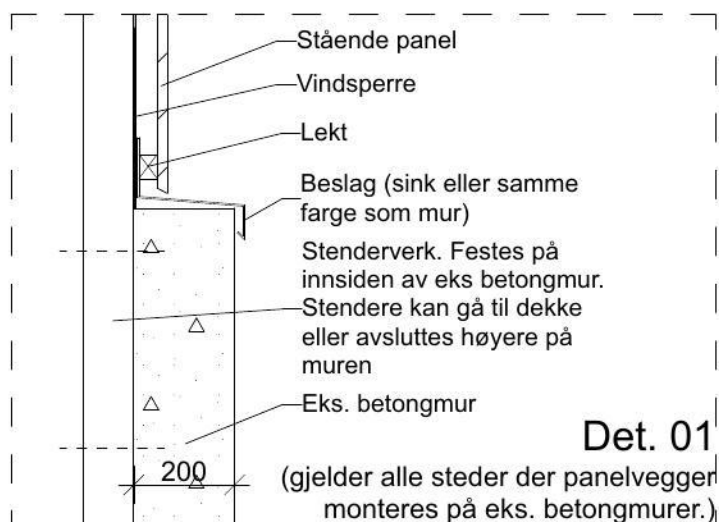

Detaljer gavler, møne og gesimsavslutninger, inkl innfesting takrenner, skal løses likt som på bolighuset (uten takutspring).

Garasje Gamle Austråttvei 21, Gnr. 39/398
Endring av rammesøknad

Prosjektnr.: 4285.2
Type tegning: Snitt og detaljer garasje

BRANDSBERG-DAHLS
ARKITEKTER
Engelsminnegata 16a, 4008 Stavanger
Tlf. 000 000 00

Kontroll prosjekt		Målestokk:	(A4)	Tegningsnr.:
Sign.:	Kontroll:	1:50, 1:20		A 30
AEO				
Dato:				
11.01.2024				
Gnr. 39				
Bnr. 398				