



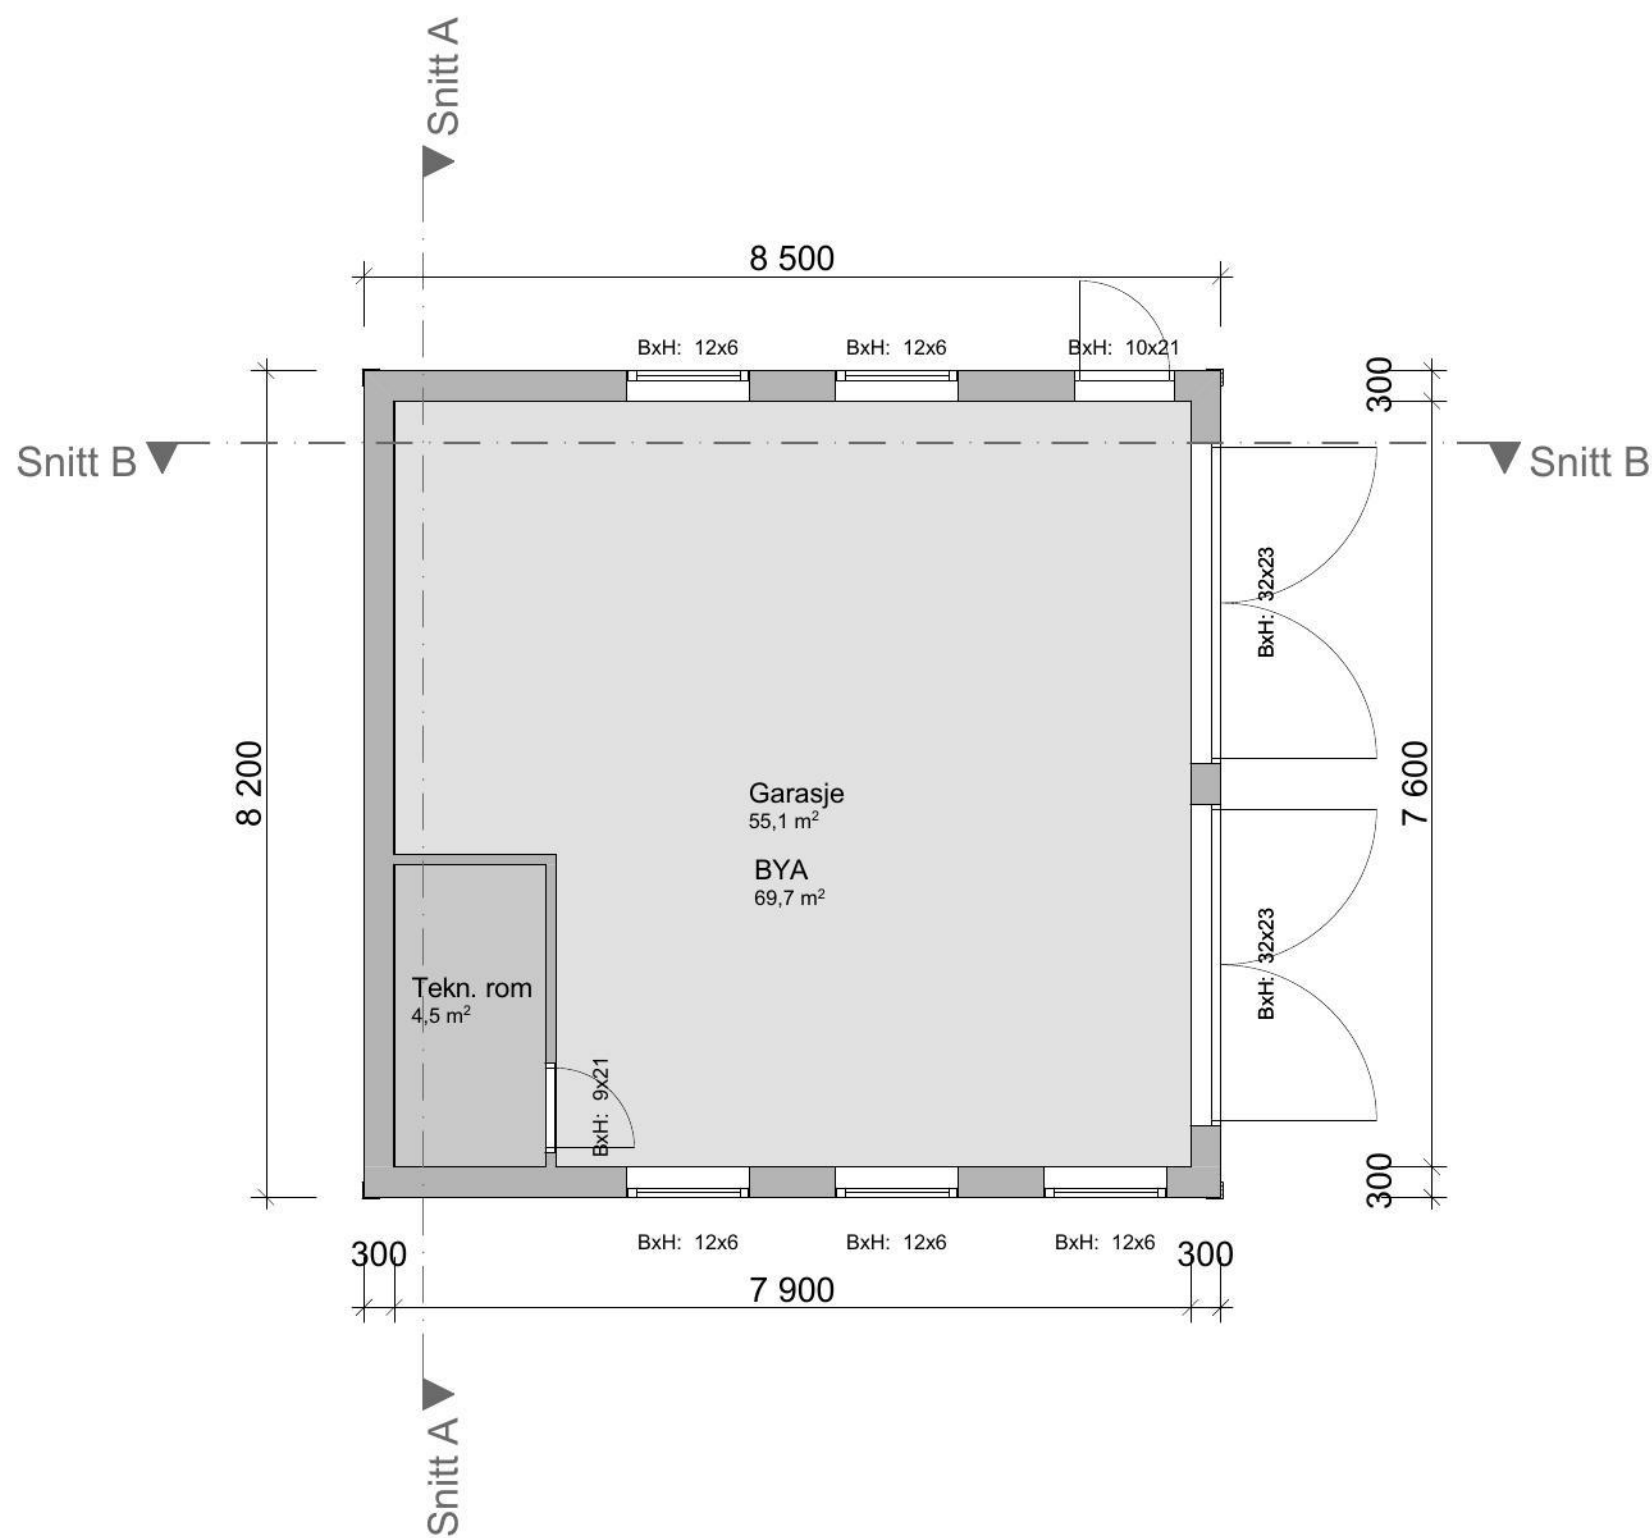

1. Etasje 1:100

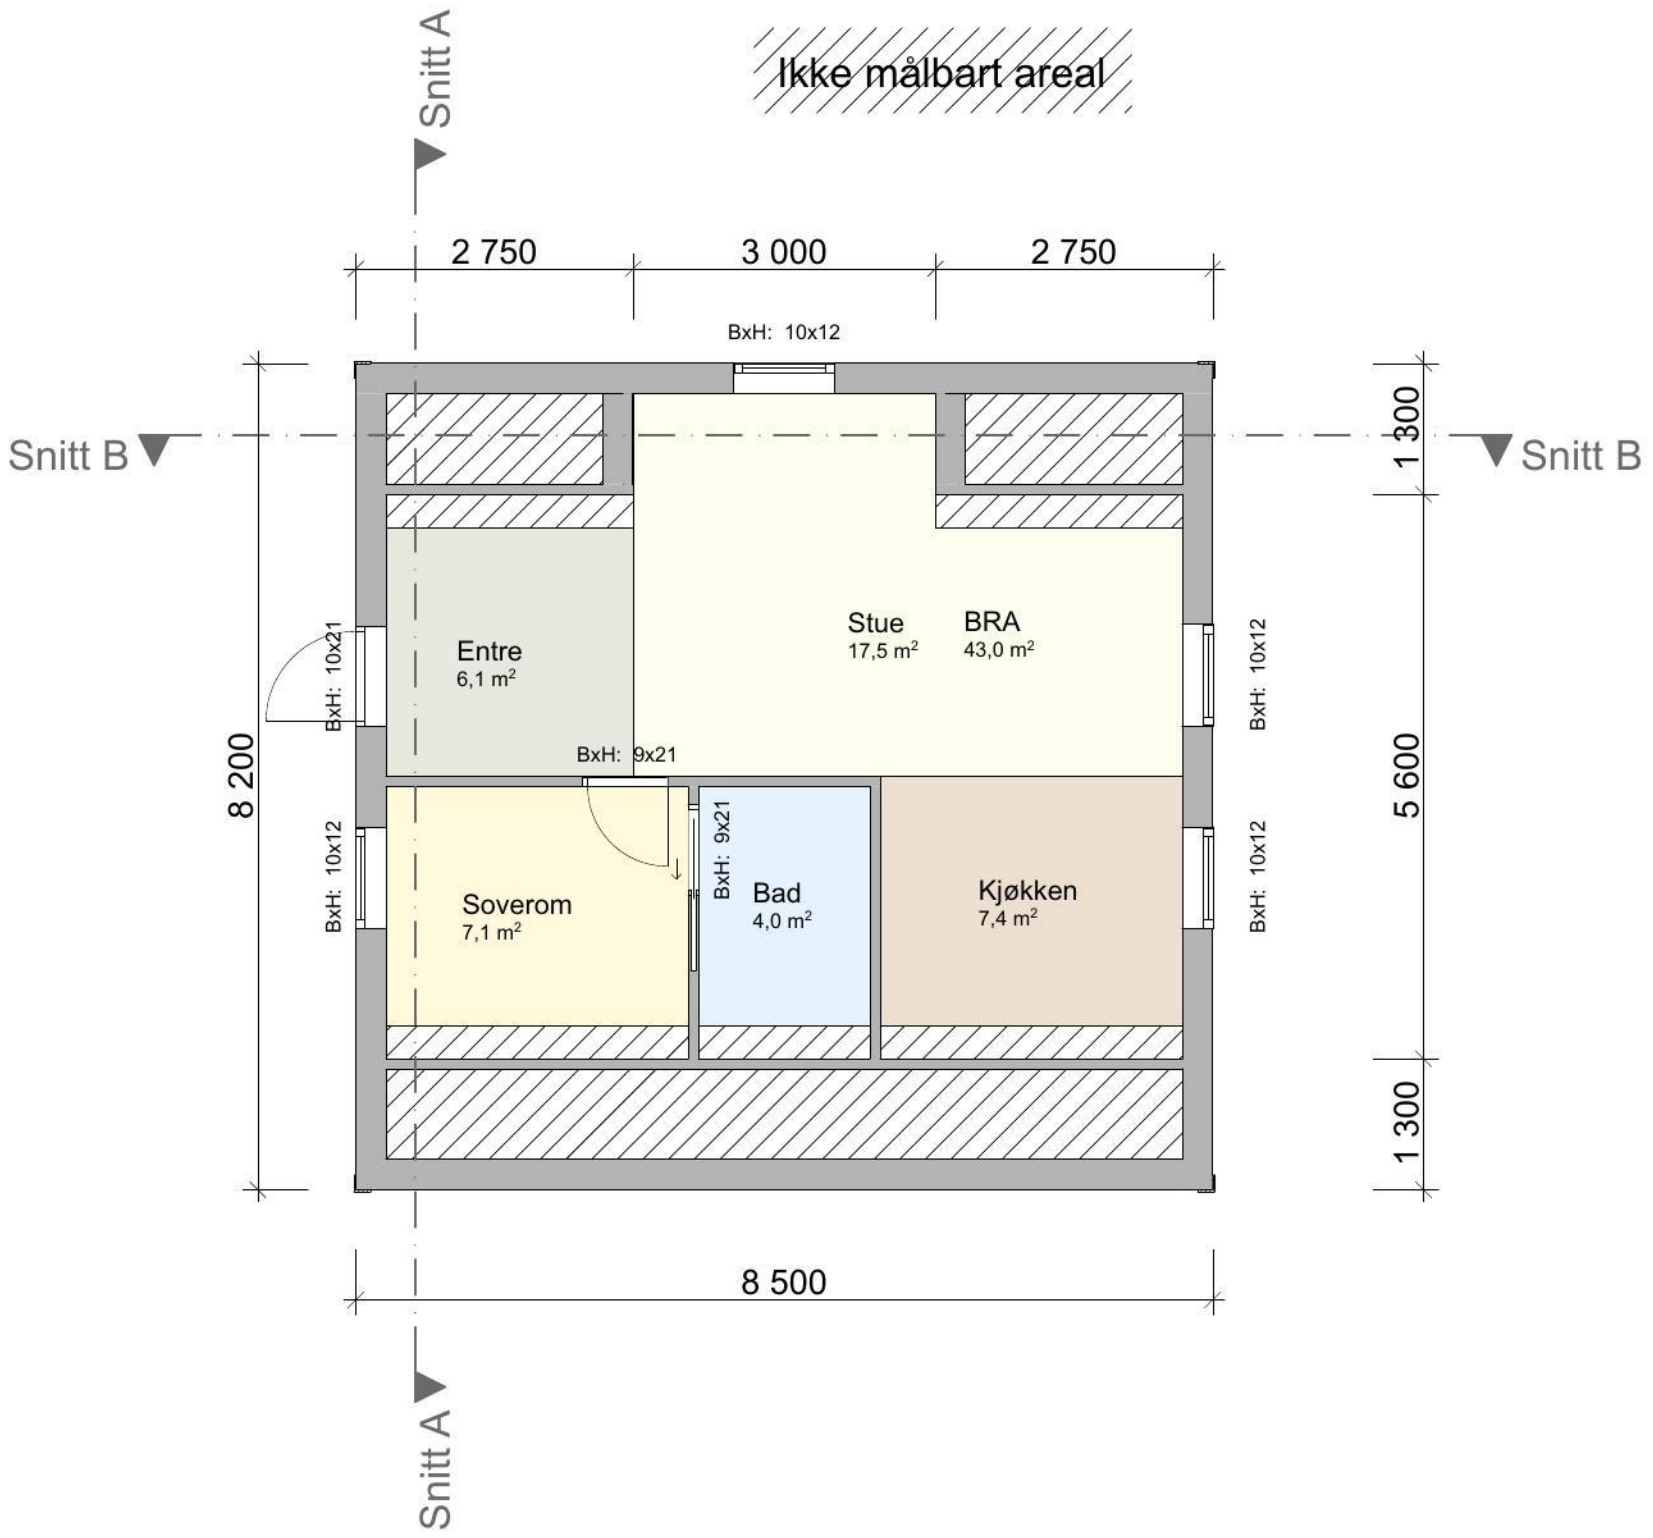

2. Etasje 1:100

Tiltakshaver: Arve Gundersen Gamle Tindlundvei 33 1718 Greåker		Gnr./Bnr./Festnr.: 2075/54	
		Dato: 15.12.2023	
TN Tegning AS Yvenbråten 2 1715 YVEN			
© Alle rettigheter tilhører utførende for prosjektering, kopiering eller bruk av disse tegningene er forbudt uten skriftlig samtykke		Målestokk: 1:100	
Tegning: Plan		Tegningsnr.: A20-01	Rev.: .
		Sign.:	