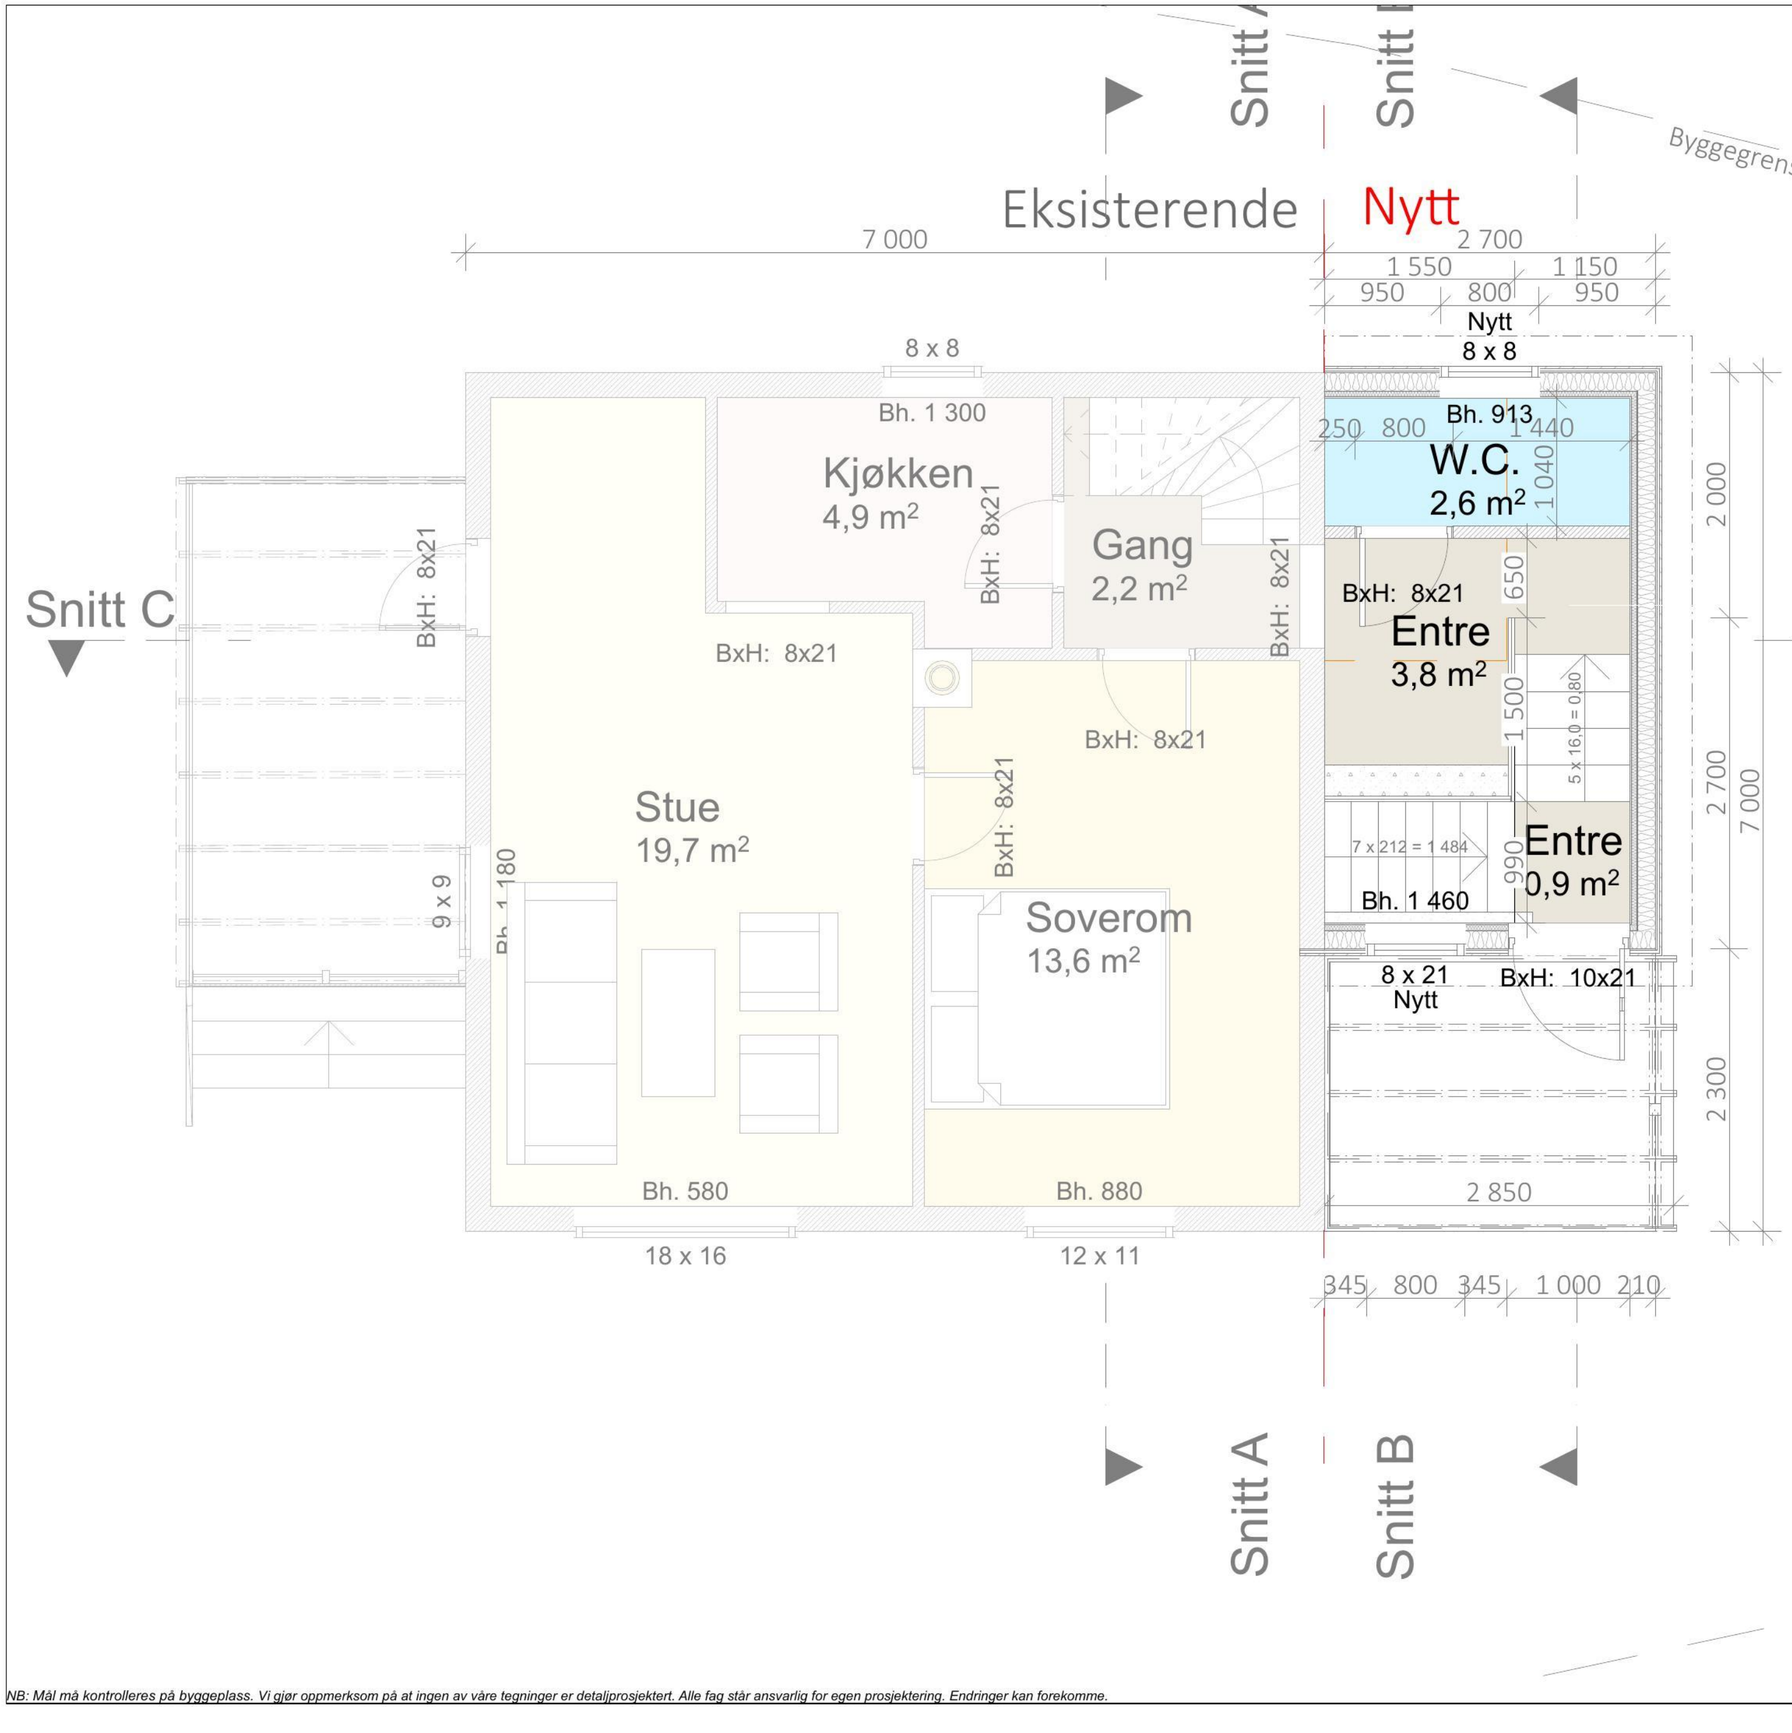


Eksisterende BRA
47,0 m²

Rives BRA
2,8 m²

Nytt BRA
10,7 m²

Åpent area ny pergola BRA
6,3 m²

Vinterhage BRA
9,3 m²

BYA Eksisterende
62,1 m²

BYA Rives
3,3 m²

BYA Nytt tilbygg
13,0 m²

BYA Nytt glasstak
6,2 m²

REV.	BESKRIVELSE	SIGN.	DATO
B			
A			

Prosjekt:
Påbygg og tilbygg

Tiltakshaver:
Katrin Gering
Byggeplass: Gitleveien 2 gnr/bnr 62 /129
4319 Sandnes

Entreprenør:

Arkitekt:
MARK arkitekter AS
Hillevågsveien 101, 4016 Stavanger
www.onlinearkitektene.no

Prosjektnr.:	Prosjektfase:	Tegnet av:	Kontrollert av:	Dato:
975	SØK / ARB	A. V. K.	O. M.	20.12.2023

Tegning:
Plan 1. etasje

Målestokk: 1:50 **Papir:** A3

© Alle rettigheter tilhører MARK arkitekter, kopiering eller bruk av disse tegningene er forbudt uten skriftlig samtykke.

Tegningsnr.: Tegning v.5 - 2

NB: Mål må kontrolleres på byggeplass. Vi gjør oppmerksom på at ingen av våre tegninger er detaljprosjektert. Alle fag står ansvarlig for egen prosjektering. Endringer kan forekomme.