

Situasjonskart

Eiendom: 62/129


Utskriftsdato: 20.12.2023

Adresse: Gitleveien 2

Målestokk: 1:500



UTM-32

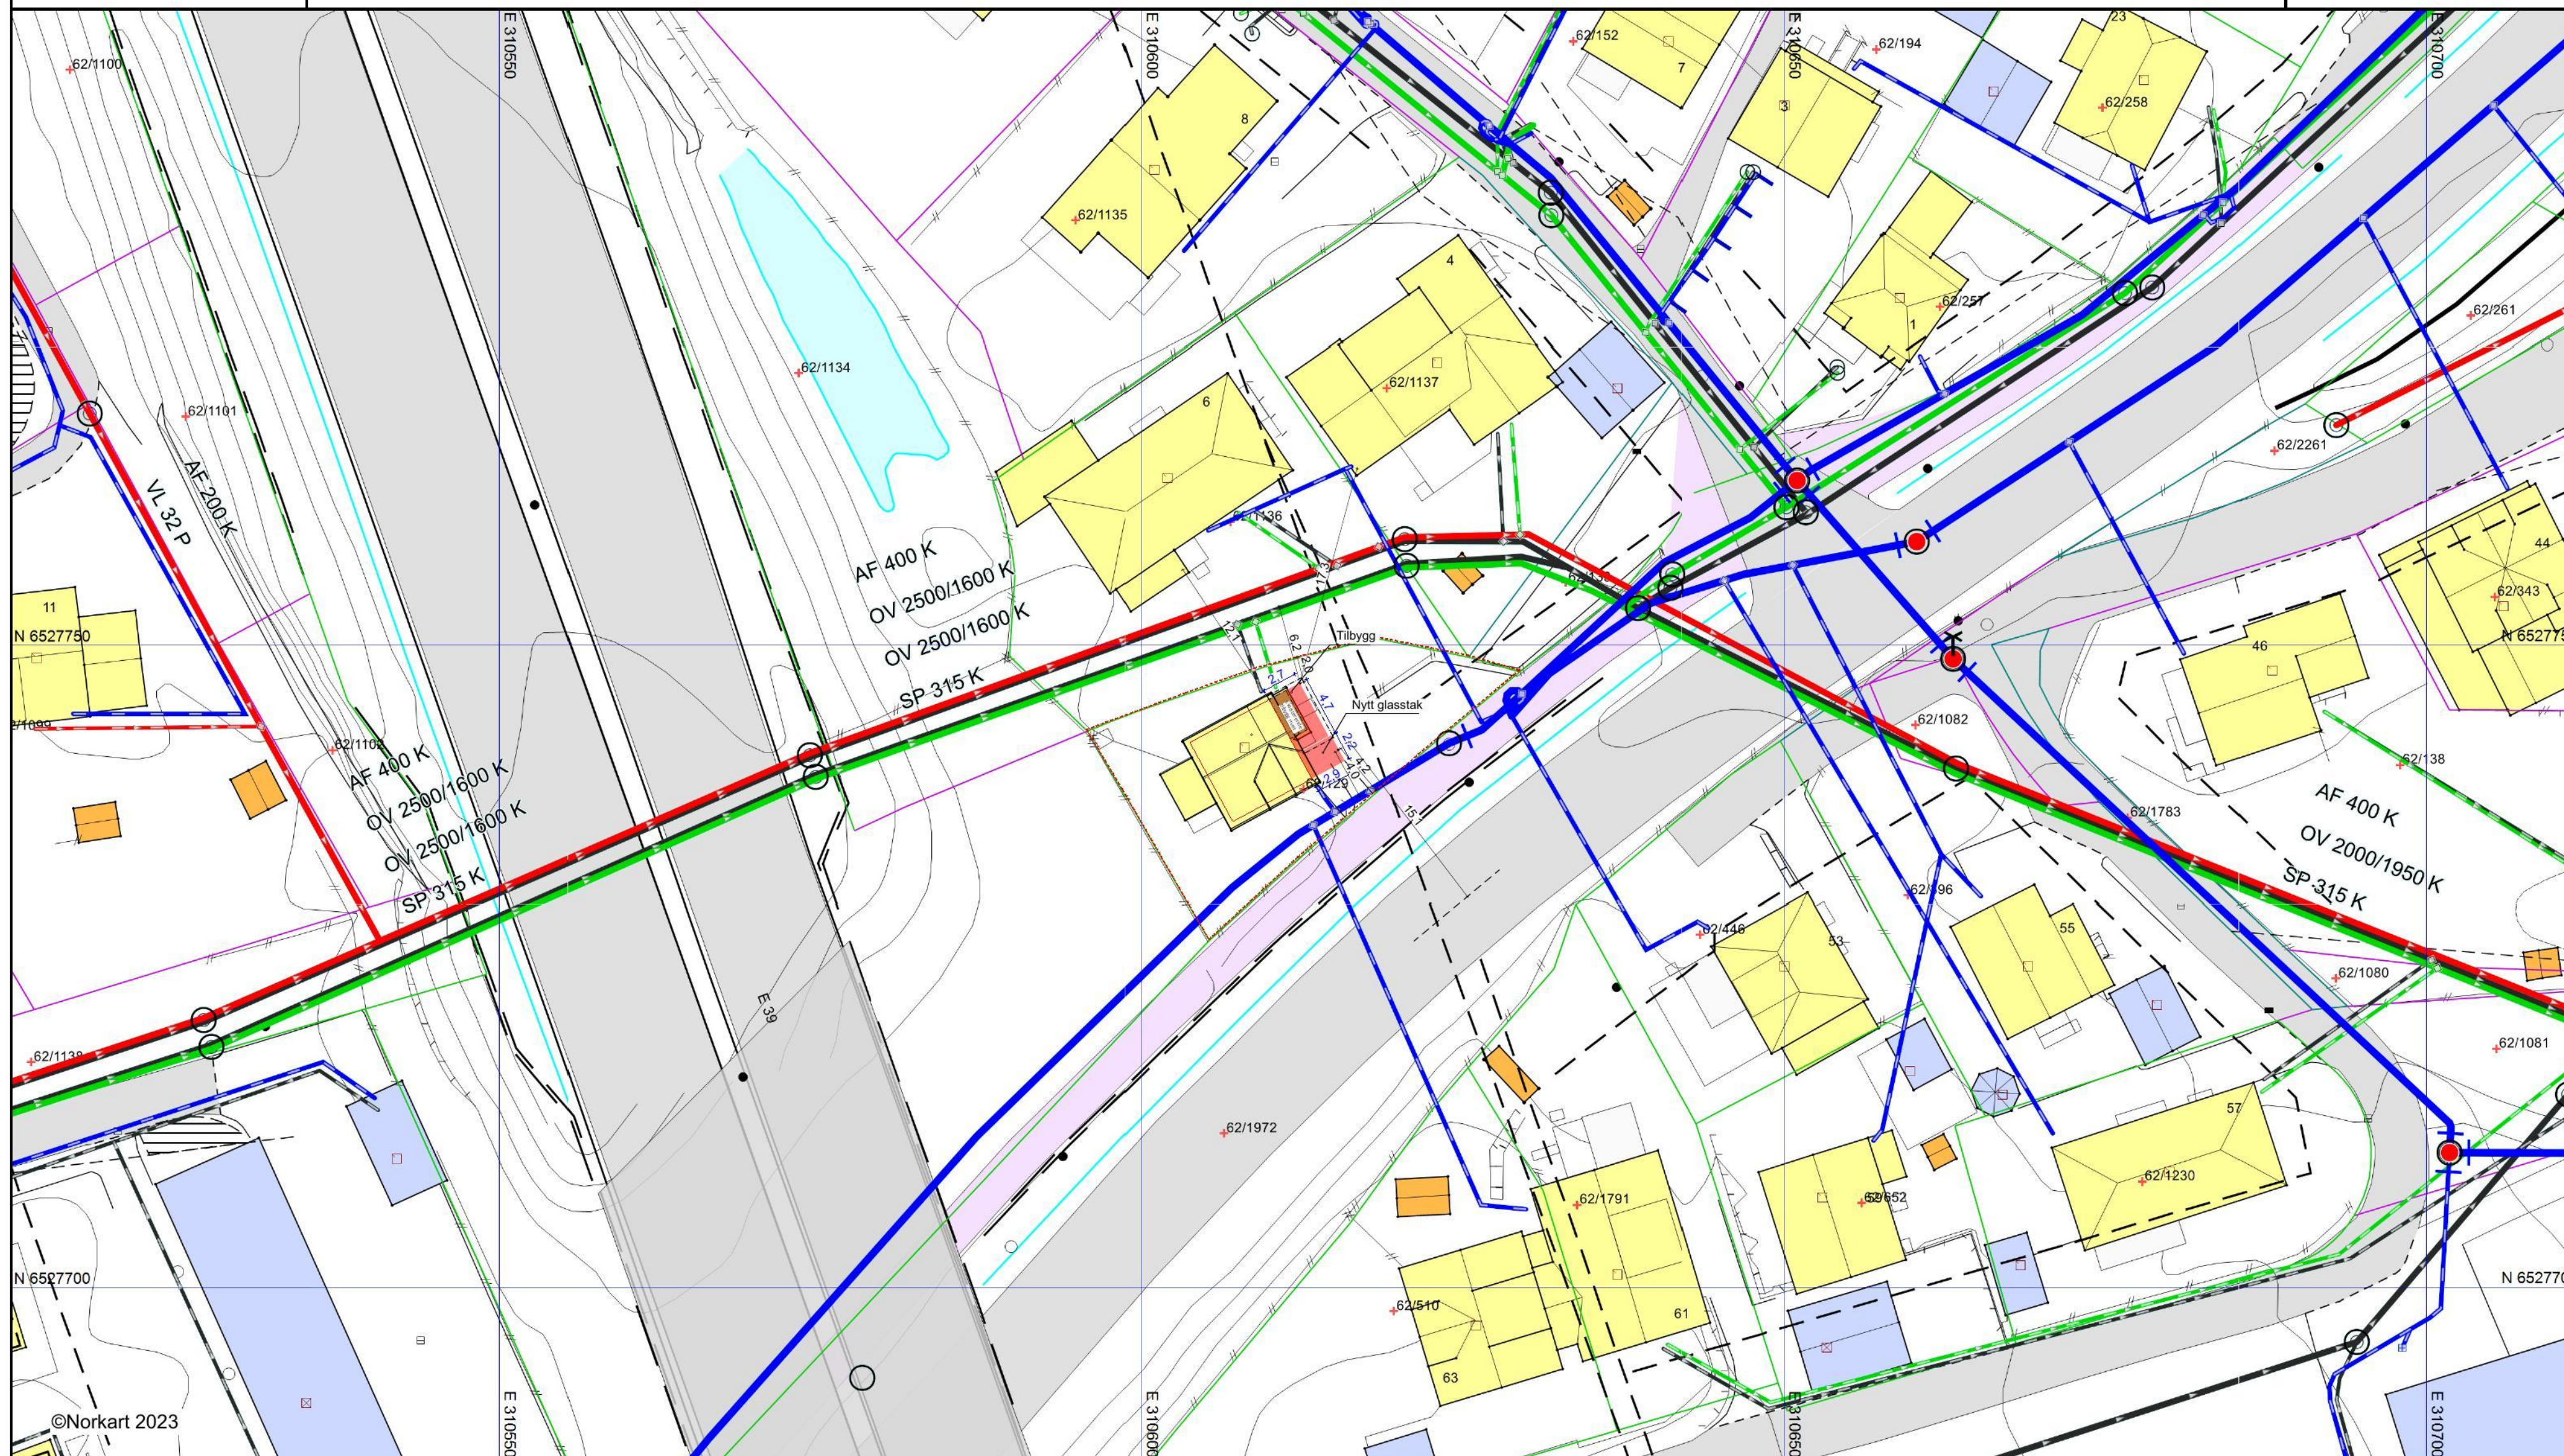

1) Det tas forbehold om feil i kartgrunnlaget. 2) Ved utskrift fra PDF-fil kan målestokken bli unøyaktig.