



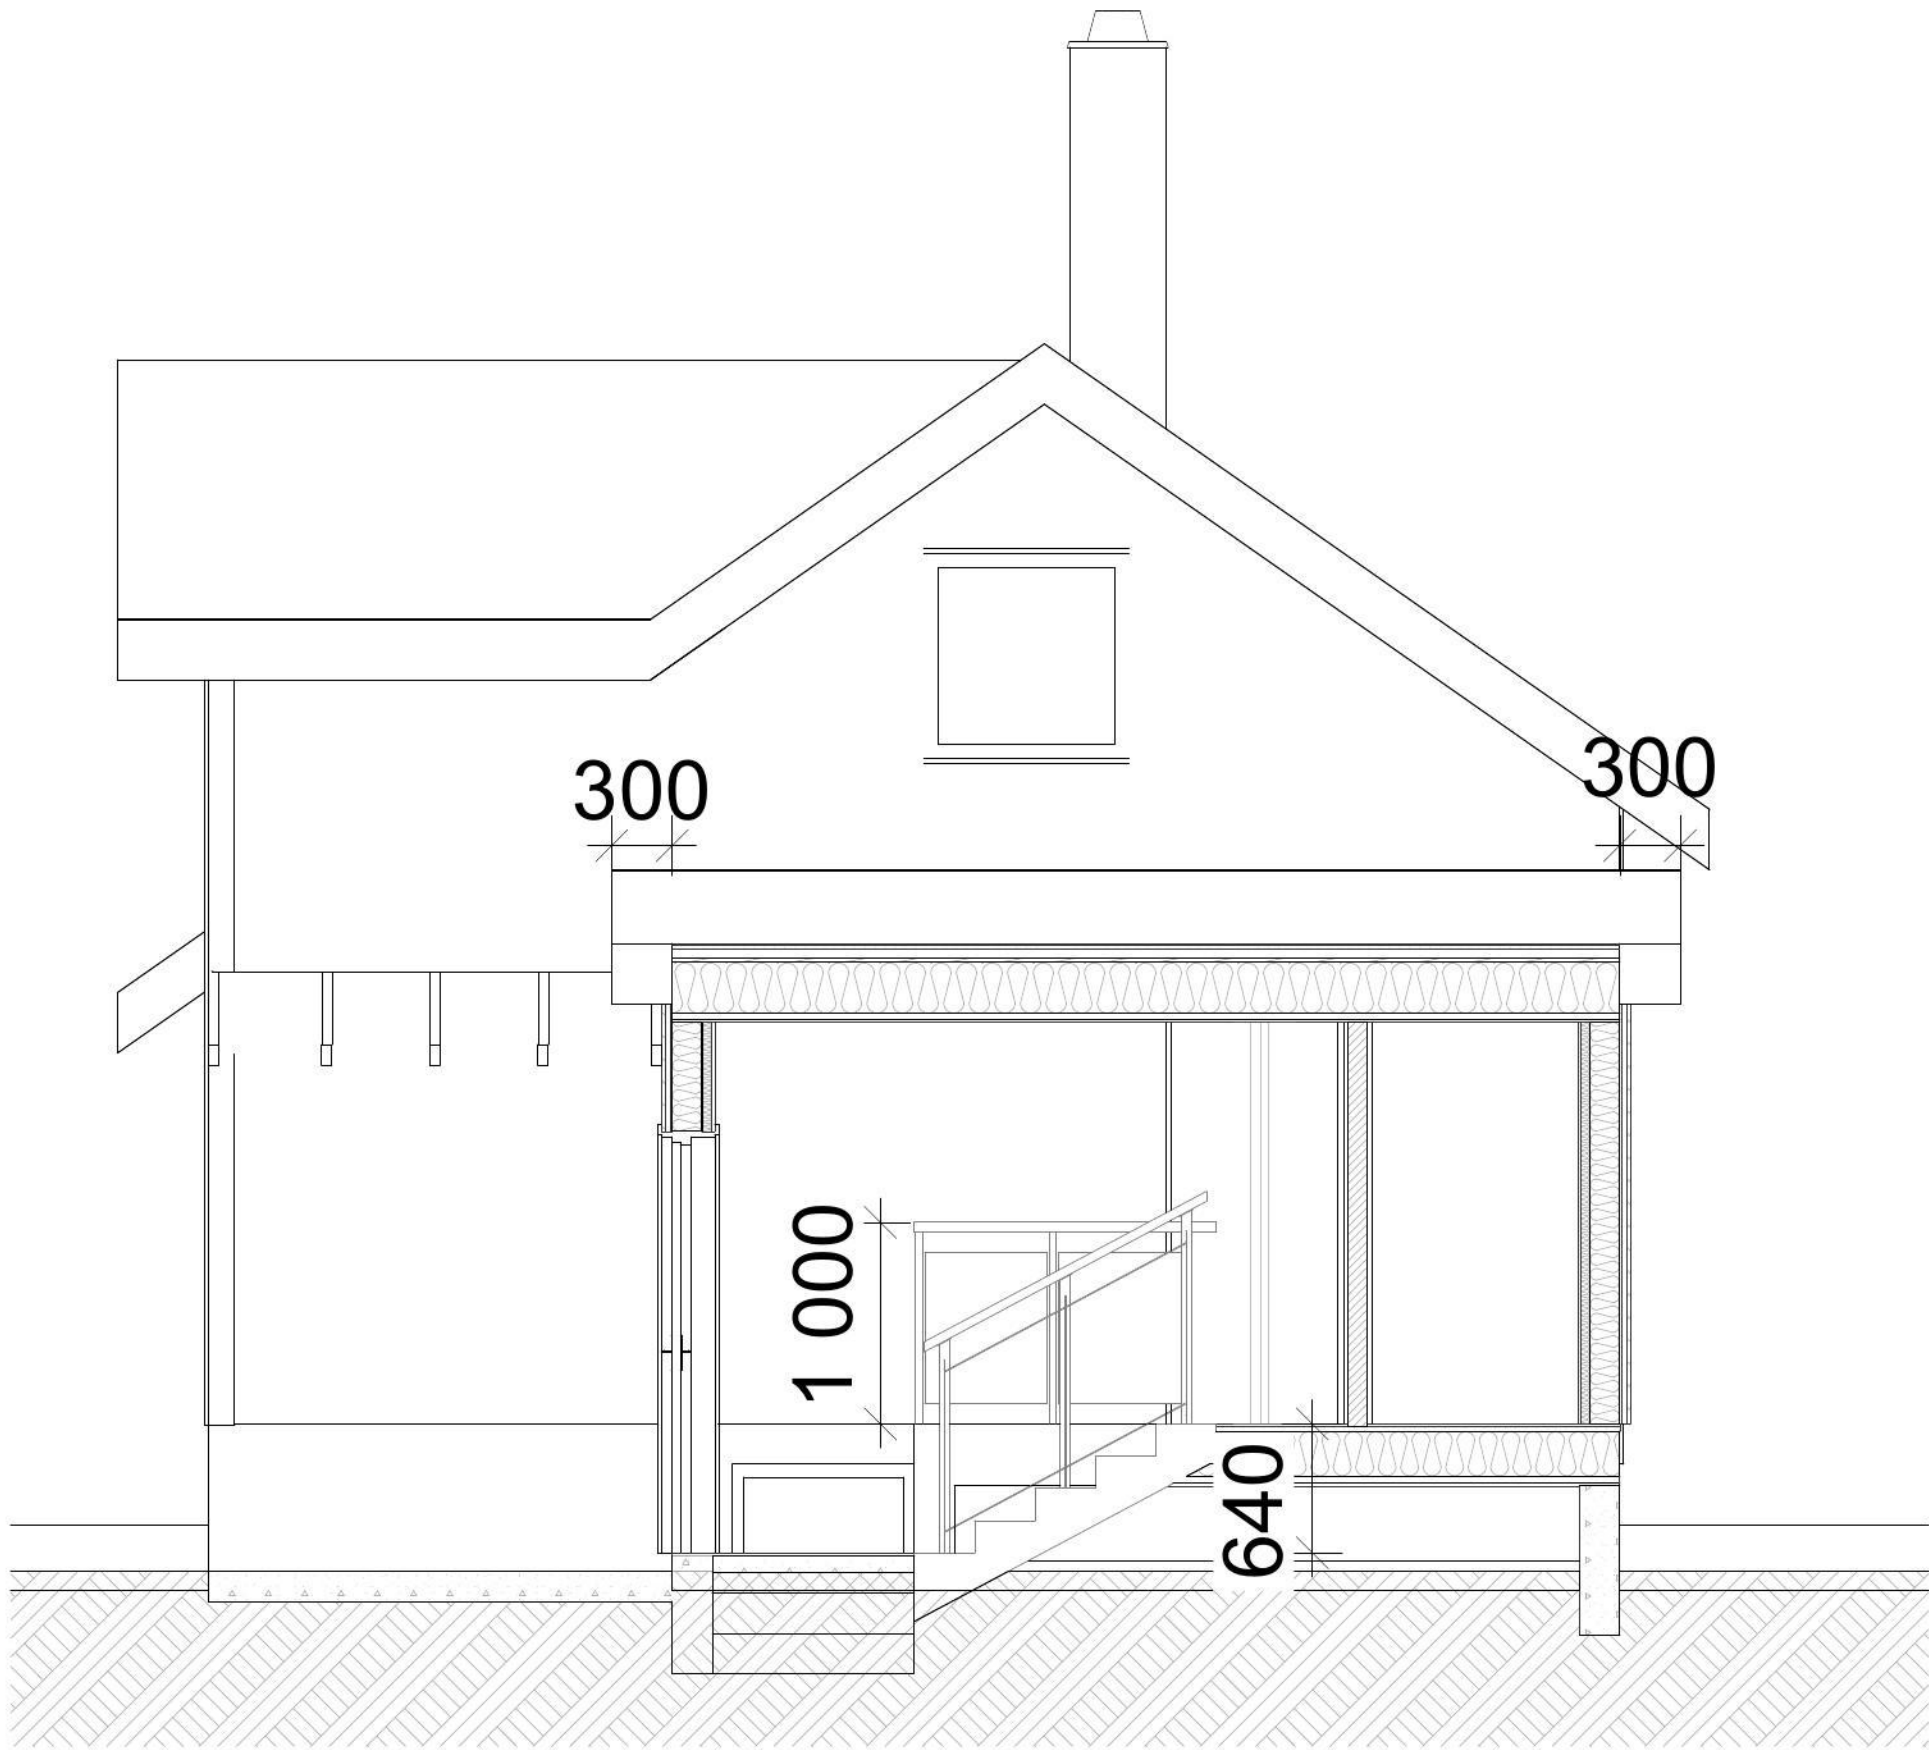

Snitt B

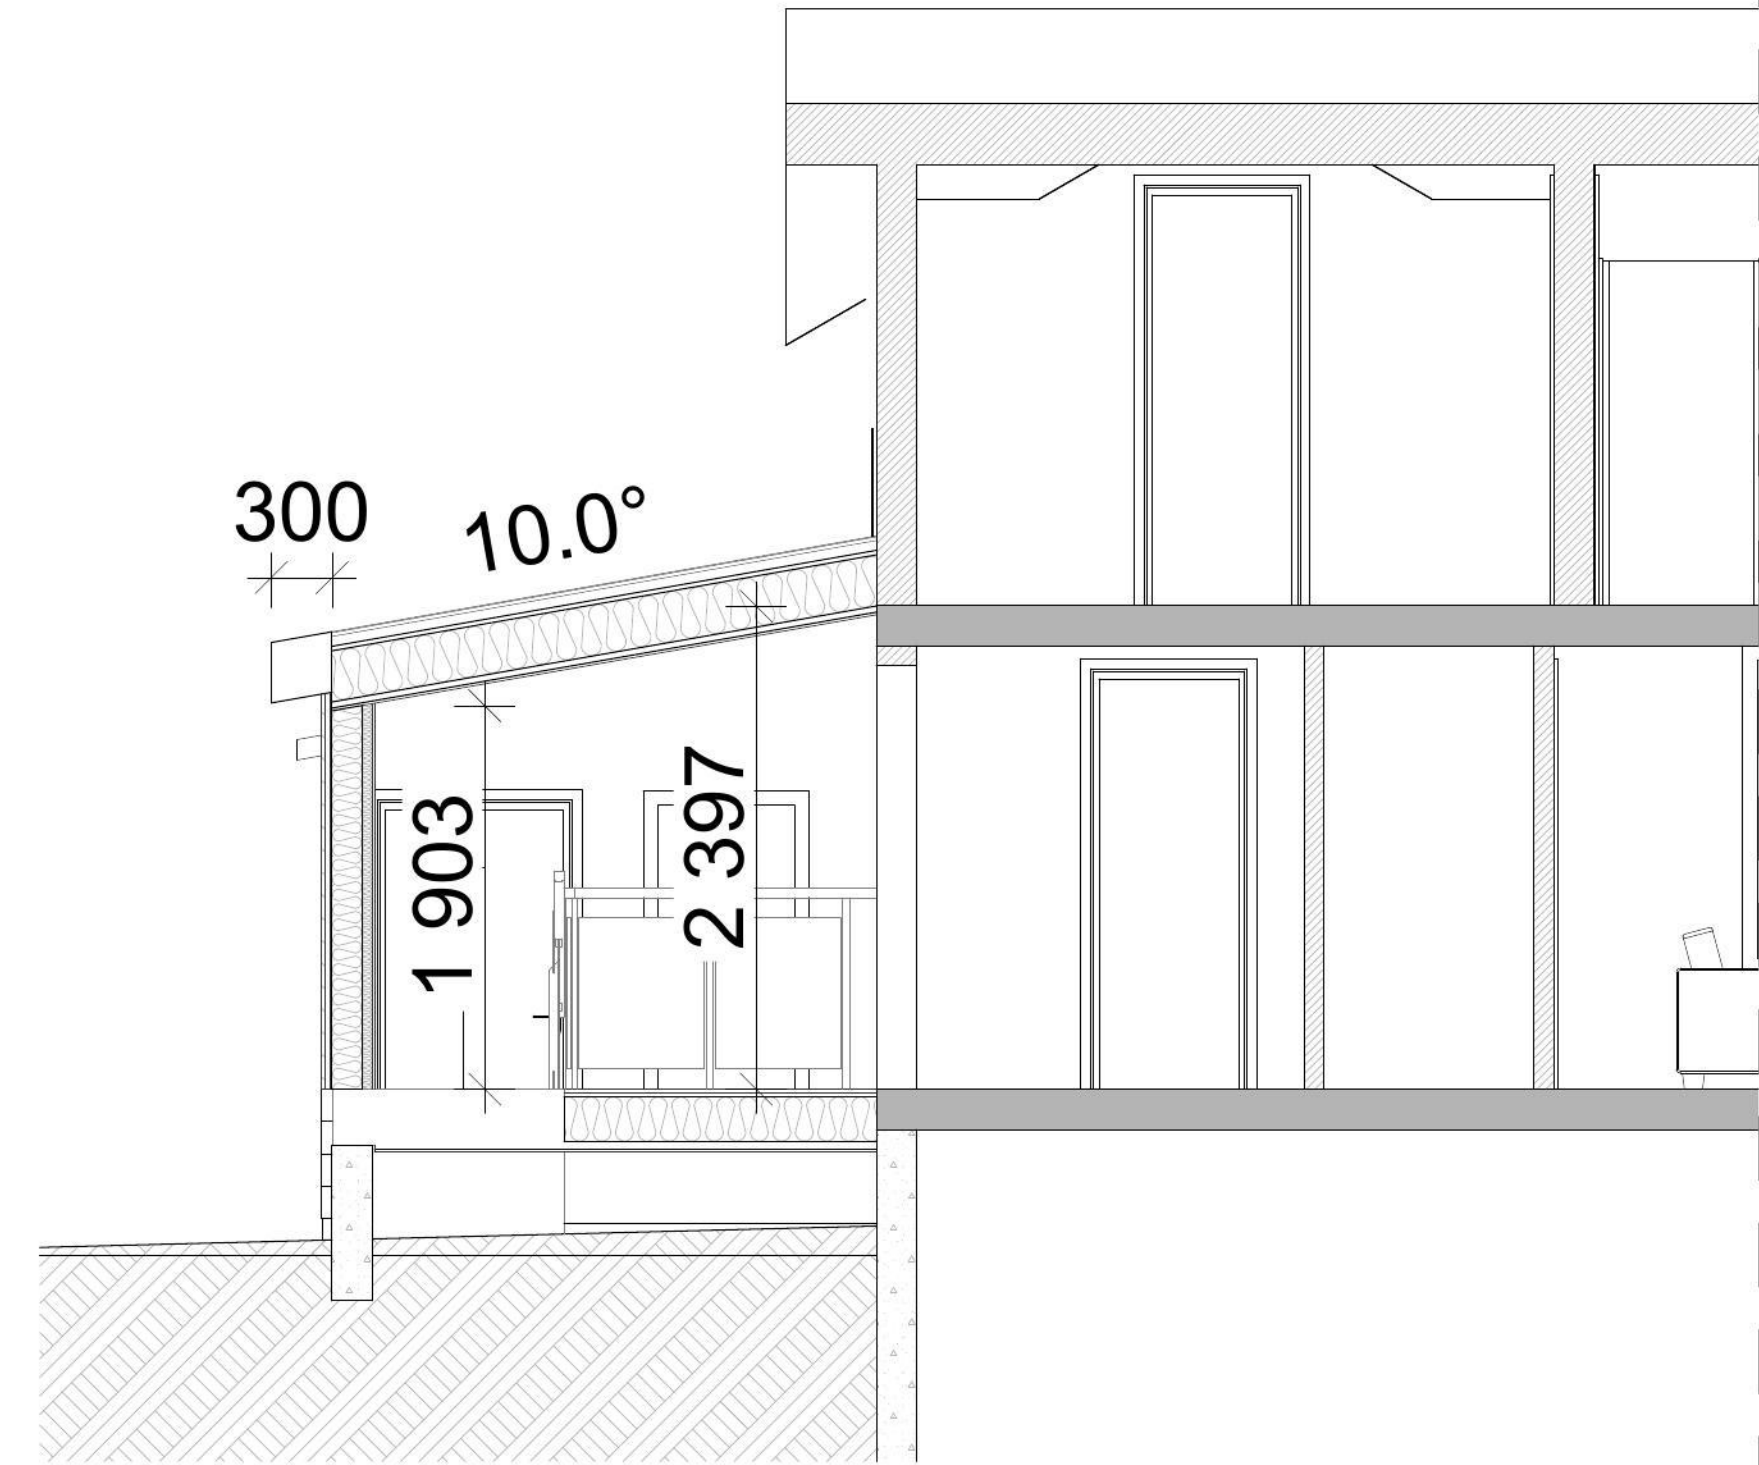

Snitt C

B			
A			
REV.	BESKRIVELSE	SIGN.	DATO
Prosjekt: Påbygg og tilbygg			
Tiltakshaver: Katrin Gering Byggeplass: Gitleveien 2 gnr/bnr 62 /129 4319 Sandnes			Entreprenør:
Arkitekt: MARK arkitekter AS Hillevågsveien 101, 4016 Stavanger www.onlinearkitektene.no			MARK ONLINEARKITEKTENE
Prosjektnr.: 975	Prosjektfase: SØK / ARB	Tegnet av: A. V. K.	Kontrollert av: O. M.
Tegning: Snitt B og C			Dato: 20.12.2023
Målestokk: 1:50			Papir: A3
© Alle rettigheter tilhører MARK arkitekter, kopiering eller bruk av disse tegningene er forbudt uten skriftlig samtykke.			Tegningsnr.: Tegning v.5 - 6

NB: Mål må kontrolleres på byggeplass. Vi gjør oppmerksom på at ingen av våre tegninger er detaljprosjektert. Alle fag står ansvarlig for egen prosjektering. Endringer kan forekomme.