

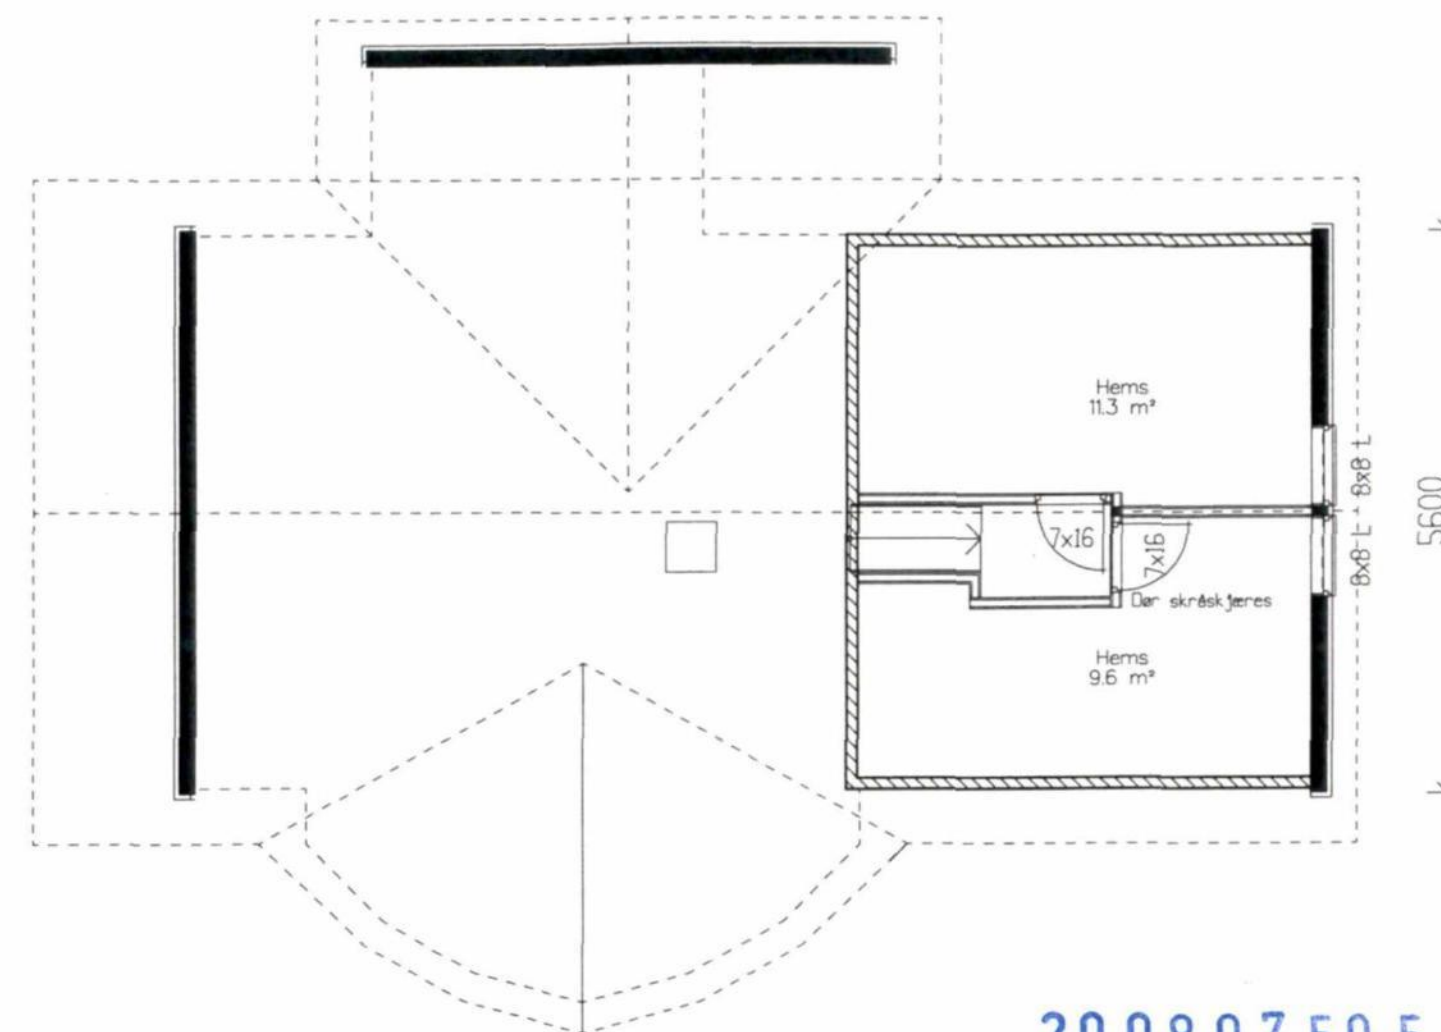
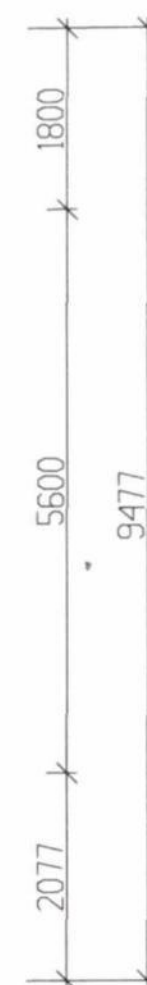


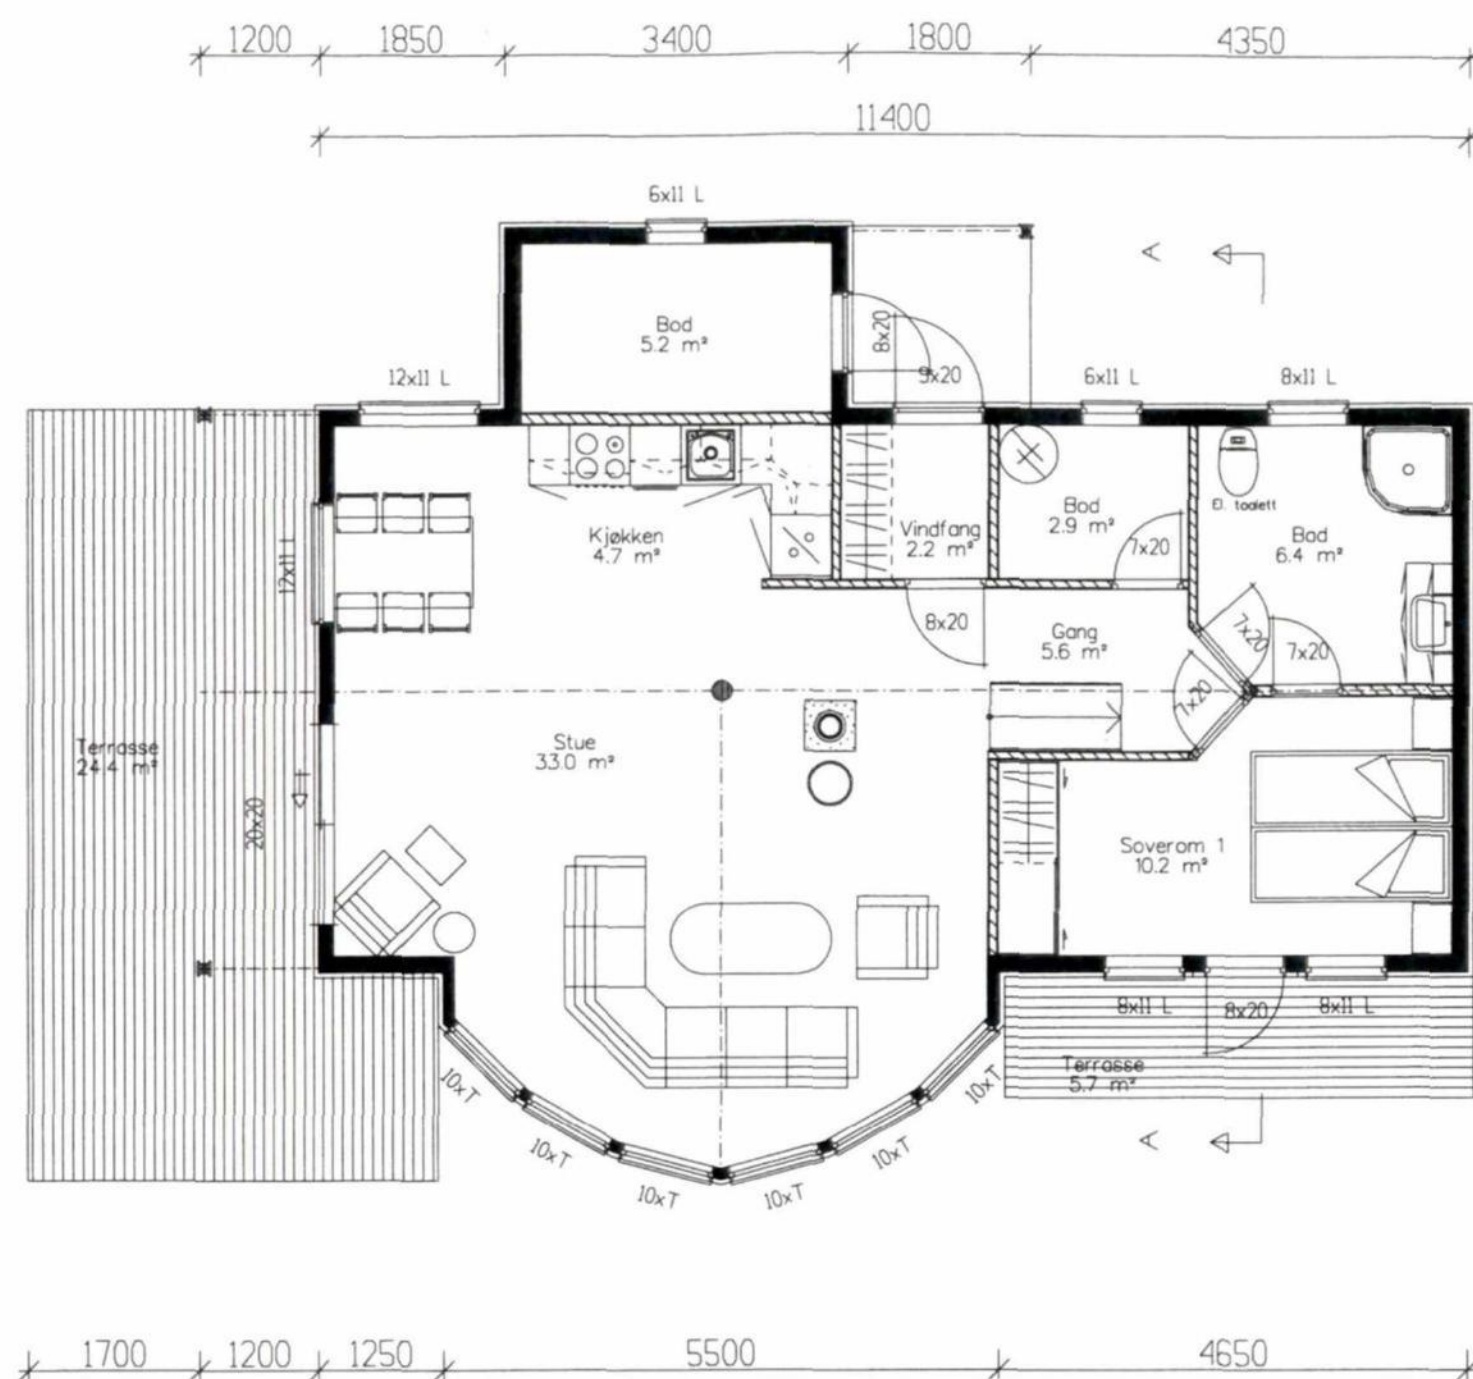

200807505-1

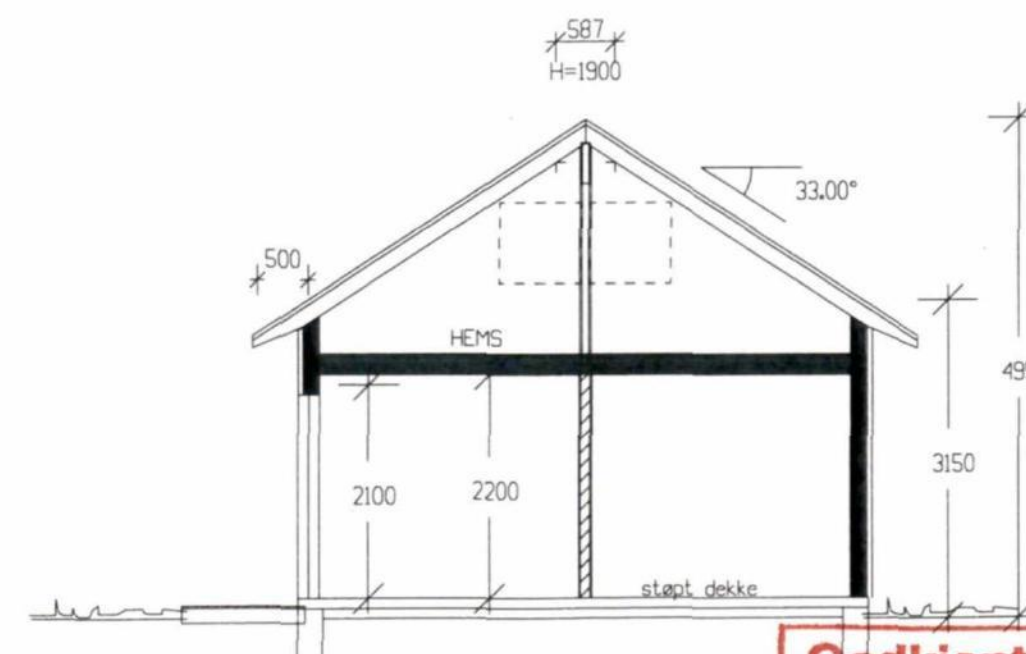

Snitt A-A

Godkjent av bygningsjefen
i Sandnes kommune

Sak: 267/2009

	BRA	BYA	89.7 m²
Hovedplan	74.00	Isolert grunnflate	78.2m²
Sum 1 m²	74.00		

Panorama 2+



www.stjernehytten.no



Tiltakshaver: Øyvind Wathne

Byggeplass: Li - Hommersåk

Kommune: Sandnes kommune

Gnr: 110 Bnr: 218

Mål: 1 : 100

Planer og snitt

Vedlegg E1

Arkitekt: A.Fraffjord

Dato: 29.08.08

Selger: TR

Prosjekt: 1040

Tegn.nr: 501

© Tegningen er beskyttet iht. lov om opphavsrett.