



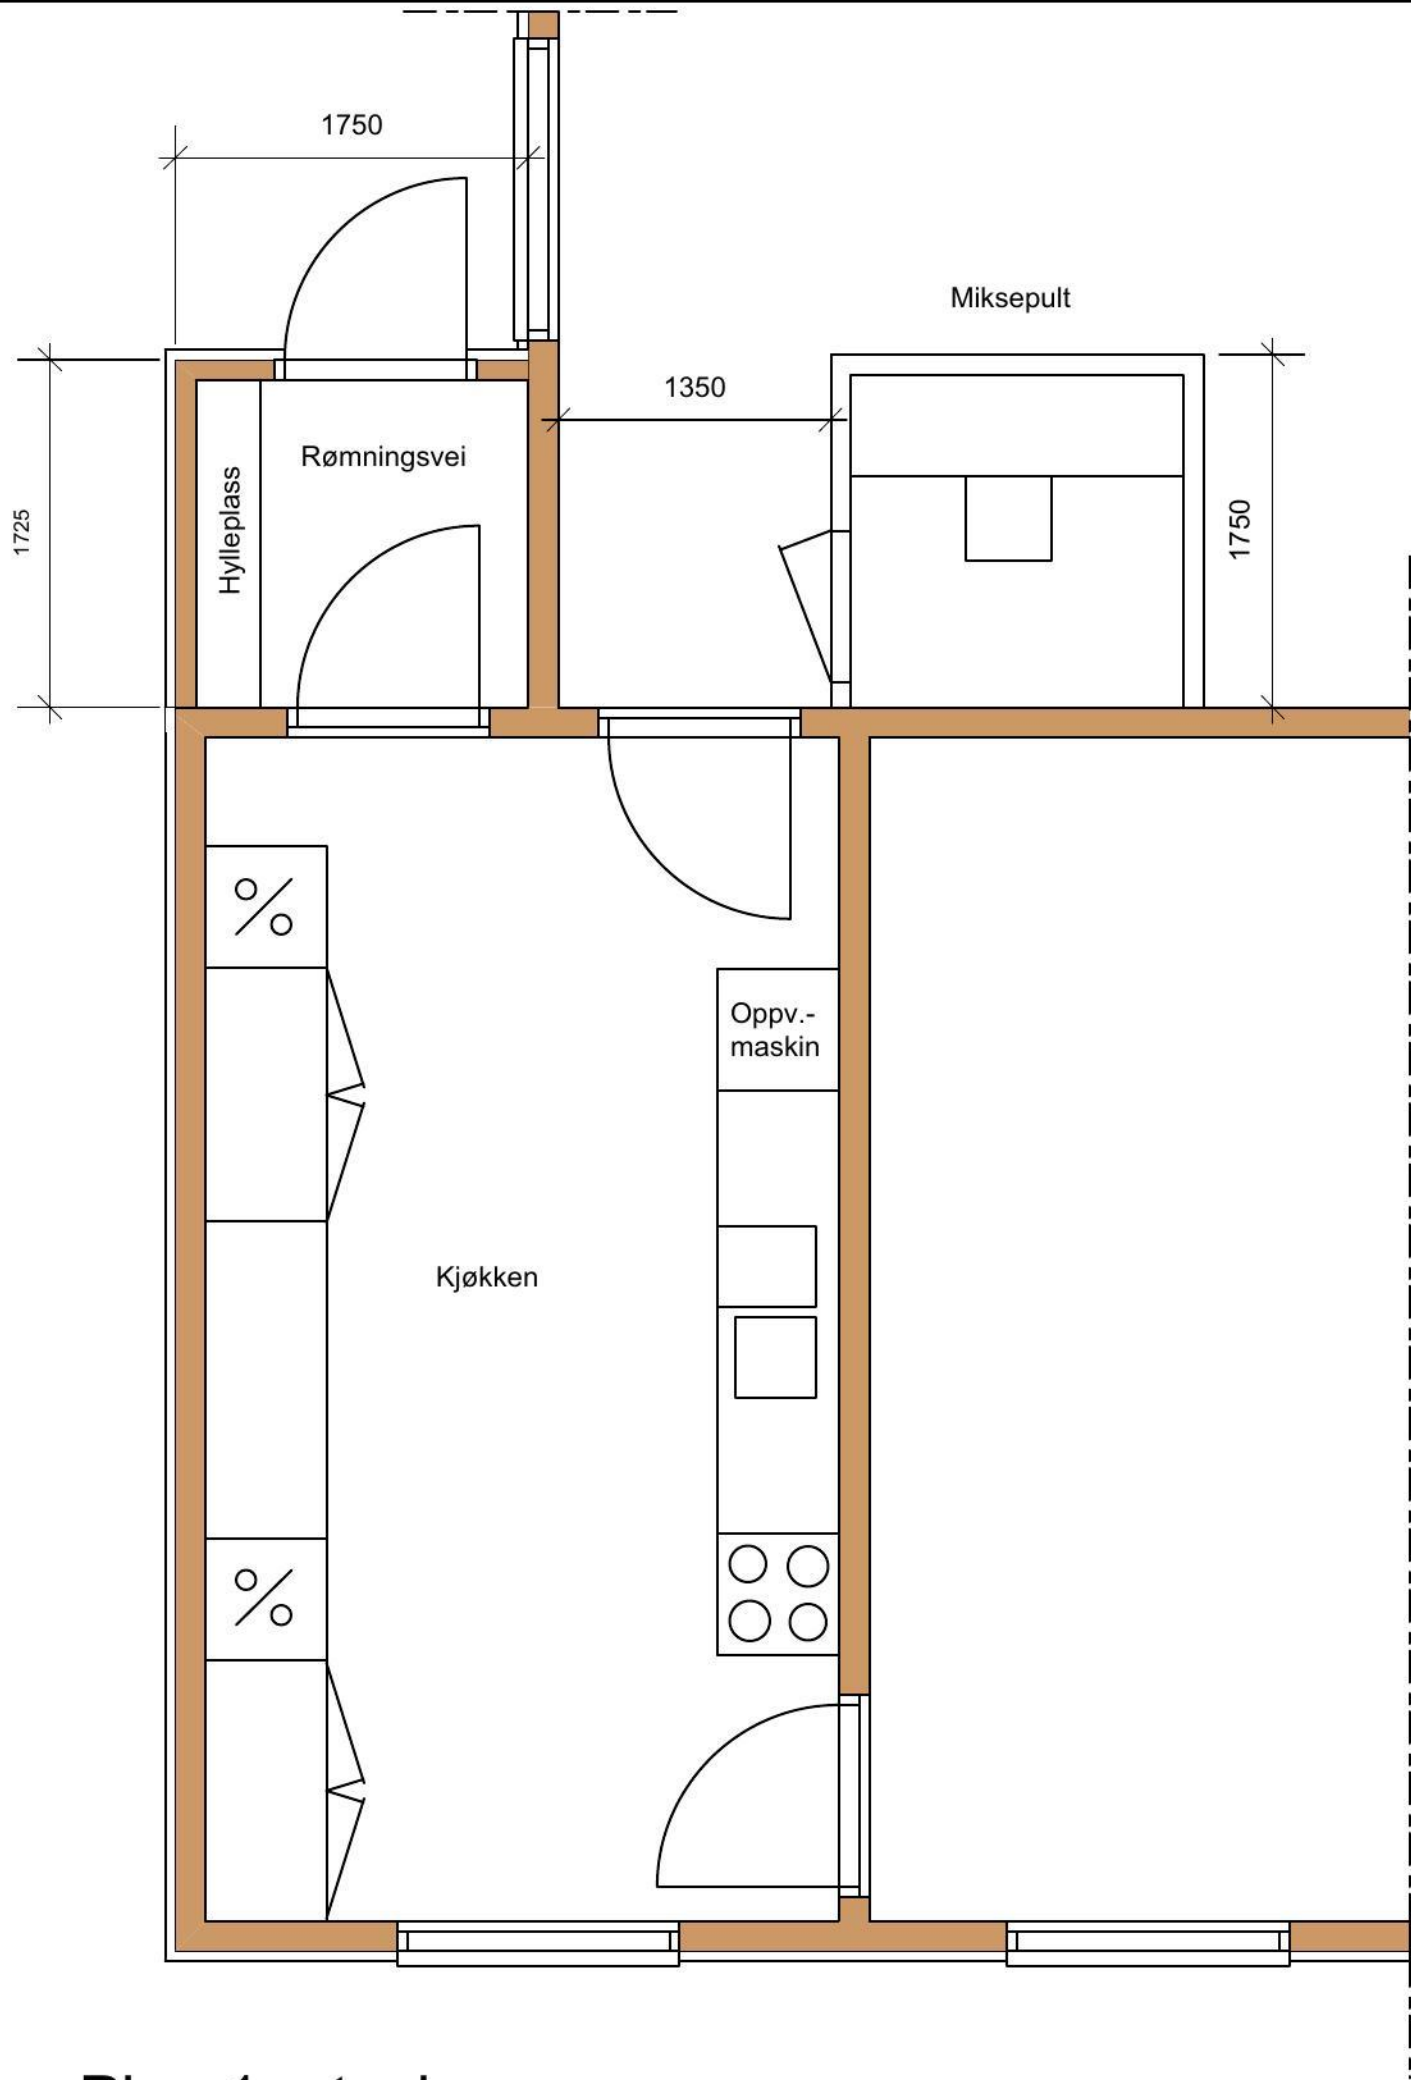

Plan 1. etasje
Eksisterende løsning
Mål 1:50

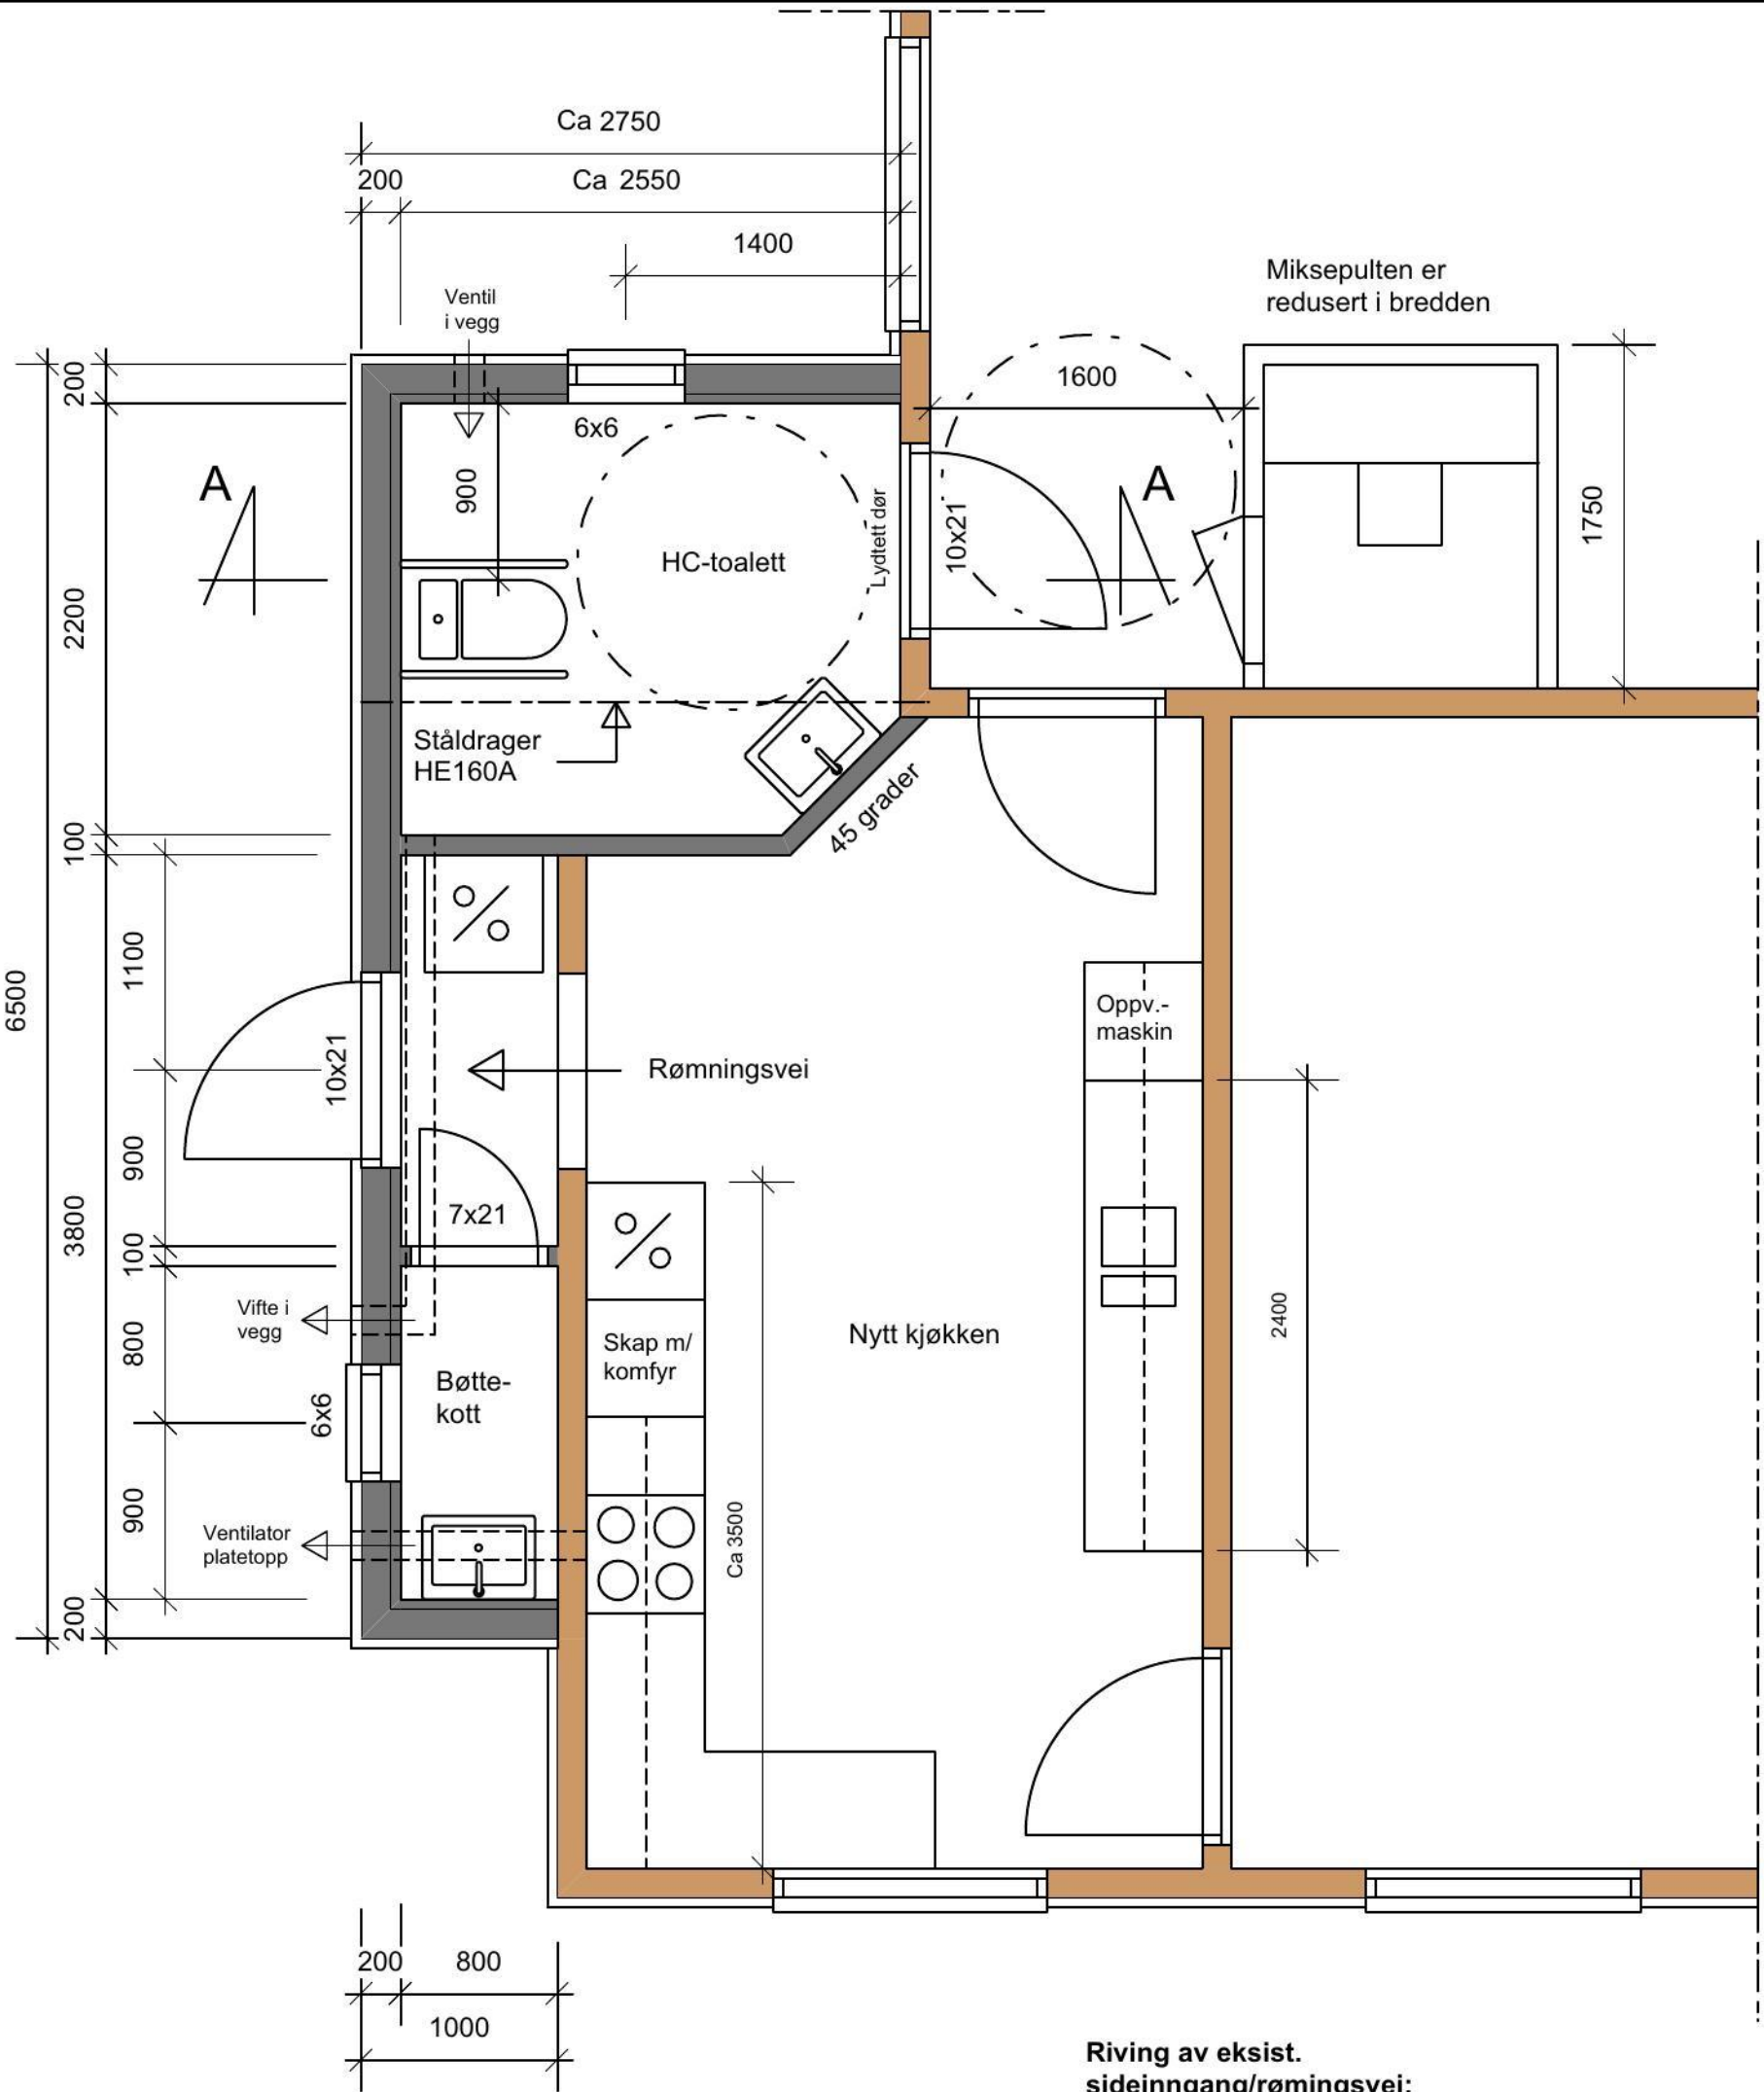

Plan 1. etasje
Tilbygg/ombygging
Mål 1:50

**Riving av eksist.
sideinngang/rømningsvei:**
BYA = 3,0 m2
BRA = 2,7 m2
Nytt tilbygg:
BYA = 9,4 m2
BRA = 7,4 m2

Tegning nr 1: Plan før og etter
Tegning nr 2: Snitt og fasader
Tegning nr 3: Situasjonsplan

Mål må kontrolleres på plassen!

Riktig målestokk ved
utskrift på A3

Endret planløsning	06 - 11 - 23	ØN
Påført ventilasjonsløsning	30 - 10 - 23	ØN
Revideringen gjelder:	Dato:	Rev. av:
Eiendom: Skjeberg Misjonshus	Gnr/bnr: 1022/38	Kommune: Sarpsborg
Eier: Skjeberg Normisjon v/Stein Holt. Stenbruddveien 22A, 1746 Skjeberg	Målestokk: 1 : 50 1 : 100 1 : 500	Arkiv nr. 21-23
Byggeadresse: Hasliveien 7, 1746 Skjeberg	Antall bl. 3	Bl.nr. 1
Oppdrag: Ombygging/tilbygg for HC-toalett	Dato: 21 - 09 - 23	
Dokumentasjonstegning	Ø. Nordberg Byggprosjektering	
Arbeidstegning	Bruseveien 14, 1738 Borgenhaugen	
Anbudstegning	Mobiltlf. 48287363. E-post:	
Anmeldelsestegning	onordber@online.no	
Foreløpig tegning	Denne tegningen skal ikke kopieres av andre uten godkjenning av Ø. Nordberg	