



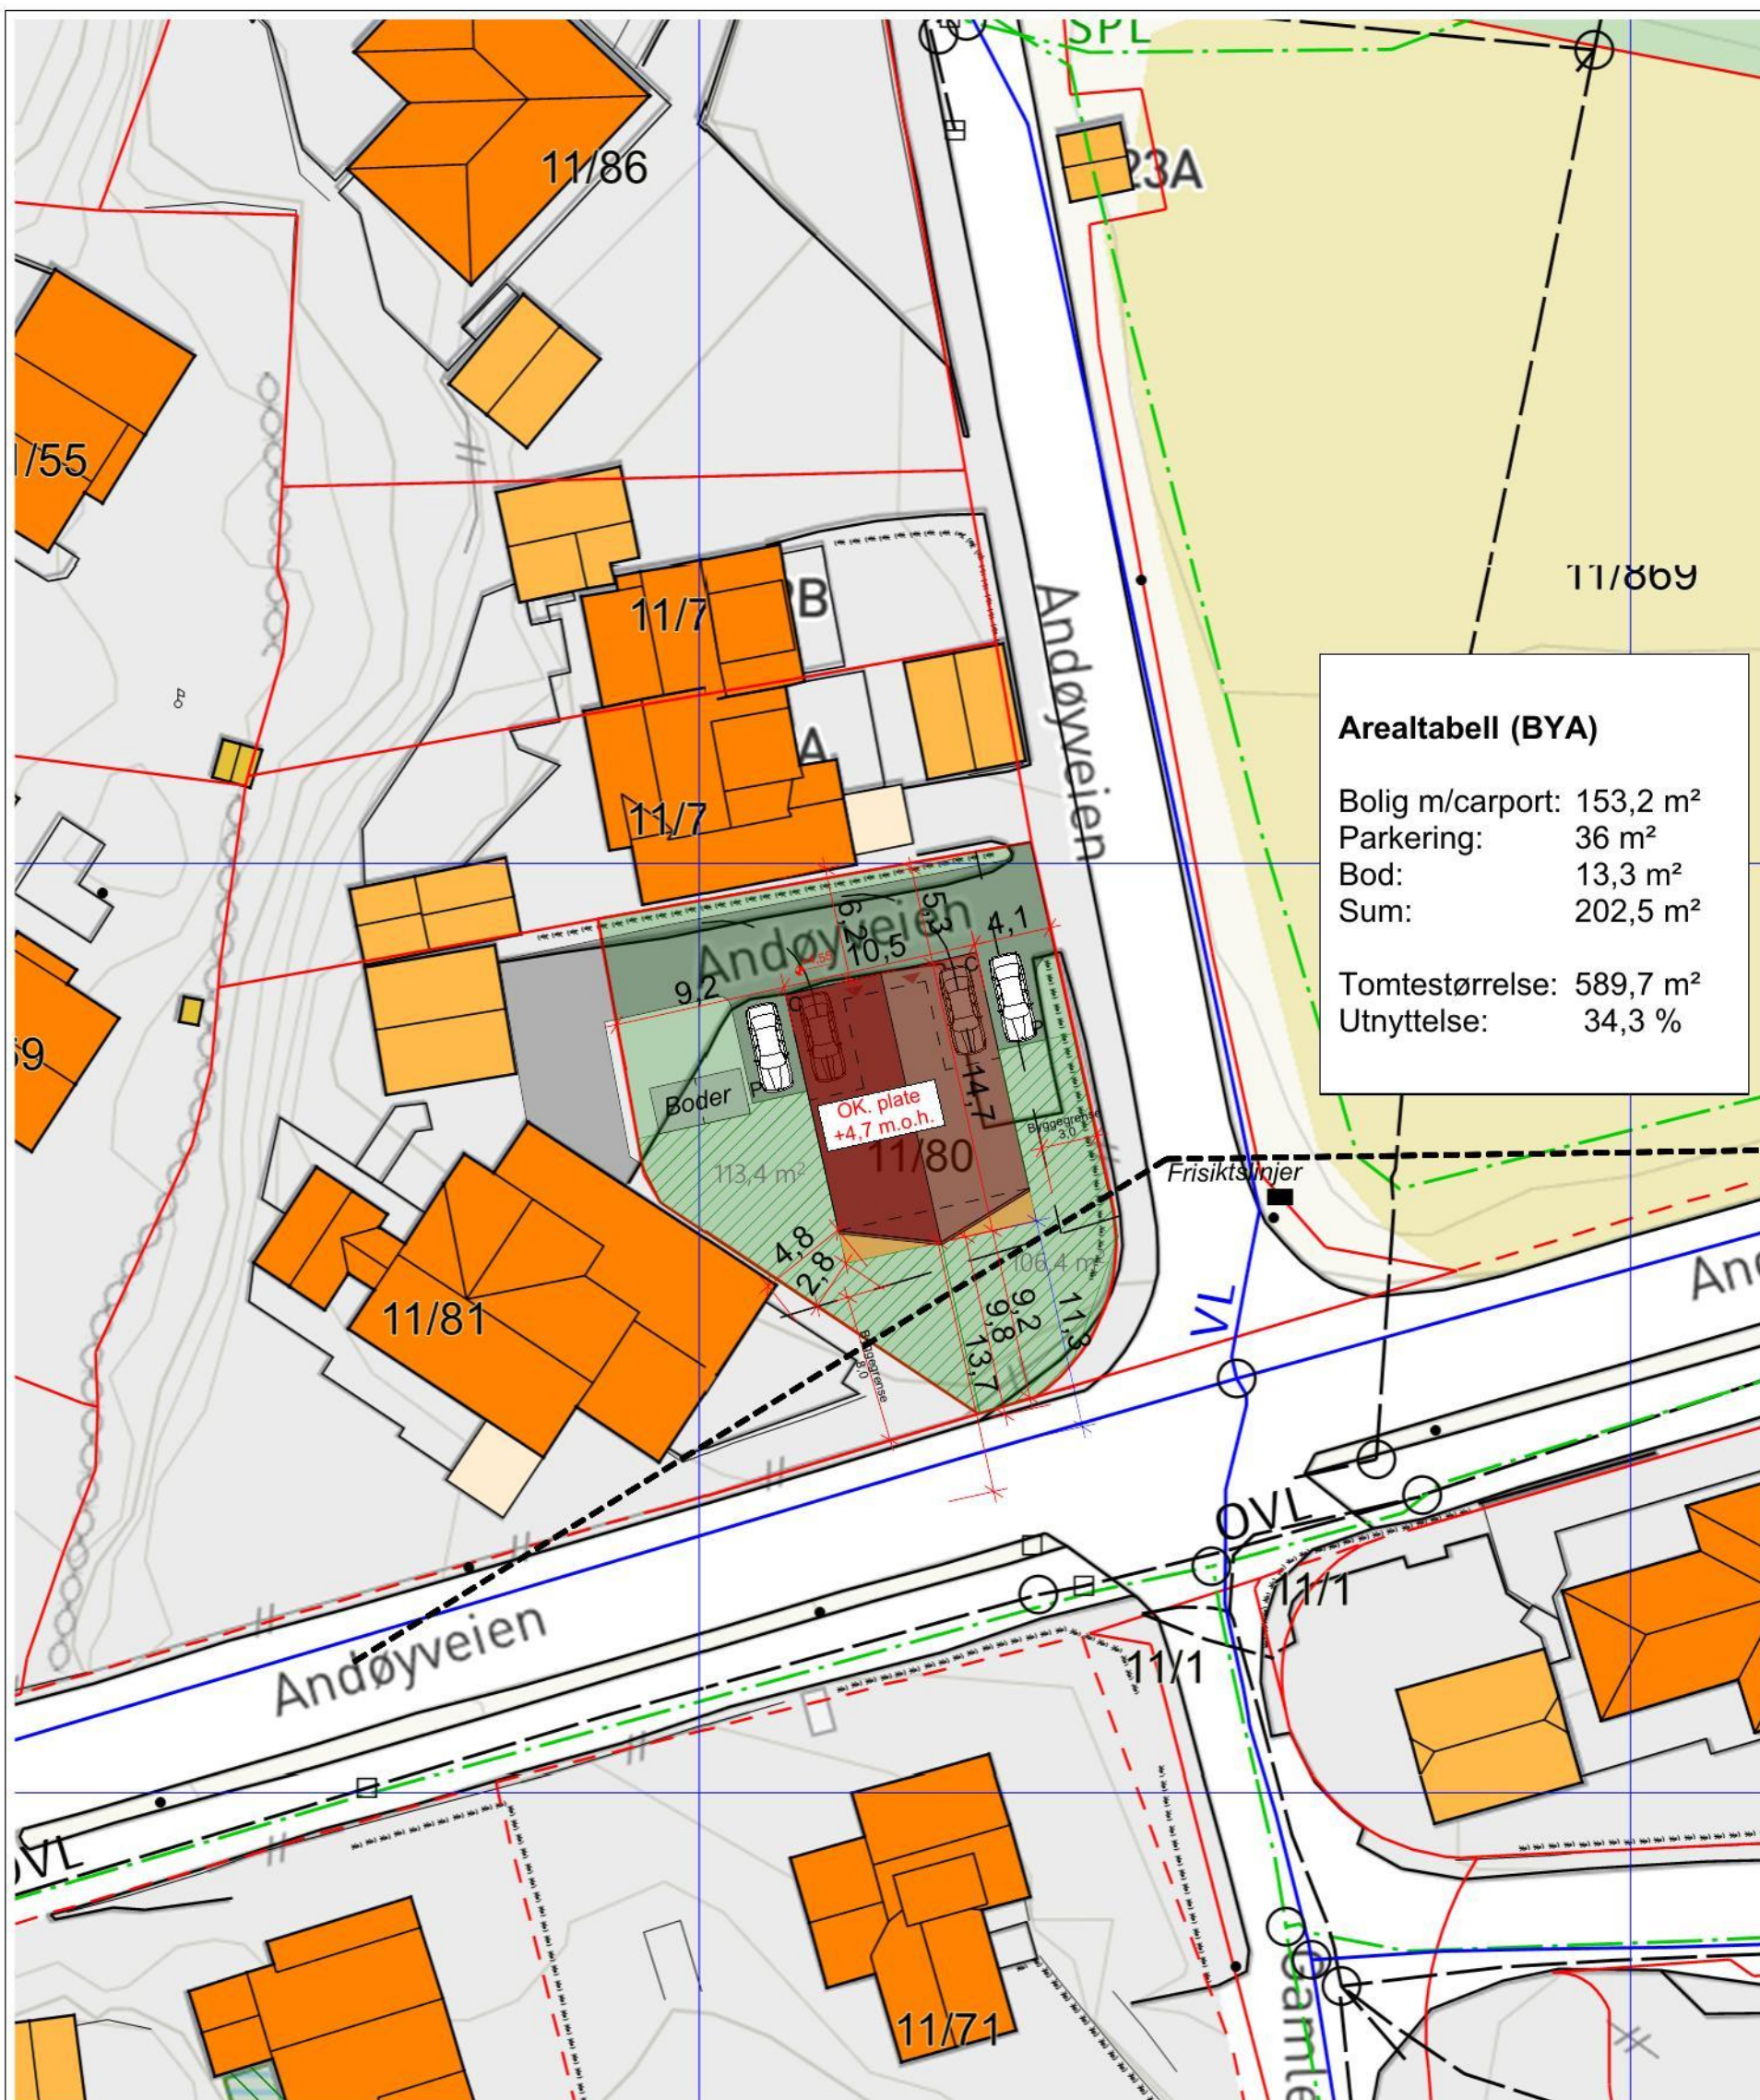

Arealtabell (BYA)	
Bolig m/carport:	153,2 m ²
Parkering:	36 m ²
Bod:	13,3 m ²
Sum:	202,5 m ²
Tomtestørrelse:	589,7 m ²
Utnyttelse:	34,3 %

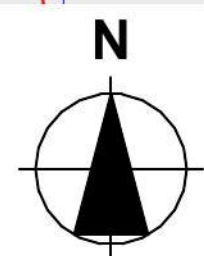

NB! Stigningsforhold og opparbeidelse av adkomst må utføres iht. forskrift

© Alle rettigheter tilhører utførende for prosjekteringen, kopiering eller bruk av disse tegningene er forbudt uten skriftlig samtykke!

SITUASJONSPLAN	TILTAKSHAVER:	MÅLESTOKK:	PROSJEKTNR.:			
	Raffinementet AS	1:500 ved A4	22874			
VÅRDAL ARKITEKTER post@vaardal.as, www.vaardal.as	BYGGEPLASS:	DATO: 12.10.23	TEGNINGSNR.:			
	Andøyveien 17	SIGN.: LJK	A10-01			
	11/80 - Kristiansand kommune	KONT.: ANP	Rev.	Sign.	Dato	Beskrivelse