


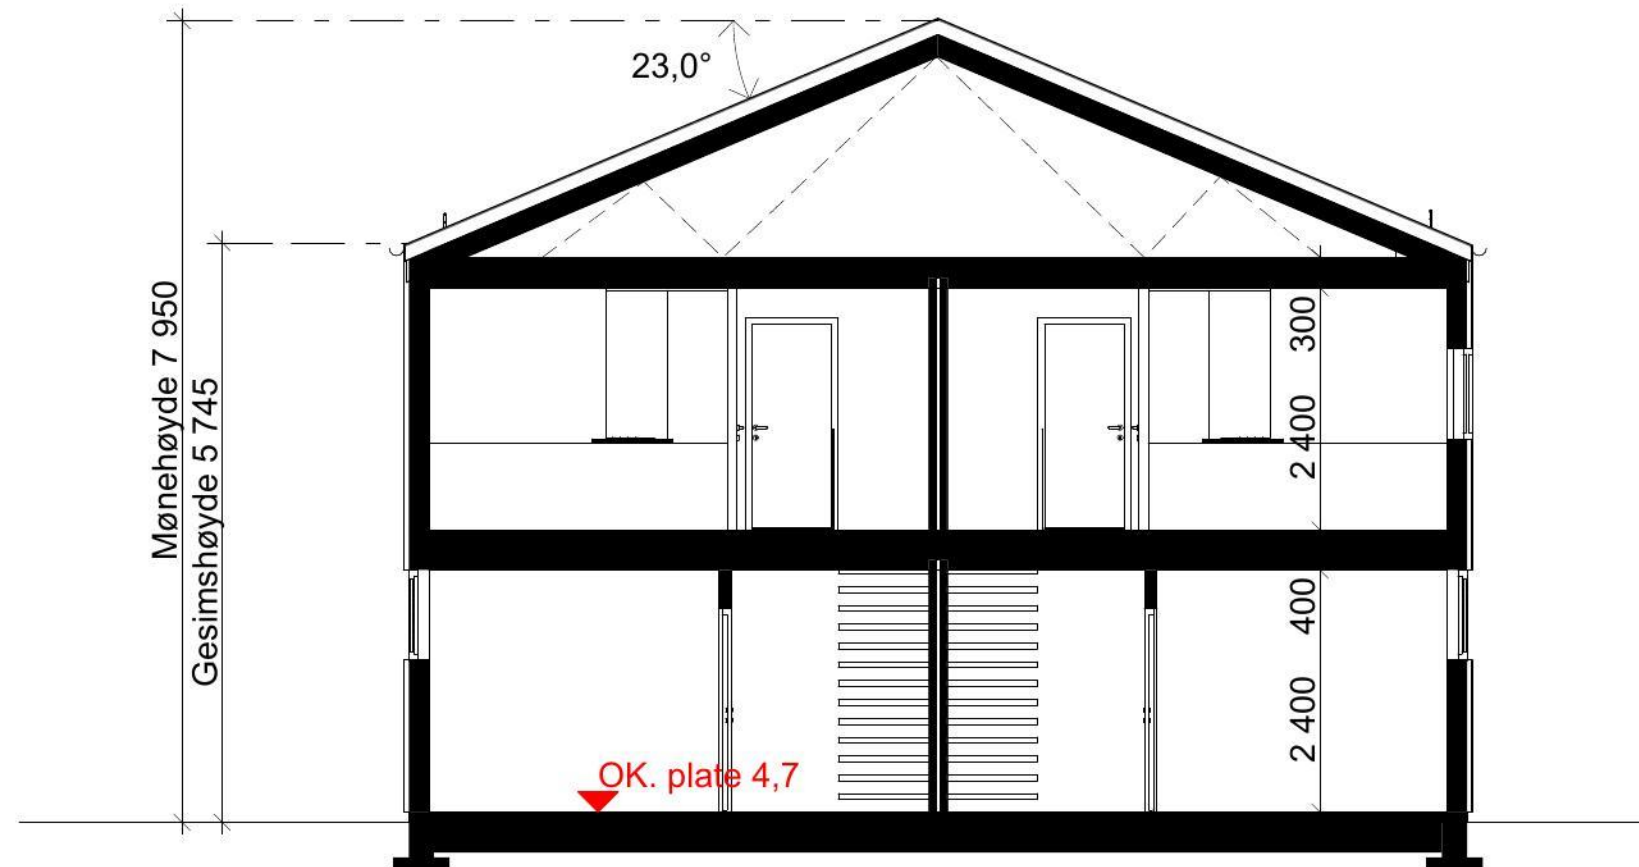

Snitt A

REVISJON:

Dato: Revisjonen gjelder: Sign.:

PROSJEKT:

Høvik

TEGNING:

Snitt A

BYGGHERRE:

Raffinementet AS

BYGGEPLASS:

Andøyveien 17, 11/80 Kristiansand

STATUS:

- ☐ Skisseprosjekt ☐ Eksisterende
☒ Forprosjekt ☐ Som bygget
☐ Detaljprosjekt ☐ Illustrasjon

 **vårdal arkitekter**
Aslyveien 19, 3170 Sem
Tlf. 33 06 10 80
post@vaardal.as

AREALTABELL	
BRA totalt:	216 m²
Leil. 1	105,8 m²
Leil. 2	105,8 m²
BYA totalt:	153,2 m²

DATO:	SIGN.:	KONT.:	MÅL.:
12.10.23	LJK	ANP	1:100
PROSJEKTNR.:		TEGningsnr.:	
22874		A30-01	