


 = Rives

 = Nybygg/endring

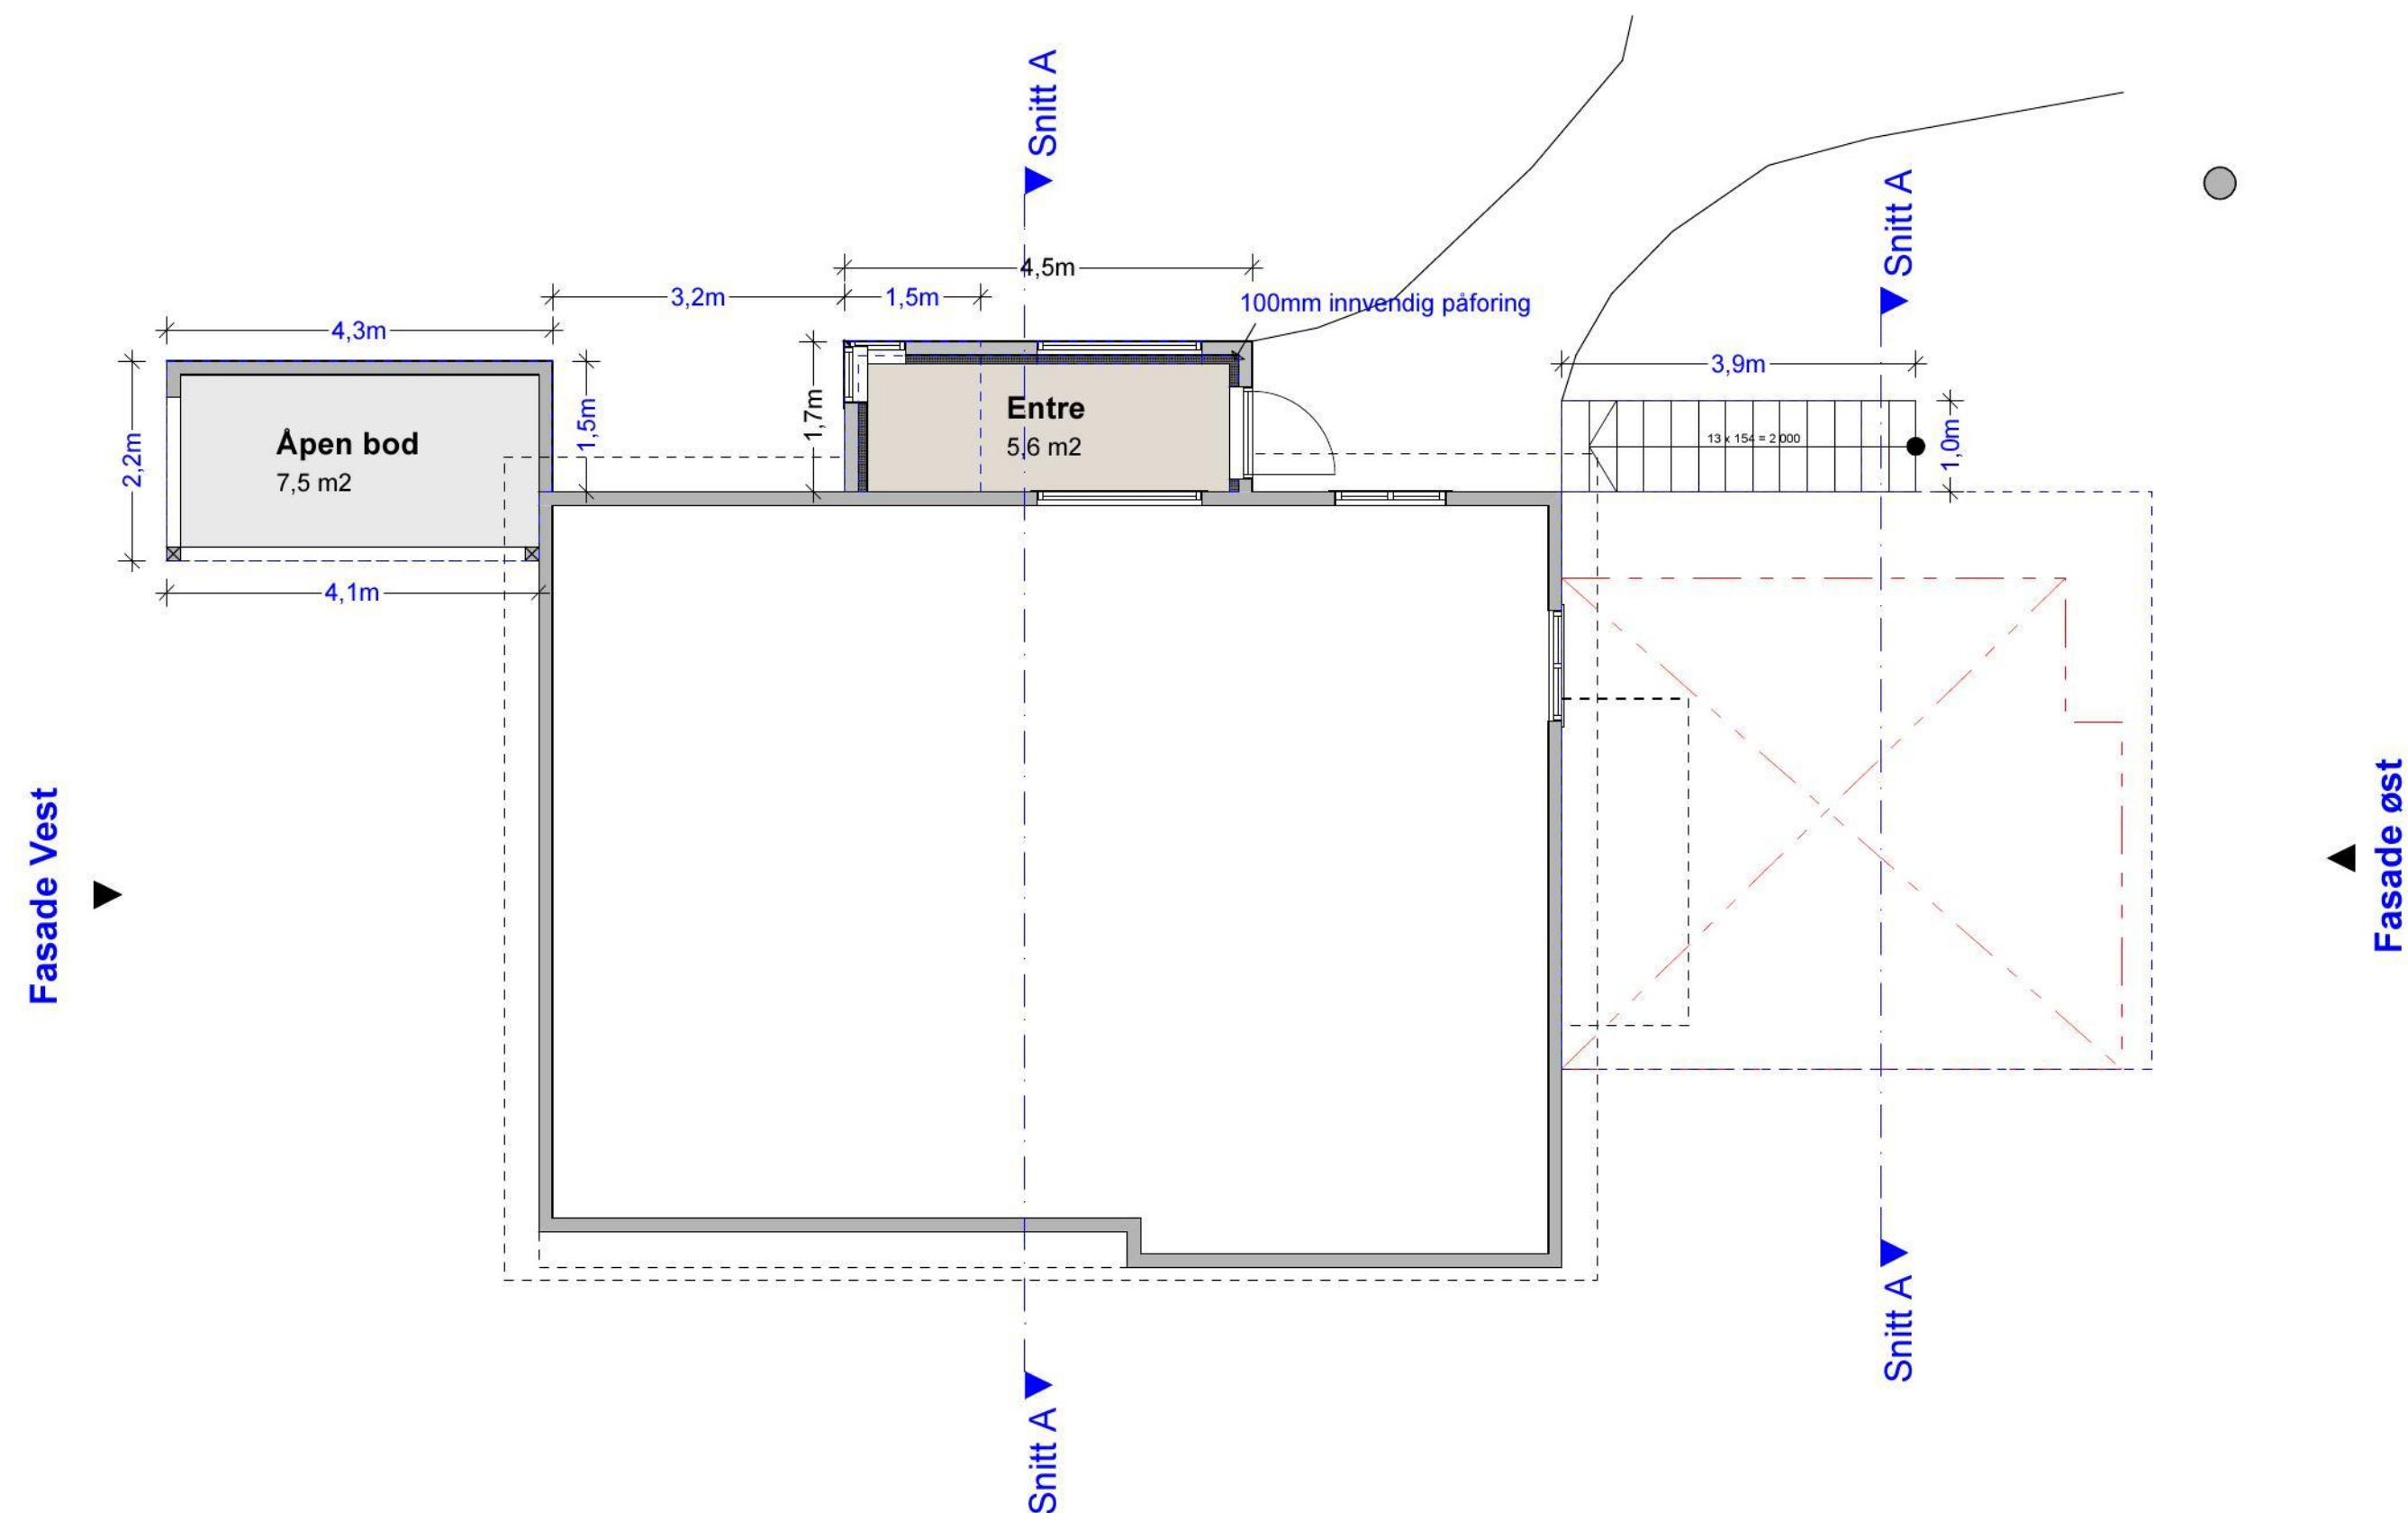

Rives:
Garasjetilbygg = 28,9 m²-BYA

Nybygg/tilbygg:
Garasjetilbygg = 39,1 m²-BYA
Åpen bod = 9,3 m²-BYA
Utv. inngang = 2,5 m²-BYA
Totalt, nybygg = 50,9 m²-BYA

Tegningsnr.: A20-2			Revisjon nr.: 3	
Type tegning: Plan 1. Etasje				
Index	Dato	Beskrivelse	Sign	Kontr.
Prosjekteringsgruppen:				
☒ ARK : Alexander Karlsen Tlf.: 97 67 46 27 E-post: alexander@krsbygg.no ☐ RIB : ☐ RIE : ☐ RIV :				
Fase:				
Byggemelding				
KRISTIANSAND BYGGRÅDGIVNING				
Tittel:			Godkjent:	
Cay-Ove Vallesverd Gnr 33 bnr 139 Kalkveien 22 4630 KRISTIANSAND			Kontroll prosjekt	
			Sign.:	Kontroll:
			AK	MN
			Filnavn: Kalkveien 22.pln	
			Dato: 02.03.2015	
			Målestokk: 1:100	
			Kontroll utførende	
Sign.:		Kontroll:		
Prosjektnr.: 20150028		Tegningsnr.: A20-2		Prosjektnr. for prosjekterende/lev
Type tegning: Plan 1. Etasje				