


- = Rives
- = Nybygg/endring

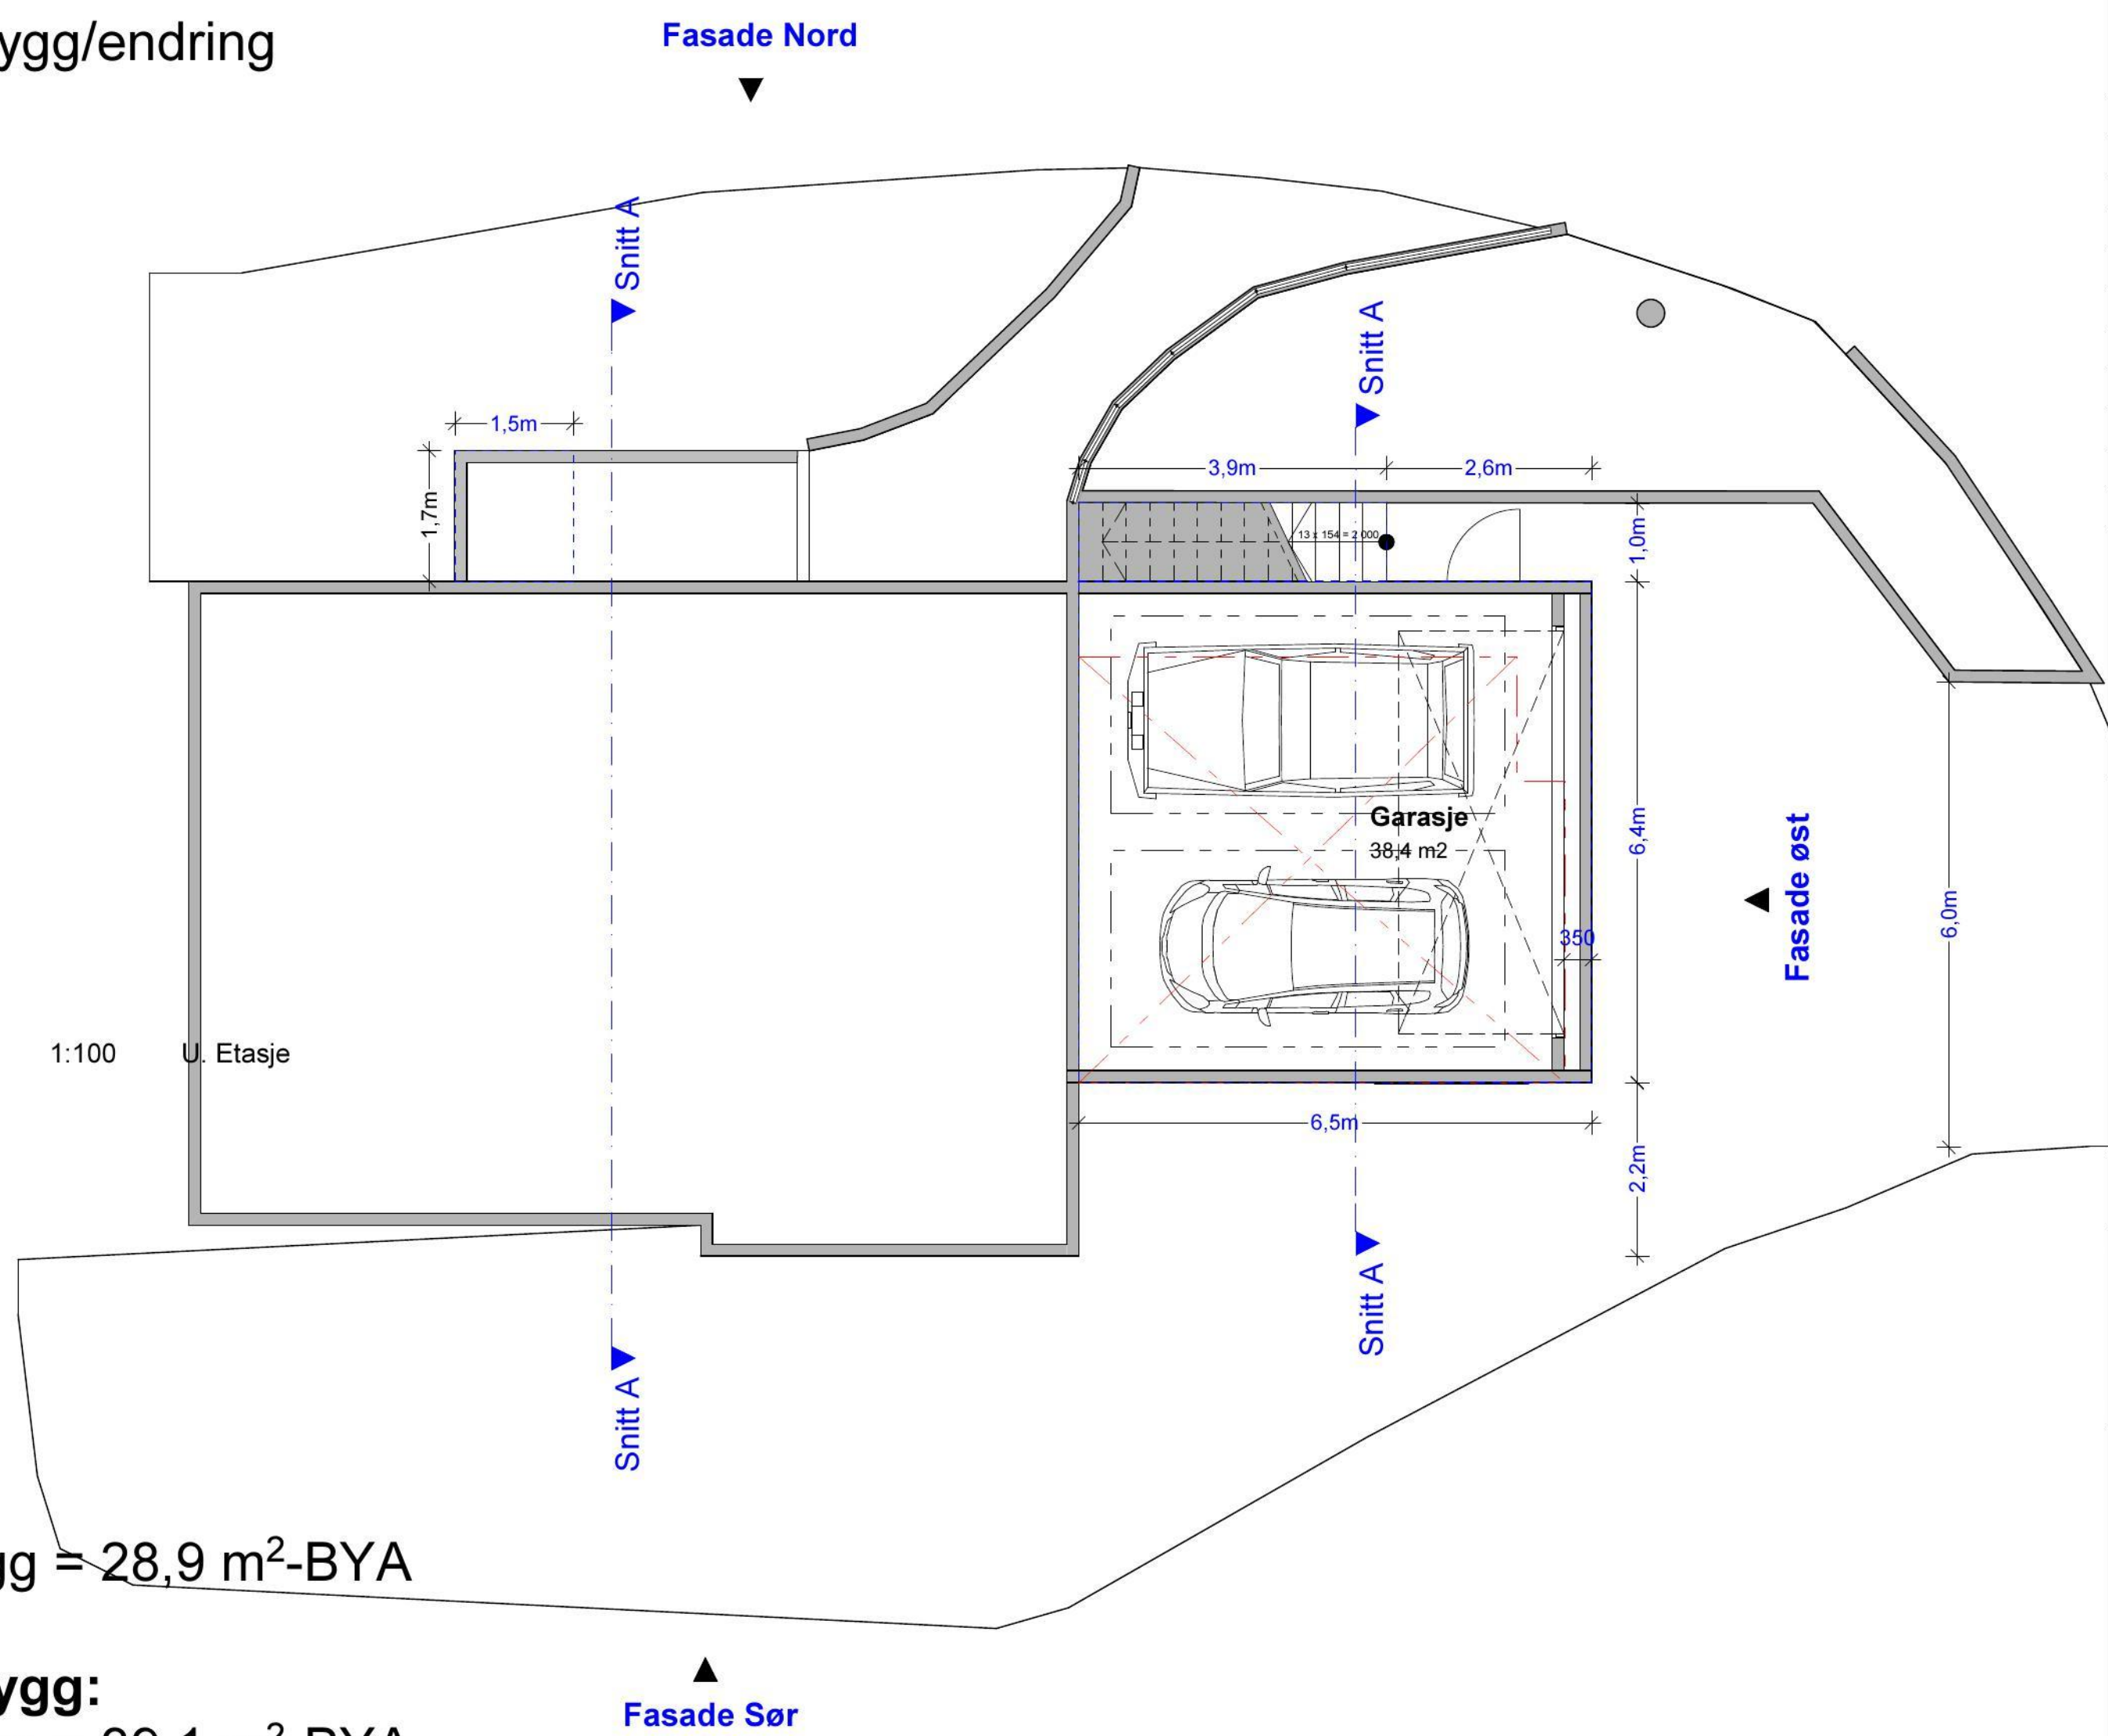

Rives:
Garasjetilbygg = 28,9 m²-BYA

Nybygg/tilbygg:
Garasjetilbygg = 39,1 m²-BYA
Åpen bod = 9,3 m²-BYA
Utv. inngang = 2,5 m²-BYA
Totalt, nybygg = 50,9 m²-BYA

Tegningsnr.: A20-3		Revisjon nr.: 3	
Type tegning: Plan U. Etasje			
Index	Dato	Beskrivelse	Sign Kontr.
Prosjekteringsgruppen:			
☒	ARK :	Alexander Karlsen	Tlf.: 97 67 46 27 E-post: alexander@krsbygg.no
☐	RJB :		
☐	RIE :		
☐	RIV :		
Fase: Byggemelding			
KRISTIANSAND BYGGRÅDGIVNING			
Tittel:		Godkjent:	
Cay-Ove Vallesverd		Kontroll prosjekt	
		Sign.:	Kontroll:
		AK	MN
		Filnavn: Kalkveien 22.pln	
Gnr 33 bnr 139		Dato: 02.03.2015	
Kalkveien 22		Målestokk: 1:100	
4630 KRISTIANSAND		Kontroll utførende	
		Sign.:	Kontroll:
Prosjektnr.: 20150028		Tegningsnr.: A20-3	Prosjektnr. for prosjekterende/lev
Type tegning: Plan U. Etasje			