




Sandnes kommune

Situasjonsplan

Eiendom: 100/44
Adresse: Kleivadalveien 252
Dato: 12.10.2023
Målestokk: 1:500



UTM-32

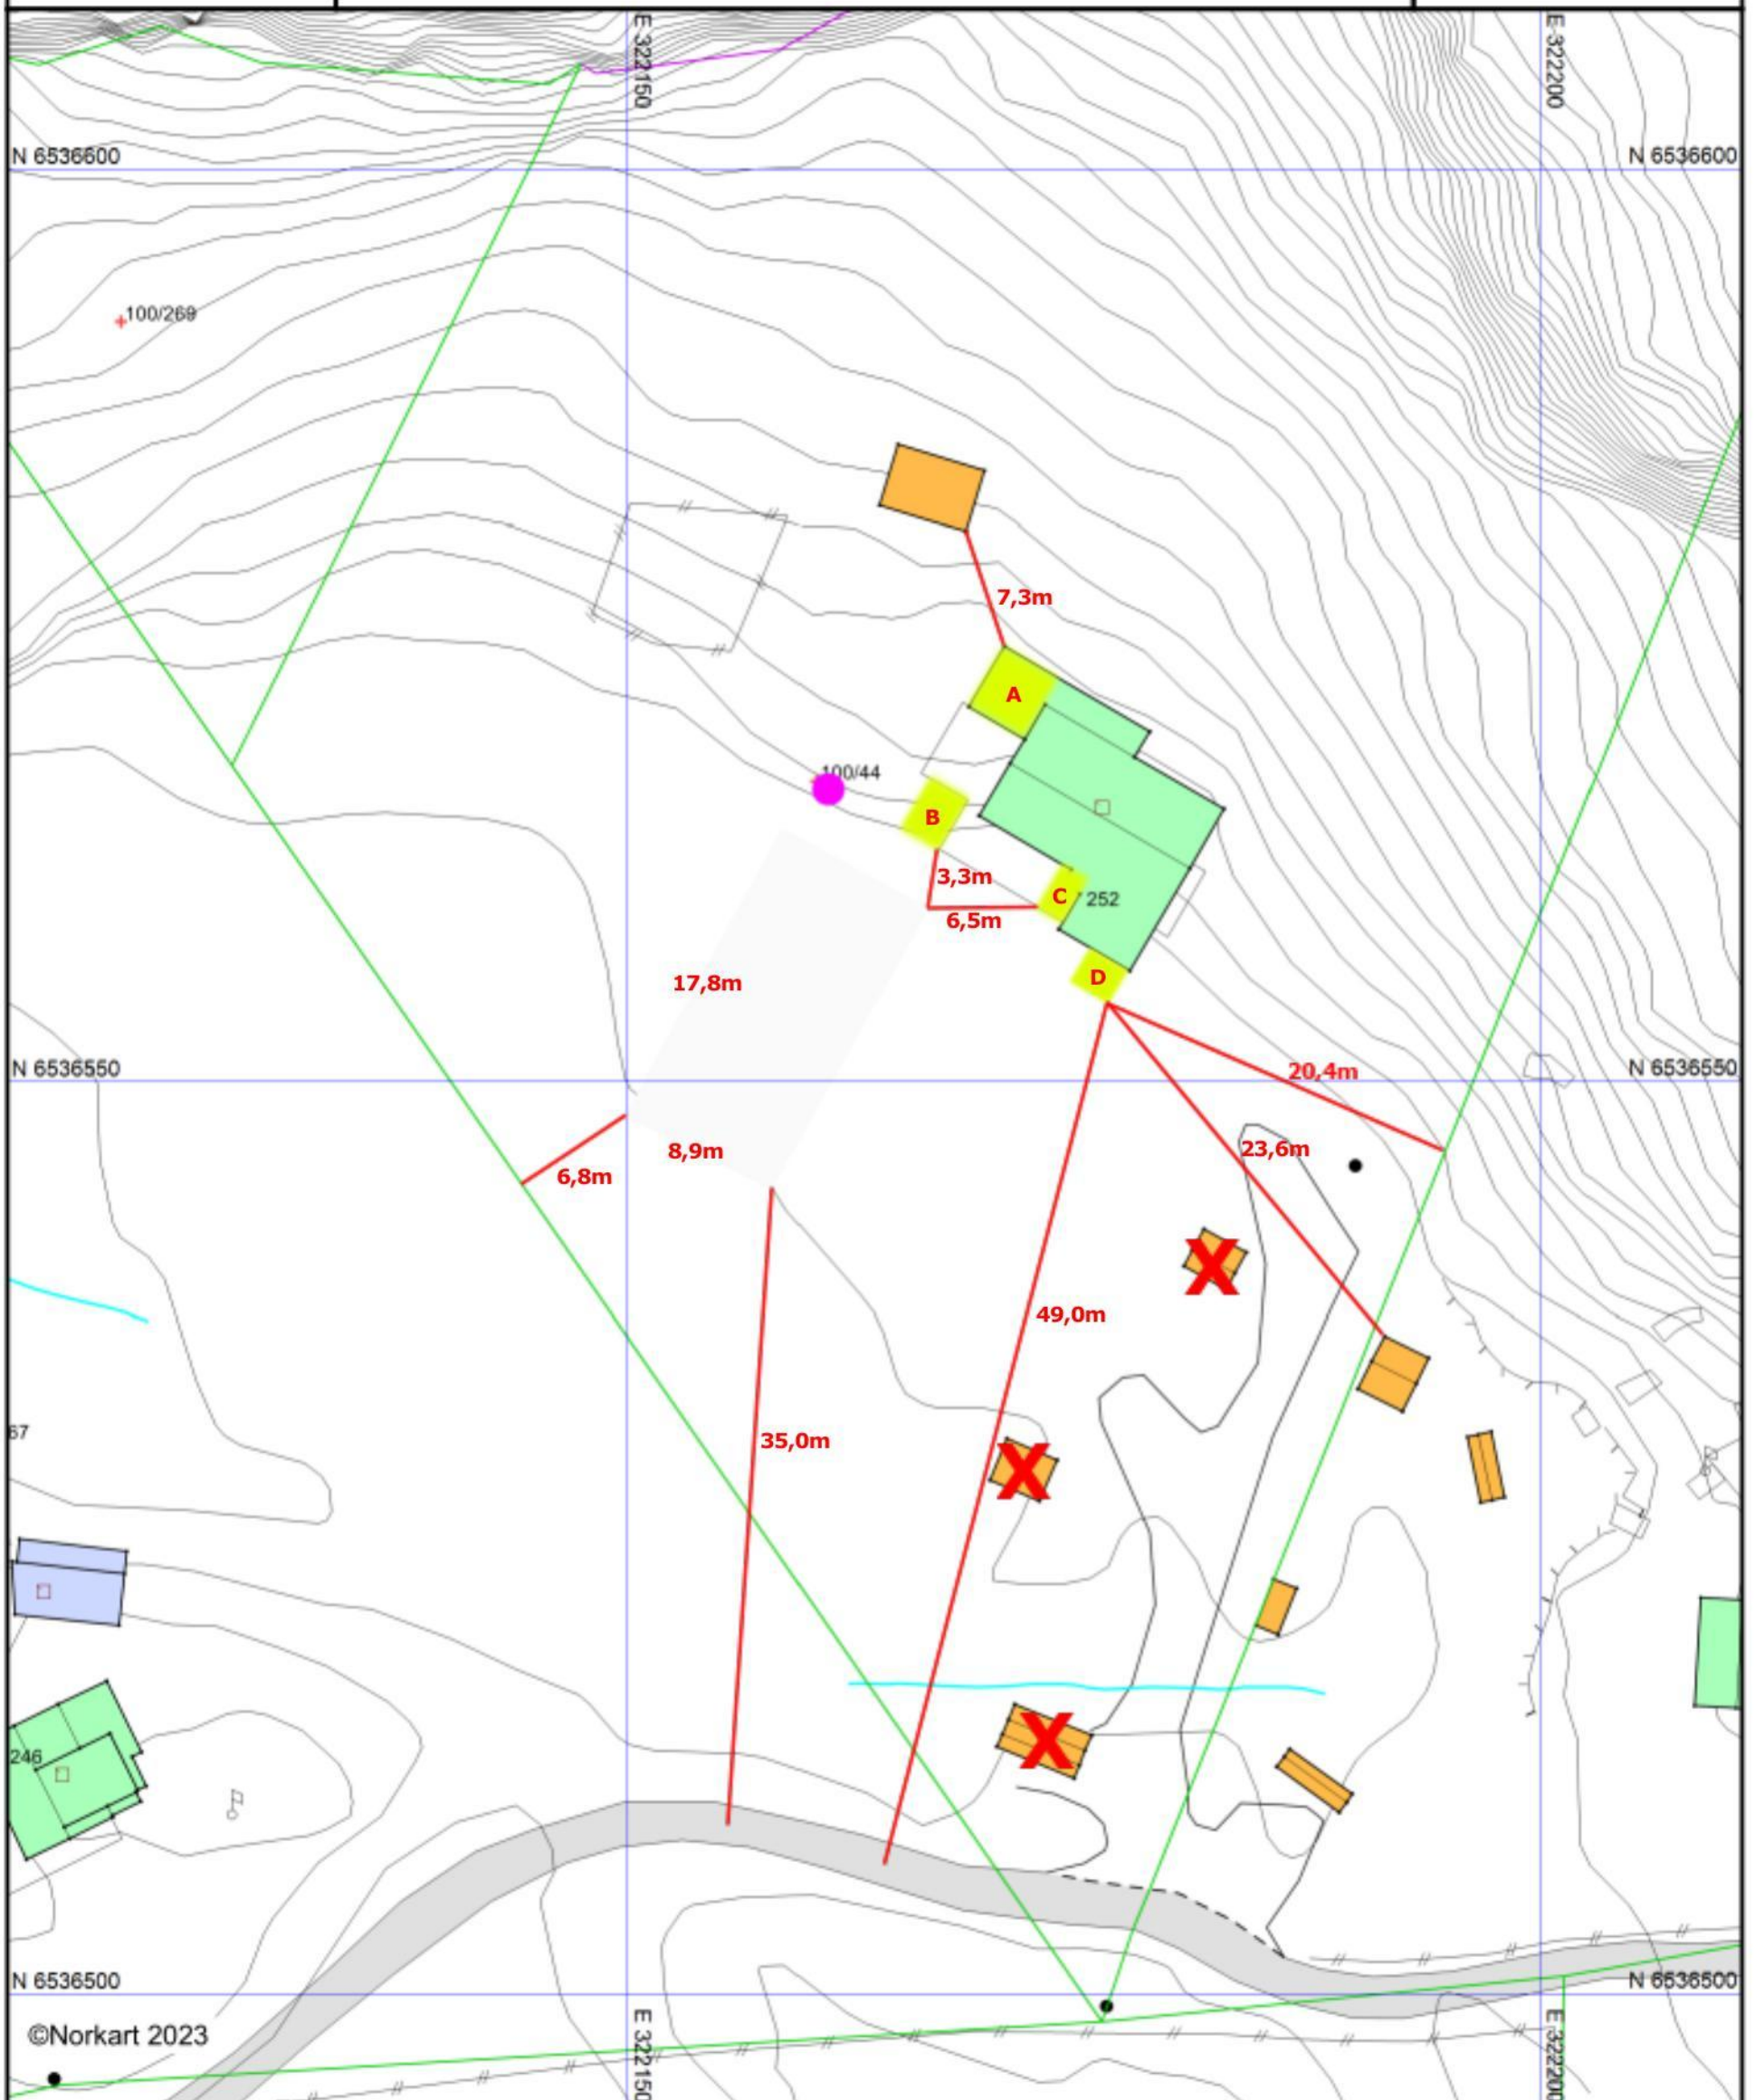

©Norkart 2023

- 1) Det tas forbehold om feil i kartgrunnlaget
- 2) Ved utskrift fra PDF-fil kan målestokken bli unøyaktig