


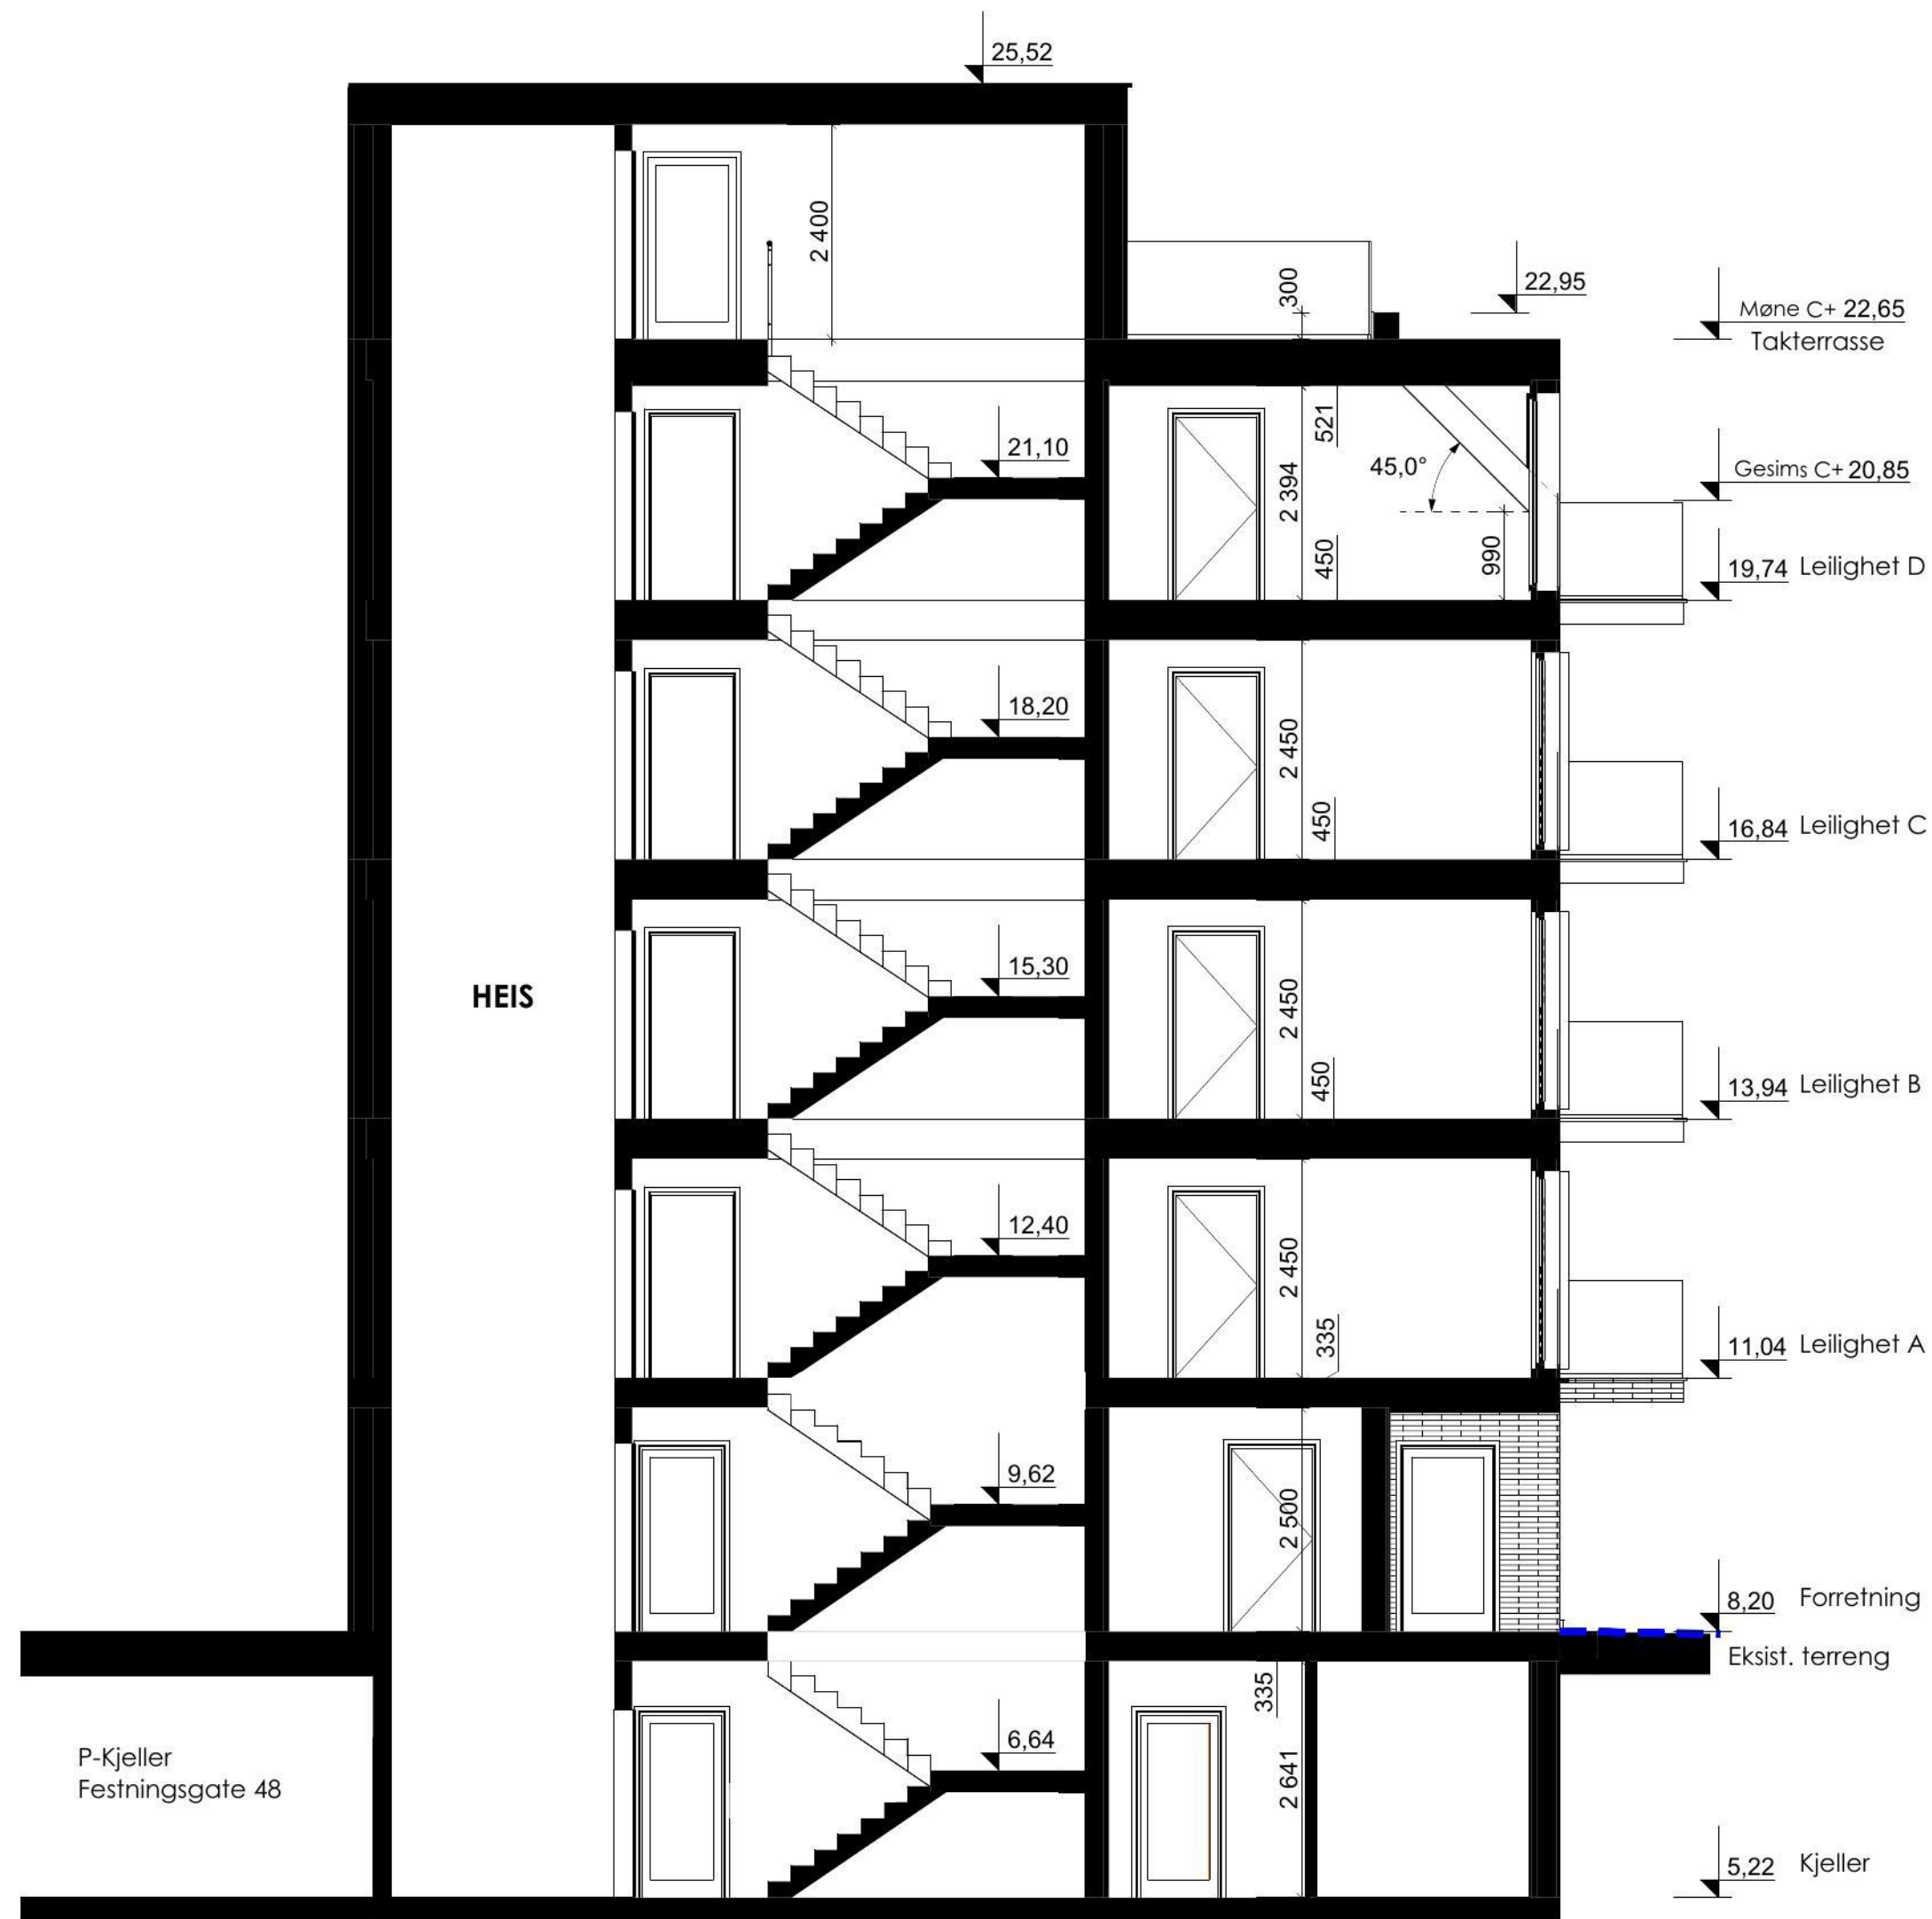



SPISS

ARKITEKTUR & PLAN AS

SPISS Arkitektur & Plan AS

Vestre Strandgate 26

Telefon: 4177 8000

Postboks 151

Mail: post@spissark.no

4662 Kristiansand

Prosjekt:

Kristian IVs gate 68

4614 KRISTIANSAND S

Gnr. / Bnr.: 150/812

Tegnet

TW

Arkitekt

SEB / TW

Ark

A3

ProsjektNr..

2344

Dato Opprettet

03.07.2023

Målestokk

1:100

Oppdragsgiver:

Chr Iv Gate Holding AS

Tegningsnr.:

A30-1

Tegnings Tittel:

Snitt A-A

| Rev.