


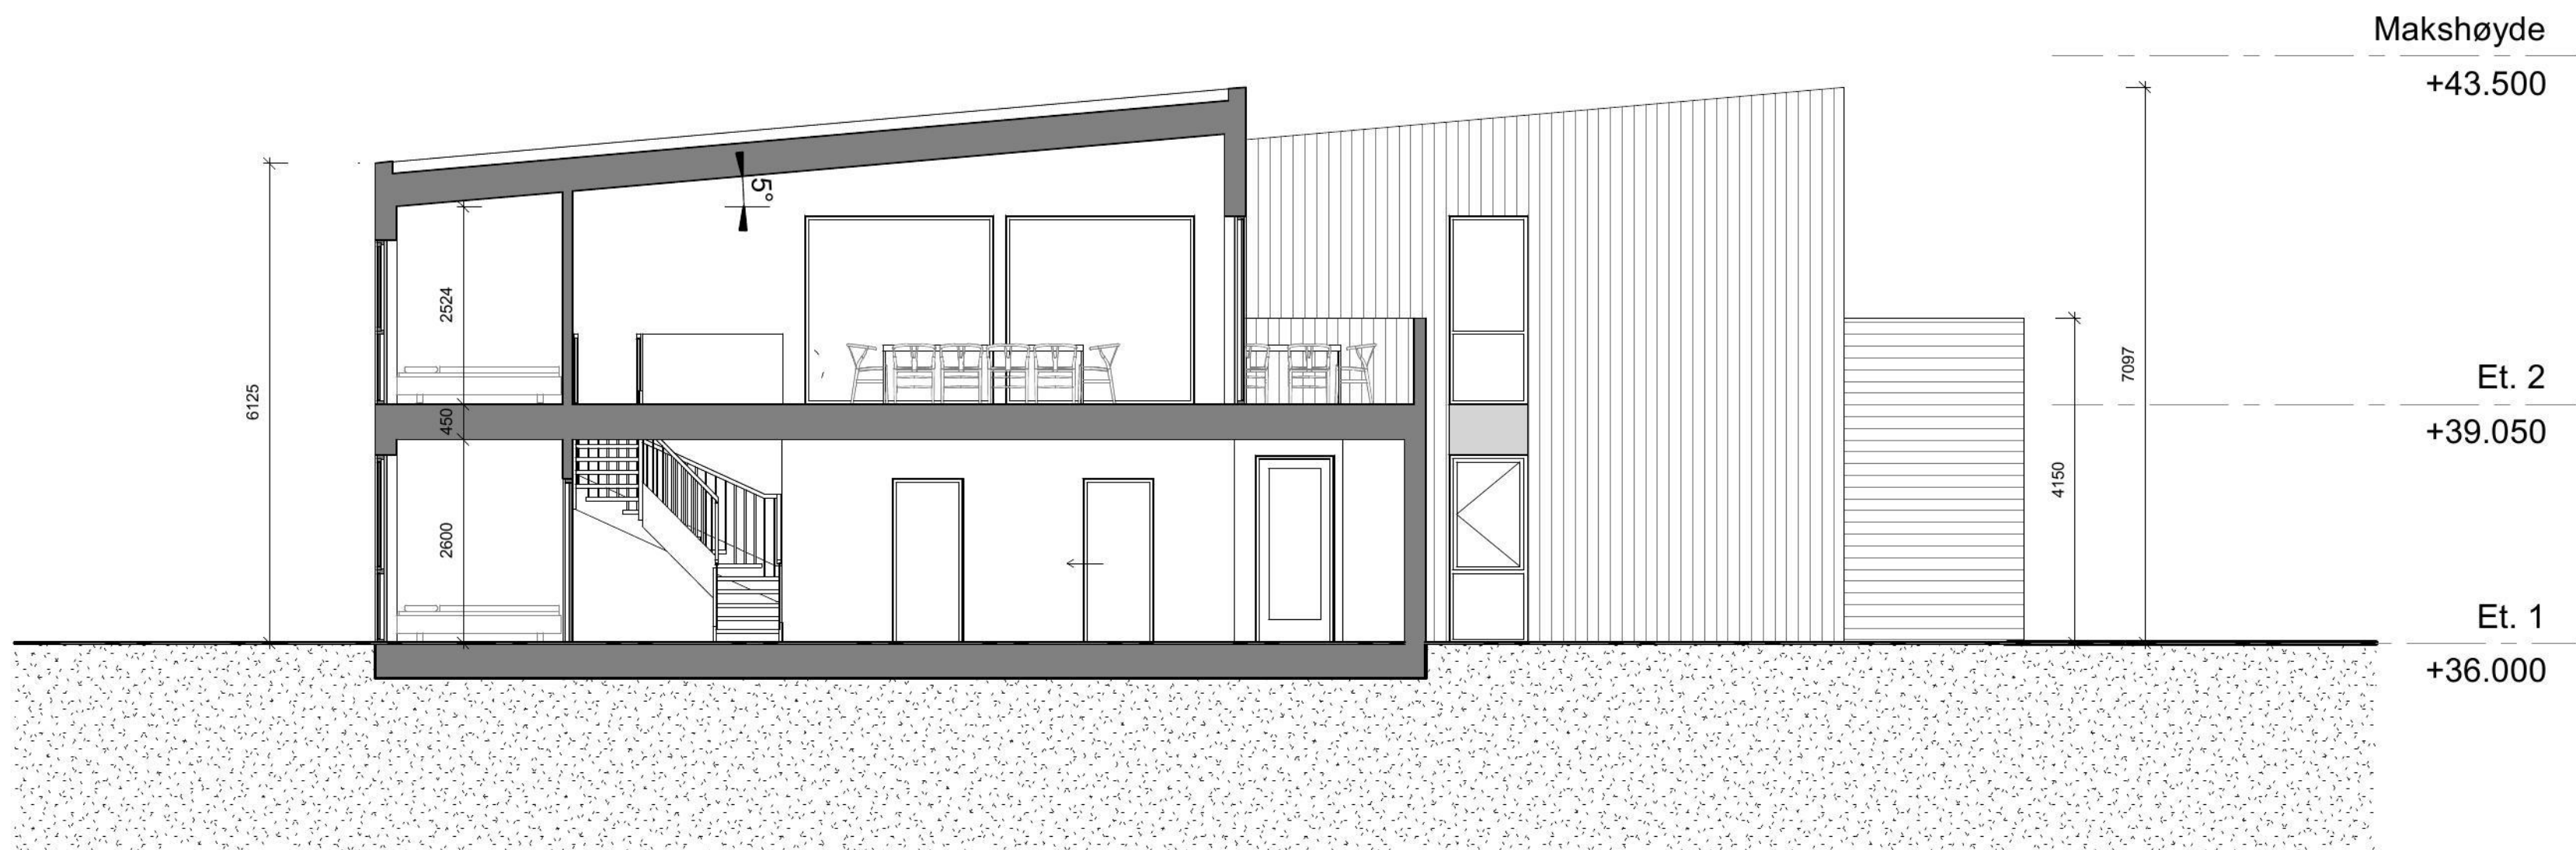

REV	ENDRINGER			DATO	UTF. KTR.		
LANGETJØNNTOPPEN 25-31				SEIL ARKITEKTER			
NIVÅ SØKNADSTEGNING		TEGN NR: A-41.01				REV.	
TEGNING SNITT Rekkehus		MÅL: 1 : 100				TEGN: JES ARK: A3	
		DATO: 27.06.2023				ANSV: KONTR: JJV	