
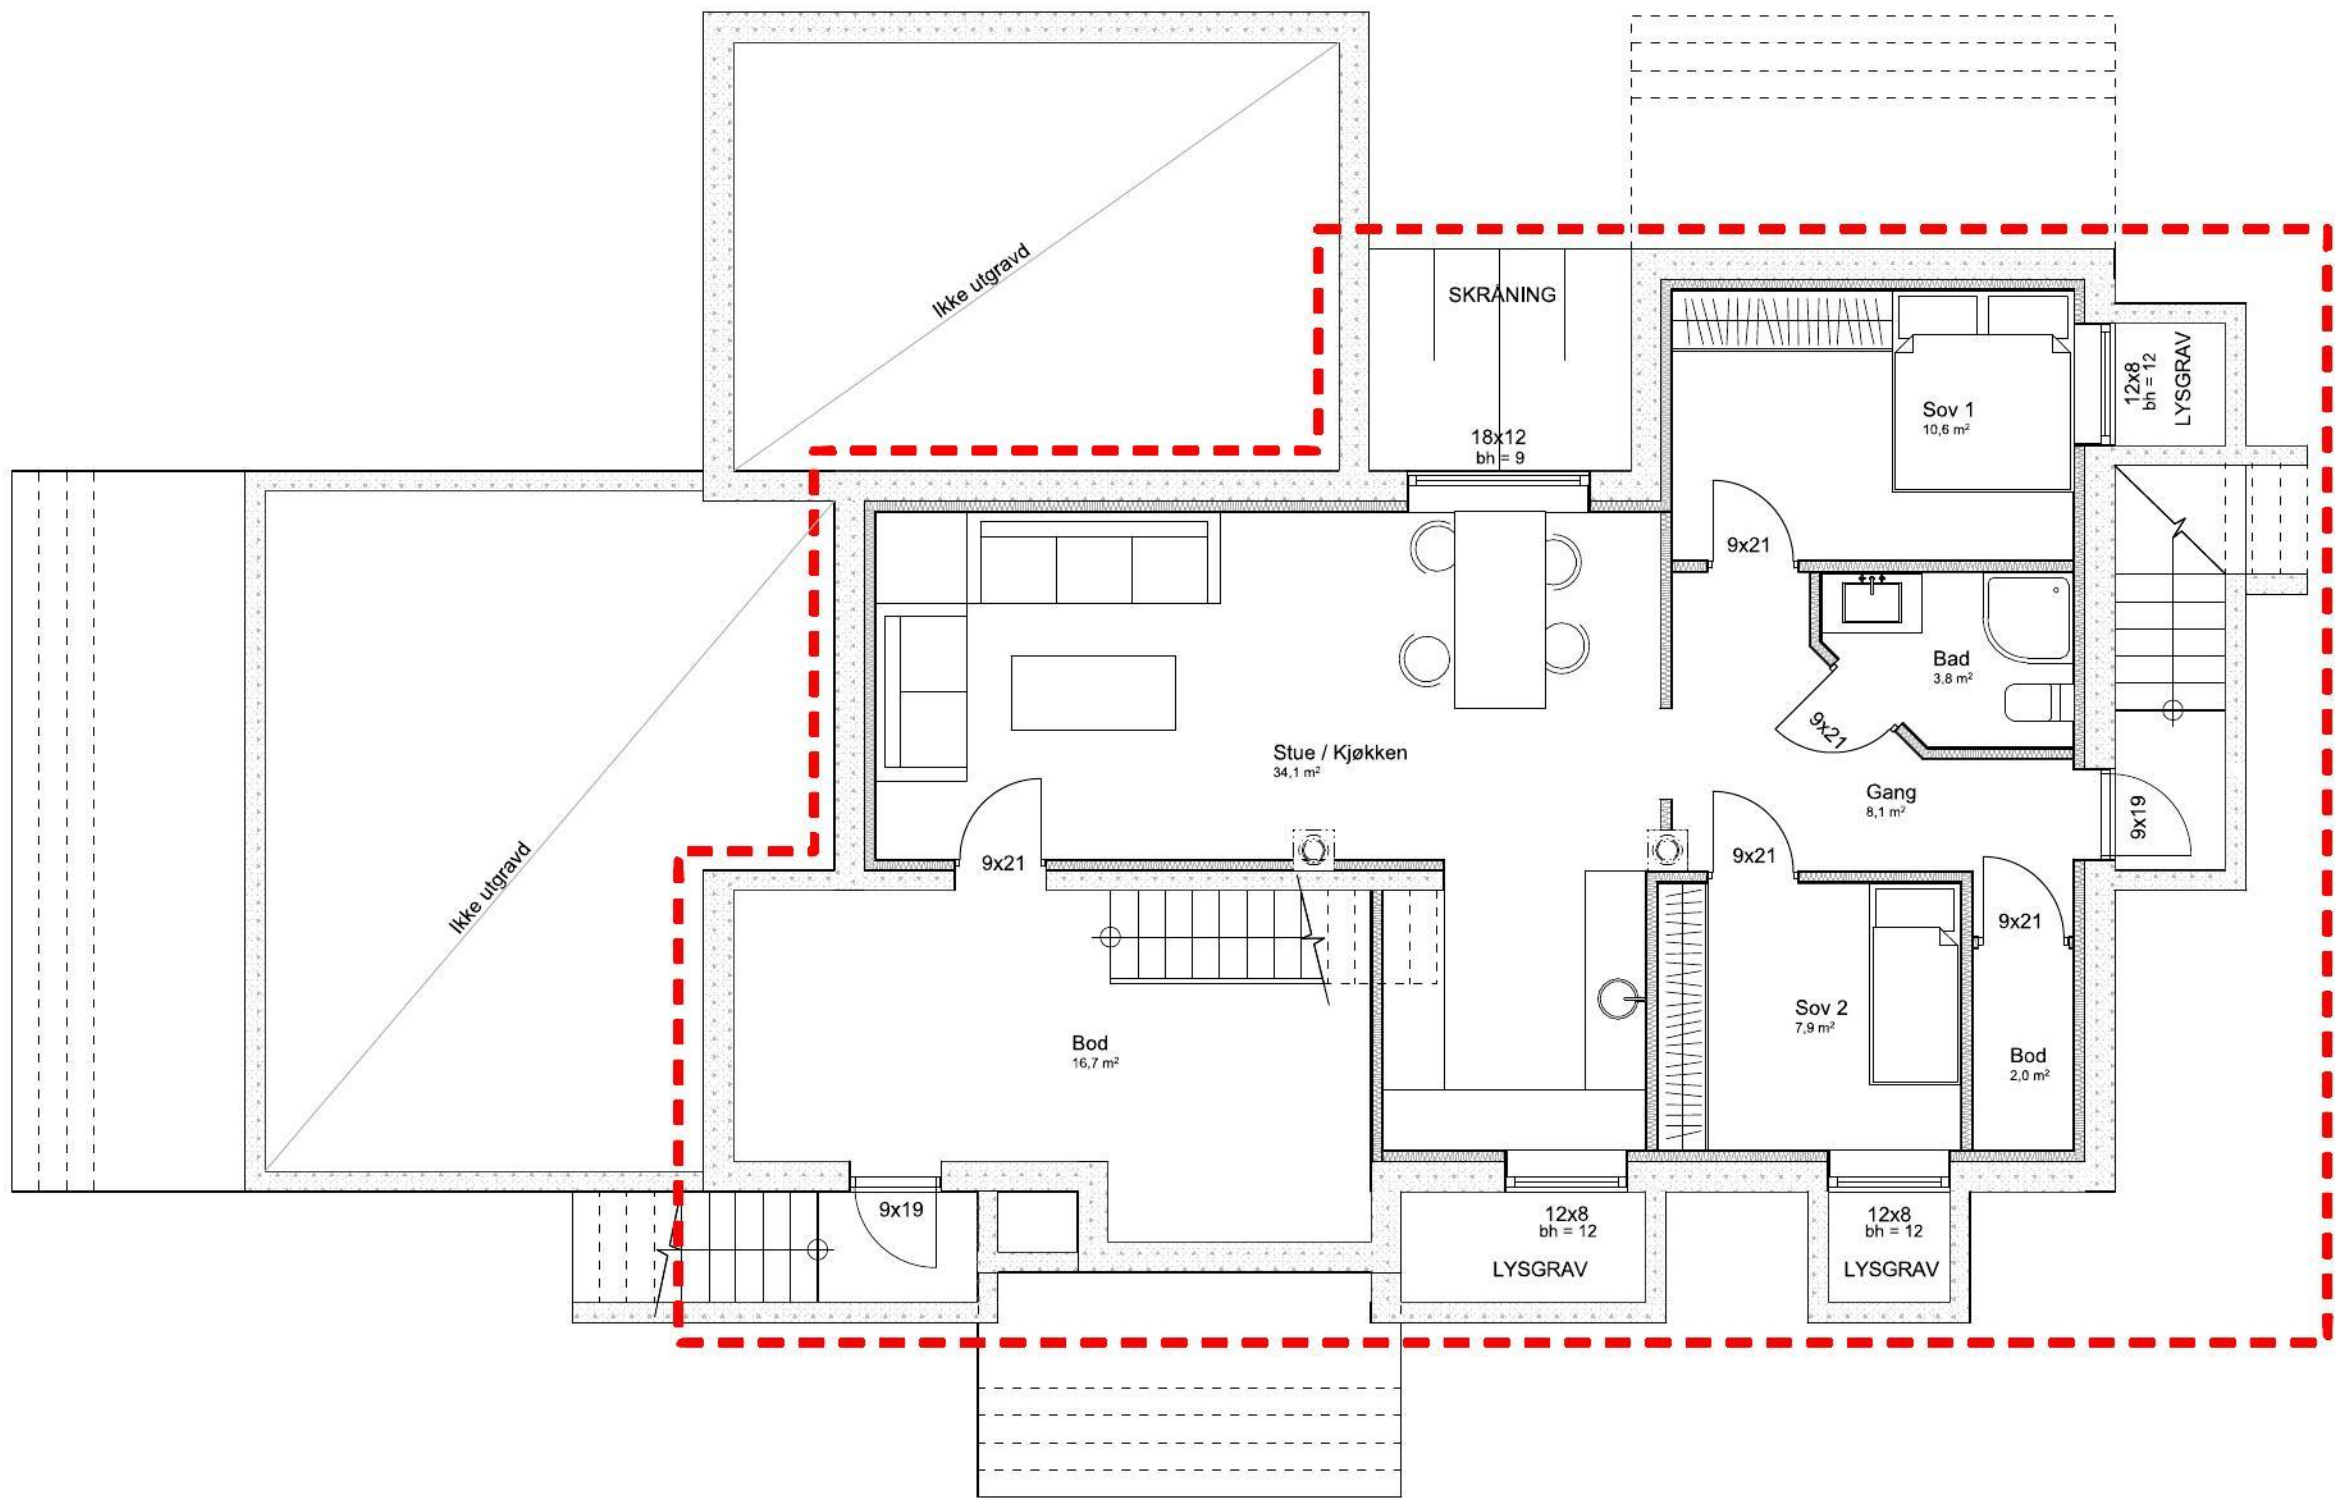


 

Arealer (BYA)		Arealer (BRA)			
BYA Eksiterende	204,0 m²		Eksist.	Nytt	SUM
Ny hagestue	12,3 m²				
Ny terrasse	58,7 m²	2. etasje	155,5 m²		155,5 m²
SUM bolig (BYA)	275 m²	1. etasje	185,0 m²		185,0 m²
SUM (BYA 25%)	26,55 %	Kjeller	91 m²		91 m²
		1. etasje (Ny hagestue)		11,2 m²	11,2 m²
BYA Eksiterende Garasje	37,0 m²	SUM bolig (BRA)	431,5 m²		442,7 m²
BYA Ny Garasje	49,2 m²				
Netto tomteareal	1035,6 m²	1. etasje (Garasje)	35,8 m²	8,5 m²	44,3 m²

BYGGE MELDING	Byggherre : OVE NORVALD STAVØ			
	Byggeplass : LERKEVEIEN 12, Lura Sandnes kommune			
	Tegner :	G.nr. :	69	B.nr. : 493
	Ark. :	Prosjektnr. :		
	Målestokk :	Tegning :	Plan kjeller	
	Dato :	Tegningsnr. :	101	Rev. :
			28.09.2021	