


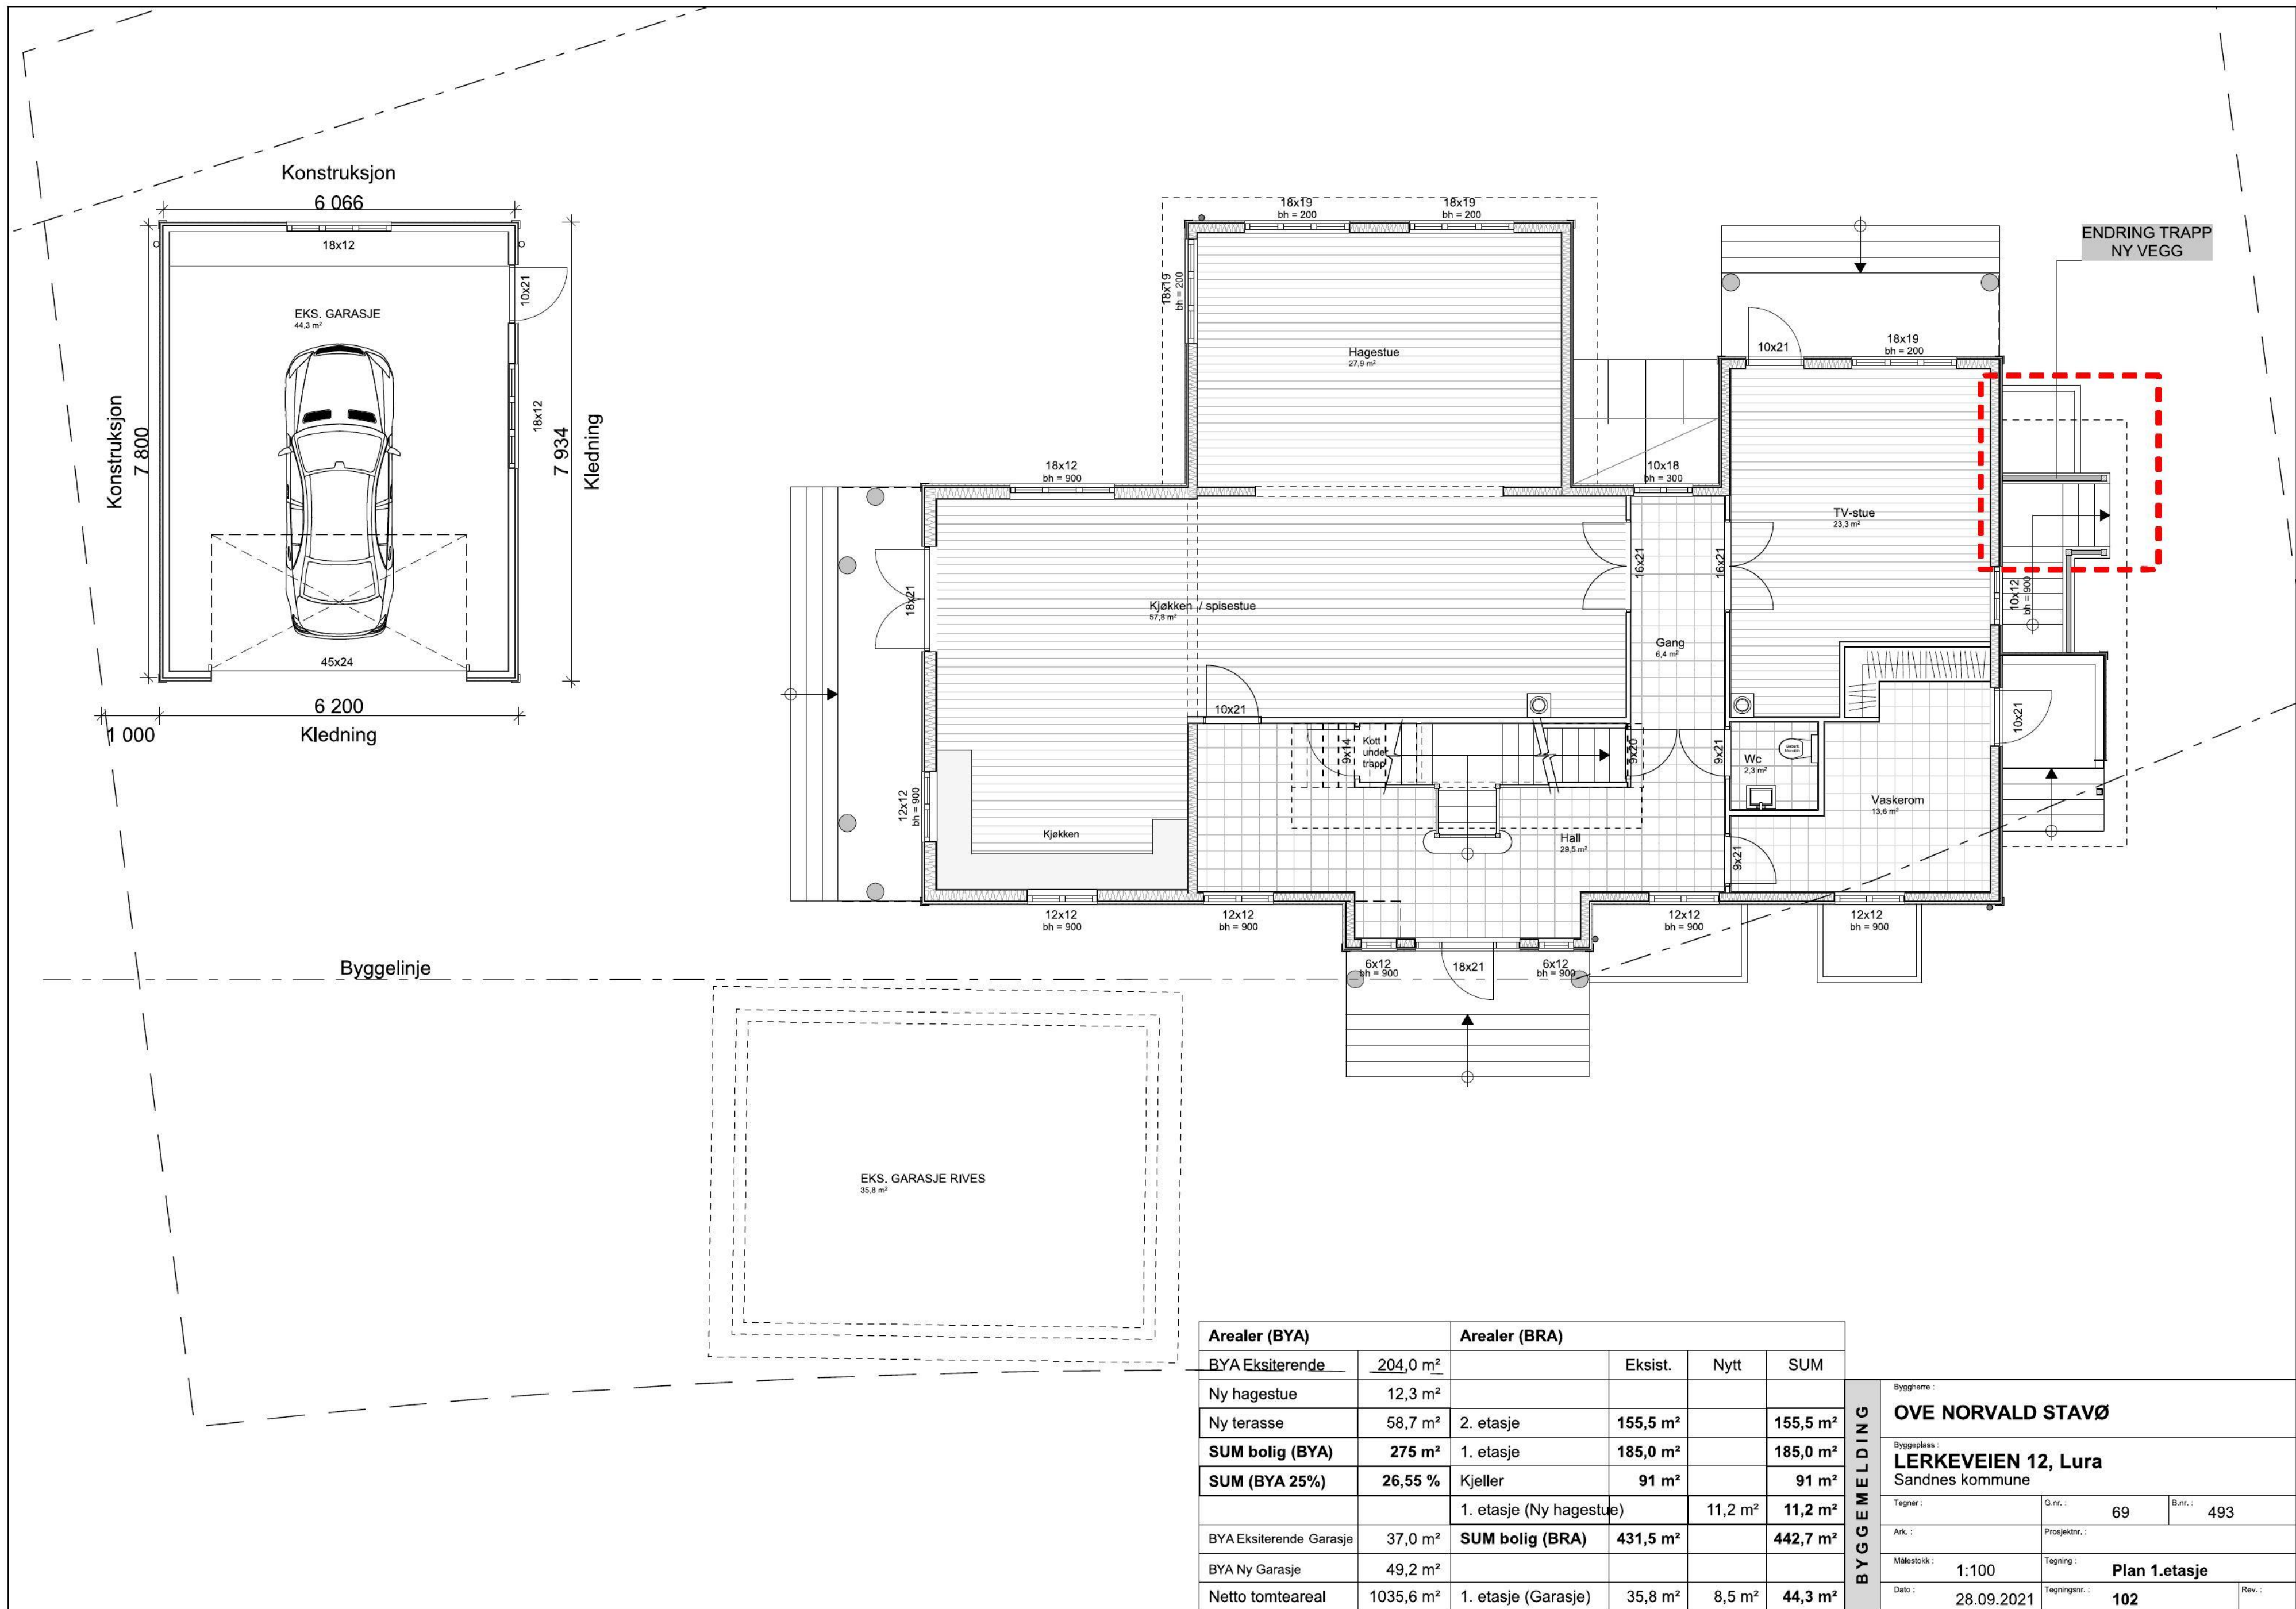

Arealer (BYA)		Arealer (BRA)			
BYA Eksisterende	204,0 m²		Eksist.	Nytt	SUM
Ny hagestue	12,3 m²				
Ny terrasse	58,7 m²	2. etasje	155,5 m²		155,5 m²
SUM bolig (BYA)	275 m²	1. etasje	185,0 m²		185,0 m²
SUM (BYA 25%)	26,55 %	Kjeller	91 m²		91 m²
		1. etasje (Ny hagestue)		11,2 m²	11,2 m²
BYA Eksisterende Garasje	37,0 m²	SUM bolig (BRA)	431,5 m²		442,7 m²
BYA Ny Garasje	49,2 m²				
Netto tomteareal	1035,6 m²	1. etasje (Garasje)	35,8 m²	8,5 m²	44,3 m²

Byggherre: OVE NORVALD STAVØ			
Byggeplass: LERKEVEIEN 12, Lura Sandnes kommune			
Tegner:	G.nr.: 69	B.nr.: 493	
Ark.:	Prosjektnr.:		
Målestokk: 1:100	Tegning: Plan 1.etasje		
Dato: 28.09.2021	Tegningsnr.: 102		Rev.: