



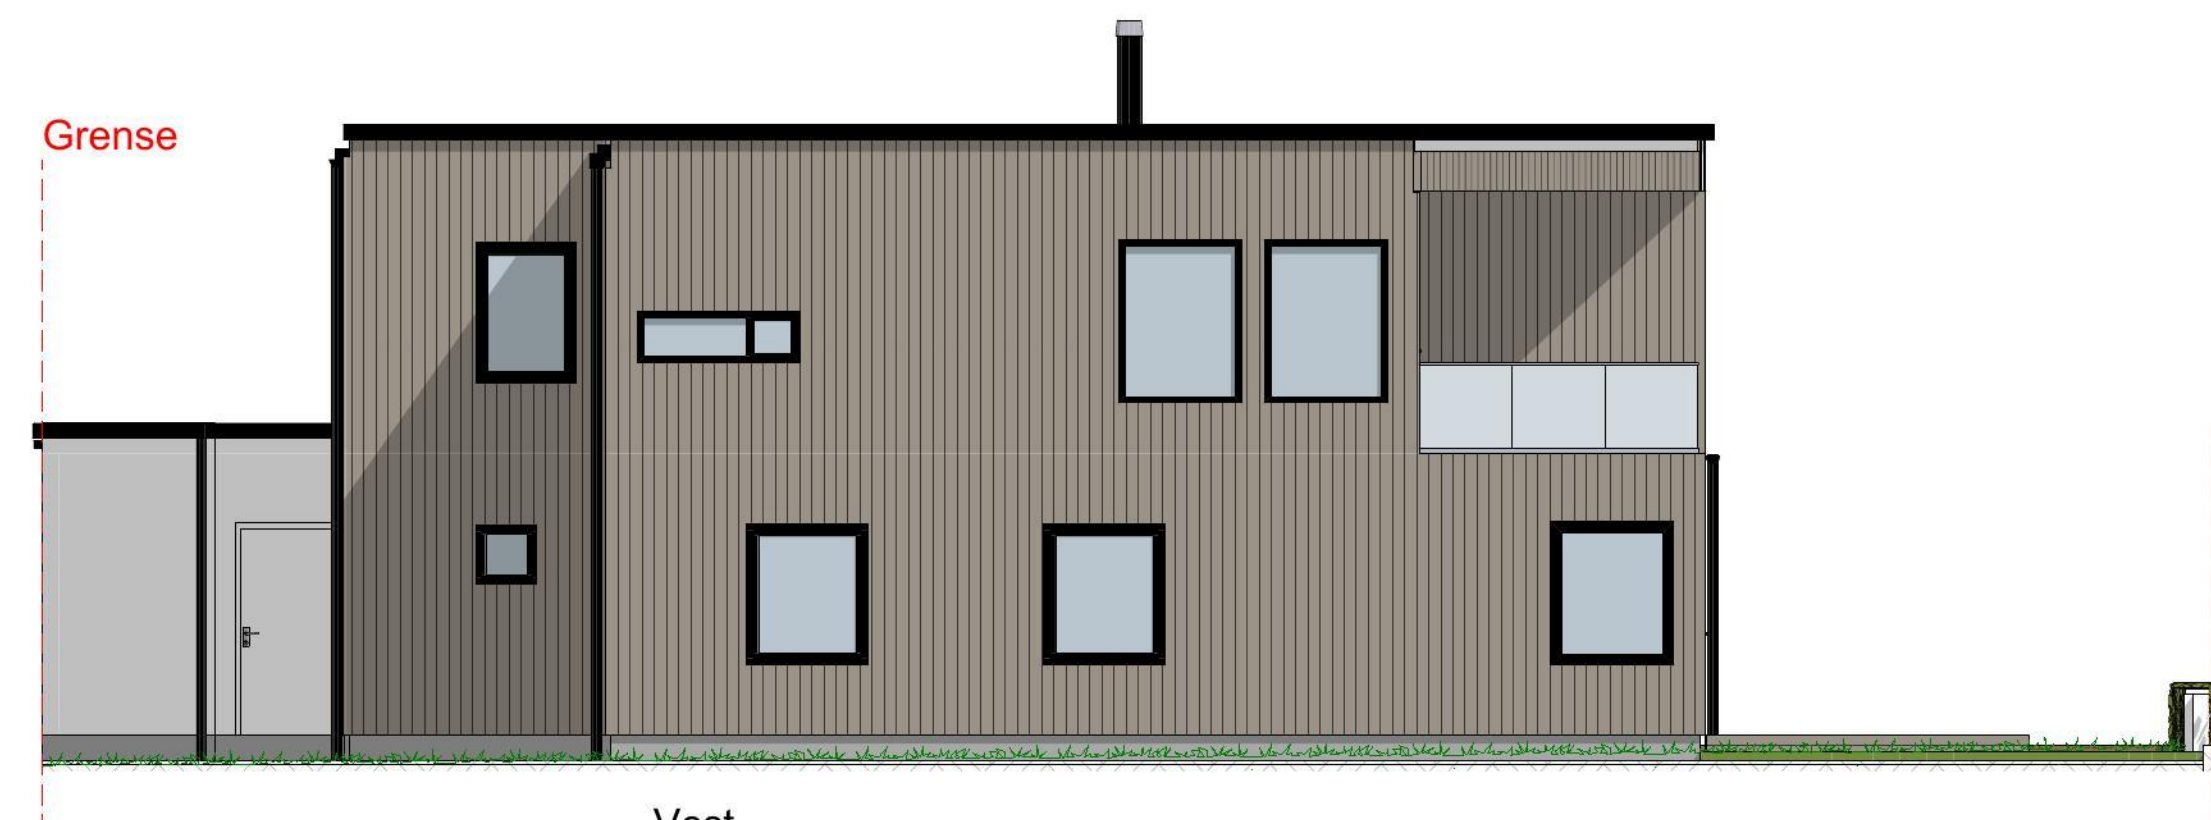

Vest

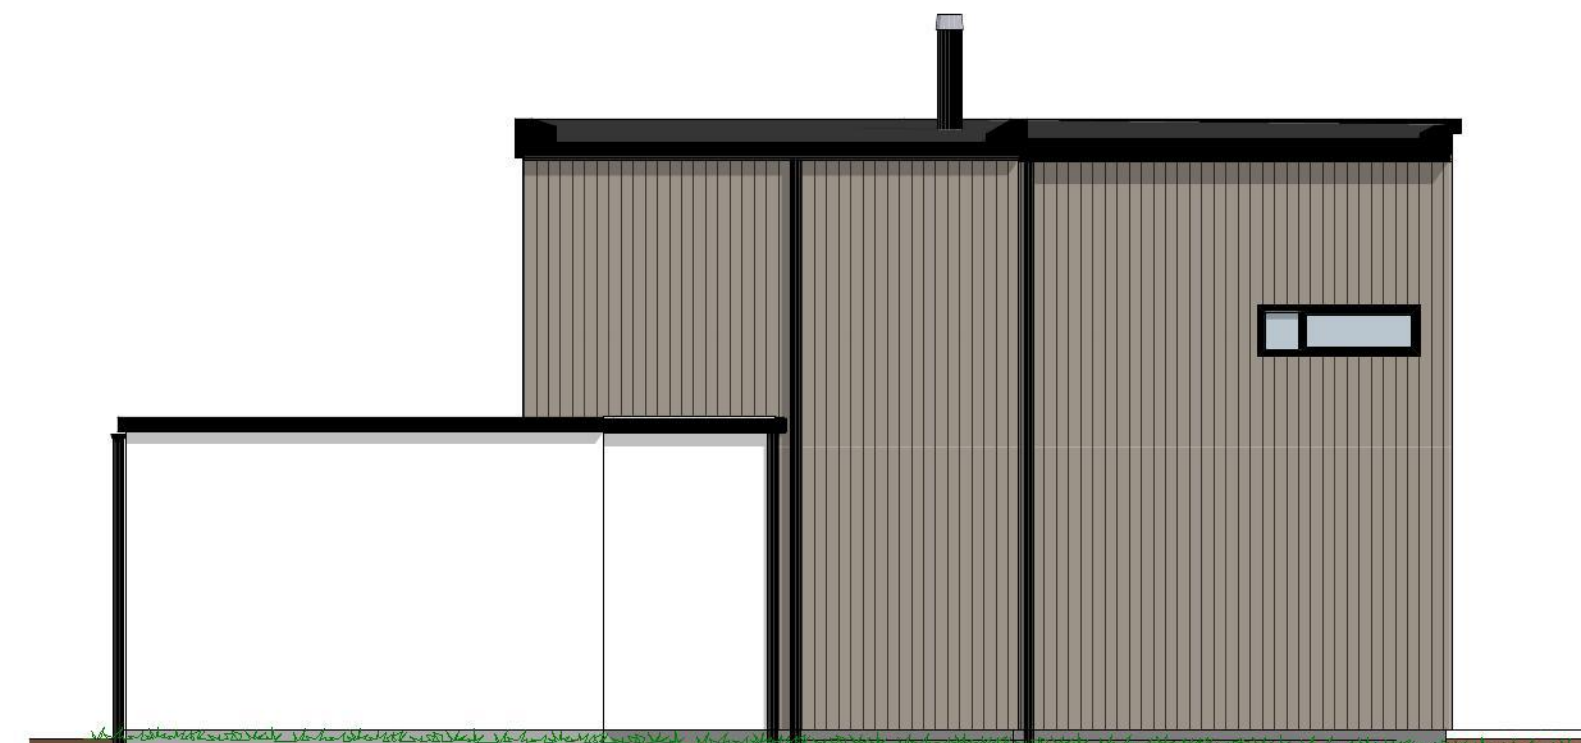


Nord



Sør



Øst

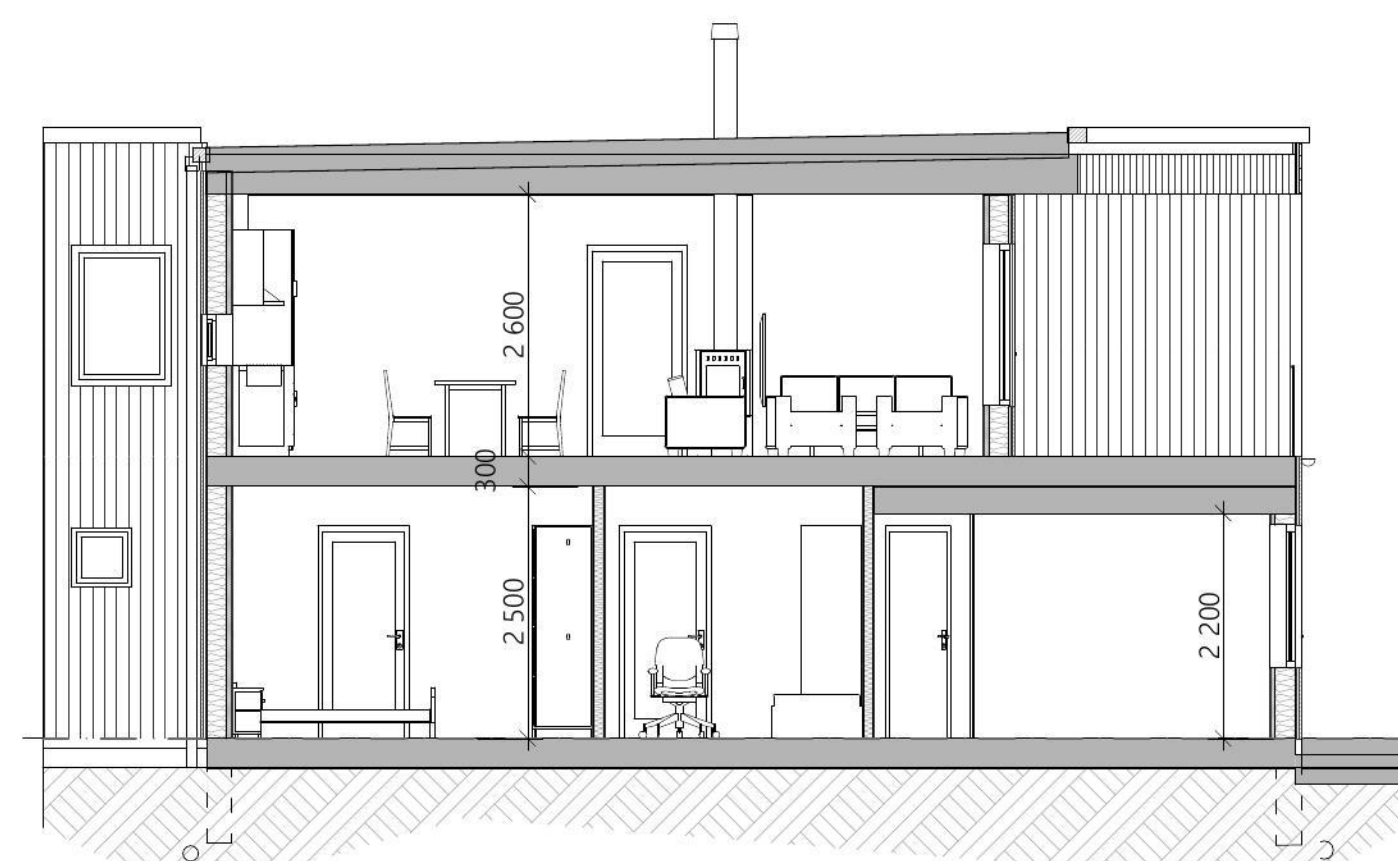

Snitt C

Tegninger kun for byggesøknad. Ved utarbeidelse av prosjekteringstegninger må det foretas kontrollmåling.

Rev.:29.11.23		
Prosjekt Erstatningsbolig m/garasje og bod	Kontroll prosjekt:	
	Sign.: t.th	Kontroll: t.th.
Adresse: Liljeveien 1A, 4316 Sandnes	Gnr/Bnr. 62/79 A:388 m2	
	Arkitektur: Botakst as Gretebakken 12 4355 Kvernaland	
© Alle rettigheter tilhører utførende for arkitektur, kopiering eller bruk av disse tegningene er forbudt uten skriftlig samtykke	Dato: 08.11.2023	
	Målestokk: 1:100	
Tegning: Fasader	Tegningsnr.: E 3	
	A3	