

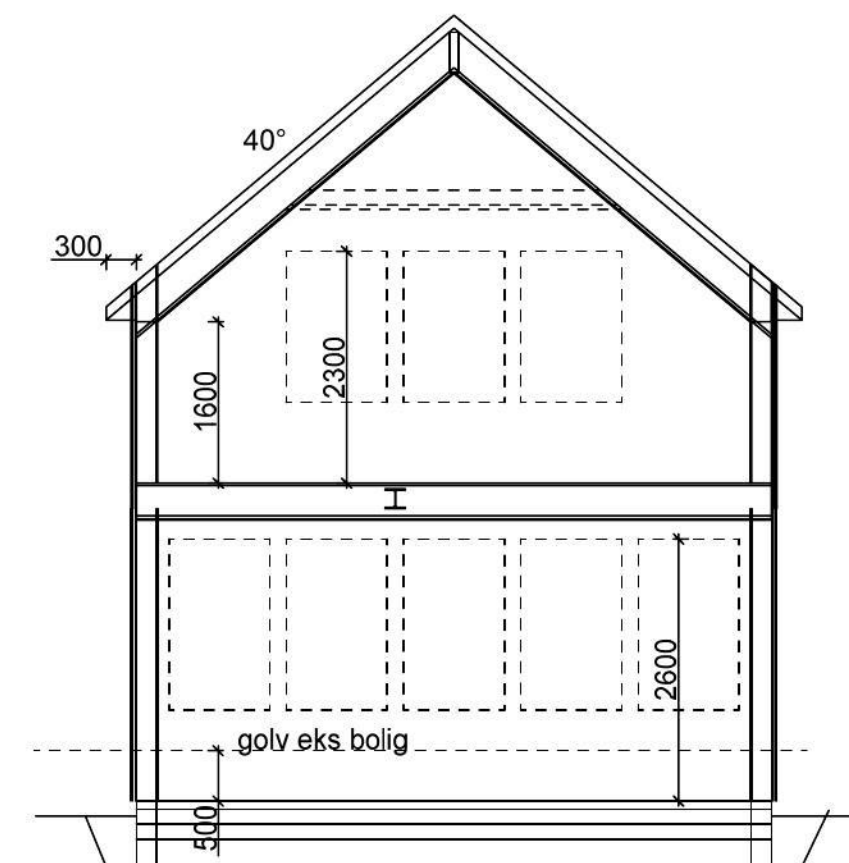
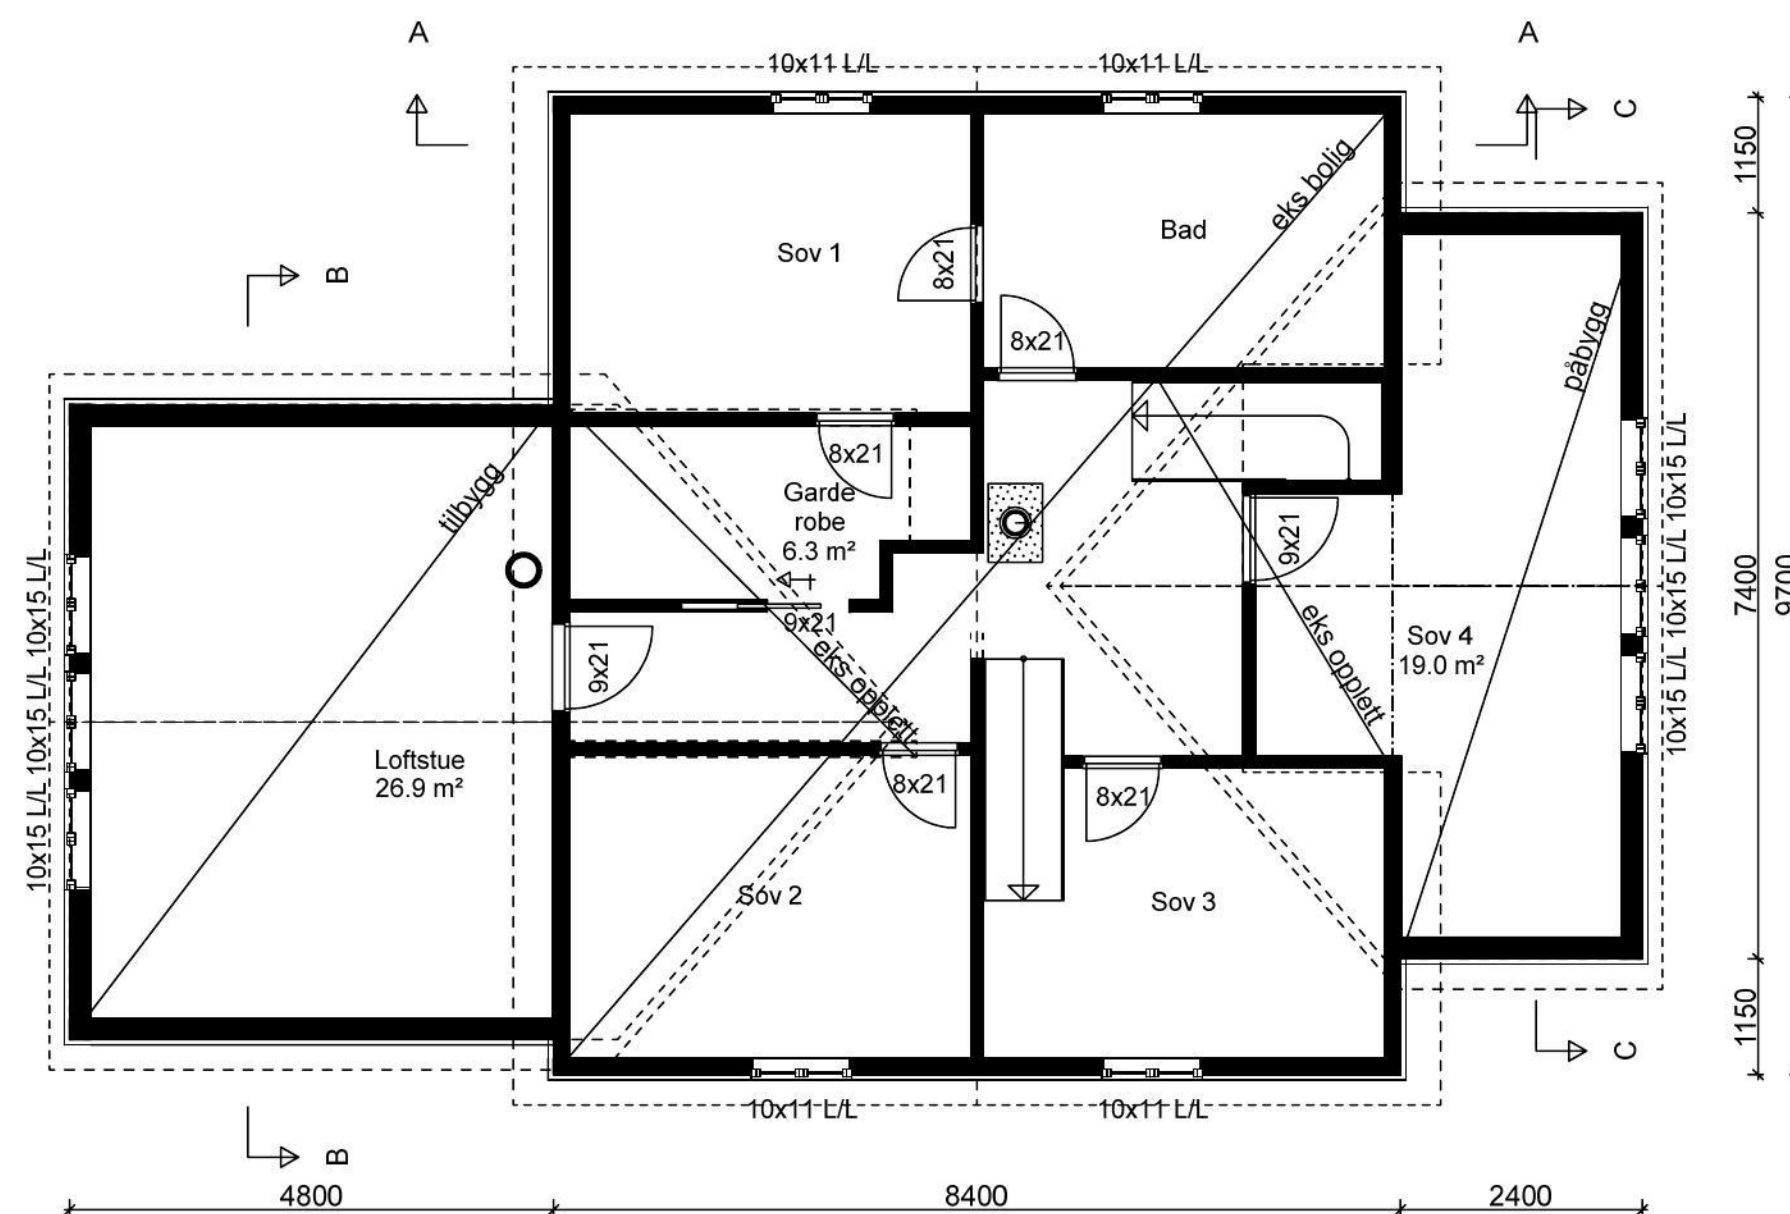


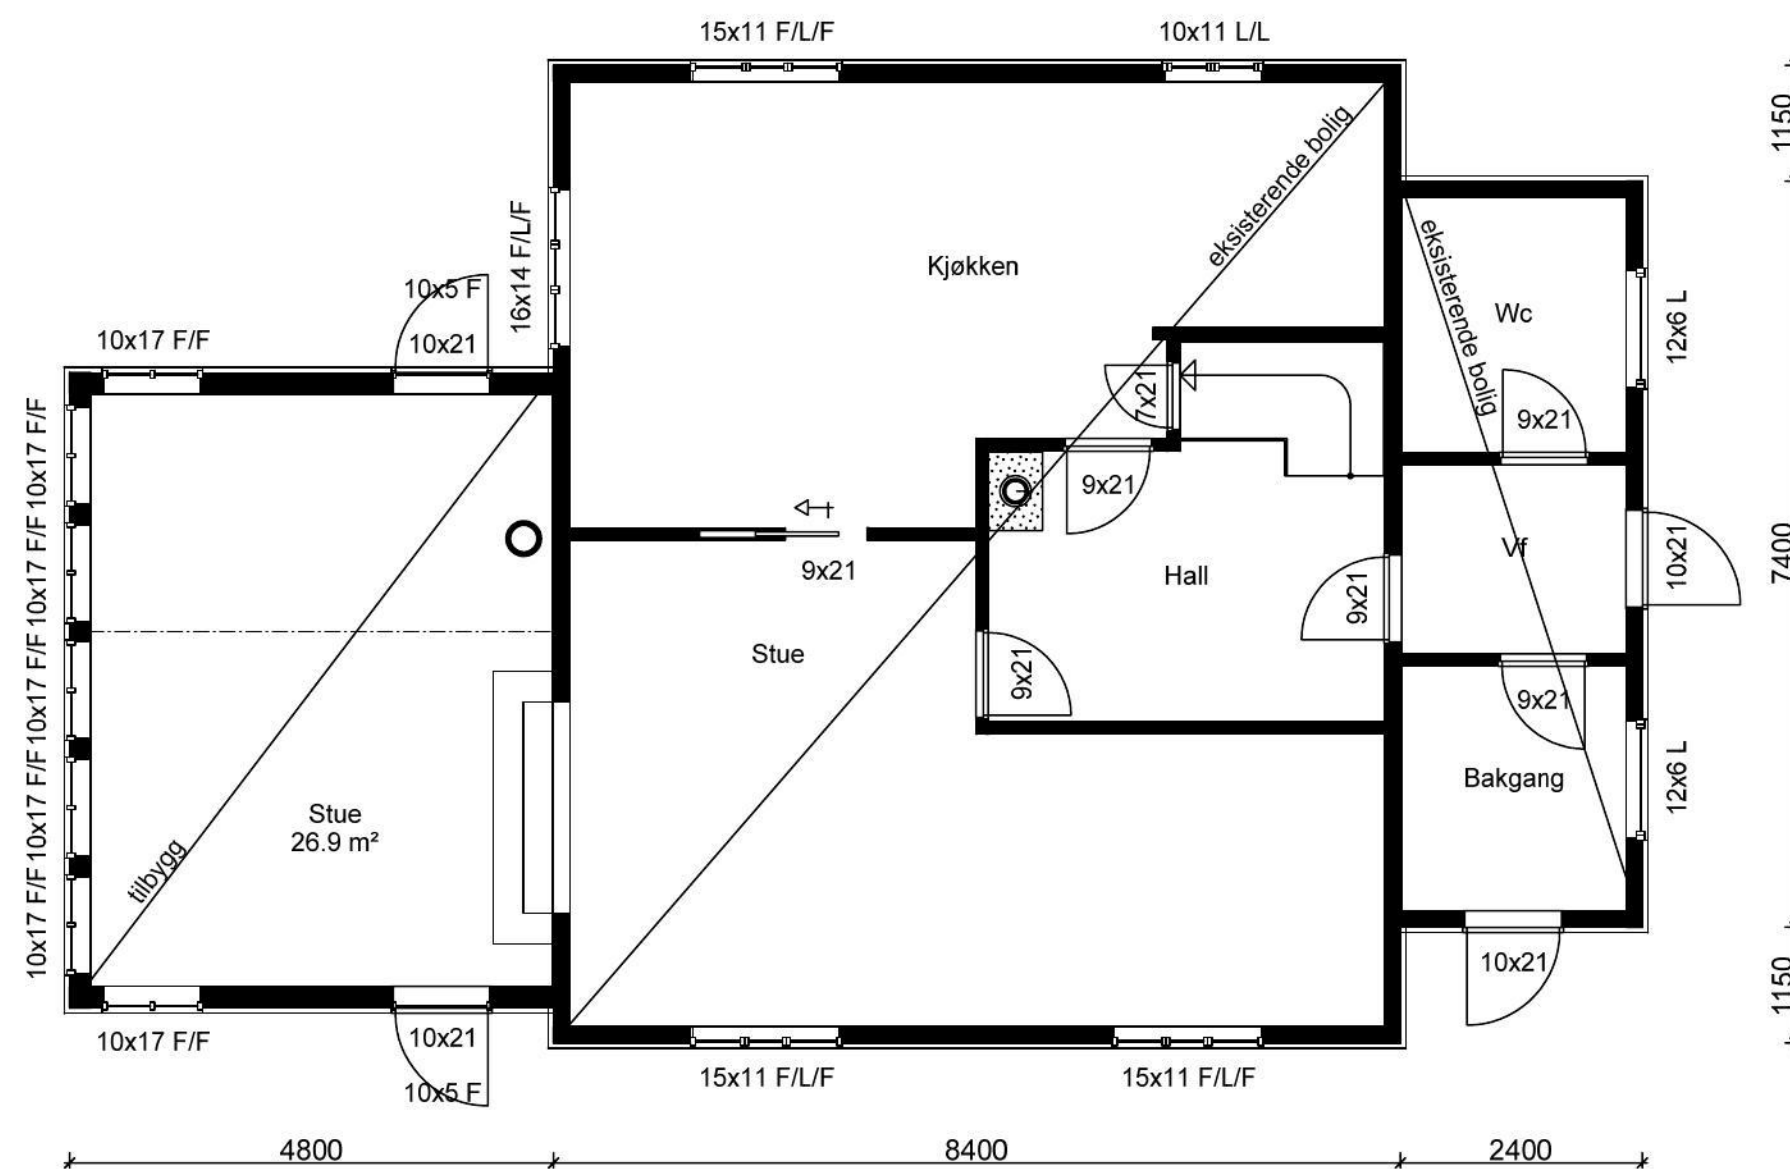

SNITT B-B

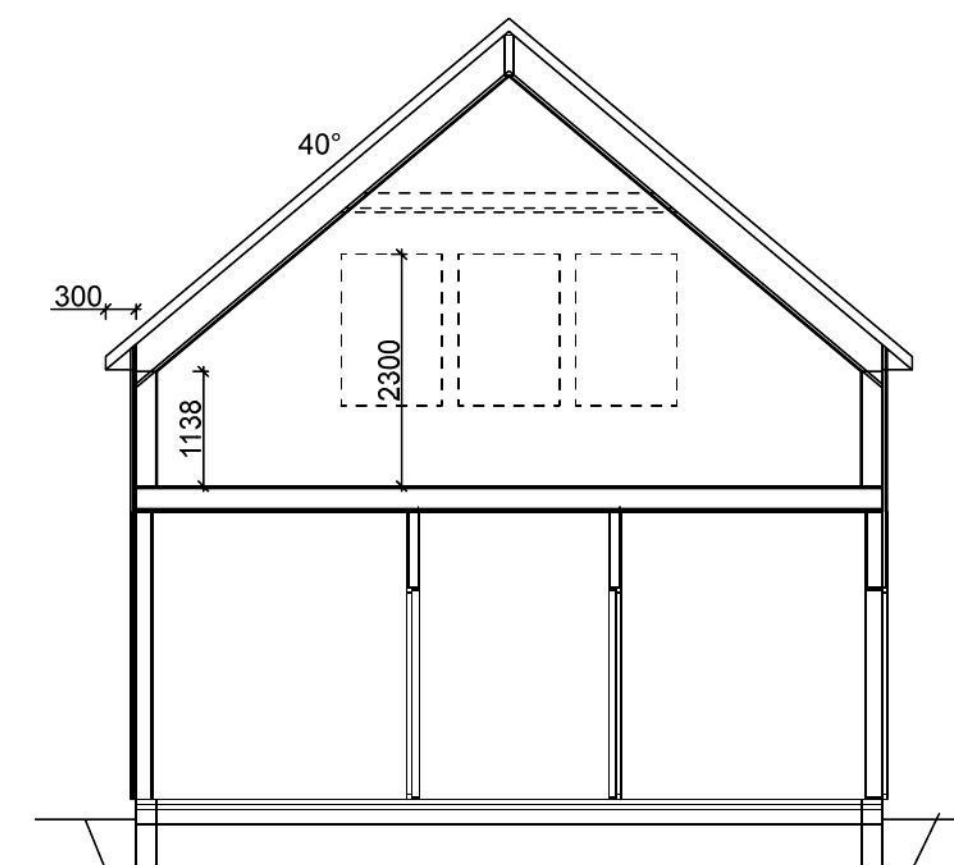

SNITT C-C

Bruksareal BRA kvm	
Arealberegninger i hht. NS 3940	Sum BRA
1. etasje	27.9
2. etasje	43.0
SUM :	70.9
BYA :	30.8

Arealberegninger i hht. NS 3940	Bruksareal BRA kvm	
	Pr etasje	Sum BRA
1. etasje	92.7	92.7
2. etasje	72.9	72.9
SUM :	165.6	165.6
BYA :	101.5	101.5

Tiltakshaver: Morten Malmin		Målestokk 1:100	Tegn AIL	Dato 23.11.2023
Byggeplass : Malminhagen 22			Trac	Dato
Kommune : Sandnes	Gnr57	Bnr41	Disk Malmin	Sak Tilbygg/påbygg
Utbygger		Planlegger	Tegn nr	Malm1503
		 anniren@ark-1.no - tlf 99090113	Prosj nr	