
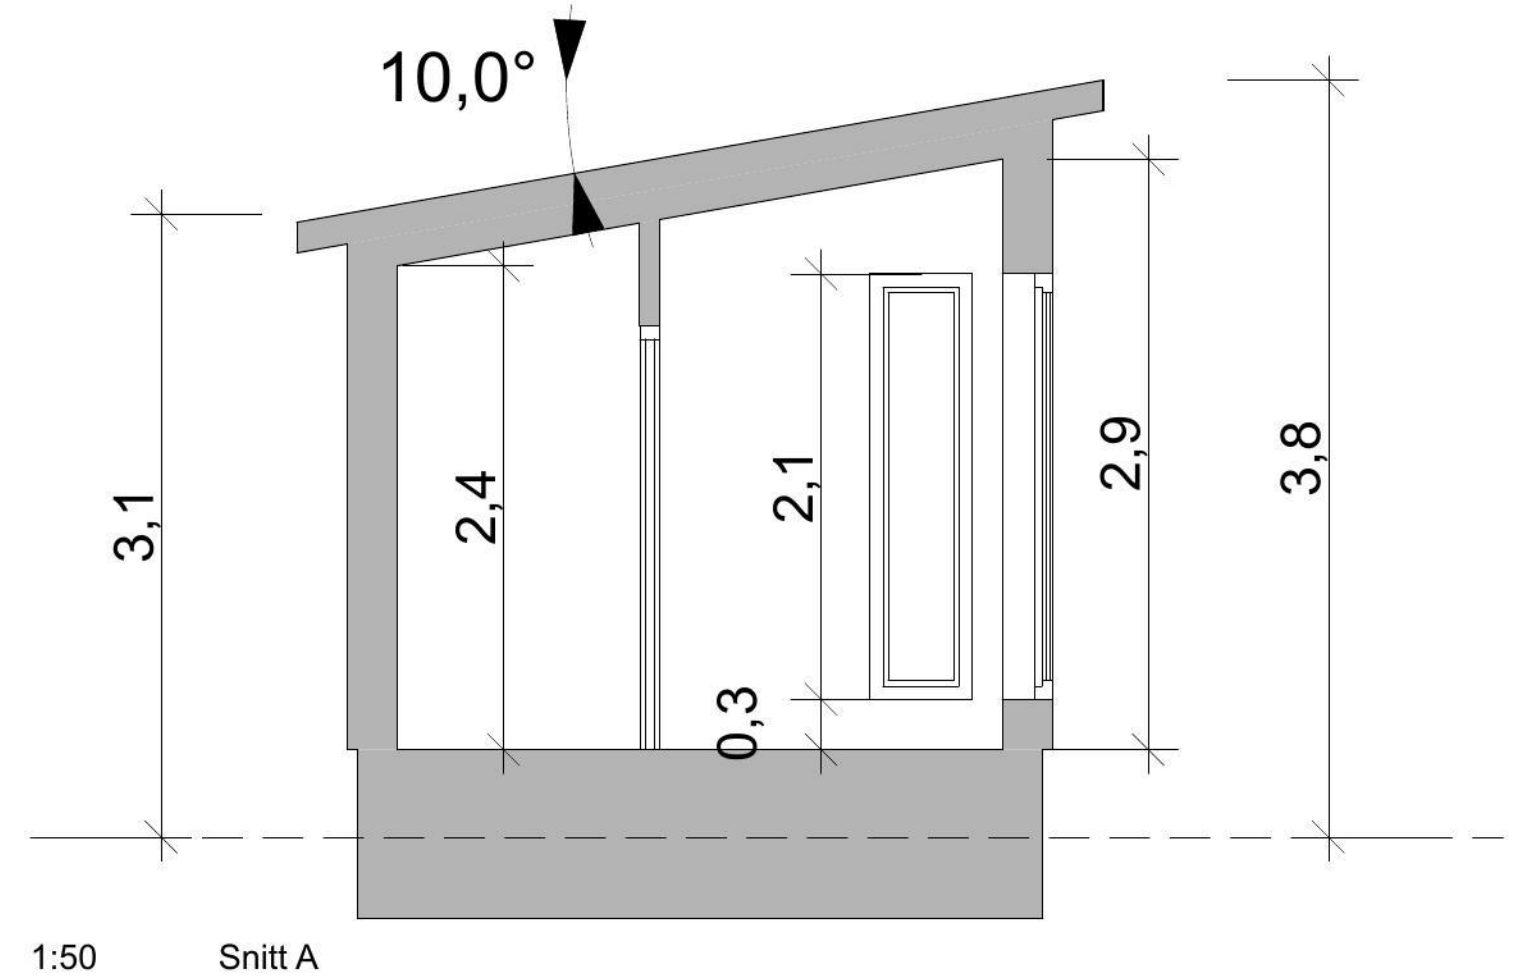


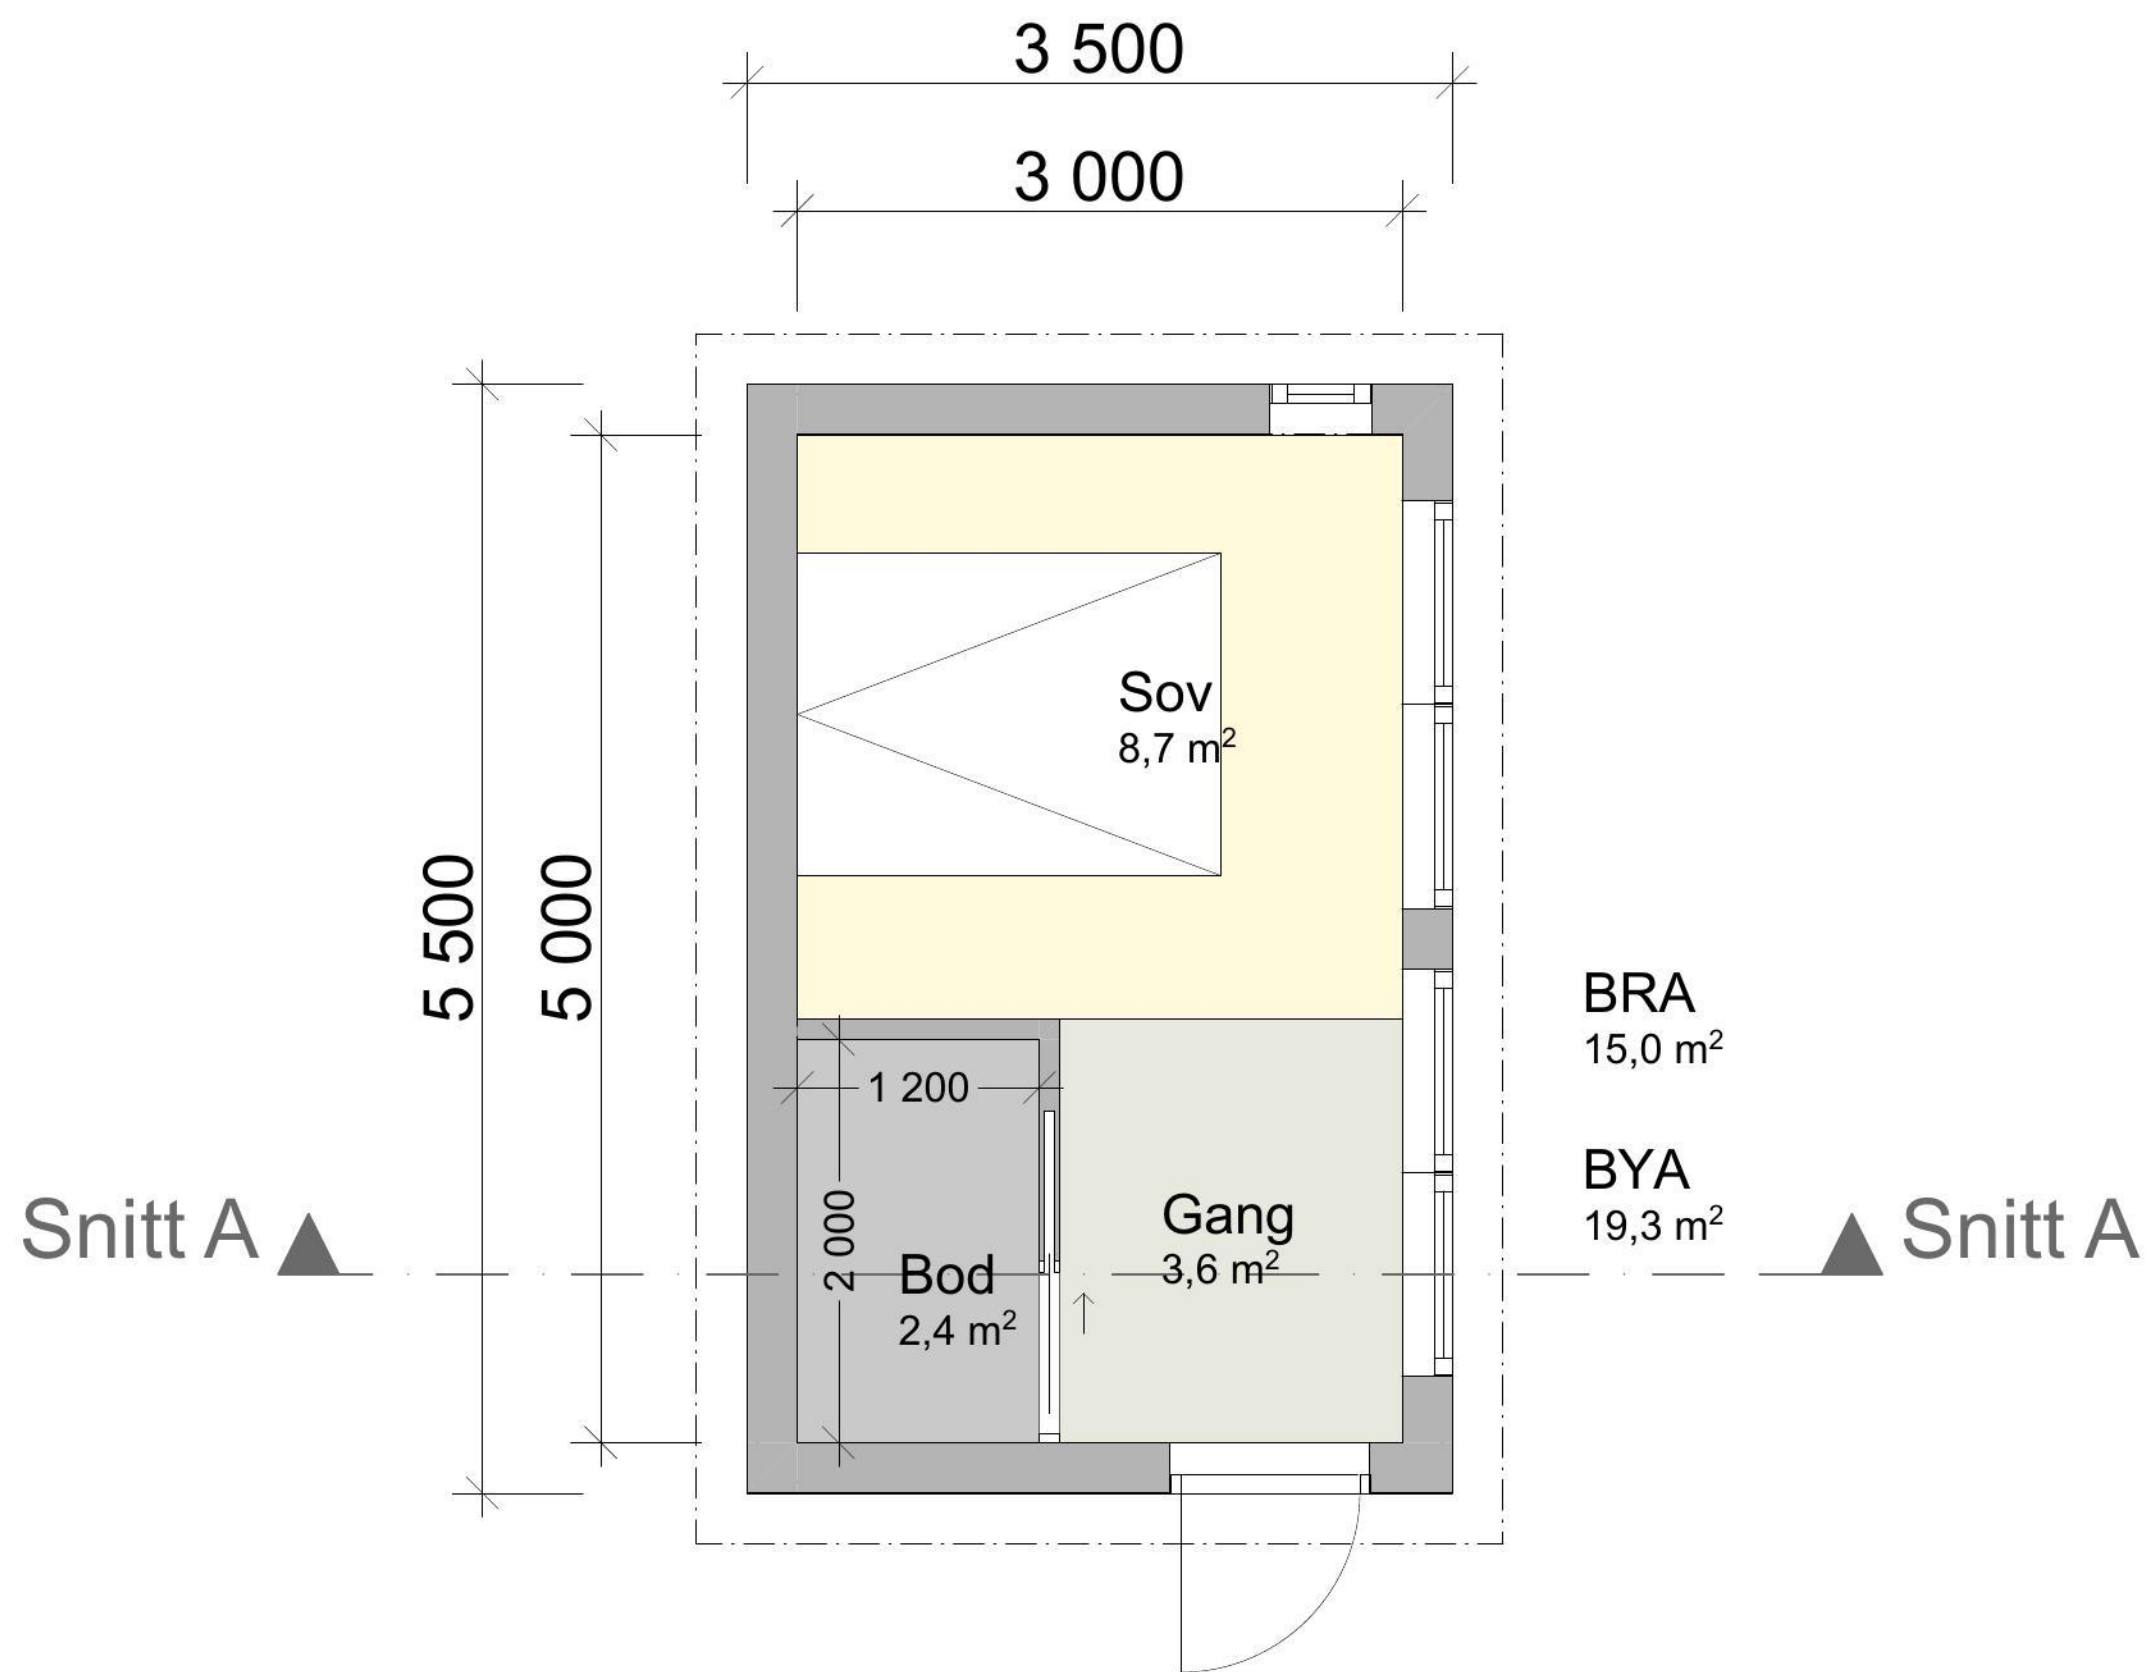

Tiltakshaver: Nina Drange Materialgården 17 1747 Skjeberg		Gnr./Bnr./Festnr.: 1133/3/57	
		Dato: 12.12.2023	
TN Tegning AS Yvenbråten 2 1715 YVEN			
© Alle rettigheter tilhører utførende for prosjektering, kopiering eller bruk av disse tegningene er forbudt uten skriftlig samtykke		Målestokk: 1:50	
Tegning: Plan og Snitt A		Tegningsnr.: A20-01	Rev.: . Sign.: