



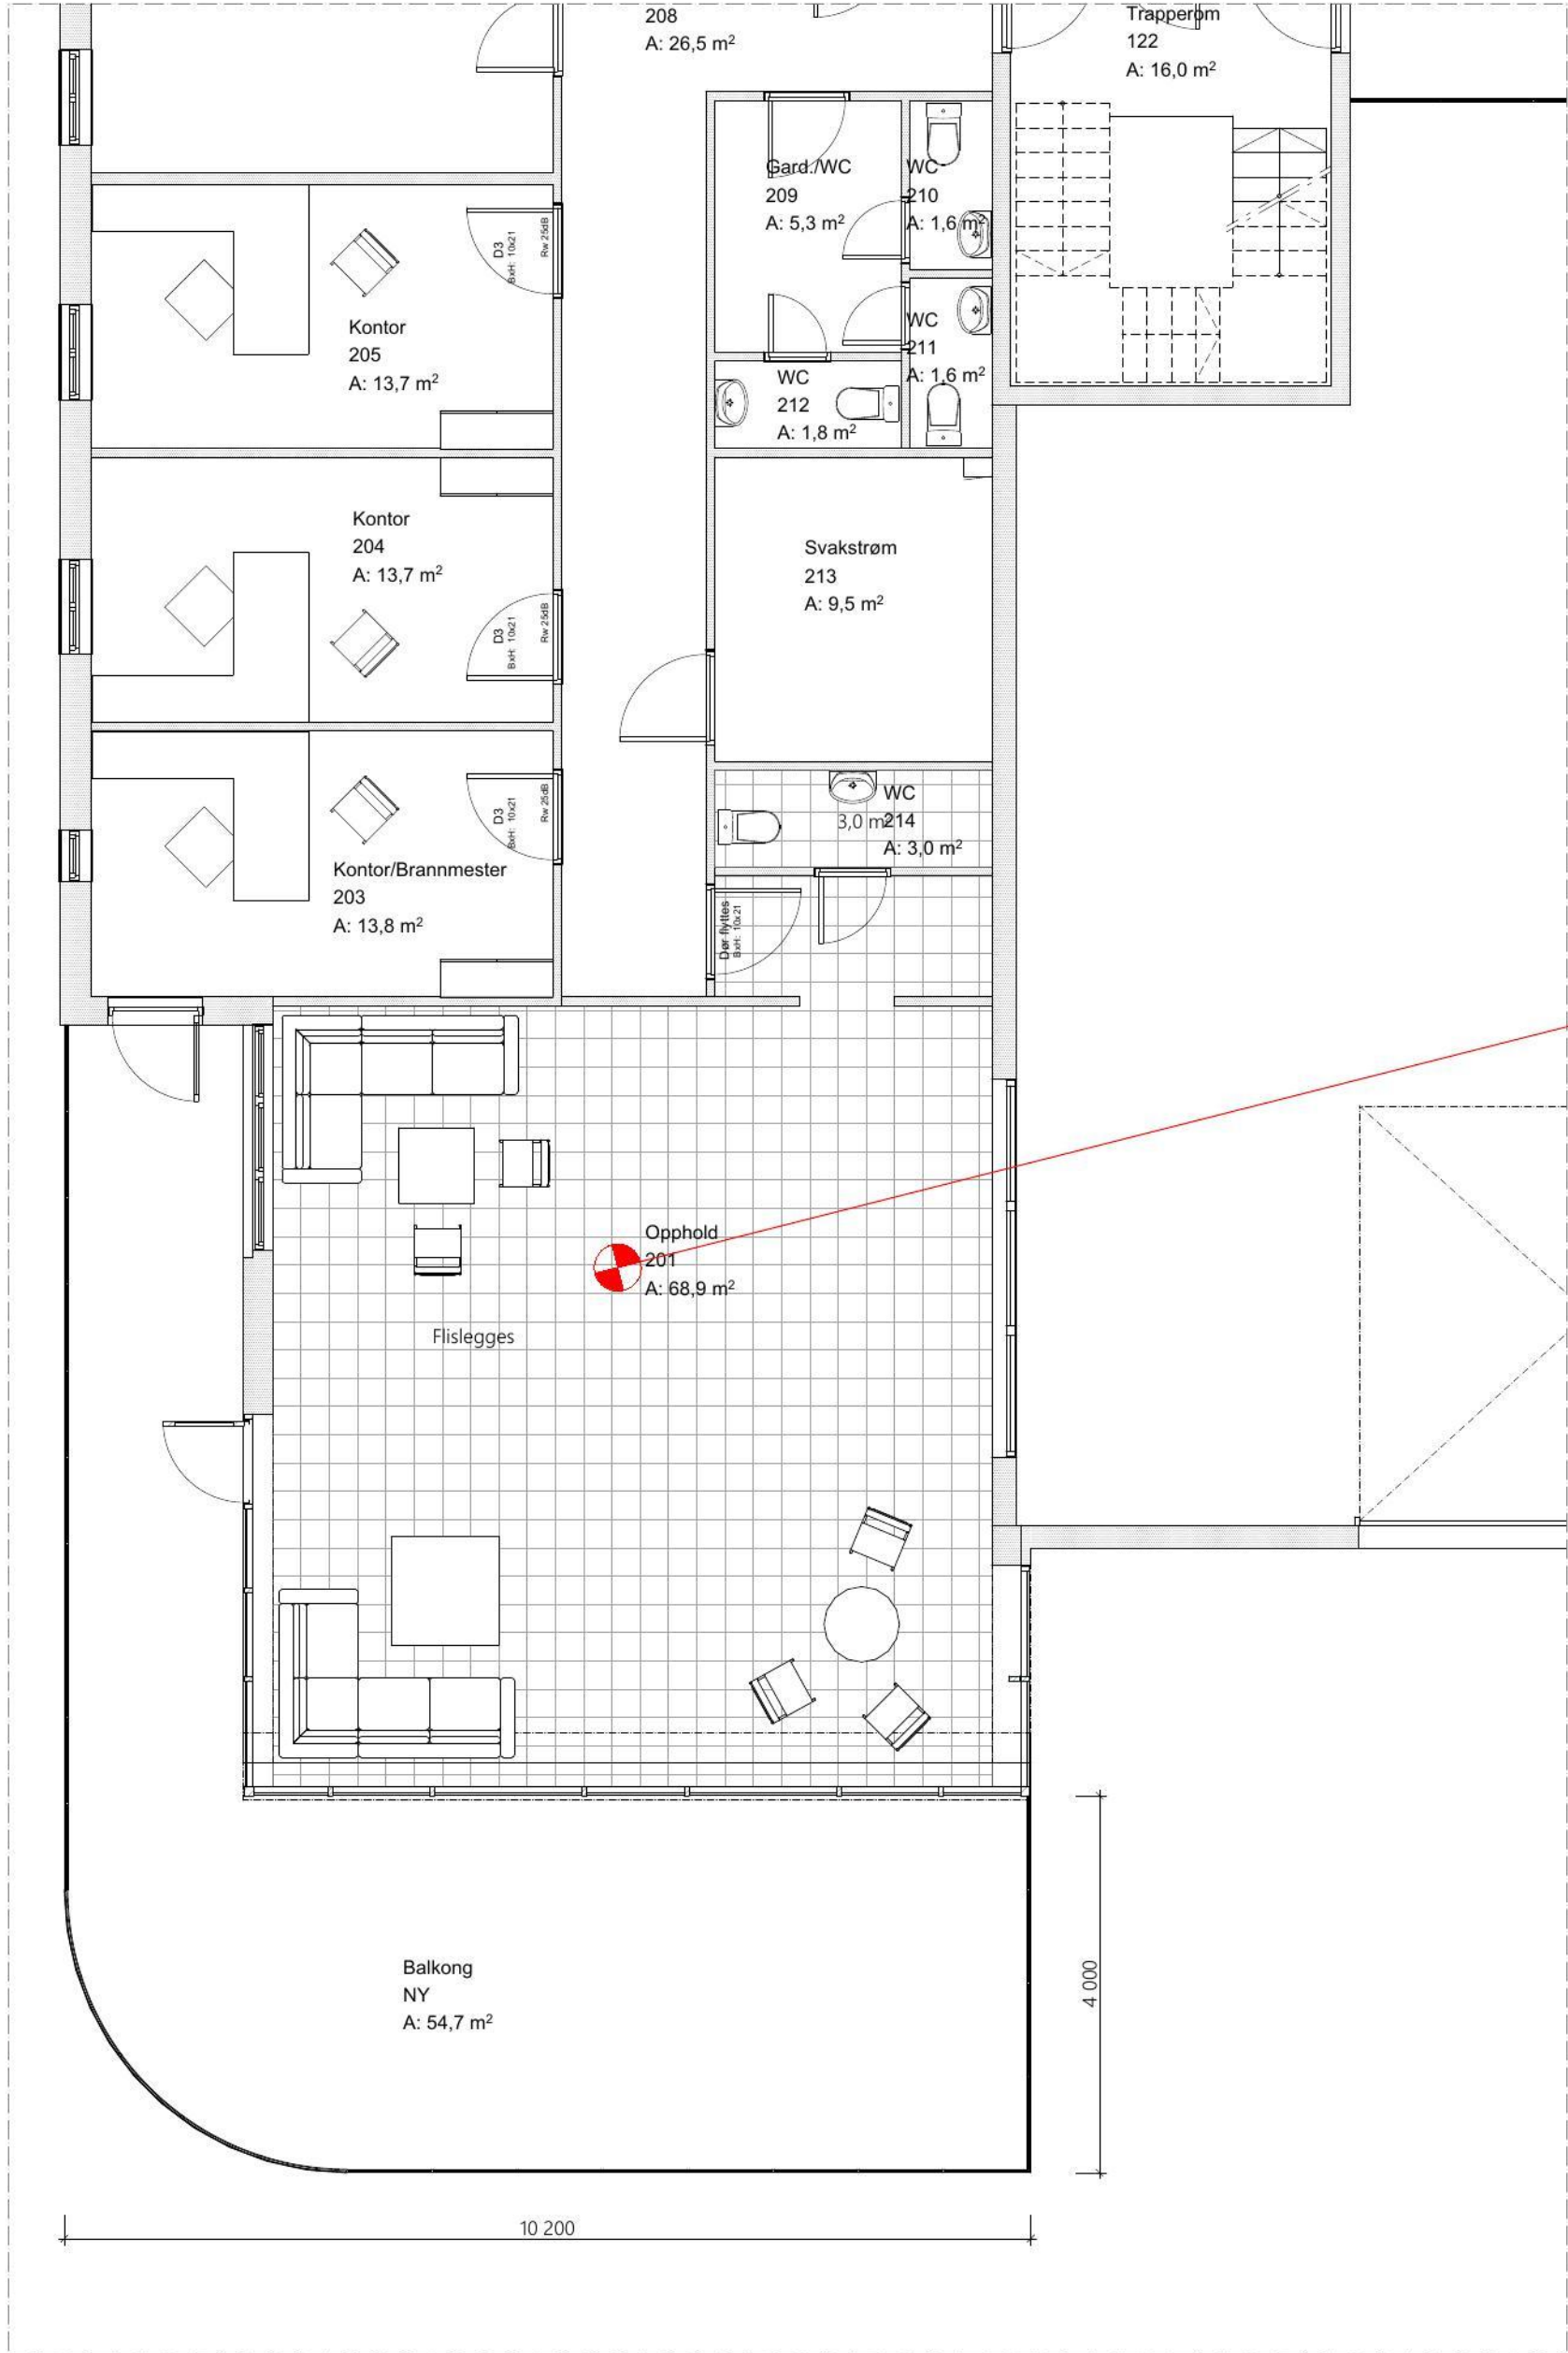


1:100 Vaktrom - Etter ombygging


NB!
Utvidelse balkong er en opsjonspost.

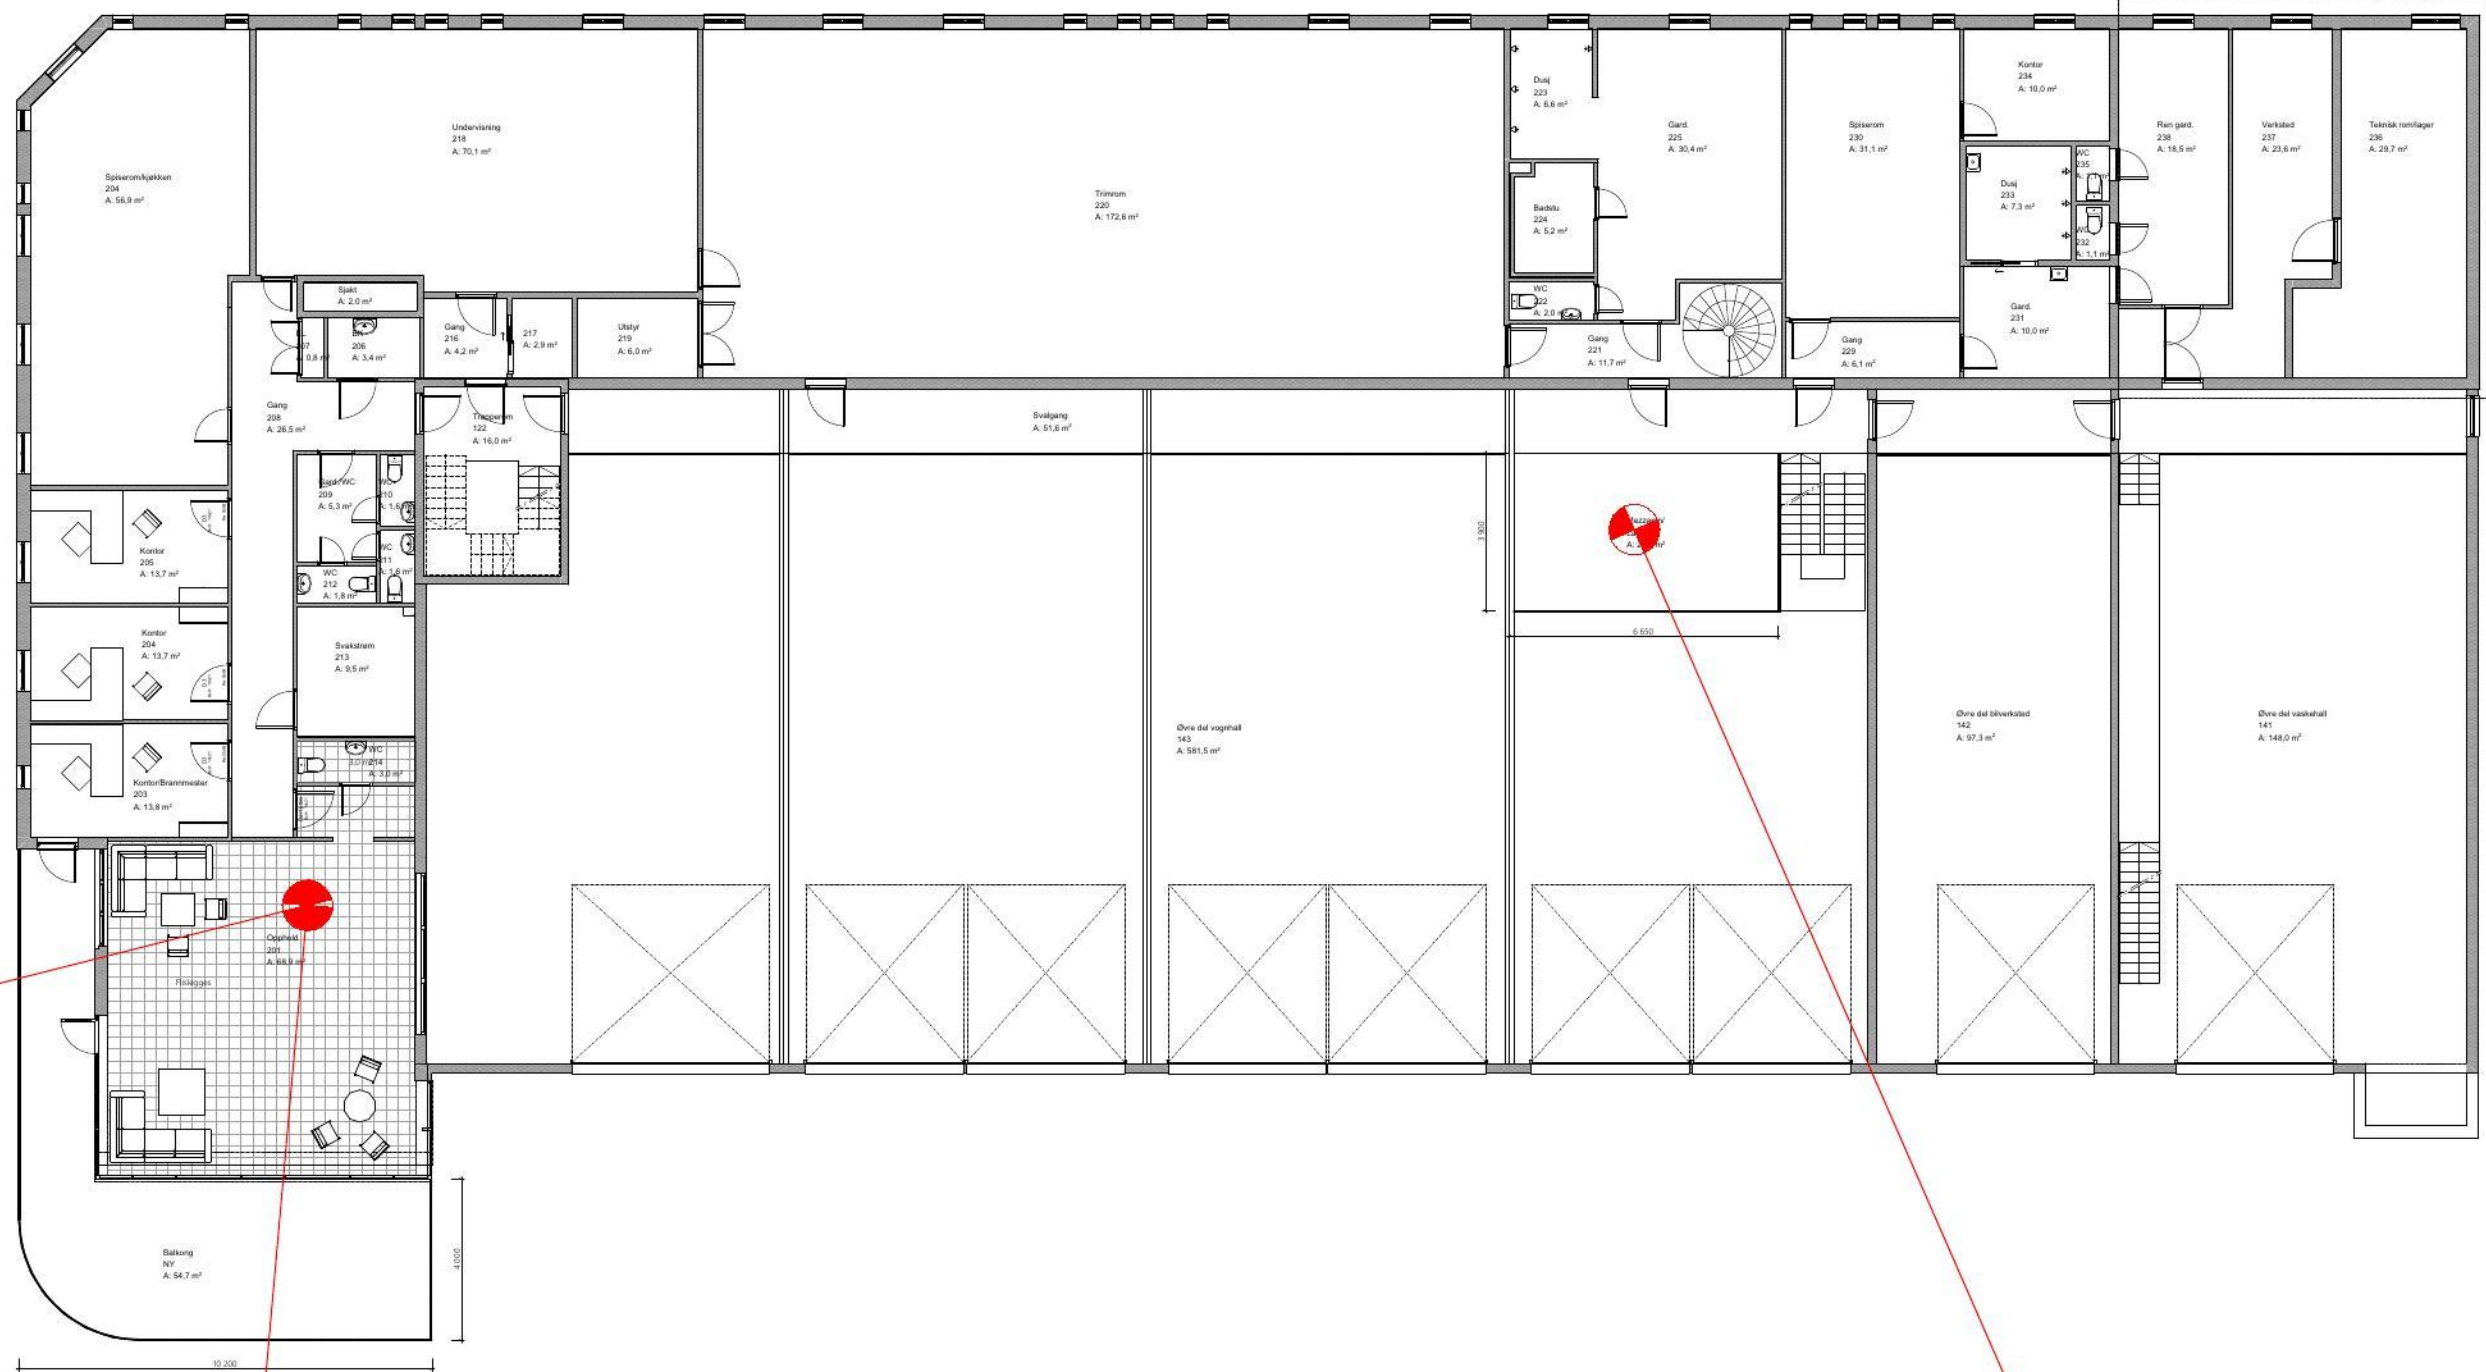

1:250 2. Etasje

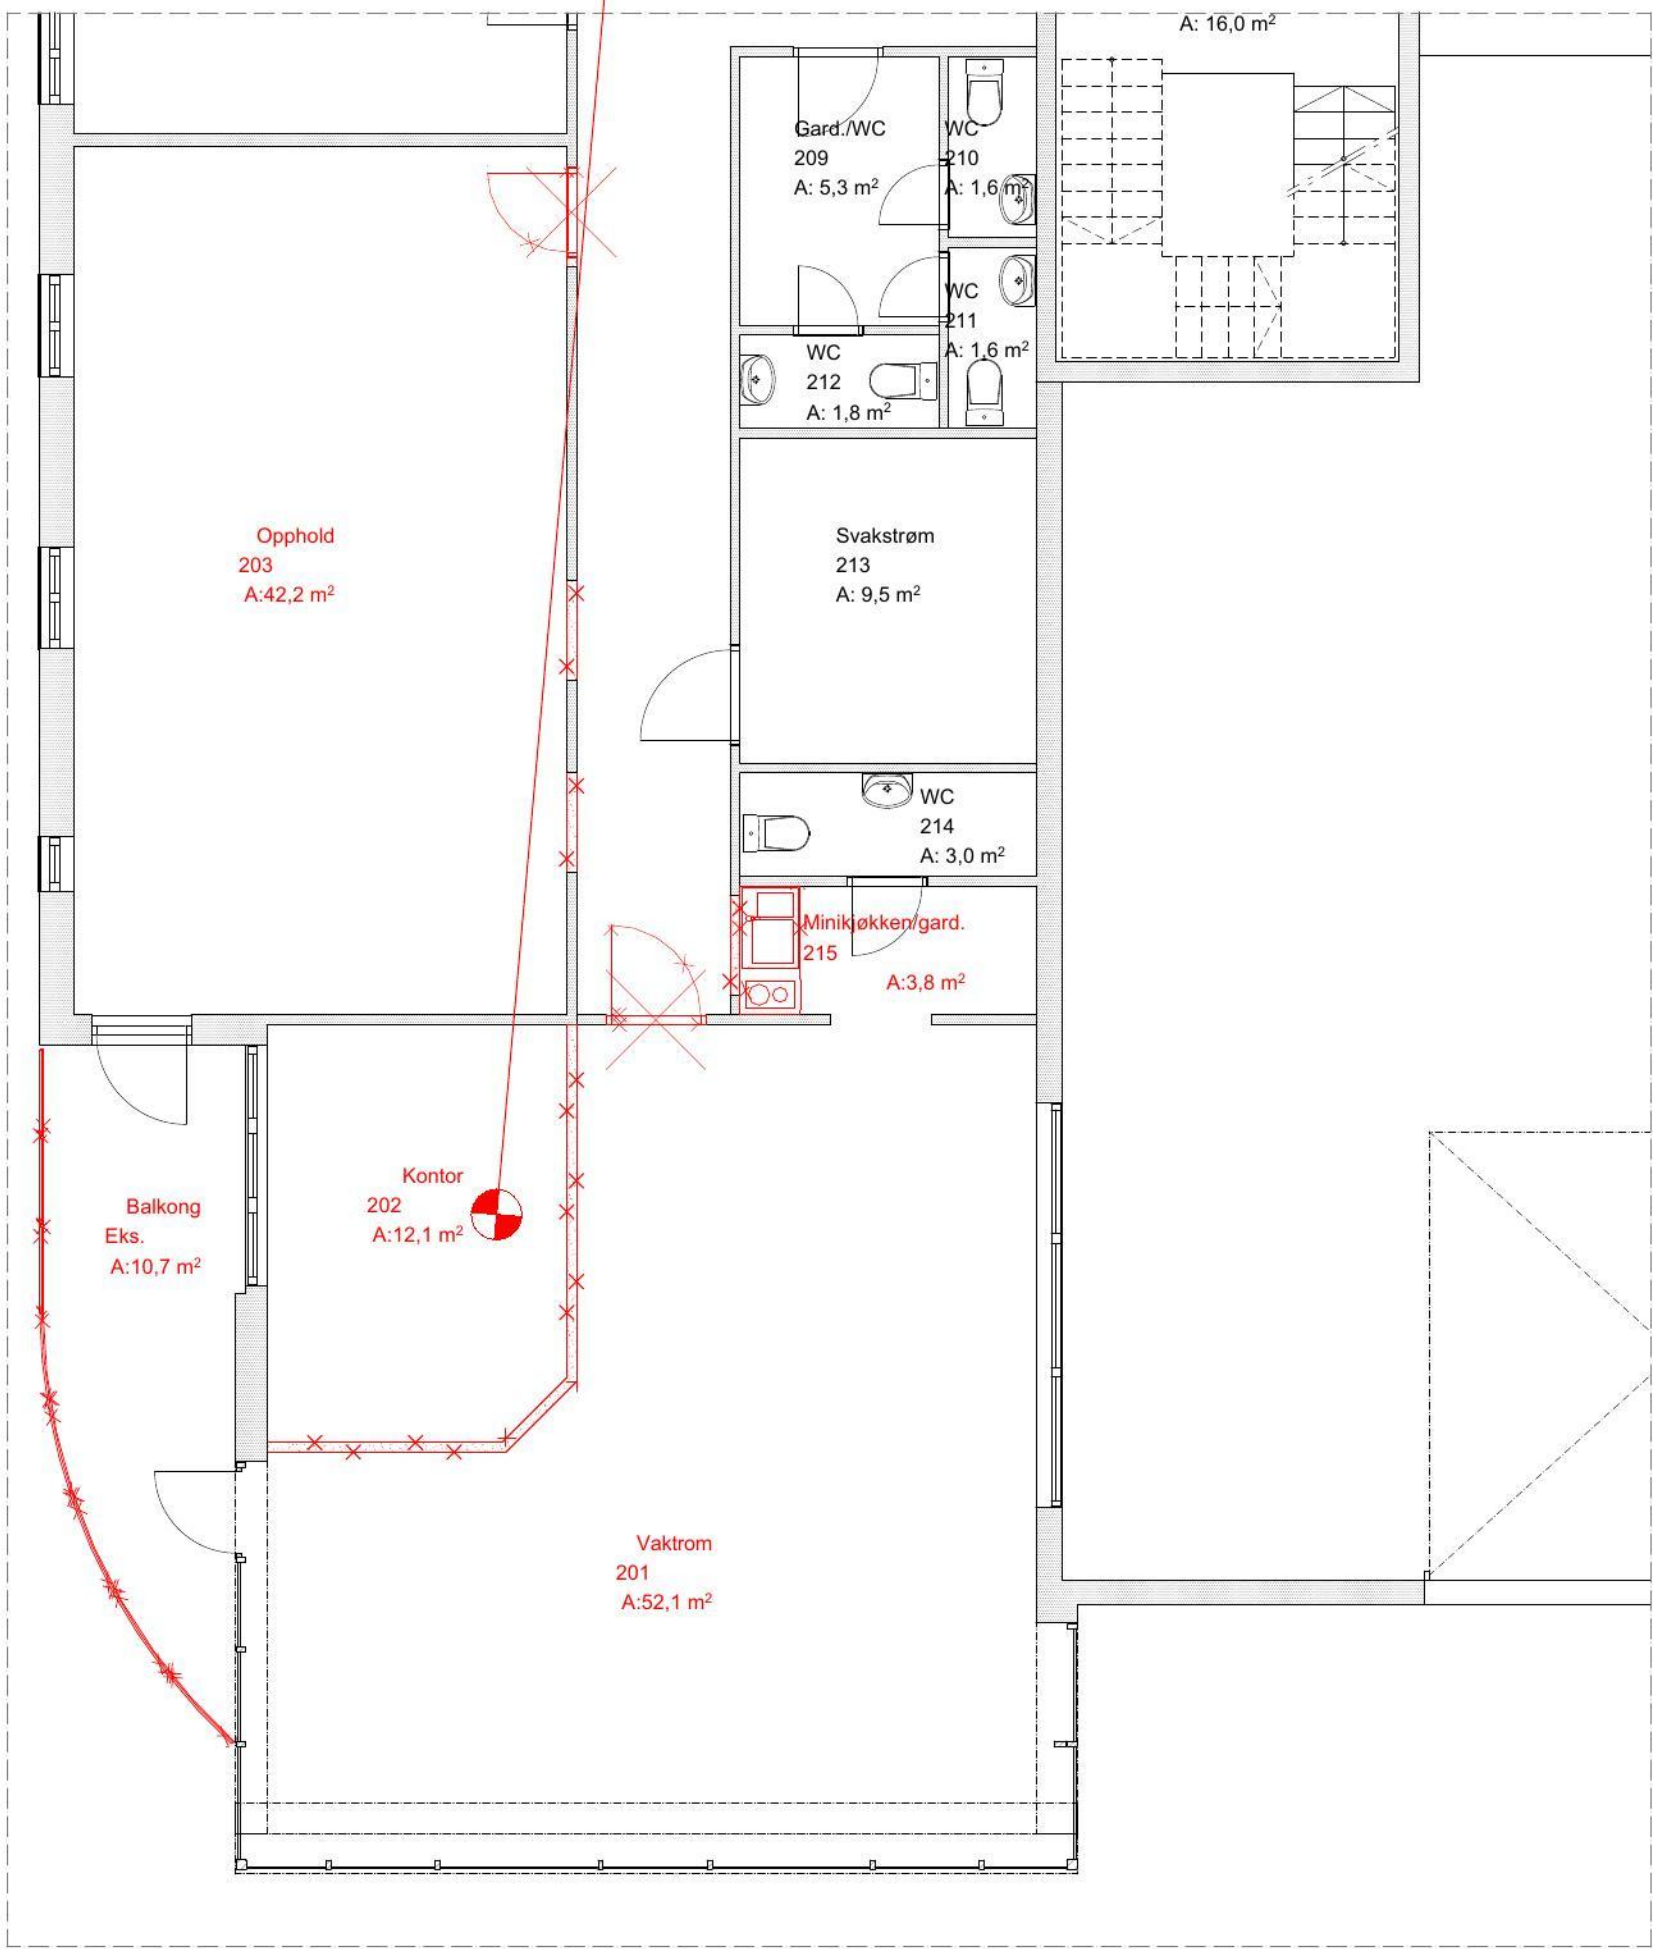

1:100 Vaktrom - Rivetegning

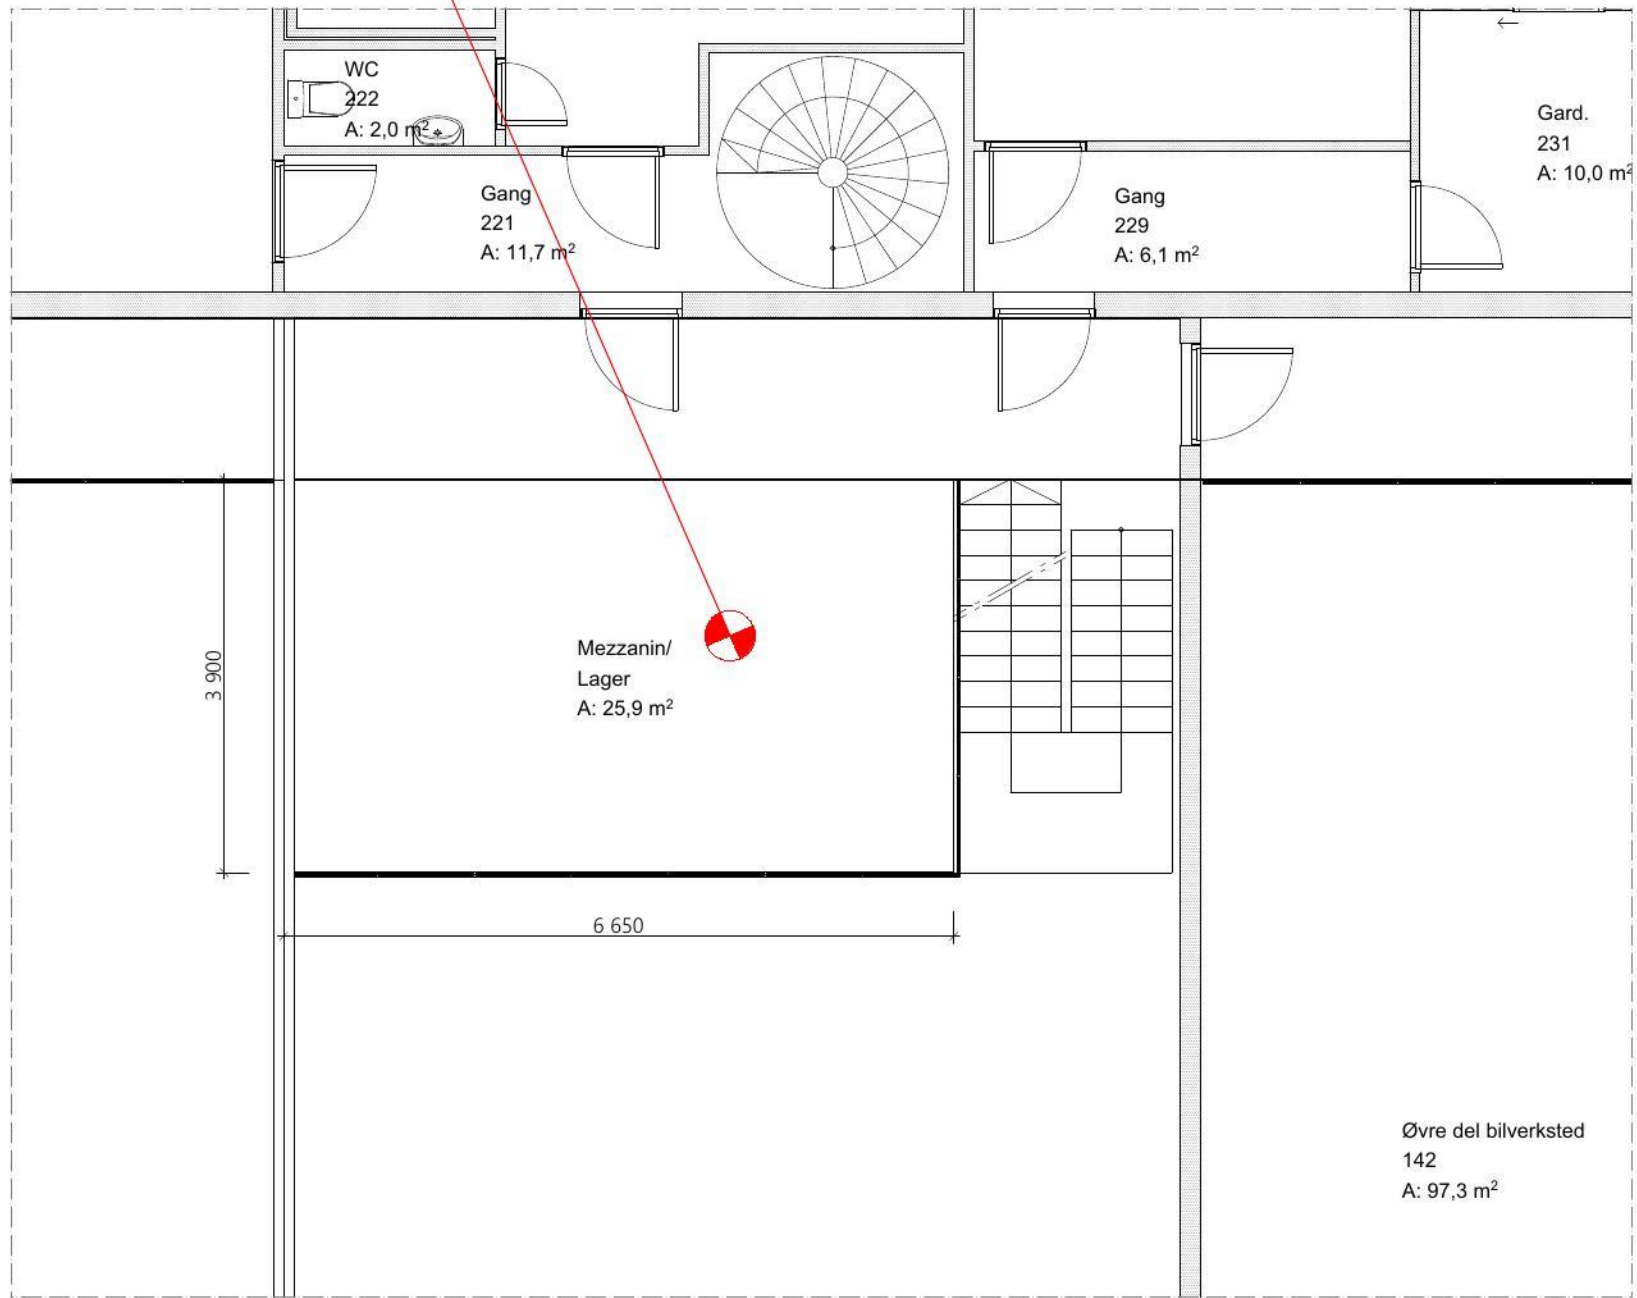

1:100 Ny mezzanin

NB!
Utvidelse Mezzanin er en opsjonspost.

OMBYGGING 2 ETASJE - FASE 2

Sarpsborg kommune					
Postboks 505, 1703 Sarpsborg postmottak@sarpsborg.com mob.69 10 80 00					
ARK AMA AS					
Ordfører Voldens vei 9 1850 Mysen e-post: post@arkama.no Tlf. +47 69 89 00 11, Org.nr.982 534 860					
N					
Prosjekt Sarpsborg Brannstasjon					
Tegning Plan 2. Etasje					
Prosjektnr. 2110	Dato opprettet 25.07.23	Gnr./Bnr. 1 / 1948	Mål 1:250, 1:100	Tegningsnr. A22-102	
Fase. Tilbudstegning	Sign. JAC	Kontroll SM	Godkjent SM	Rev. ID	
Rev	Nr	Beskrivelse	Dato	Sign	Kontr