



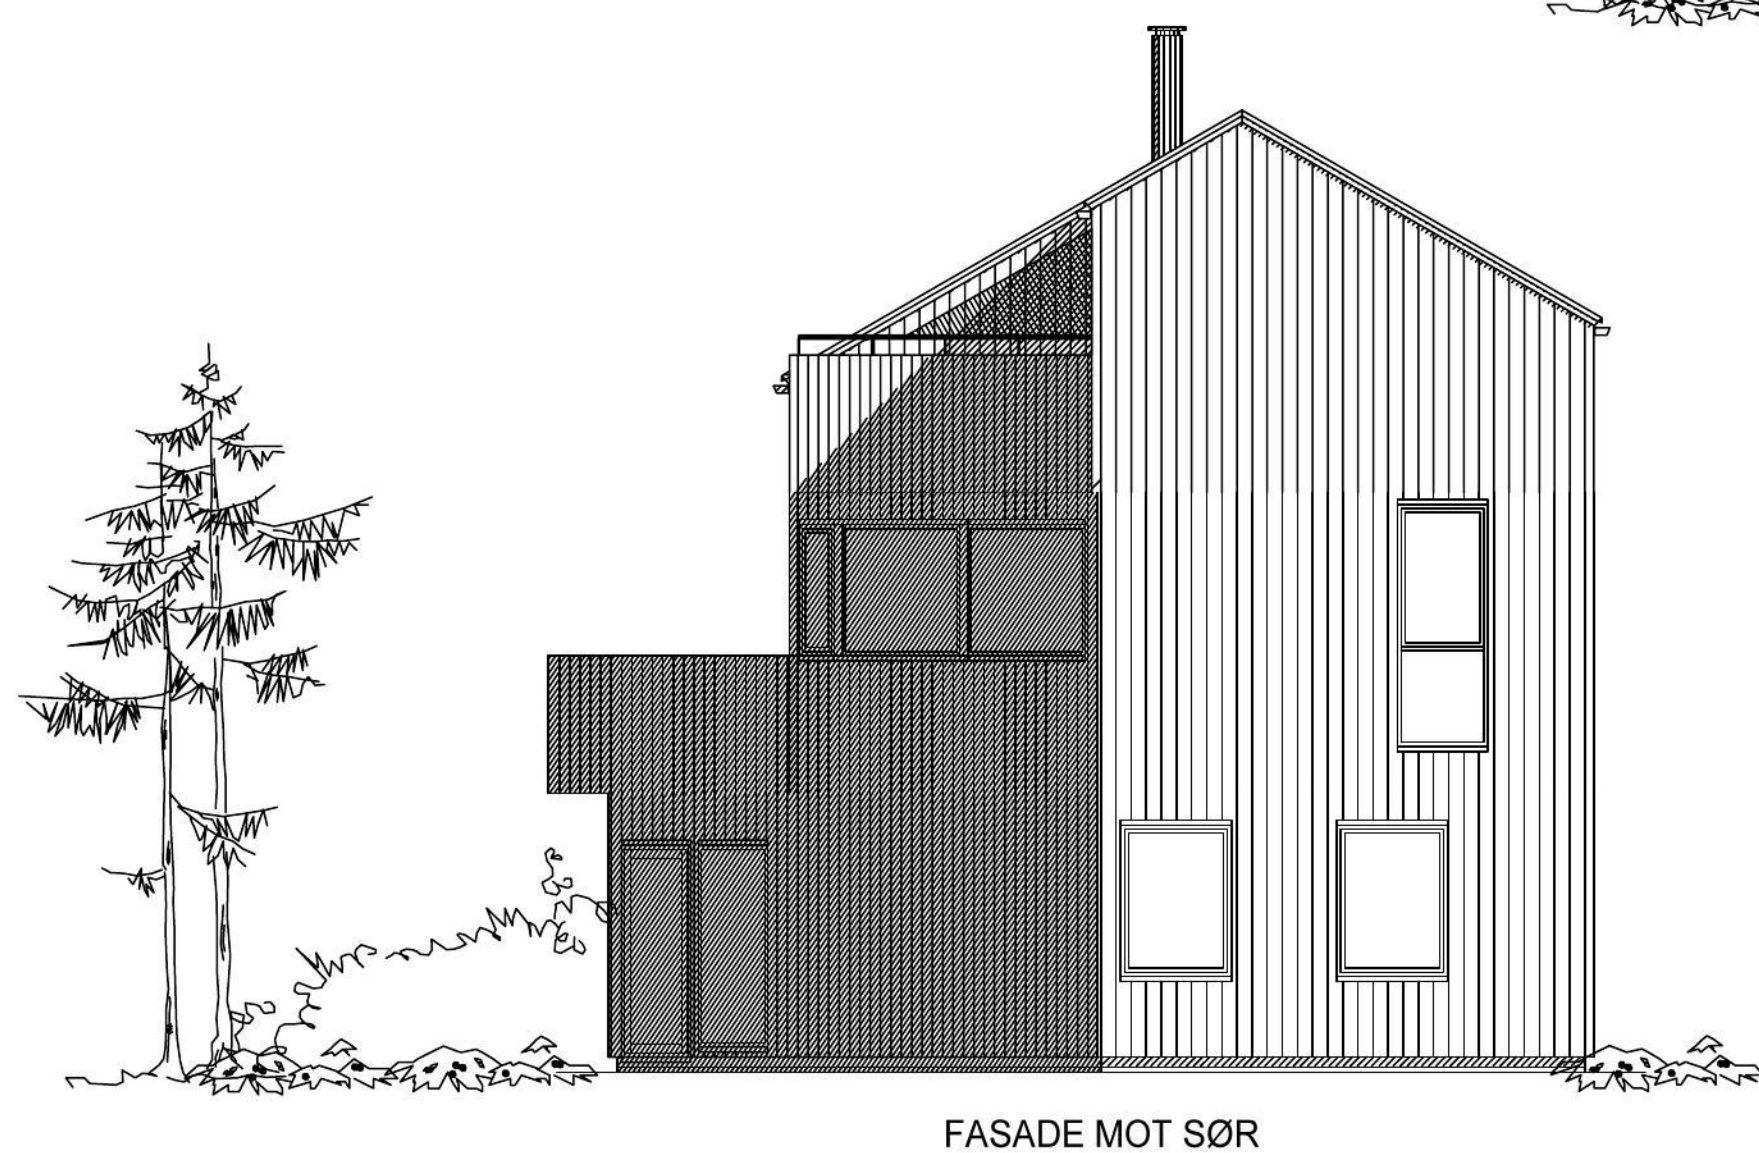

C Terrensnitt 06.02.2024 AIL  
B Rev 16.01.2024 AIL  
A Rev 12.01.2024 AIL

|   |  |  |   |          |                  |
|---|--|--|---|----------|------------------|
| Tiltakshaver: Rogaland bolig as                                                                           |  |  | Målestokk   | Tegn AIL | Dato 16.04.2021  |
| Byggeplass : Mindeveien                                                                                   |  |  | 1:100   | Trac     | Dato             |
| Kommune : Sandnes                                                                                         |  |  | Gnr38   | Bnr99    | Disk Minde       |
| Utbygger                                                                                                  |  |  | Sak BFS1   |          |                  |
|  <b>Rogalandshus</b> |  |  | Planlegger   |          | Tegn nr Mind1501 |
|   |  |  | <br>anniren@ark-1.no - tlf 99090113 |          | Prosj nr         |

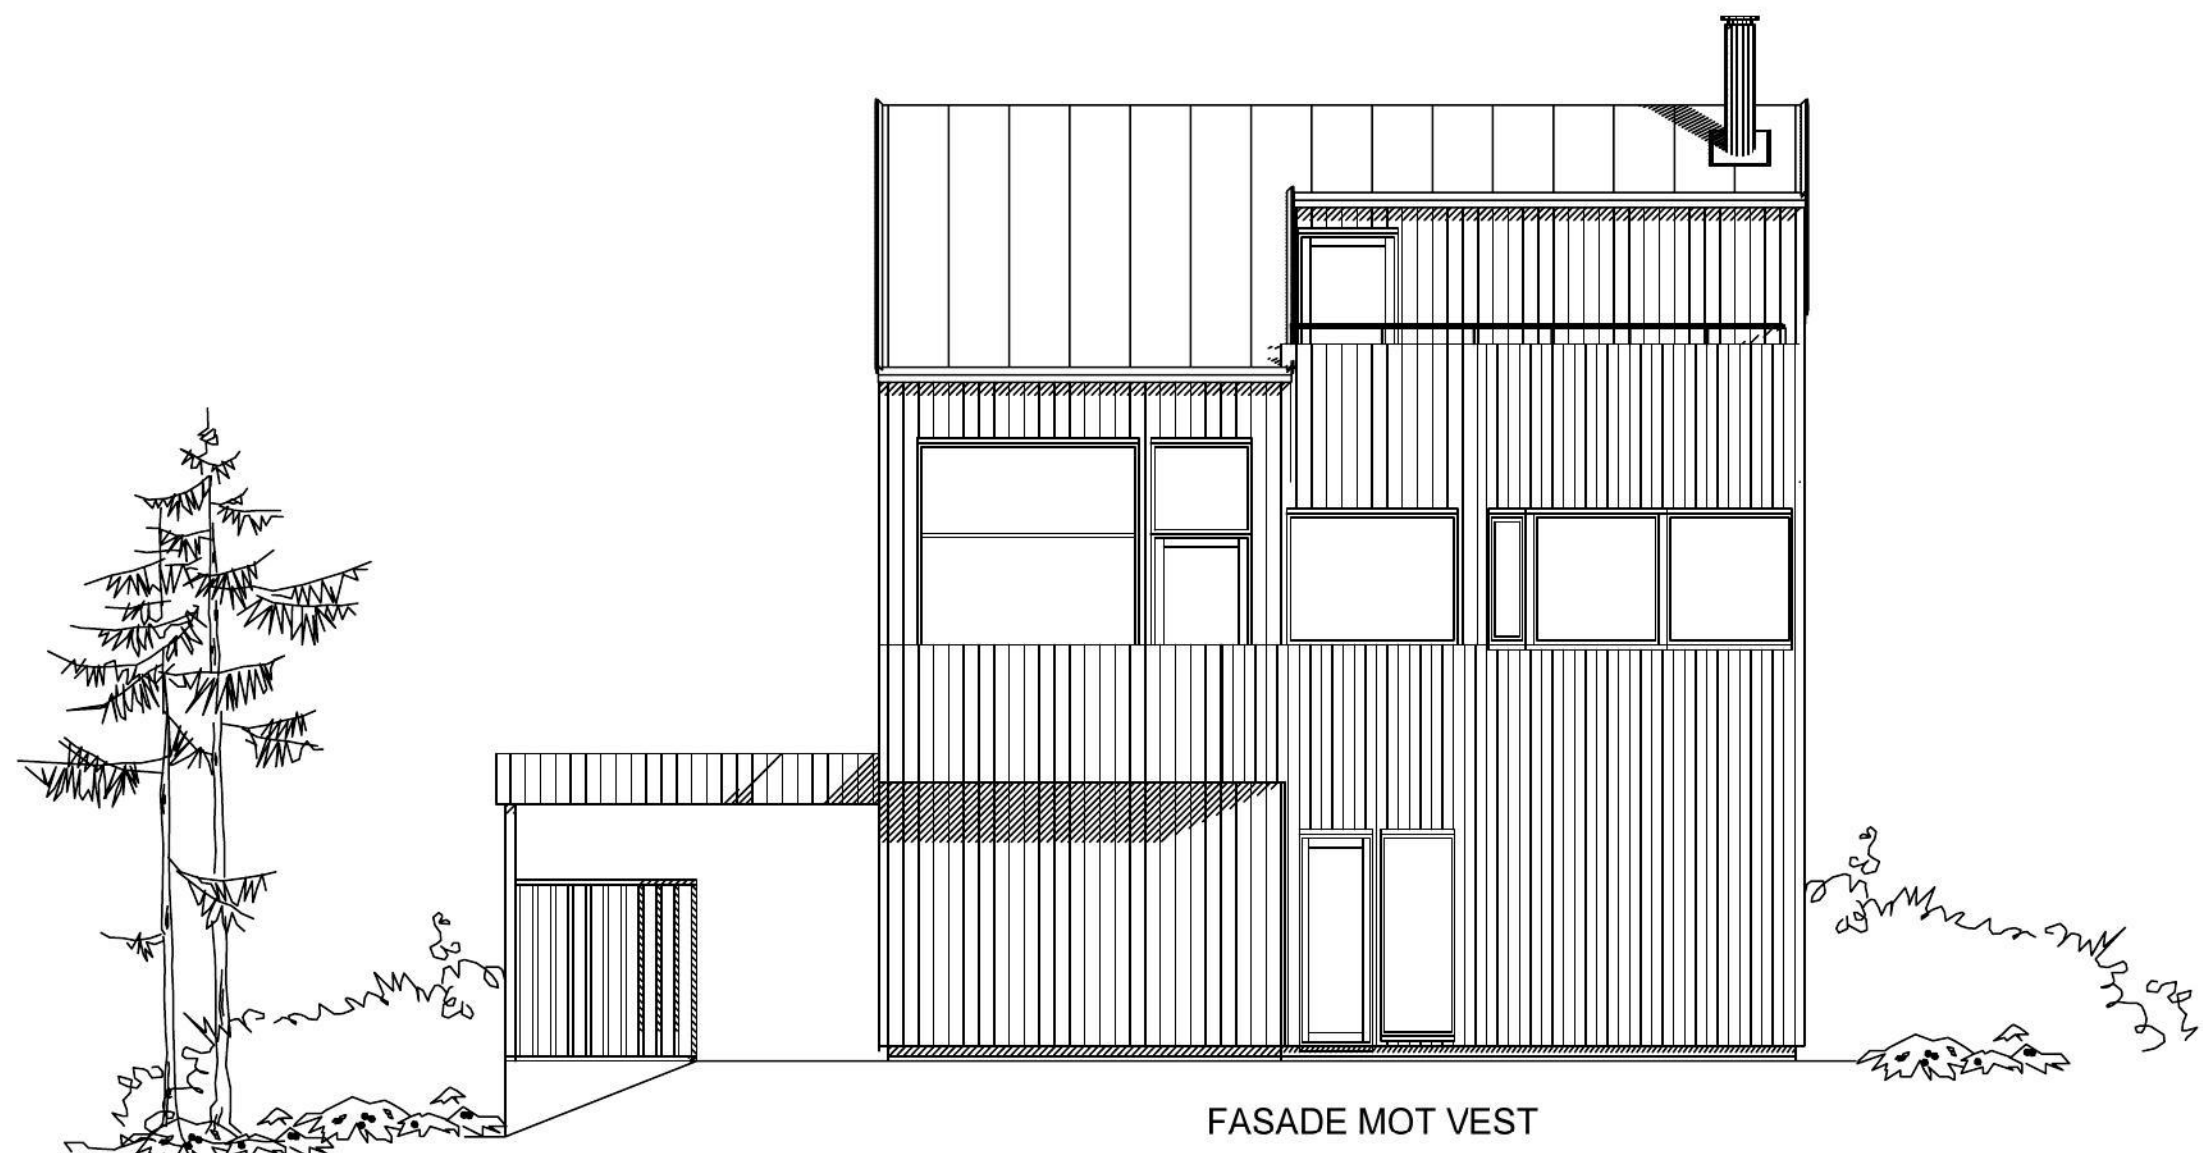