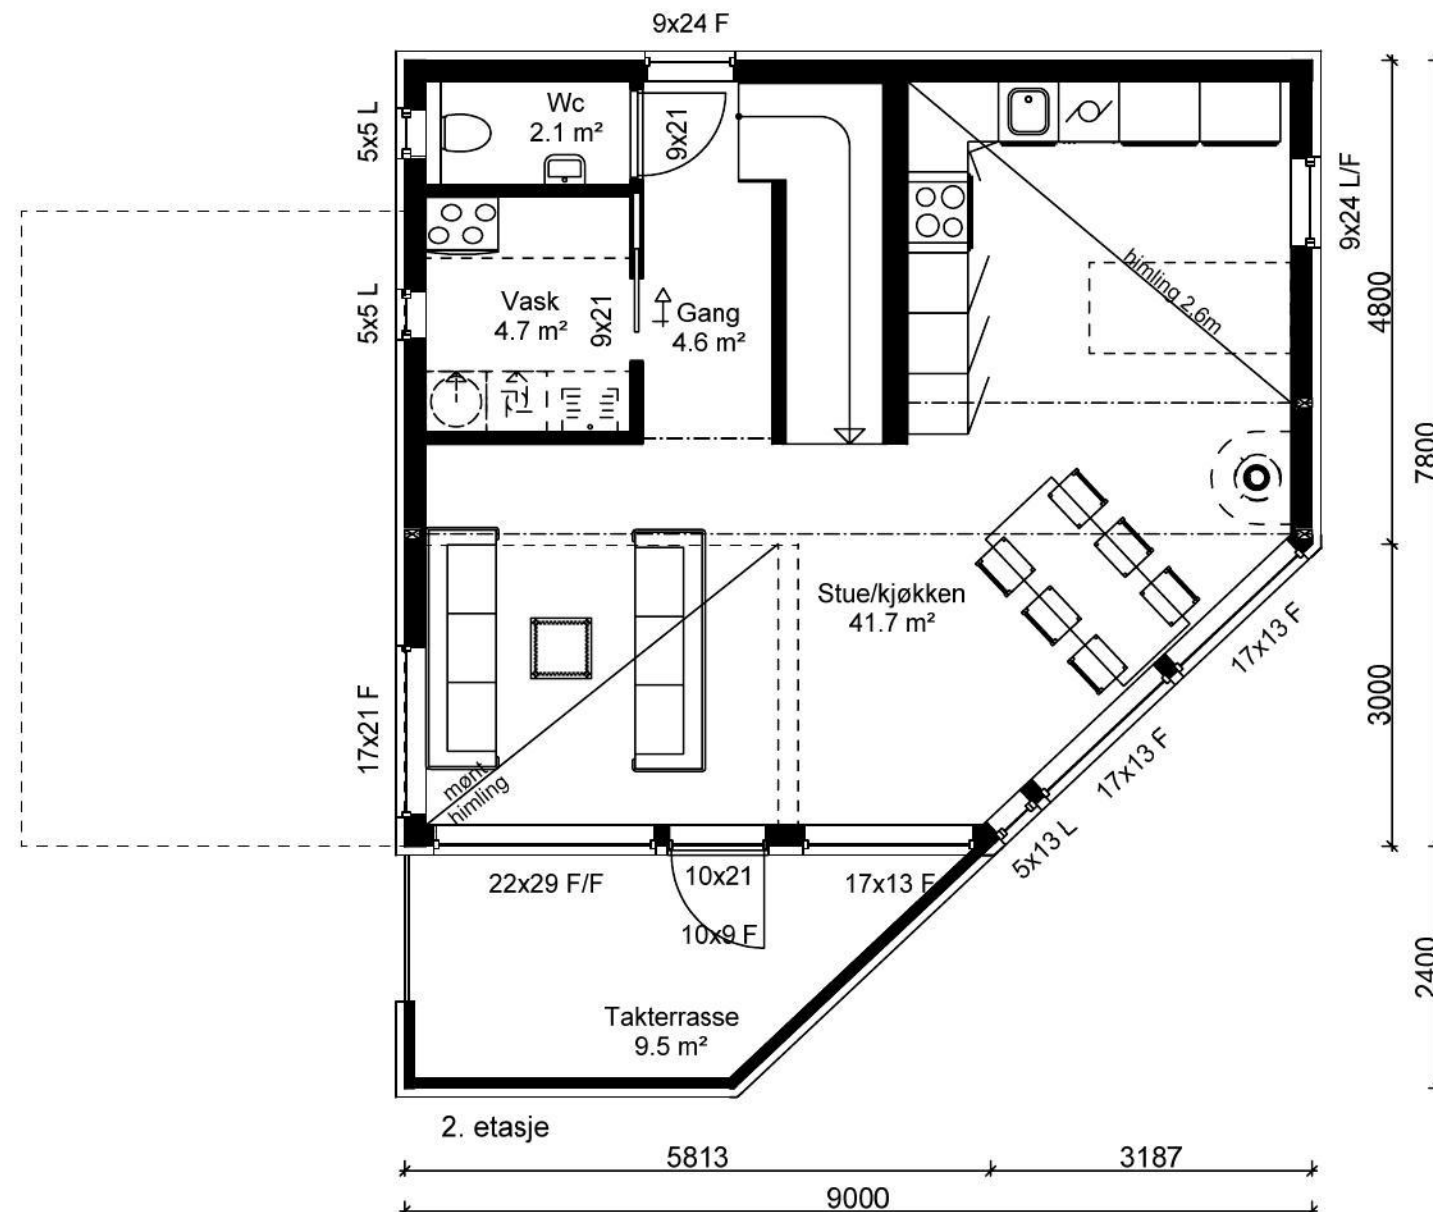


Arealberegninger i iht. NS 3940	Bruksareal BRA kvm		
	Pr etasje	Apent over- bygd areal og carport	Sum BRA
1. etasje	64.3	20.2	84.5
2. etasje	58.9	0.0	58.9
3. etasje	29.3	0.0	29.3
SUM :	152.5	20.2	172.7
BYA :	77.3	21.5	98.8

C Terrengsnitt
B Rev
A Rev

06.02.2024	AIL
16.01.2024	AIL
12.01.2024	AIL

Tiltakshaver: Rogaland bolig as		Målestokk	Tegn AIL	Dato 16.04.2021
Byggeplass : Mindeveien		1:100	Trac	Dato
Kommune : Sandnes	Gnr38 Bnr99	Disk Minde	Sak BFS1	
Utbygger 		Planlegger  anniren@ark-1.no - tlf 99090113		Tegnr nr Mind1503 Prosj nr