


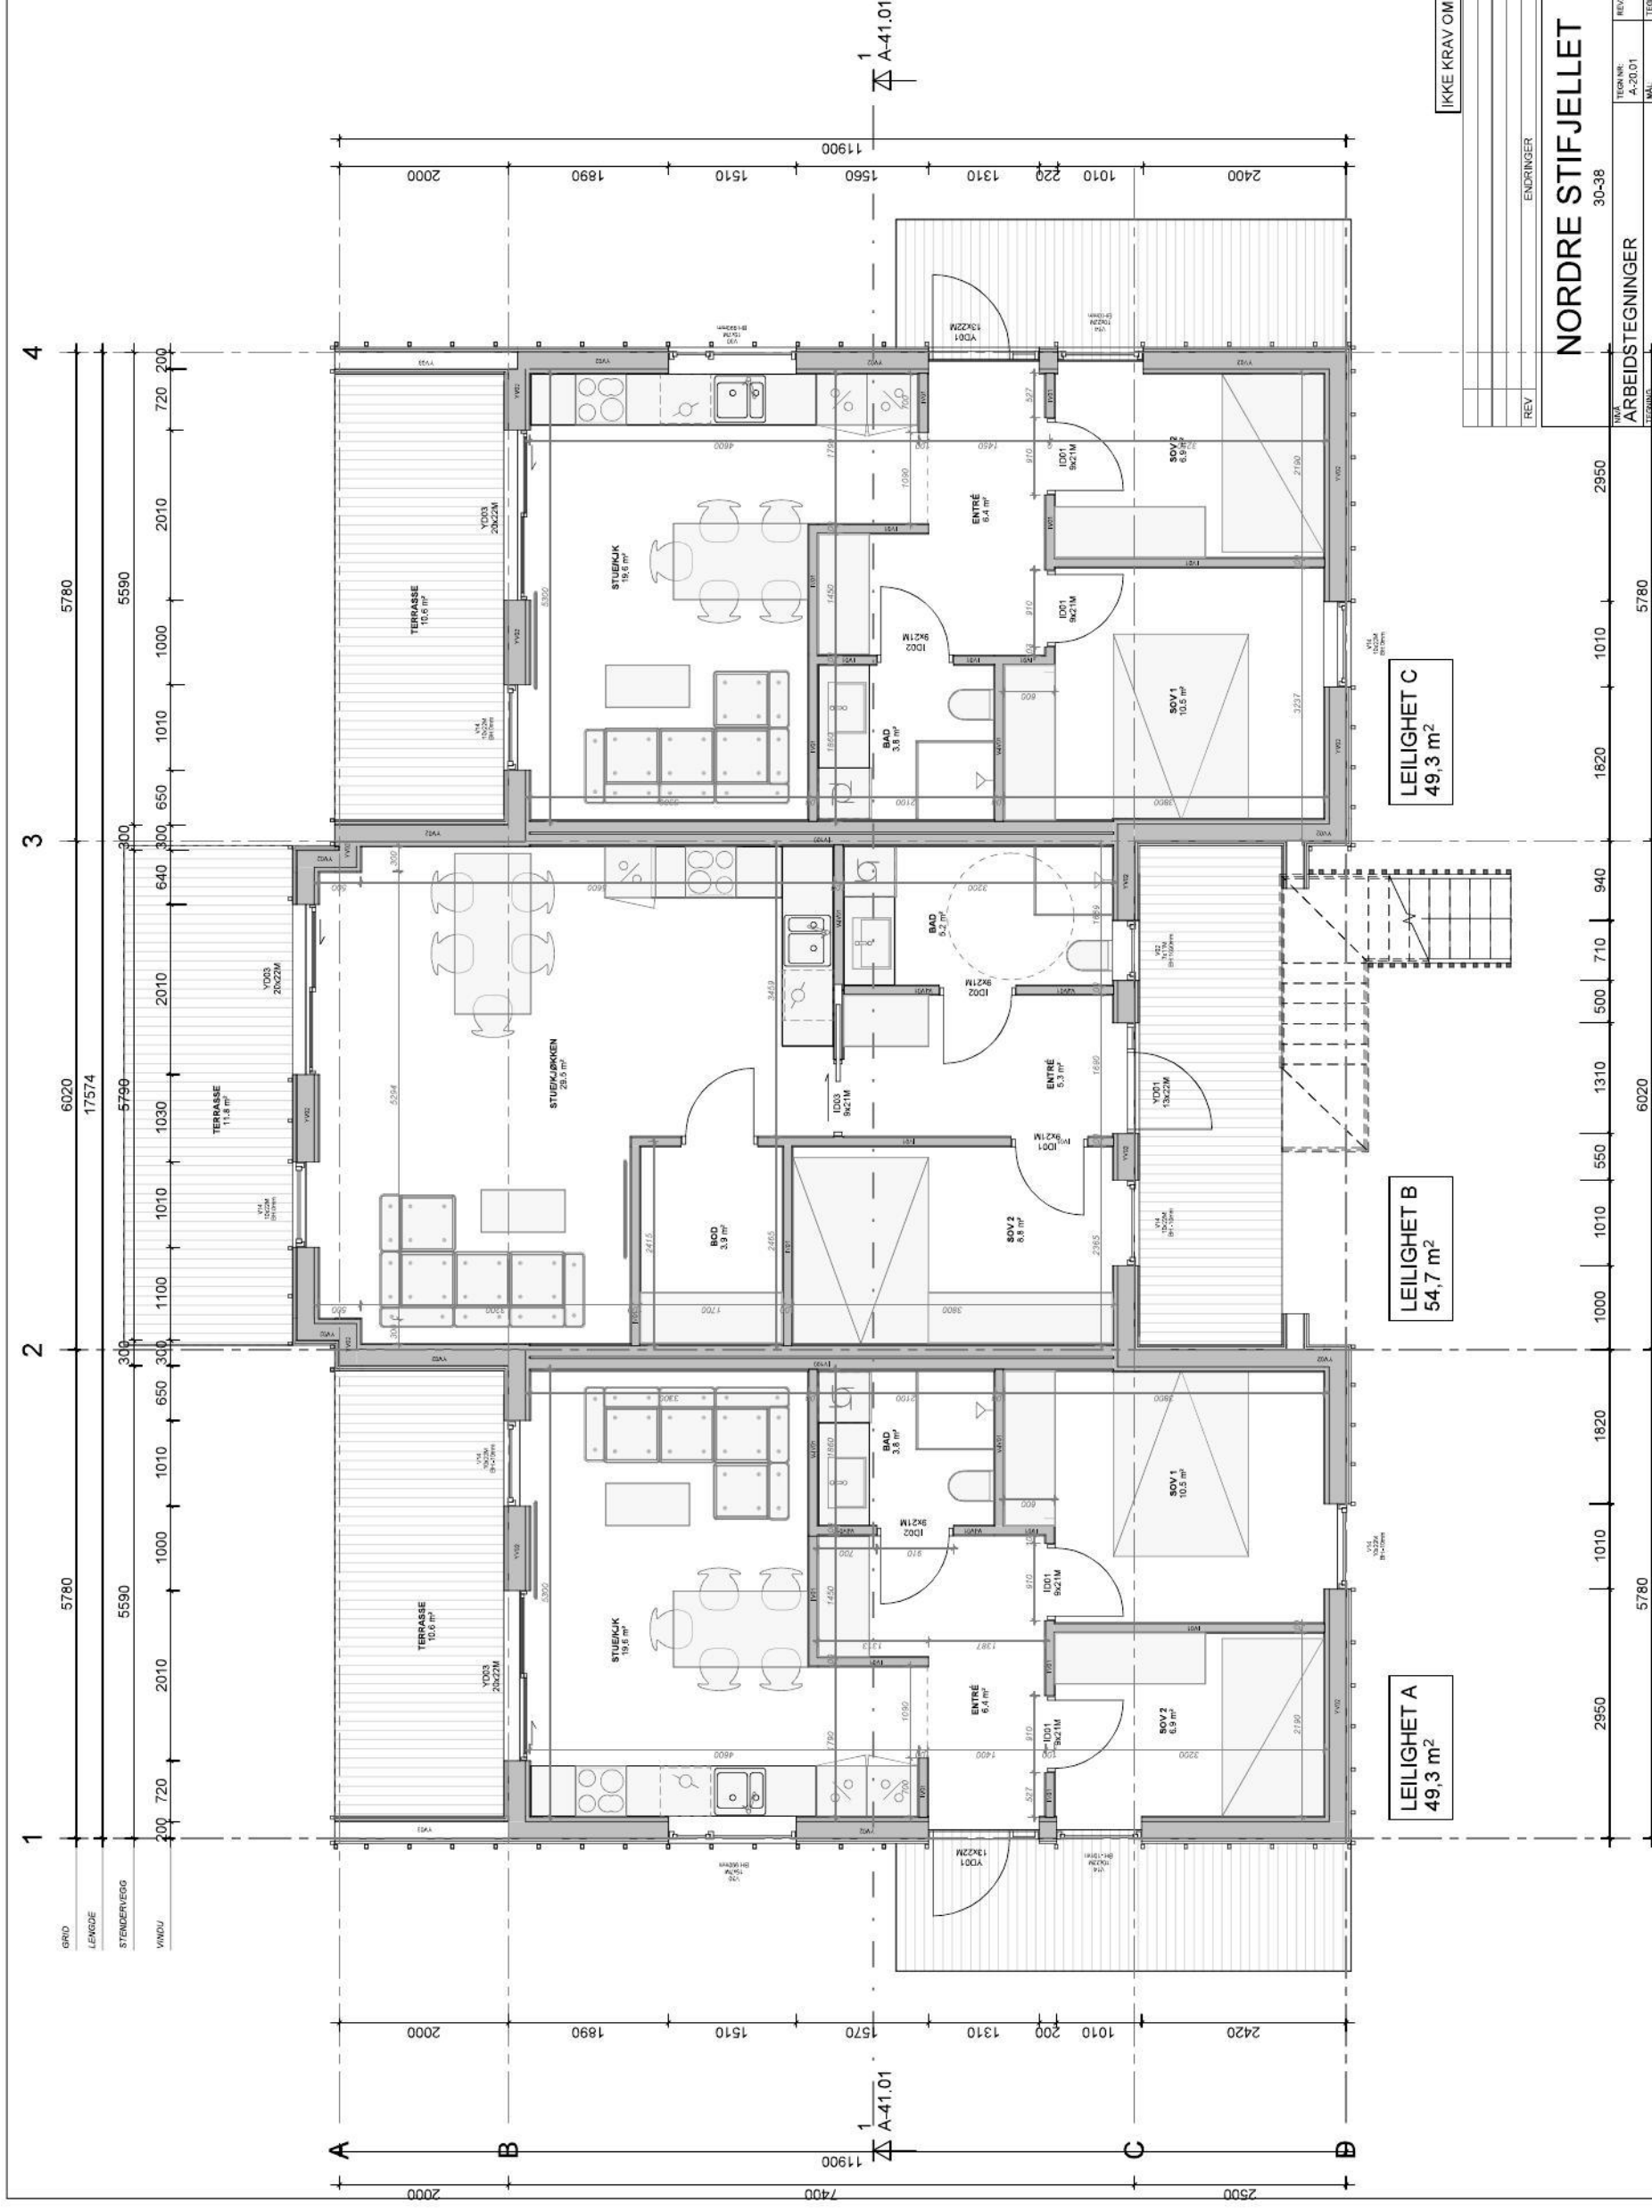

IKKE KRAV OM TILGJENGELIGHET

| REV | ENDRINGER | DATO | UTF. | KTR. |
|-----|-----------|------|------|------|
|     |           |      |      |      |
|     |           |      |      |      |
|     |           |      |      |      |

NORDRE STIFJELLET

NVA  
ARBEIDSTEGNINGER

|         |                  |          |            |       |
|---------|------------------|----------|------------|-------|
| HAVER   | ARBEIDSTEGNINGER | TEGN NR: | 4-20.01    | REV.  |
| TEGNUNG | PLAN 01          | MAK:     | 1:50       | TEGN: |
|         |                  | DATE:    | 23.08.2023 | ANSV: |
|         |                  |          |            | KONT: |
|         |                  |          |            | JUV   |

W10.112.20.8@MARK.NET Donibon/Pedro@MARK.NET orcasider@321 Stifellet boluer@06.Teneloc@058.01 Rev@W10.112.20.8