


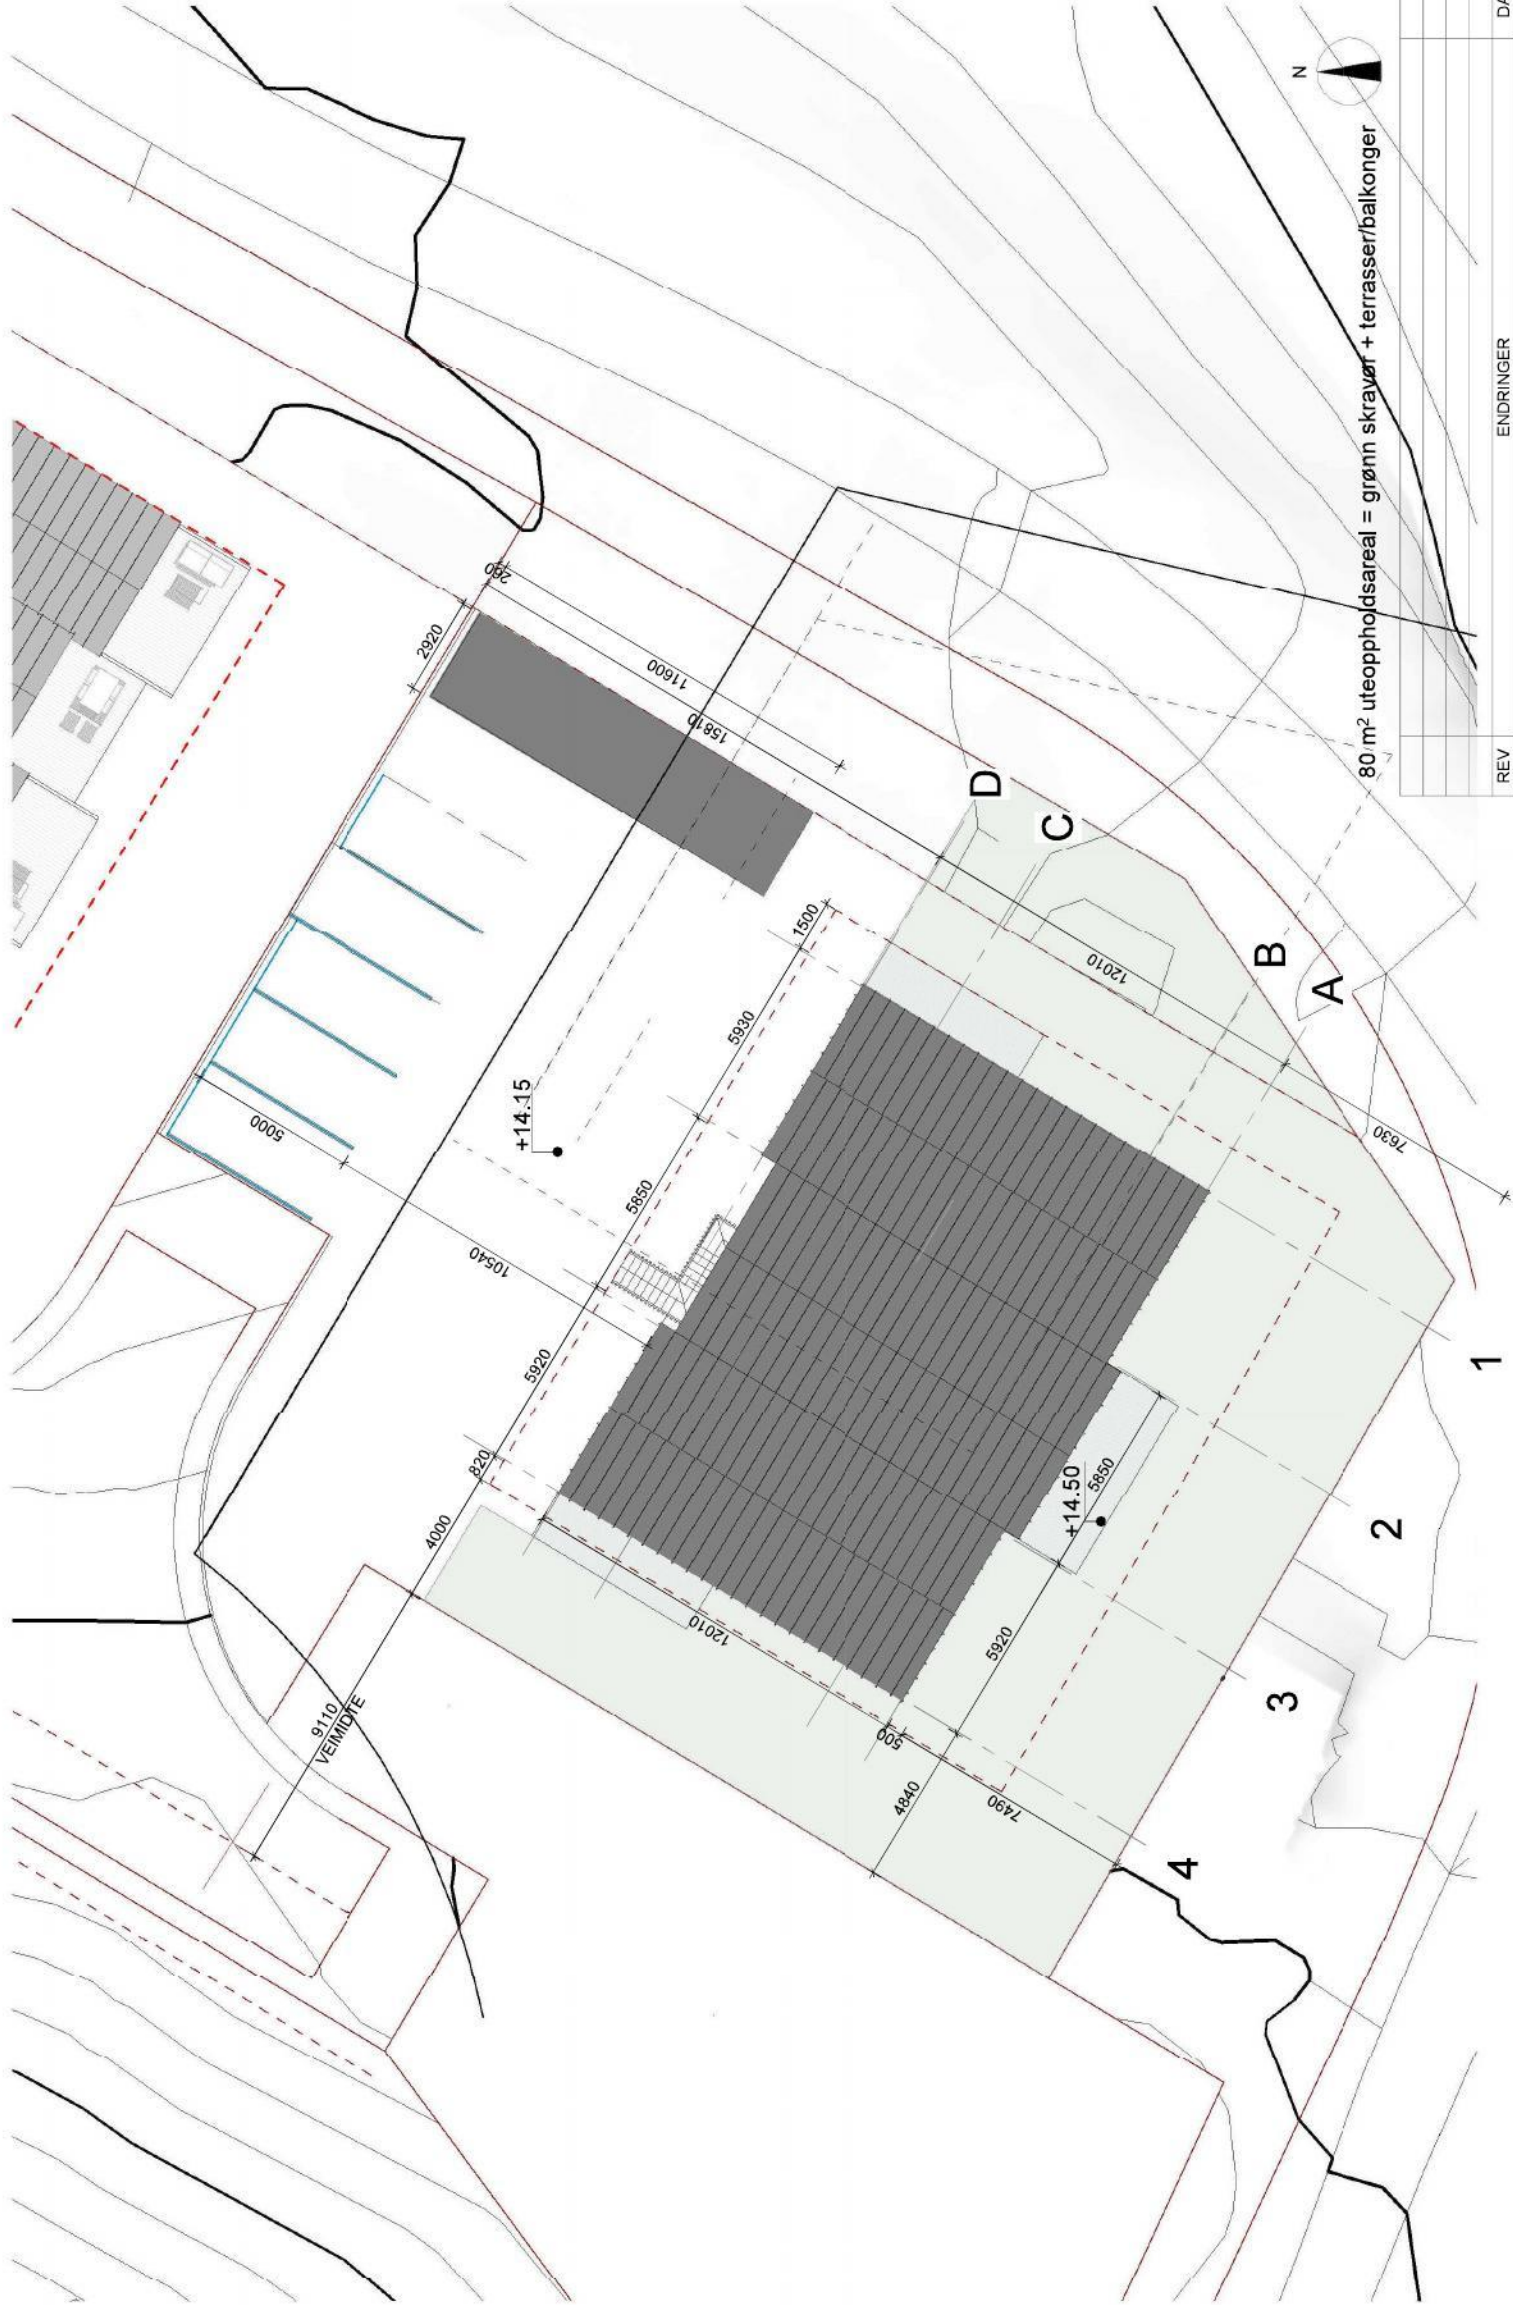

80 m² uteoppholdsareal = grønn skråner + terrasser/balkonger



ENDRINGER

REV	DATO	UTF.	KTR.

NORDRE STIFJELLET

30-38

ARBEIDSTEGNINGER

SITUASJONSPLAN

SEIL
ARKITEKTER

NVA	TEGN NR.	REV.
ARBEIDSTEGNINGER	A-10.01	
TEGNING	MÅL	TEGN
SITUASJONSPLAN	1 : 200	MCP
	DATO	ANSV.
	23.08.2023	JUV
		KONTR.
		JUV