



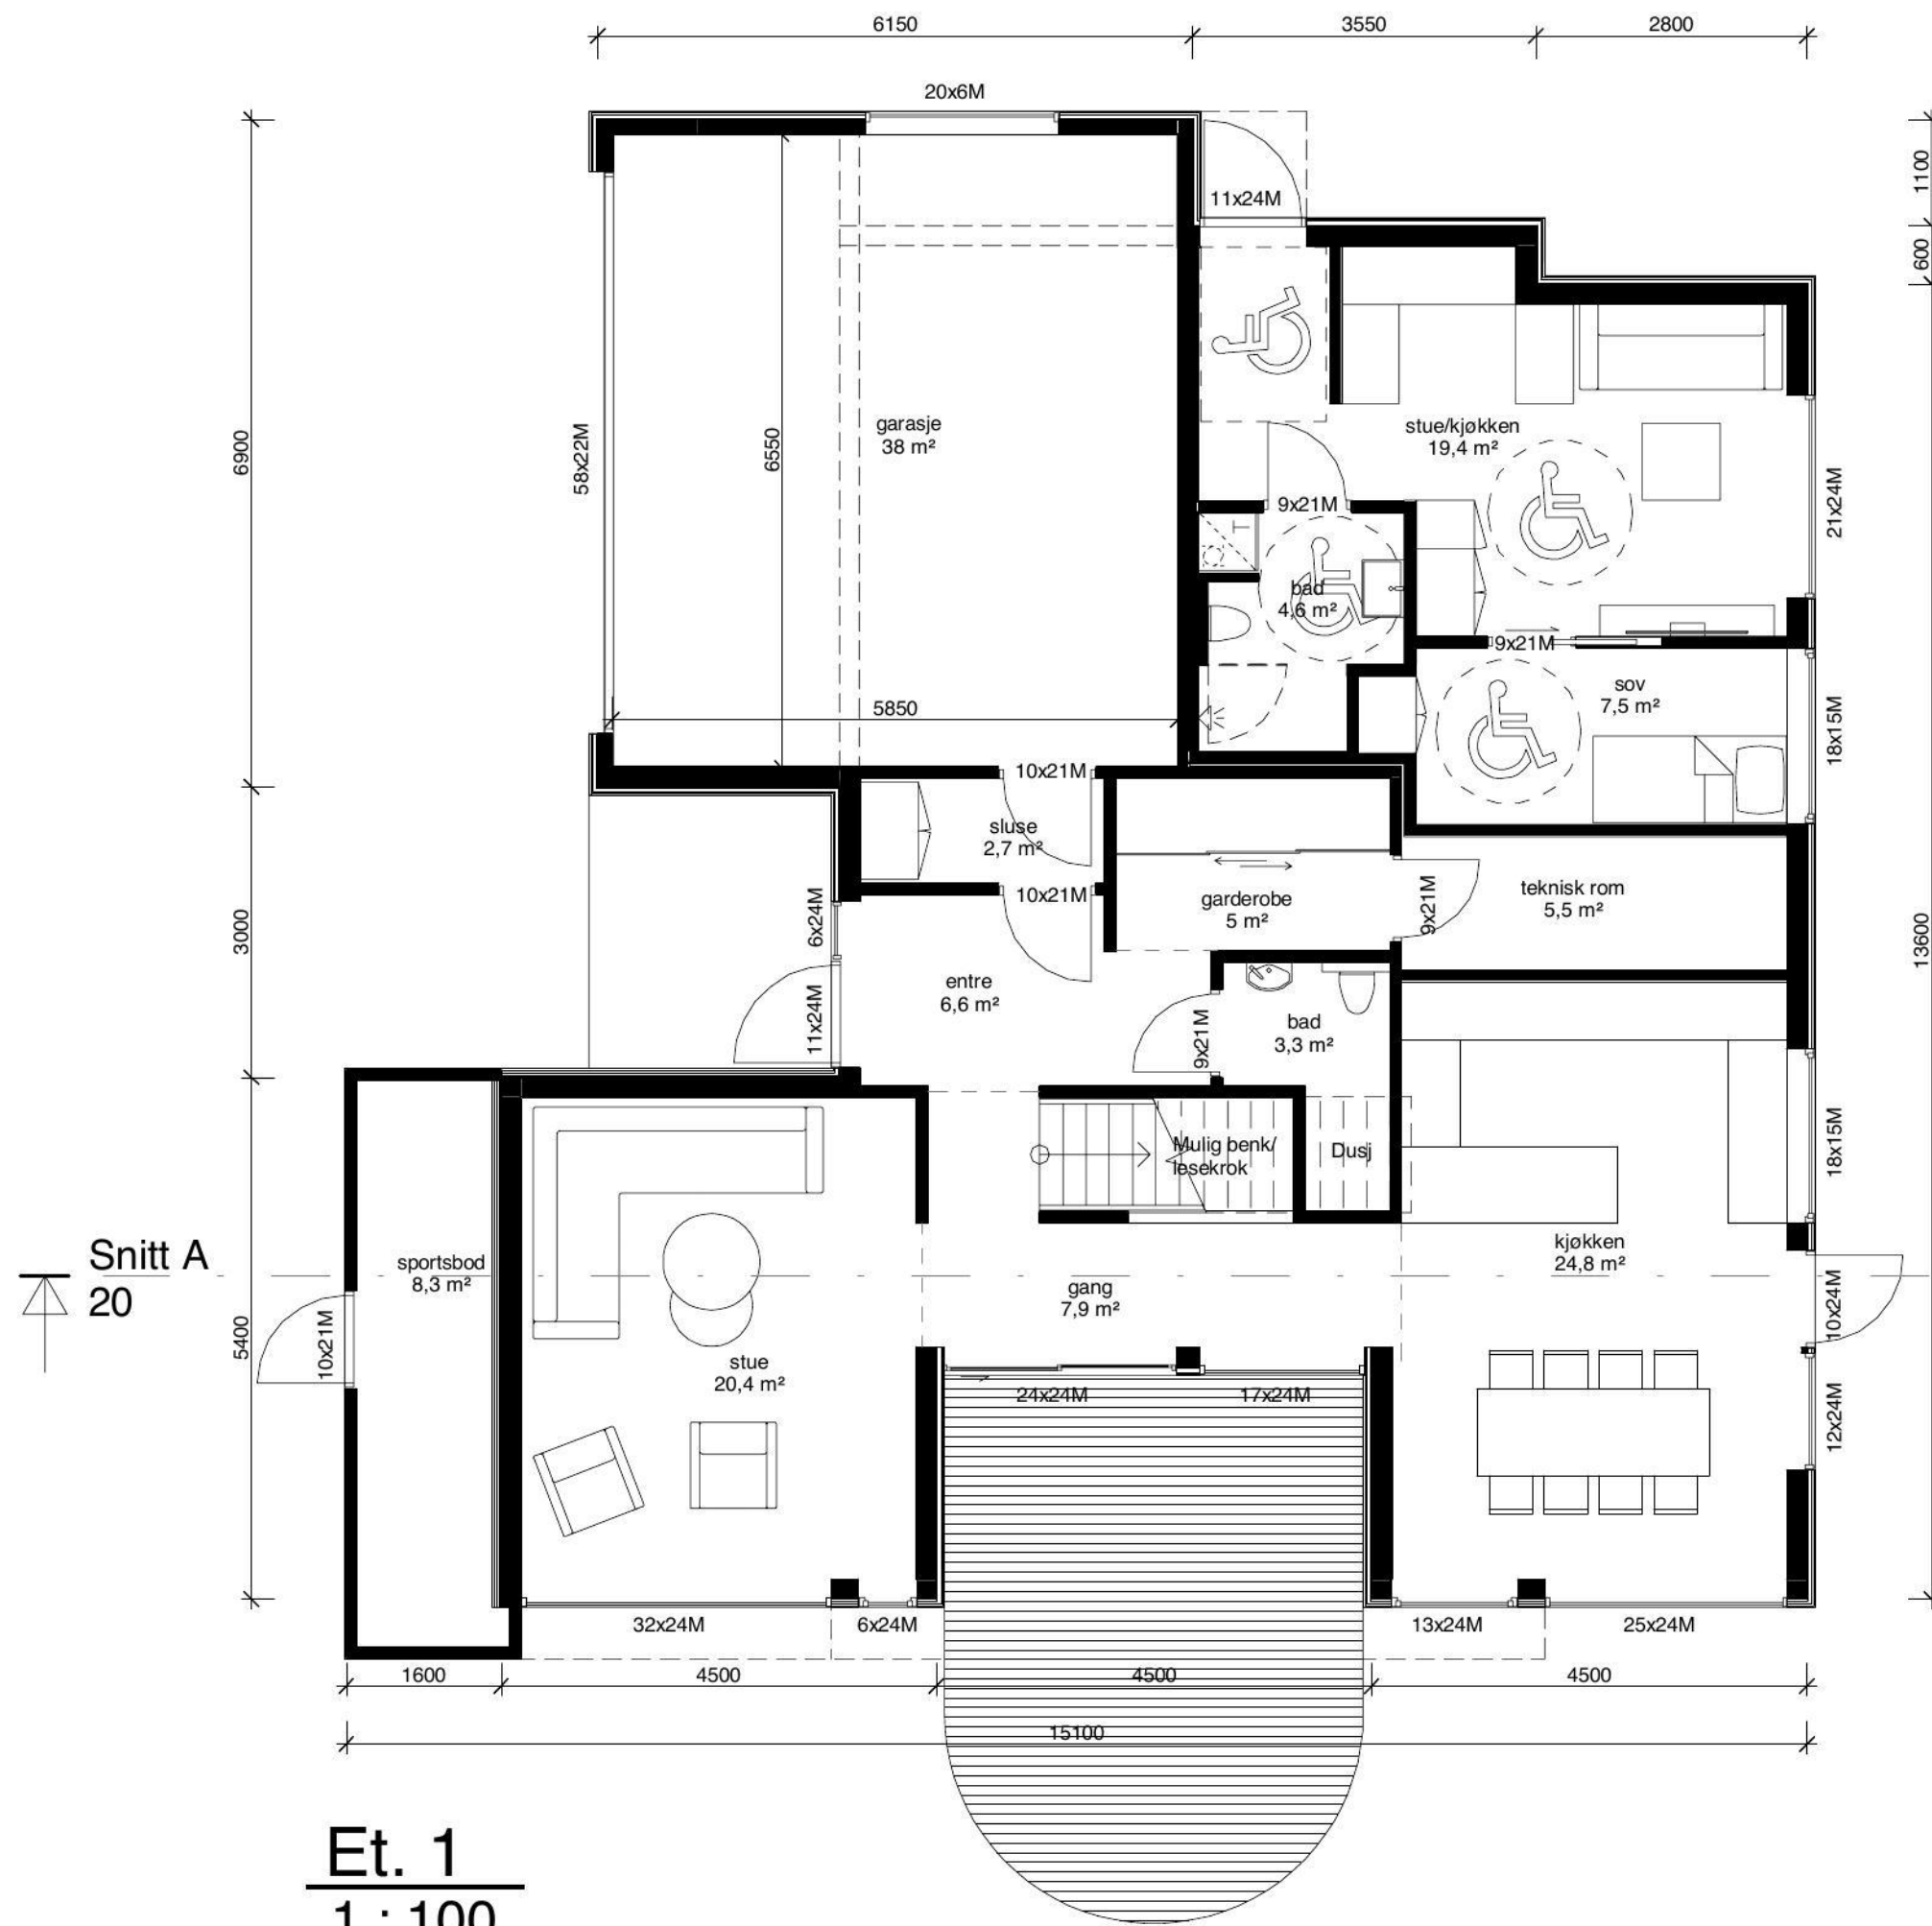

Et. 1
1 : 100

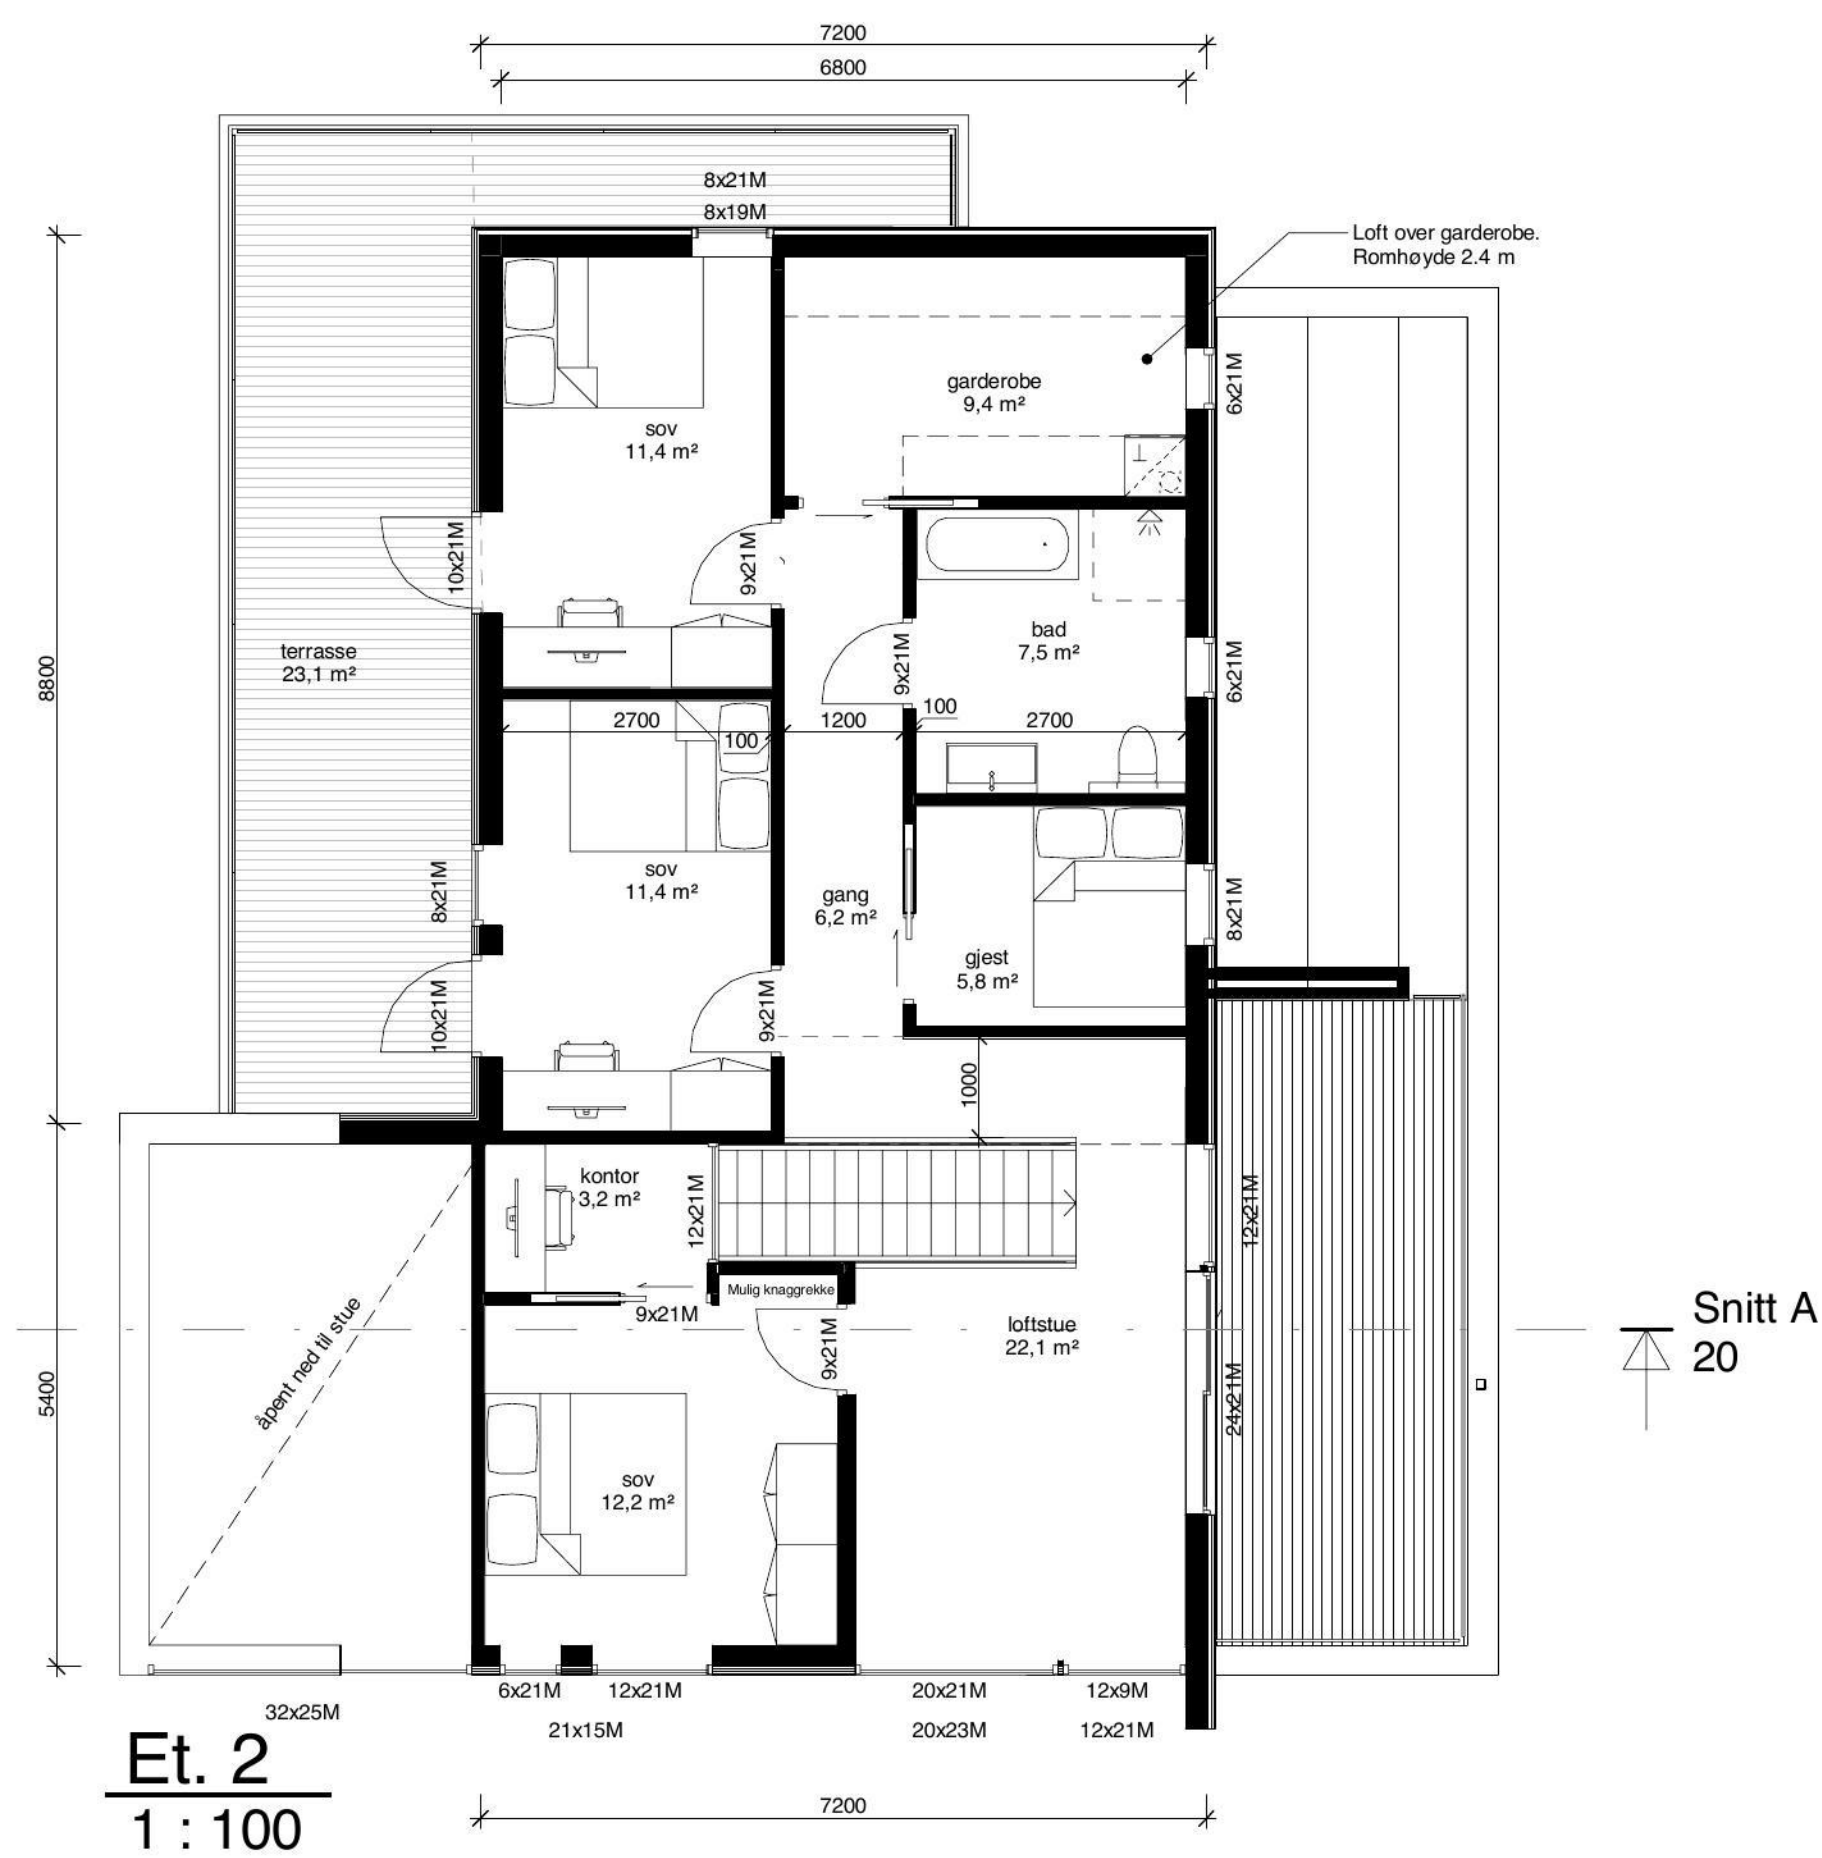

Et. 2
1 : 100

Bebygd areal (BYA)		
Etasje	Navn	Areal
Et. 1	Garasje	23,1 m²
Et. 1	Bolig	186,1 m²

Bruksareal (BRA)		
Etasje	Navn	Areal
Et. 1	Et. 1	86,2 m²
Et. 2	Et. 2	94,2 m²
Et. 1	Garasje	37,4 m²
Et. 1	Sportsbod	7,5 m²
Et. 1	Utleie	33,6 m²
		258,9 m²

Tiltakshaver
Anja og Alexander

Prosjektfase
Skisse

Kontroll dato/sign
Checker

Målestokk
1 : 100 A3

E1
Vedleggssnr.

Rv Dato Beskrivelse Ut Sgn

3331
Prosjektnr.

Prosjektadresse/gbnr.
Ofthenesheia 123

06.07.2023 10:47:34 K:\Prosjekt\3331 Anja K. Braaten Enebolig Ofthenesheia\01 Byggesak\06 Tegninger\02 Under arbeid\03 Revit_IFC\3331 - Ofthenesheia 123.rvt

Plan

10

Utarb RKP 06.07.2023

egøastrek