


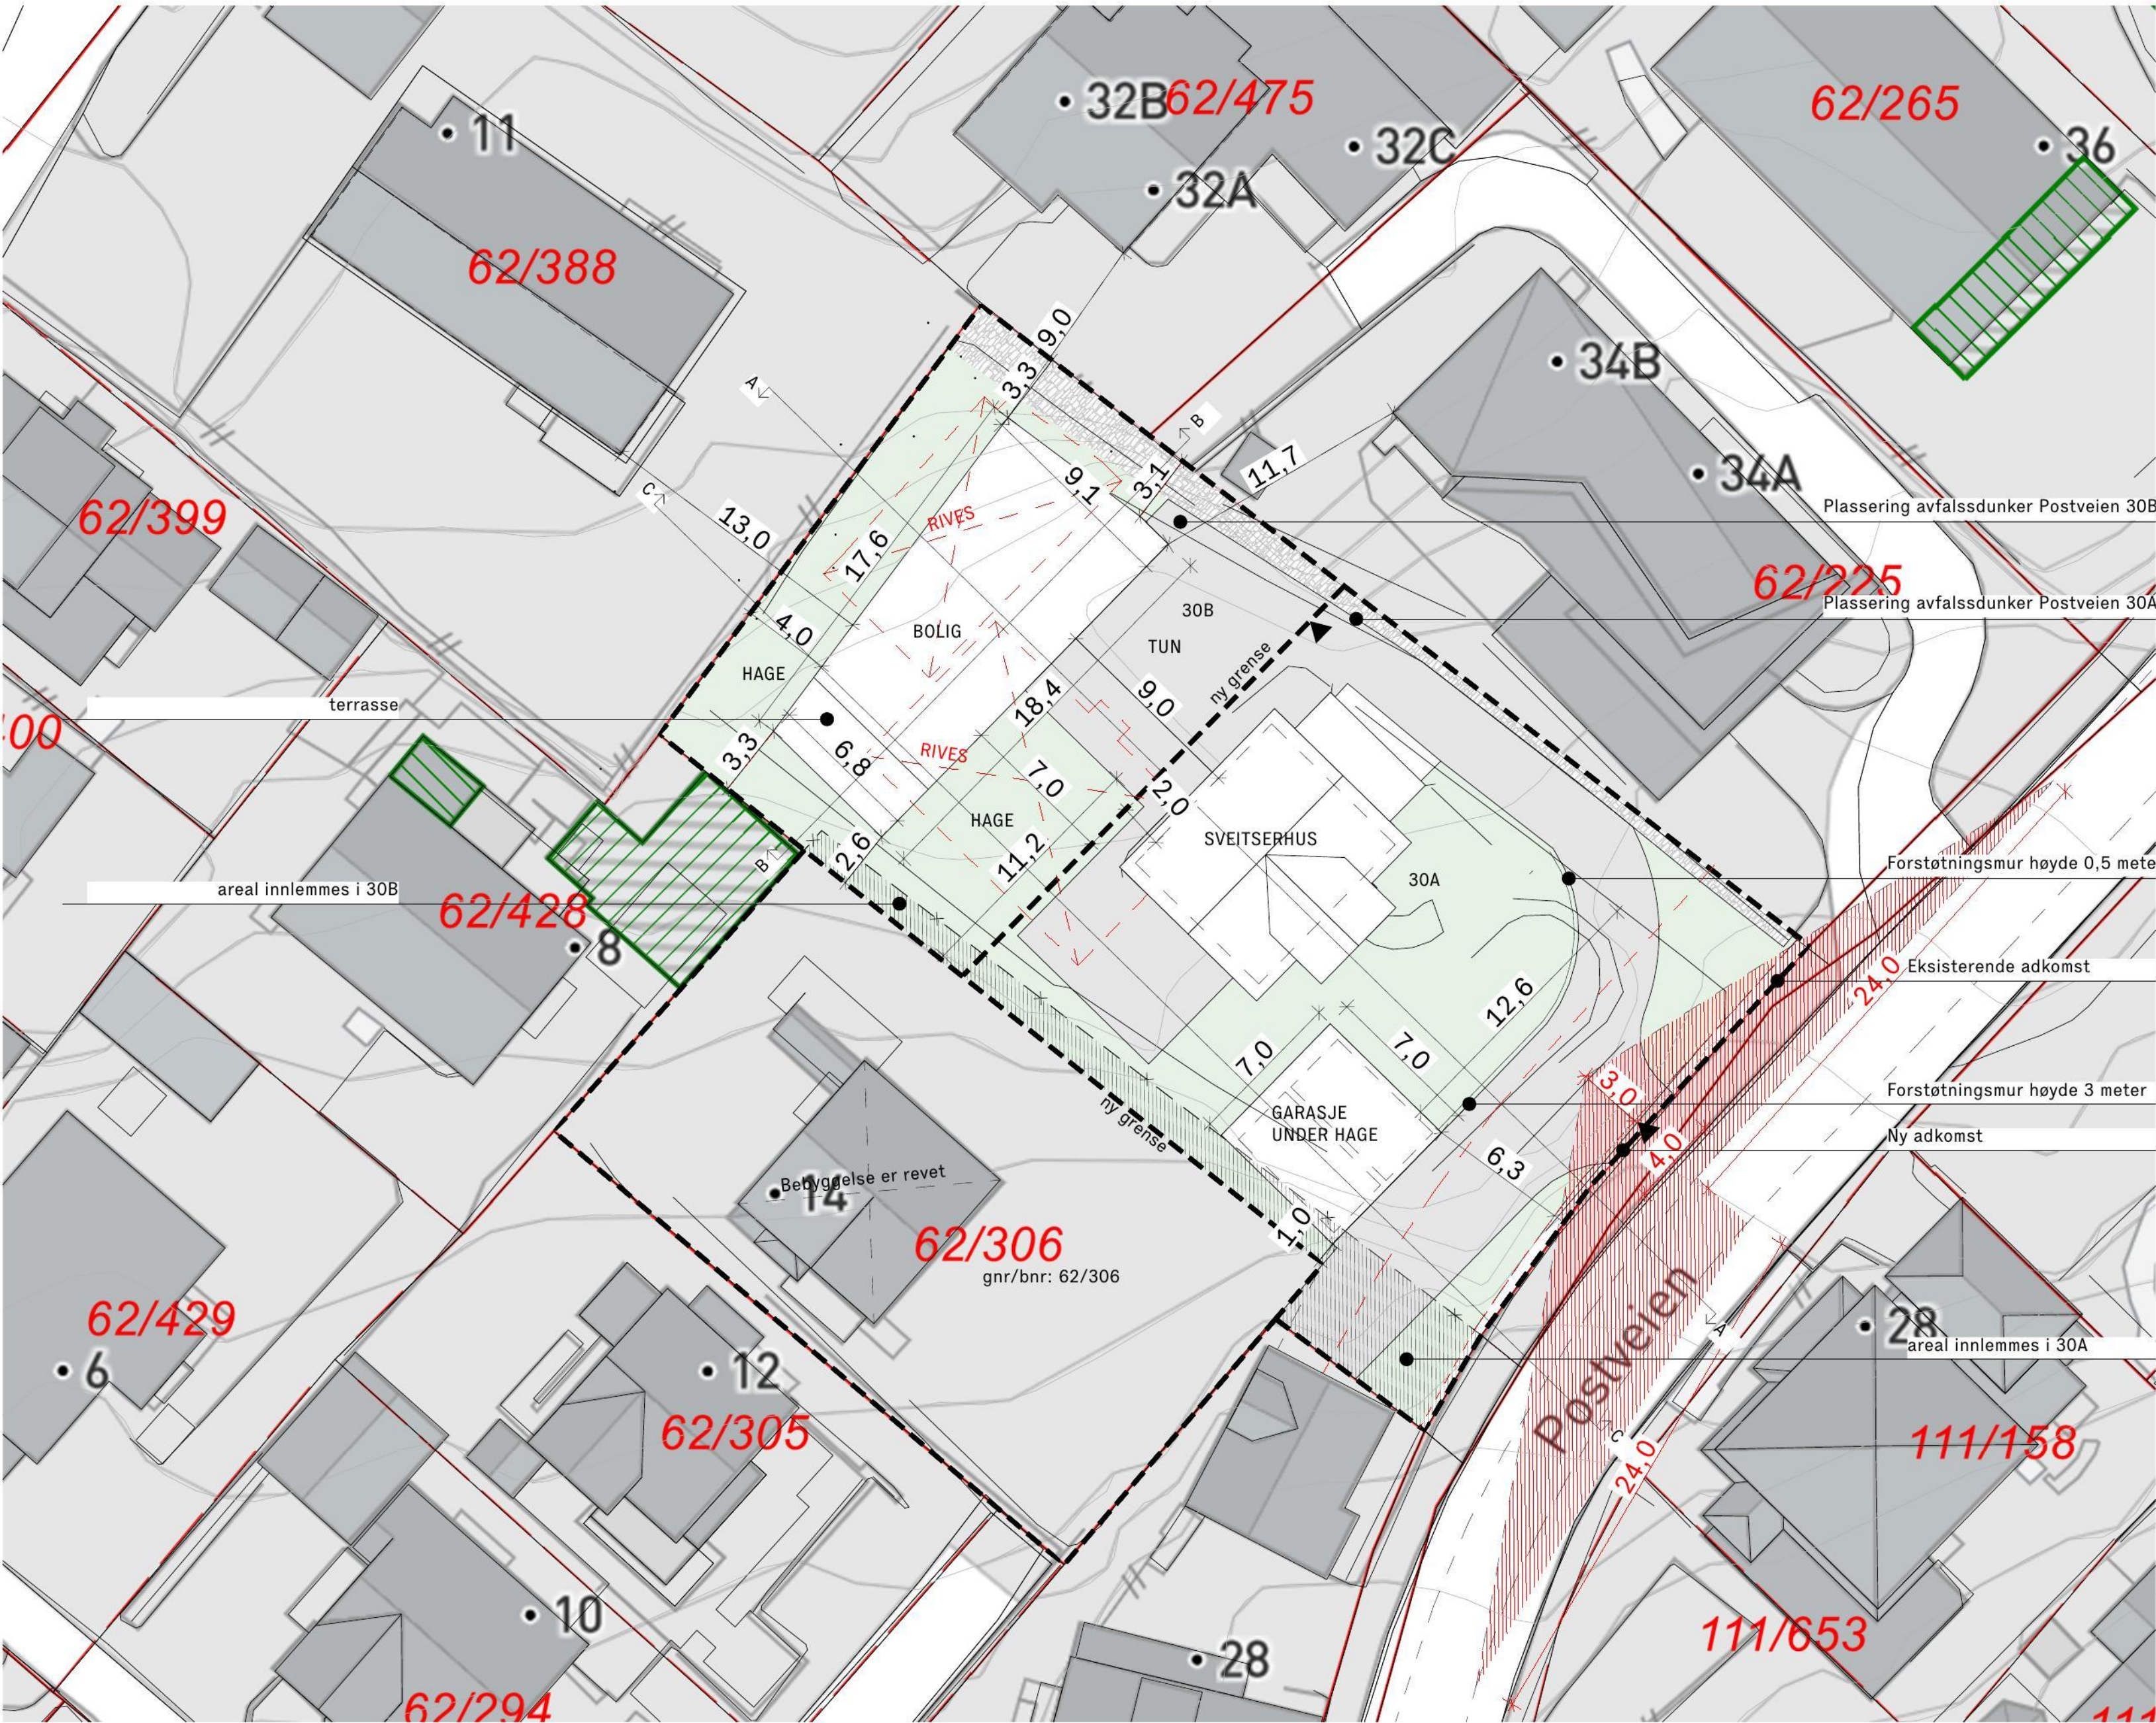

Forslag til ny eiendomsgrense

TOMT 30B:
460,8m²

TOMT 30A:
689,9m²

gnr/bnr: 62/306:
520,4m²

